

CONSTRUCTION DRAWING


RUMAH IBU FINA

KOMPLEK BALI VILLAGE - CIPETE - JAKARTA SELATAN




ARSITEKTUR

ARCHITECTURE.INTERIOR.DESIGN STUDIO

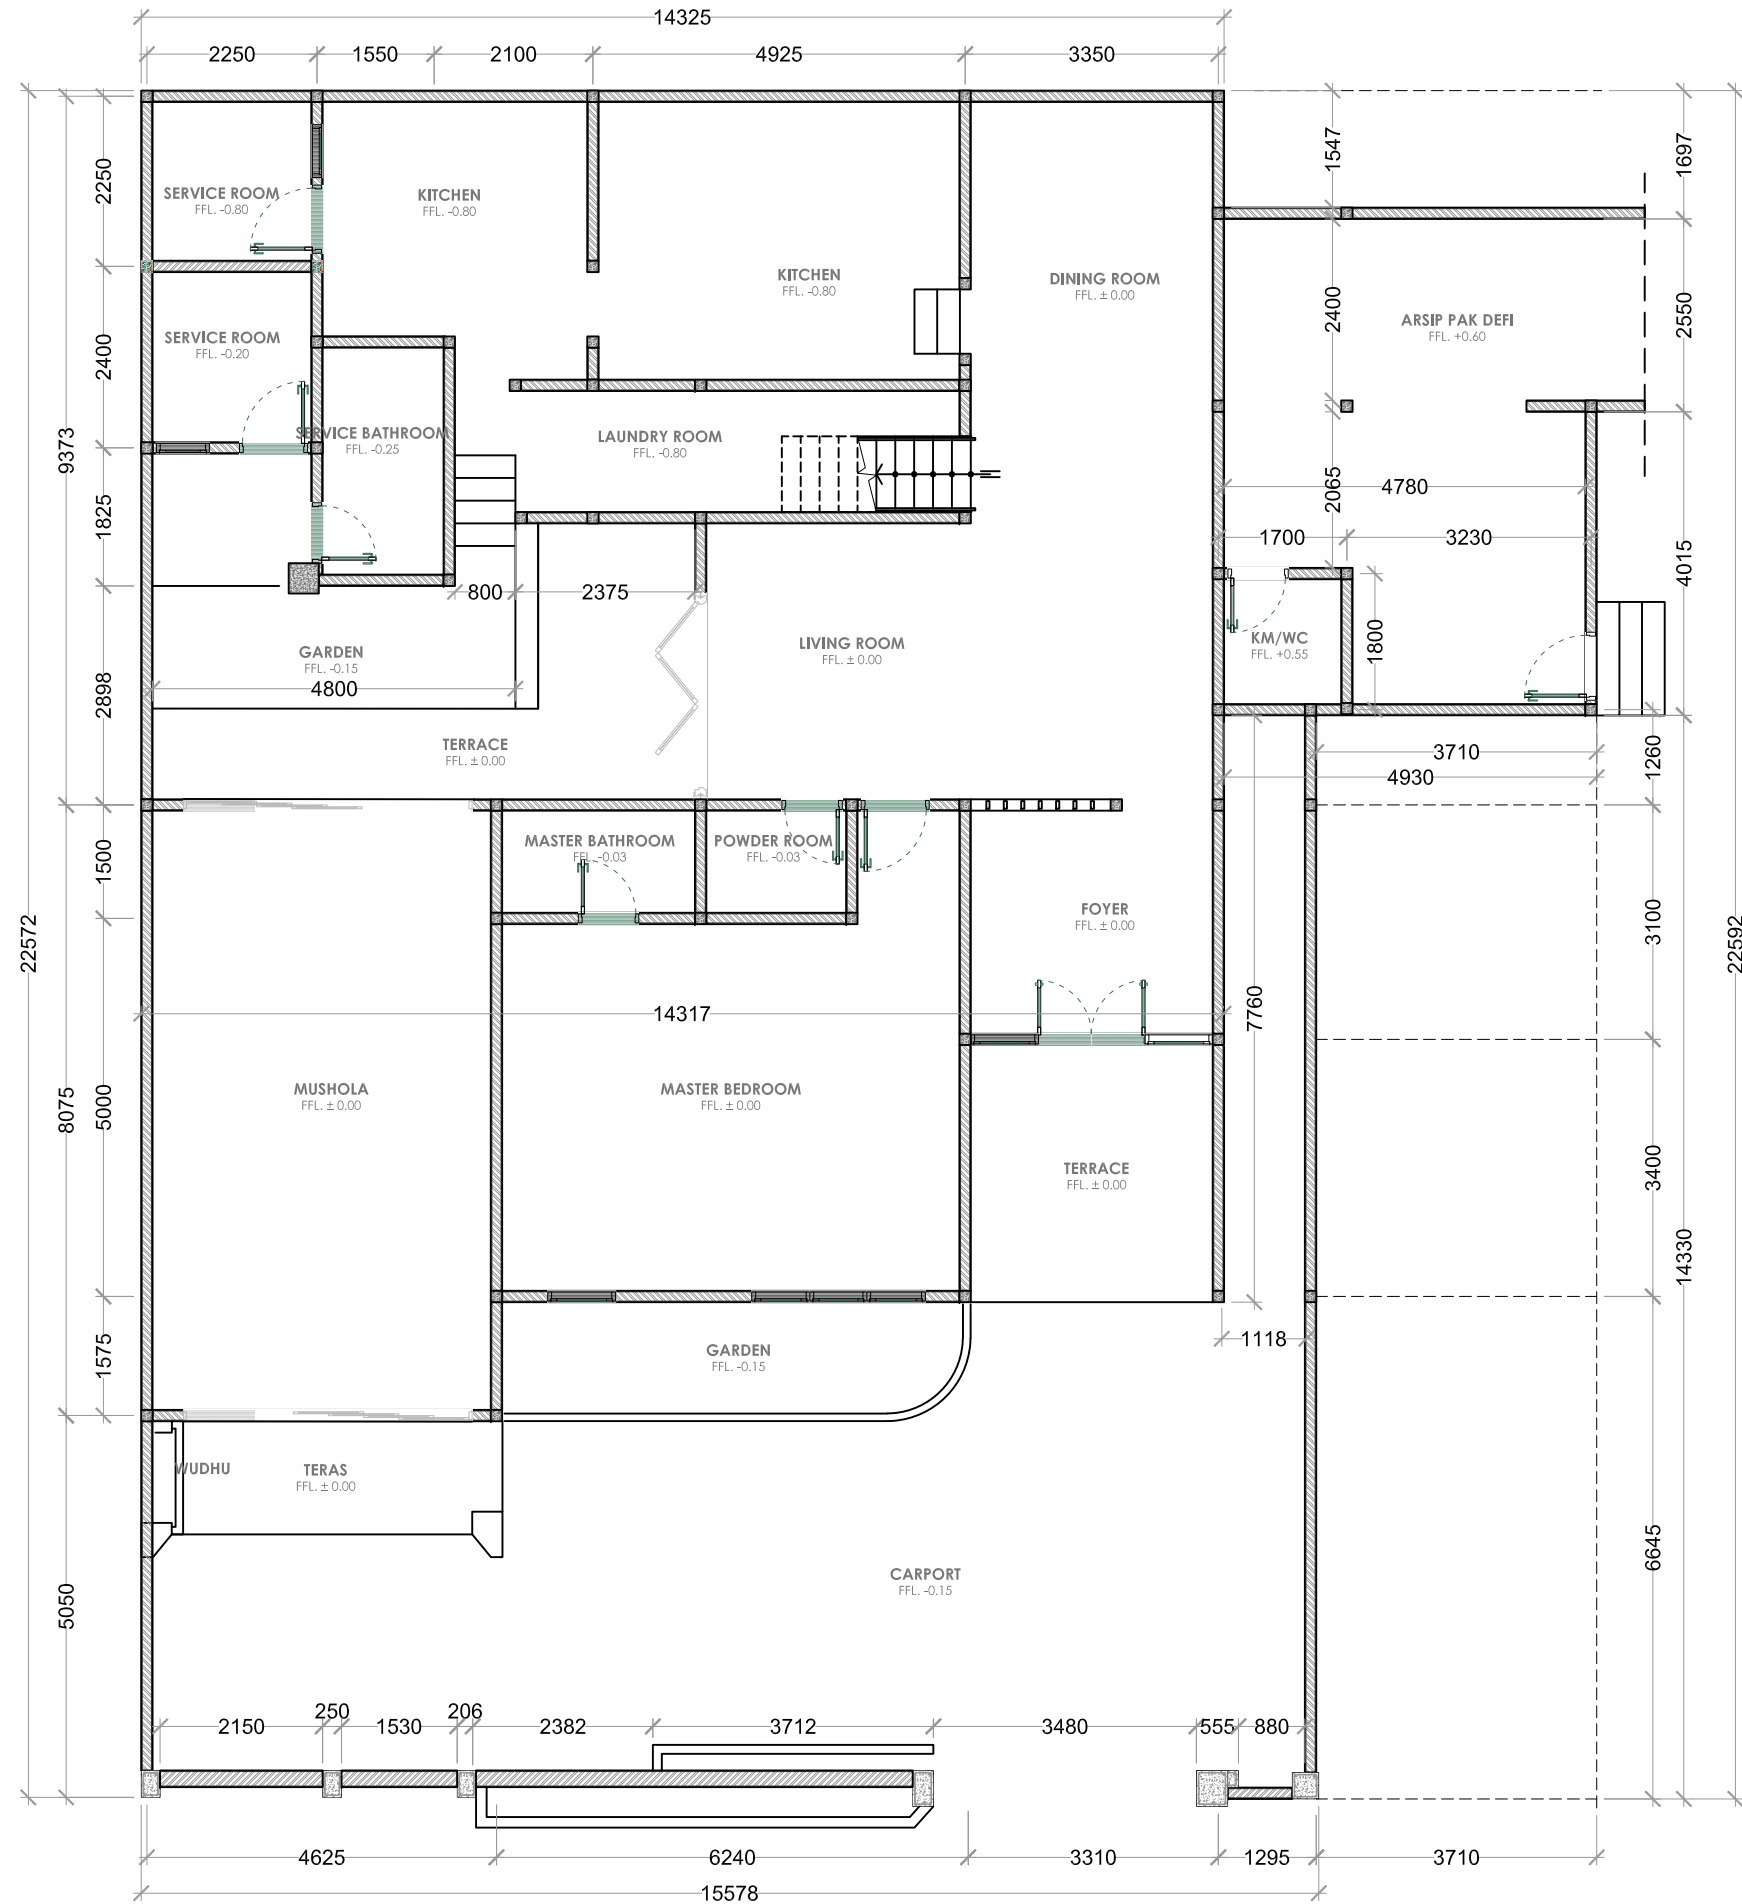


DENAH EXISTING LT. 1
SKALA 1:100

KONSULTAN					
KONTRAKTOR					
PROYEK					
KETERANGAN					
REVISI		TGL		BLN	THN
ARSITEK					
DIGAMBAR					
DIPERIKSA					
DISETUJUI					
NO. PROYEK					
-					
NAMA GAMBAR					
DENAH EXISTING					
LANTAI 1					
SKALA		1 : 100			
AR		-		001	
SUBKAT		NO. LEMBAR			

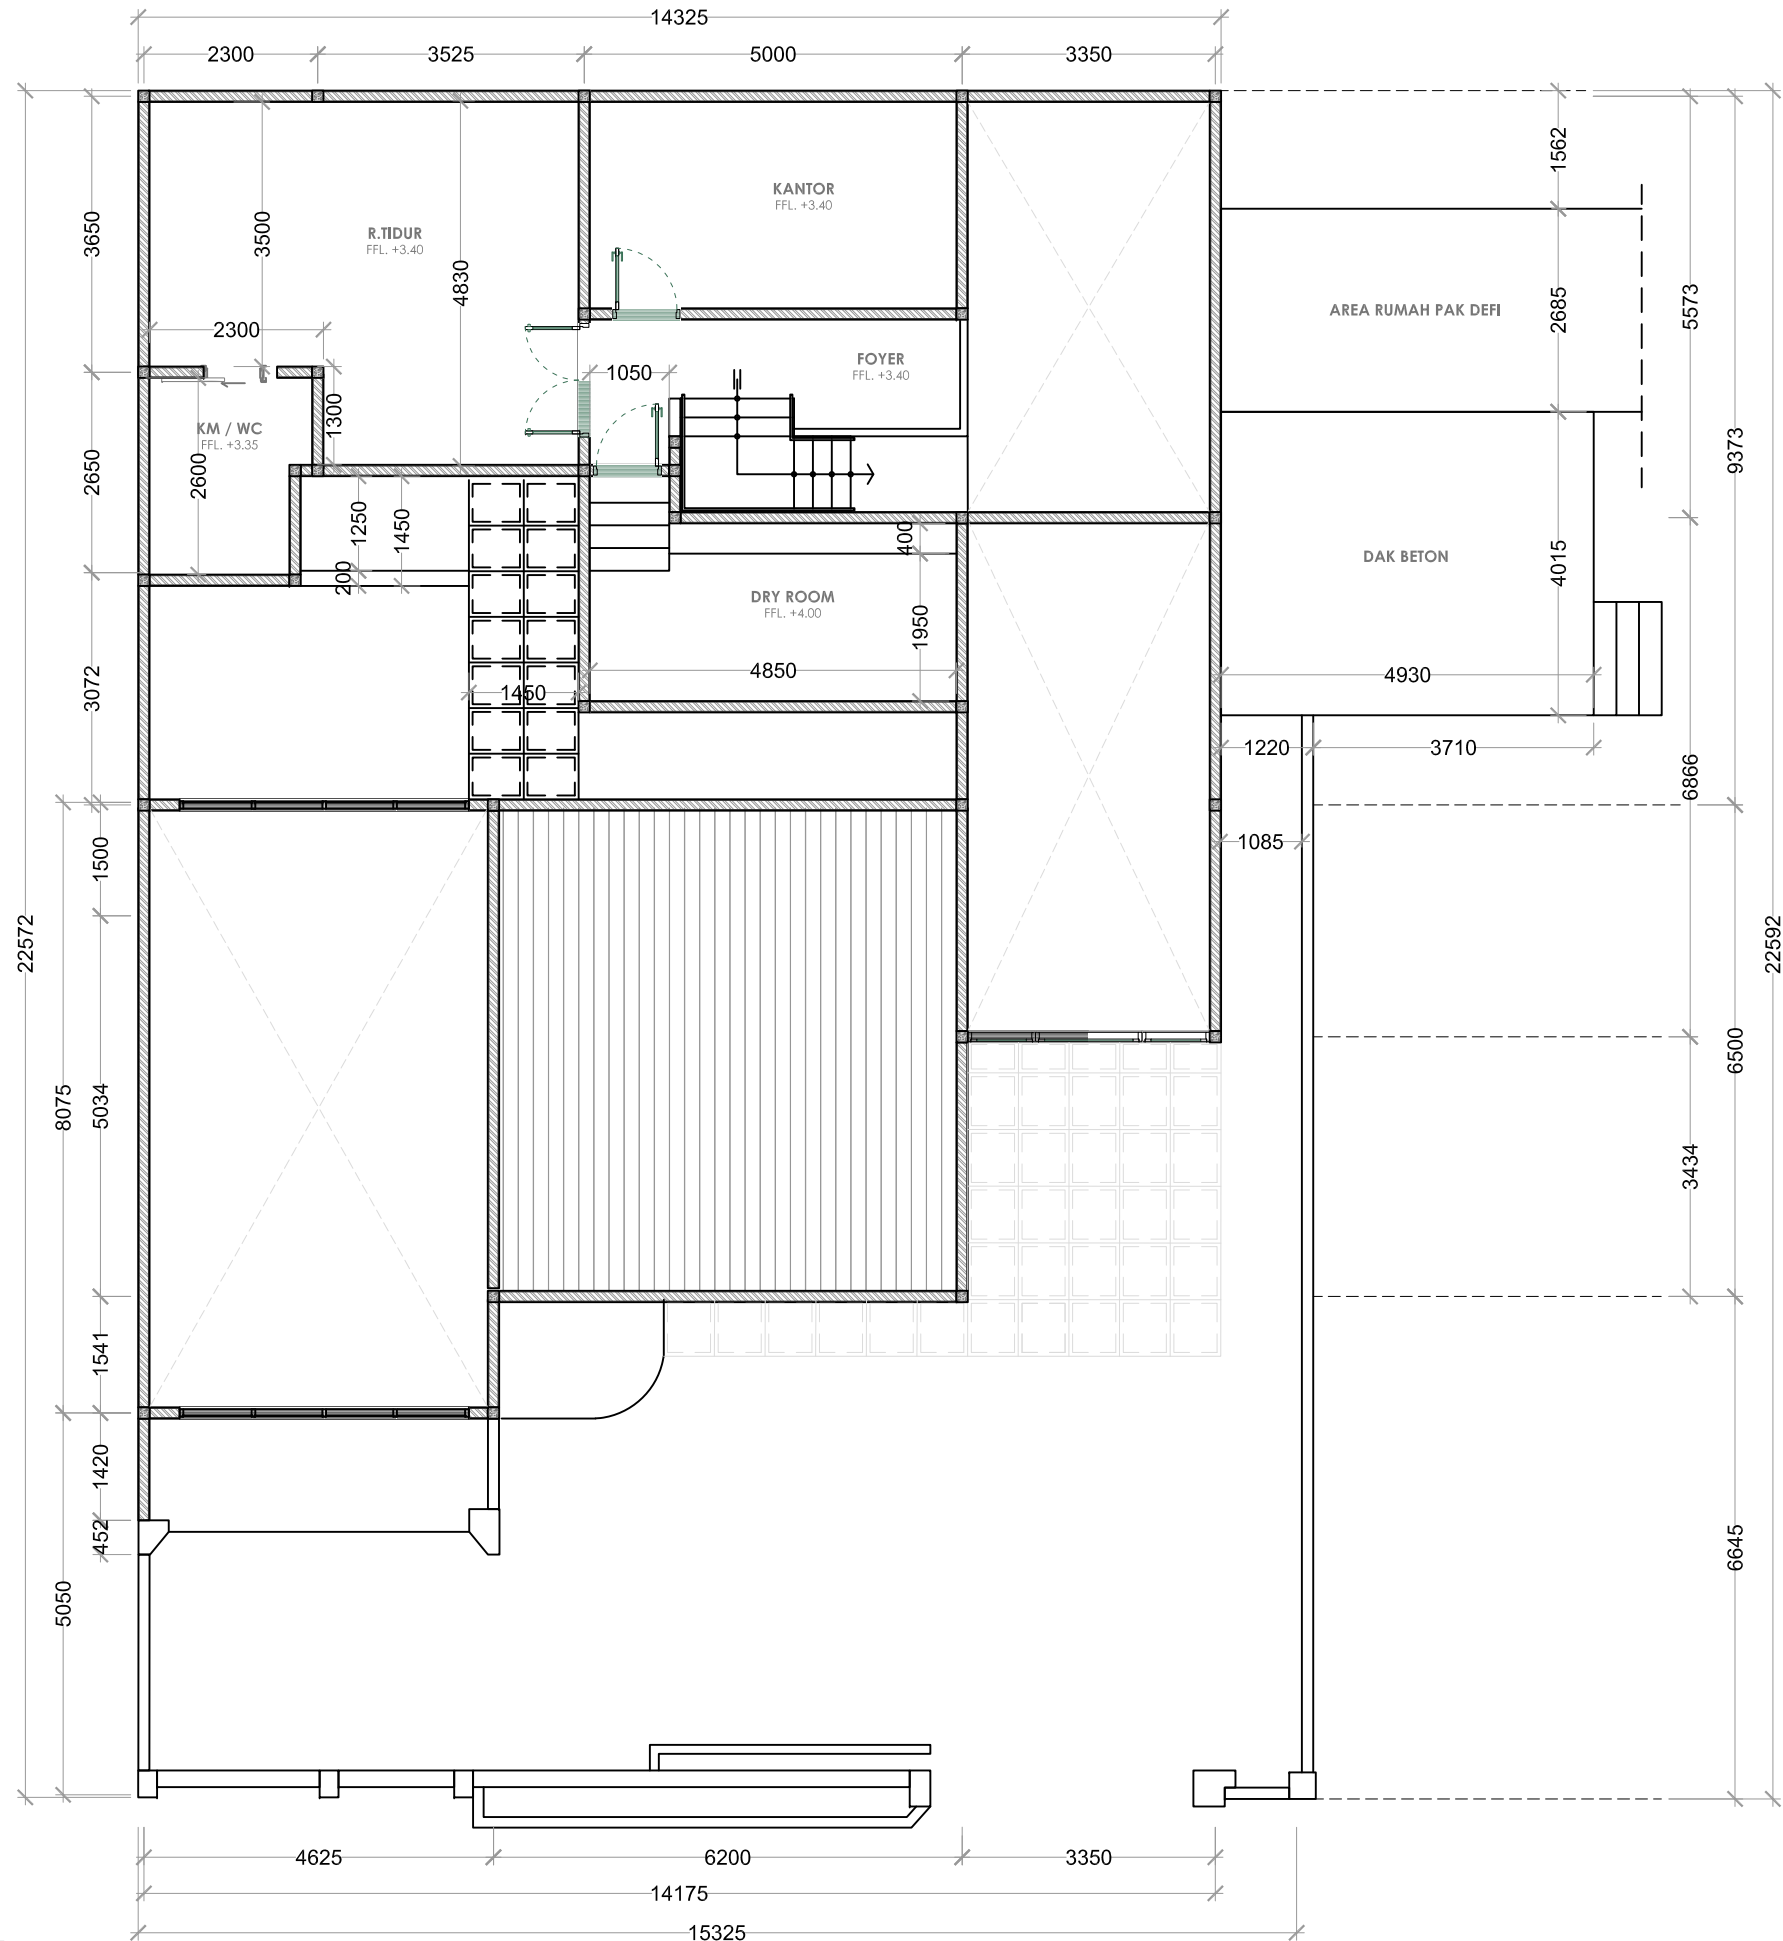


DENAH EXISTING LT. 2
SKALA 1:100

KONSULTAN			
KONTRAKTOR			
PROYEK			
KETERANGAN			
REVISI		TGL	BLN
ARSITEK			
DIGAMBAR			
DIPERIKSA			
DISETUJUI			
NO. PROYEK			
-			
NAMA GAMBAR			
DENAH EXISTING			
LANTAI 2			
SKALA		1 : 100	
AR-002			
SUBKAT	NO. LEMBAR		

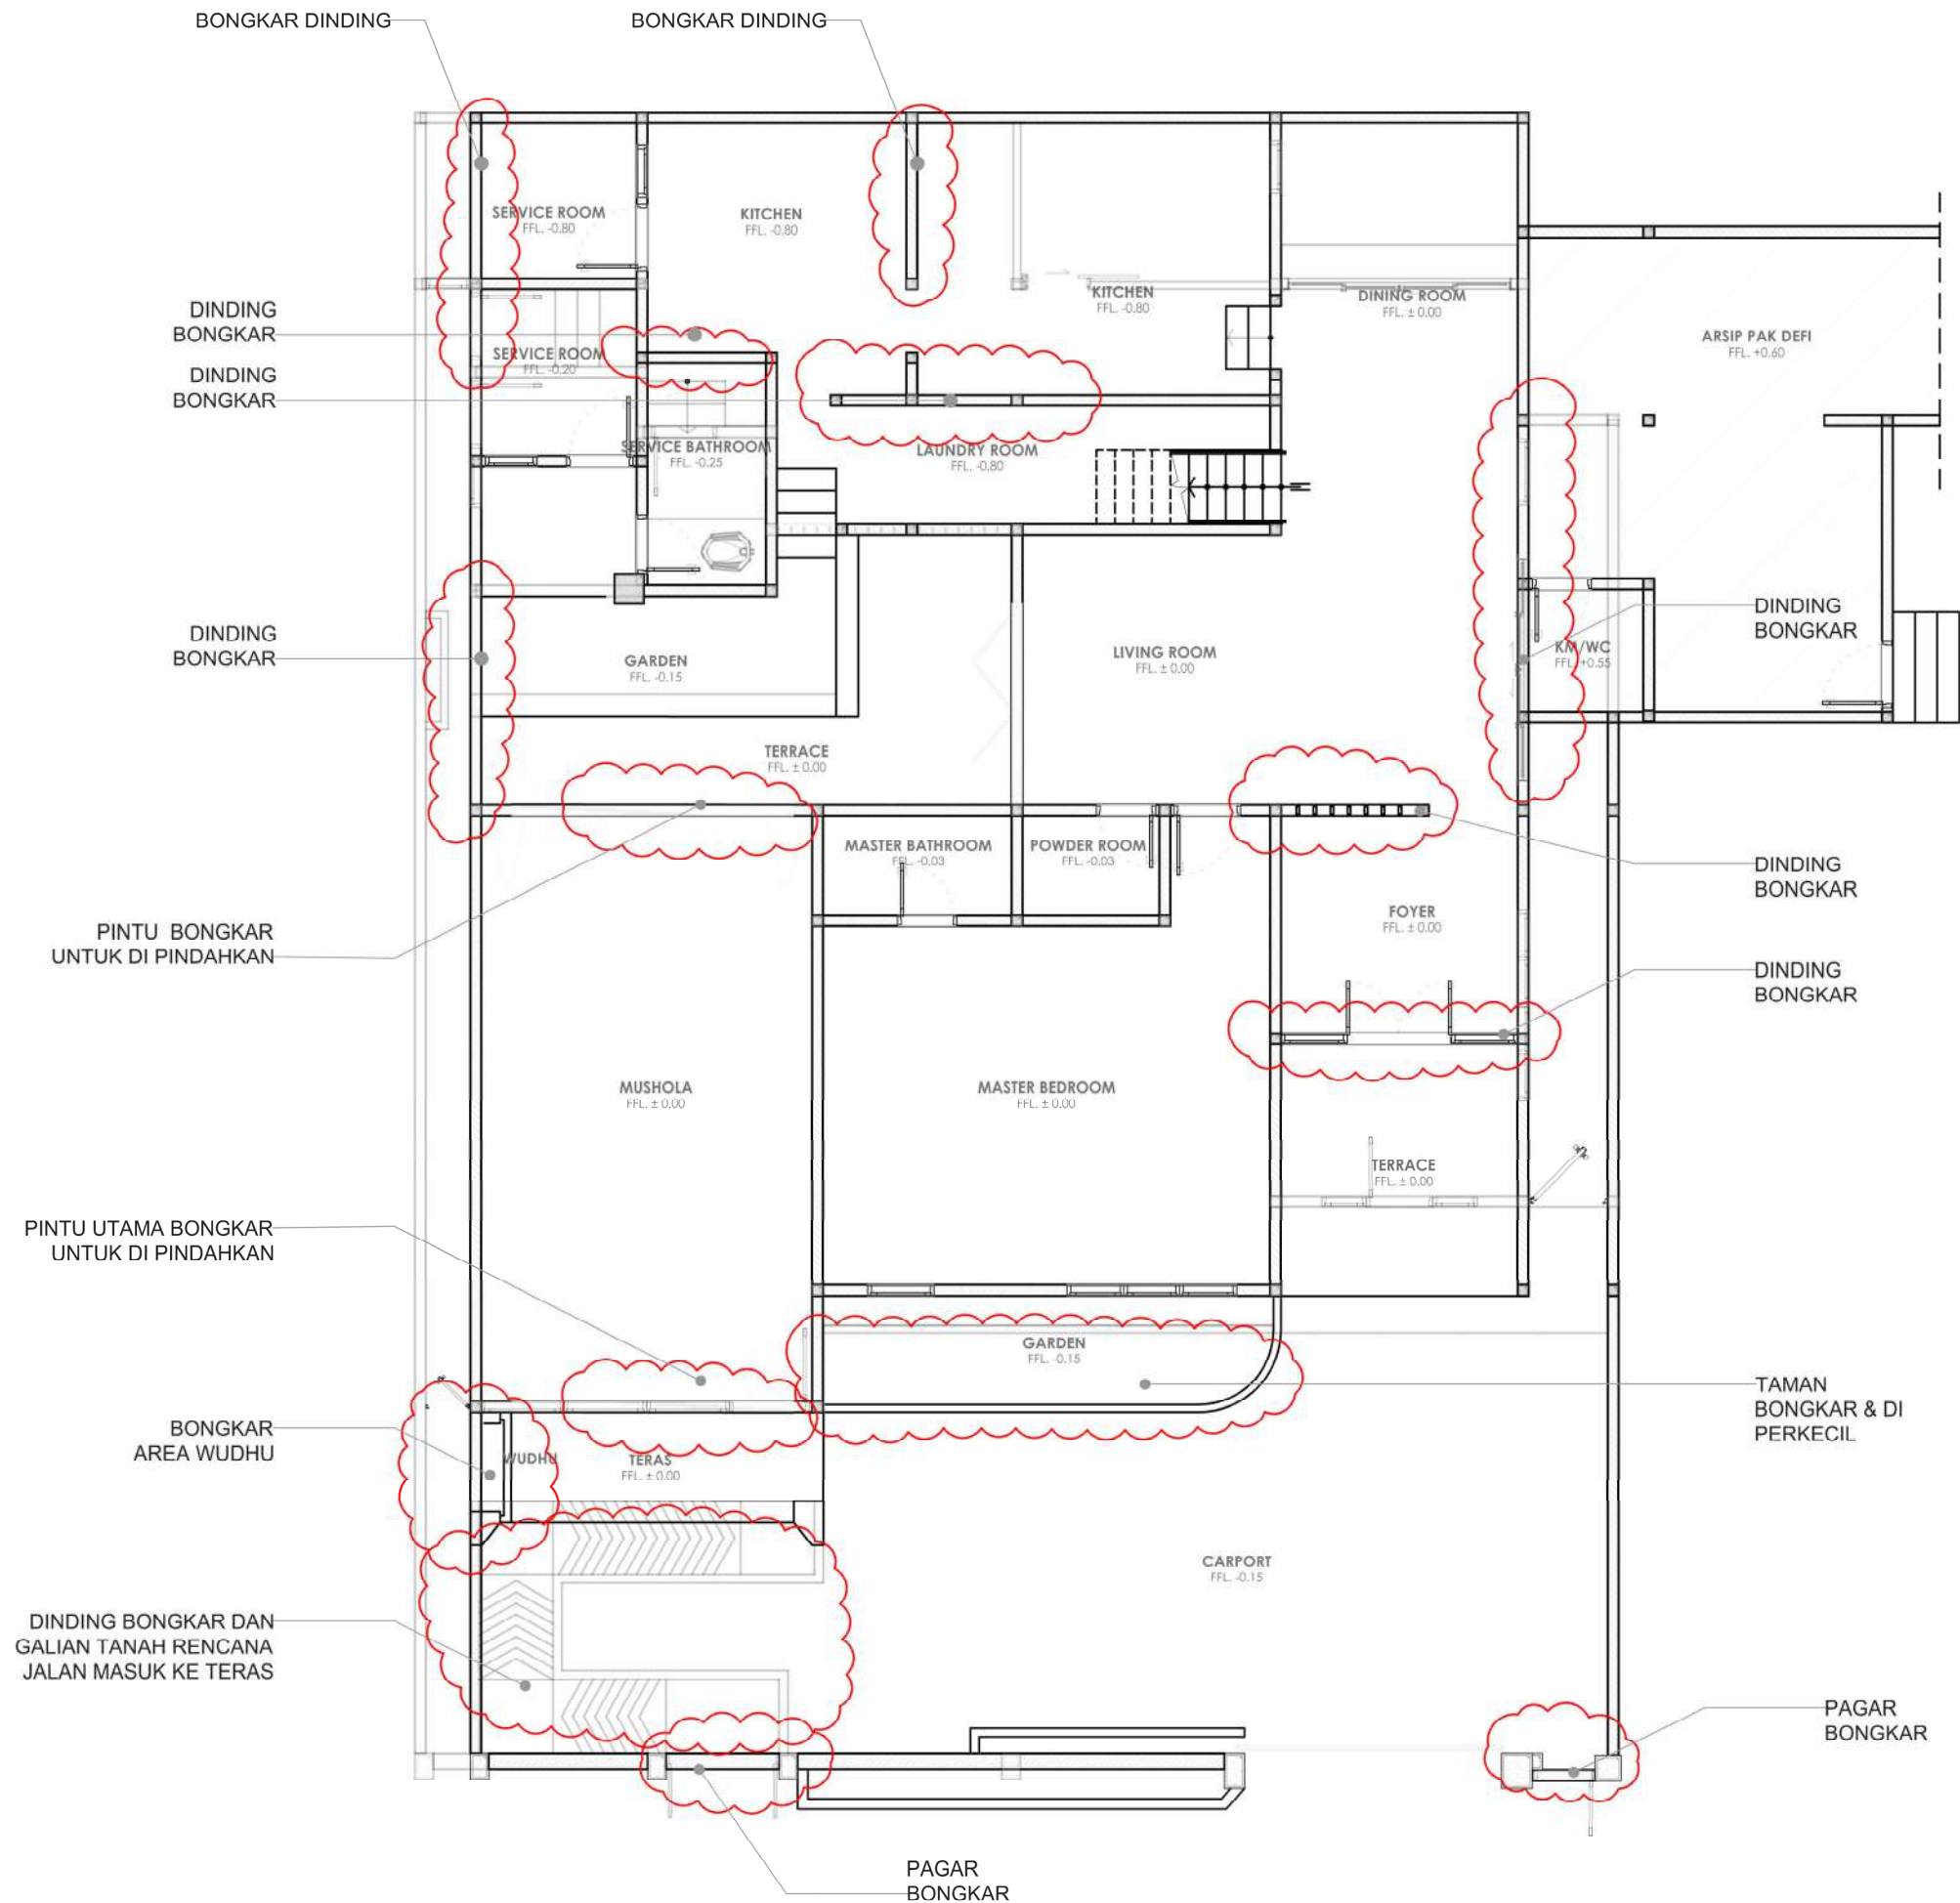

DENAH PEMBONGKARAN LT. 1
SKALA 1:100

KONSULTAN			
KONTRAKTOR			
PROYEK			
KETERANGAN			
REVISI	TGL	BLN	THN
ARSITEK			
DIGAMBAR			
DIPERIKSA			
DISETUJUI			
NO. PROYEK			
-			
NAMA GAMBAR			
DENAH PEMBONGKARAN LANTAI 1			
SKALA			
1 : 100			
AR-003			
SUBKAT	NO. LEMBAR		

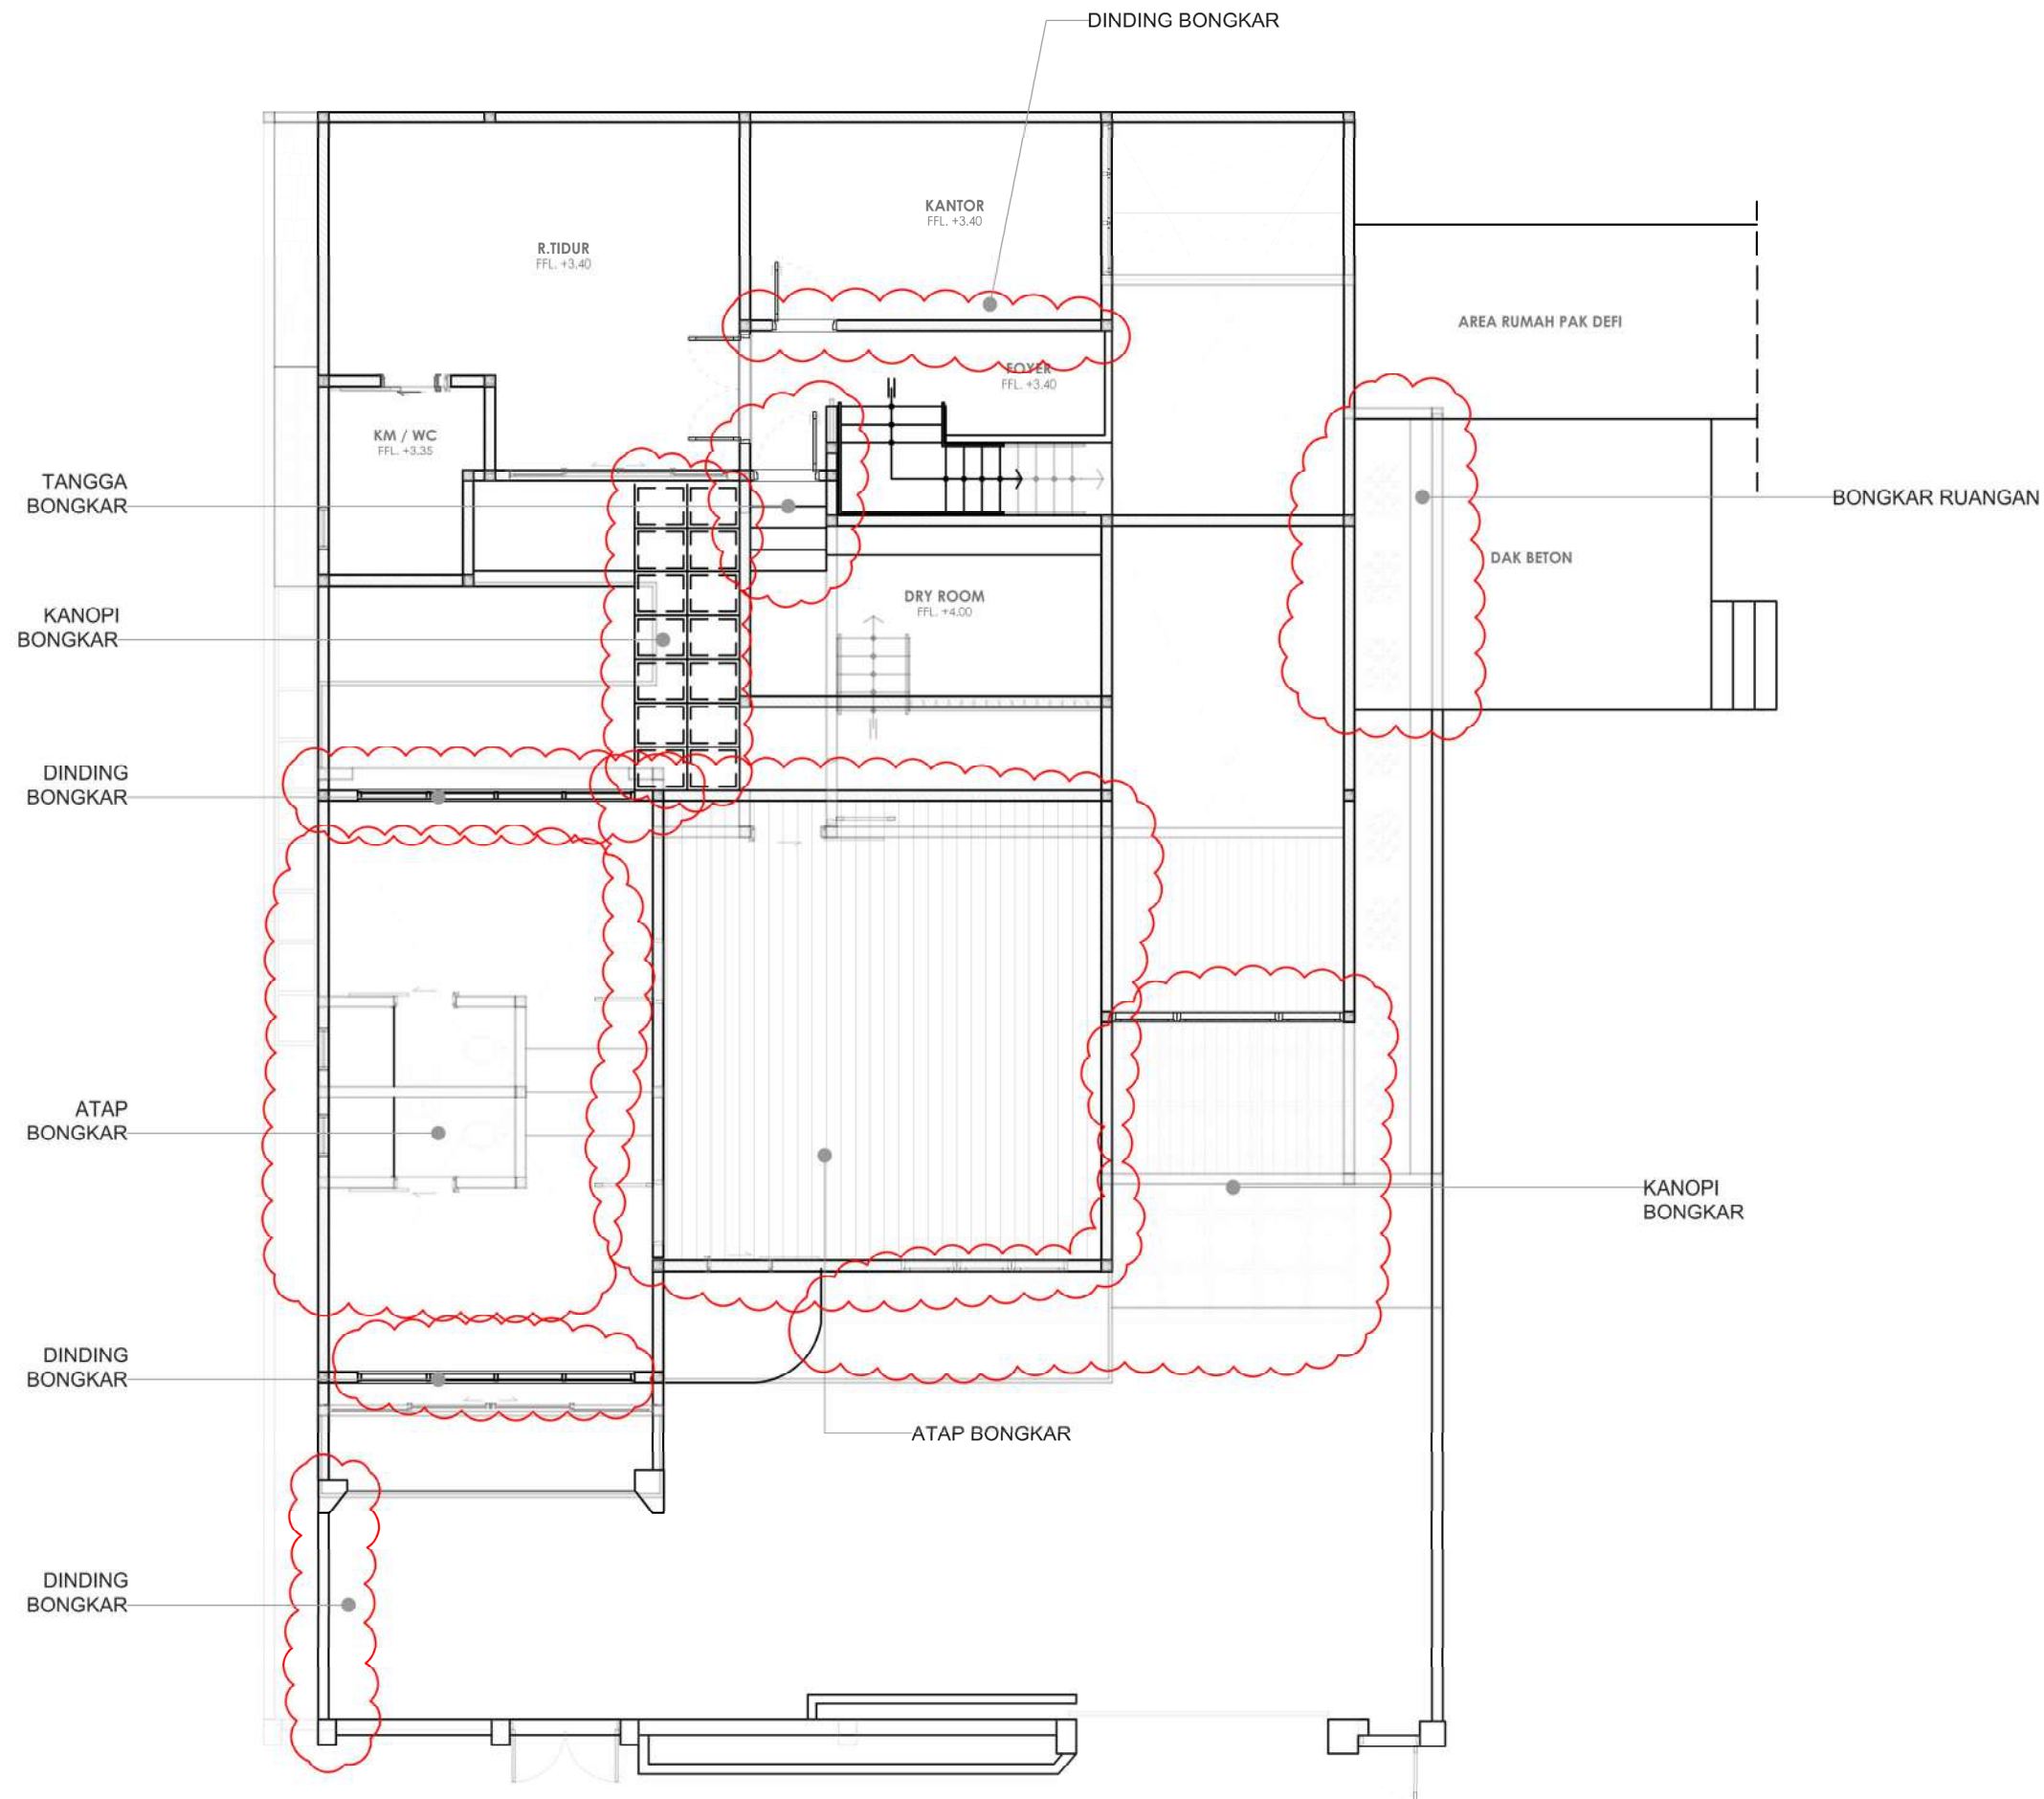


DENAH PEMBONGKARAN LT. 2
SKALA 1:100

KONSULTAN			
KONTRAKTOR			
PROYEK			
KETERANGAN			
REVISI	TGL	BLN	THN
ARSITEK			
DIGAMBAR			
DIPERIKSA			
DISETUIJUI			
NO. PROYEK			
-			
NAMA GAMBAR			
DENAH PEMBONGKARAN LANTAI 2			
SKALA 1 : 100			
AR-004			
SUBKAT	NO. LEMBAR		

DENAH LT. 1

SKALA 1:100

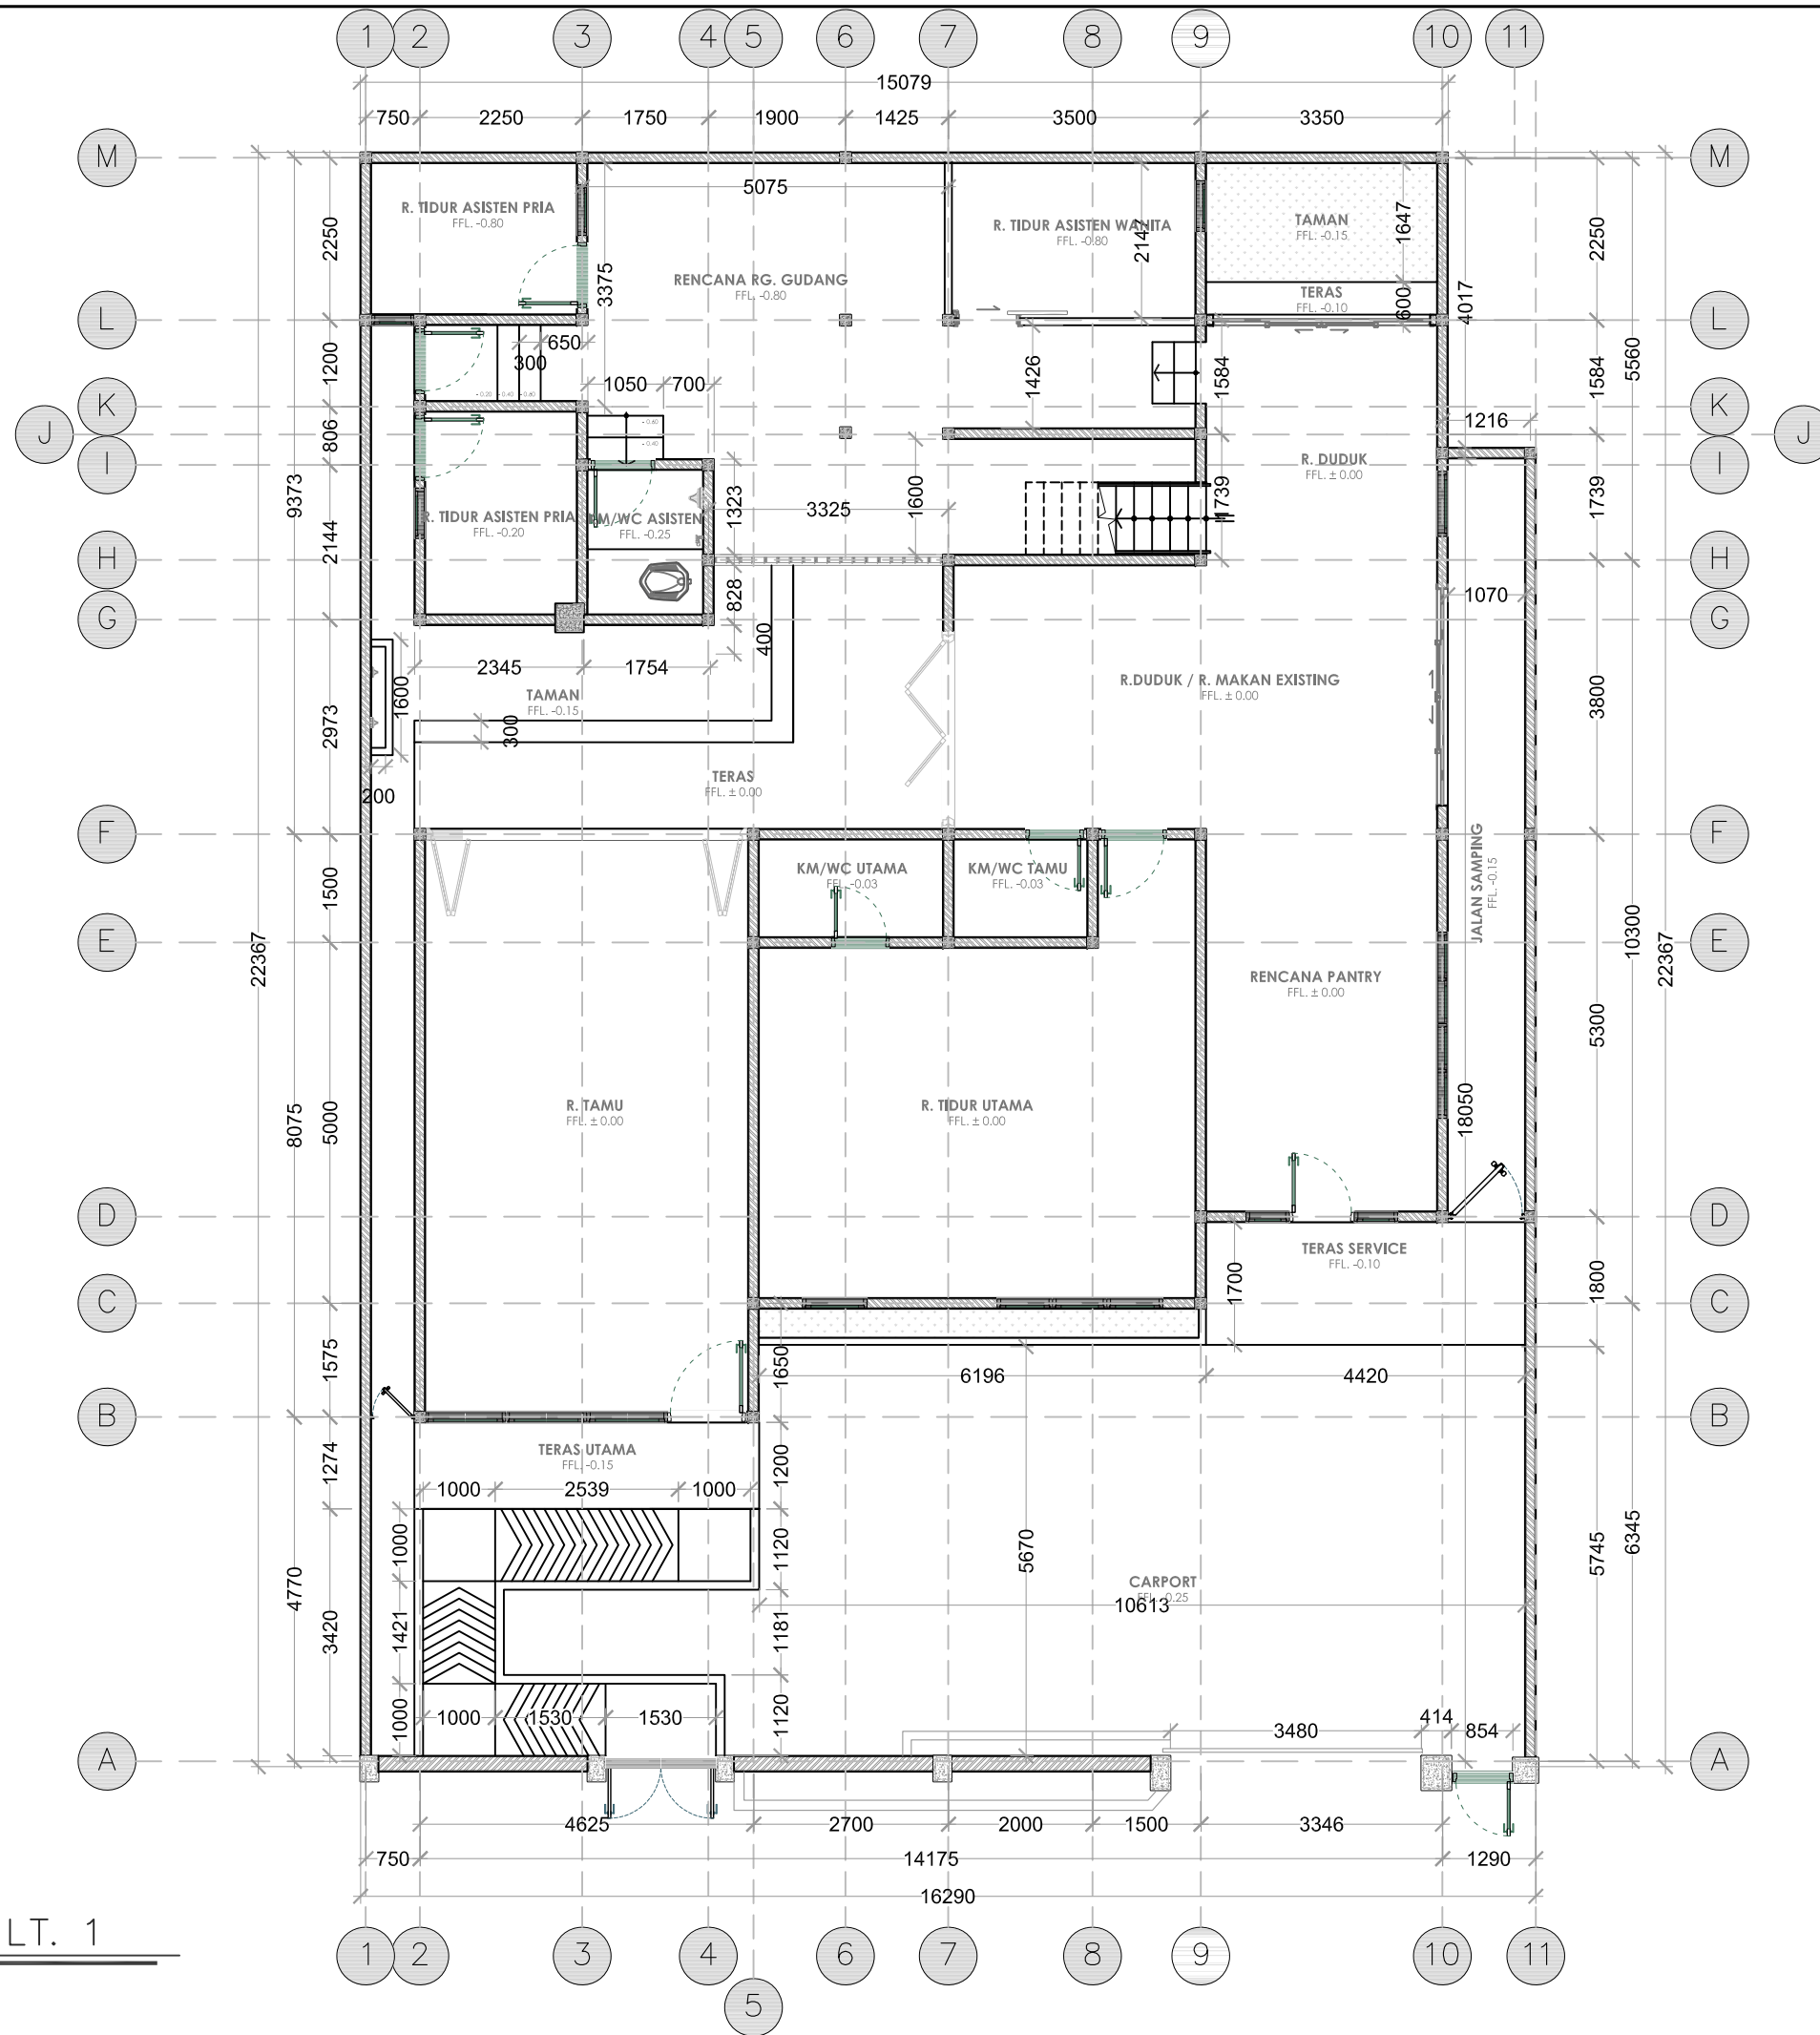

KONSULTAN

KONTRAKTOR

PROYEK

KETERANGAN

REVISI

	TGL	BLN	THN

ARSITEK

DIGAMBAR

DIPERIKSA

DISETUJUI

NO. PROYEK

NAMA GAMBAR

DENAH
LANTAI 1


SKALA

1 : 100

AR-005


SUBKAT

NO. LEMBAR

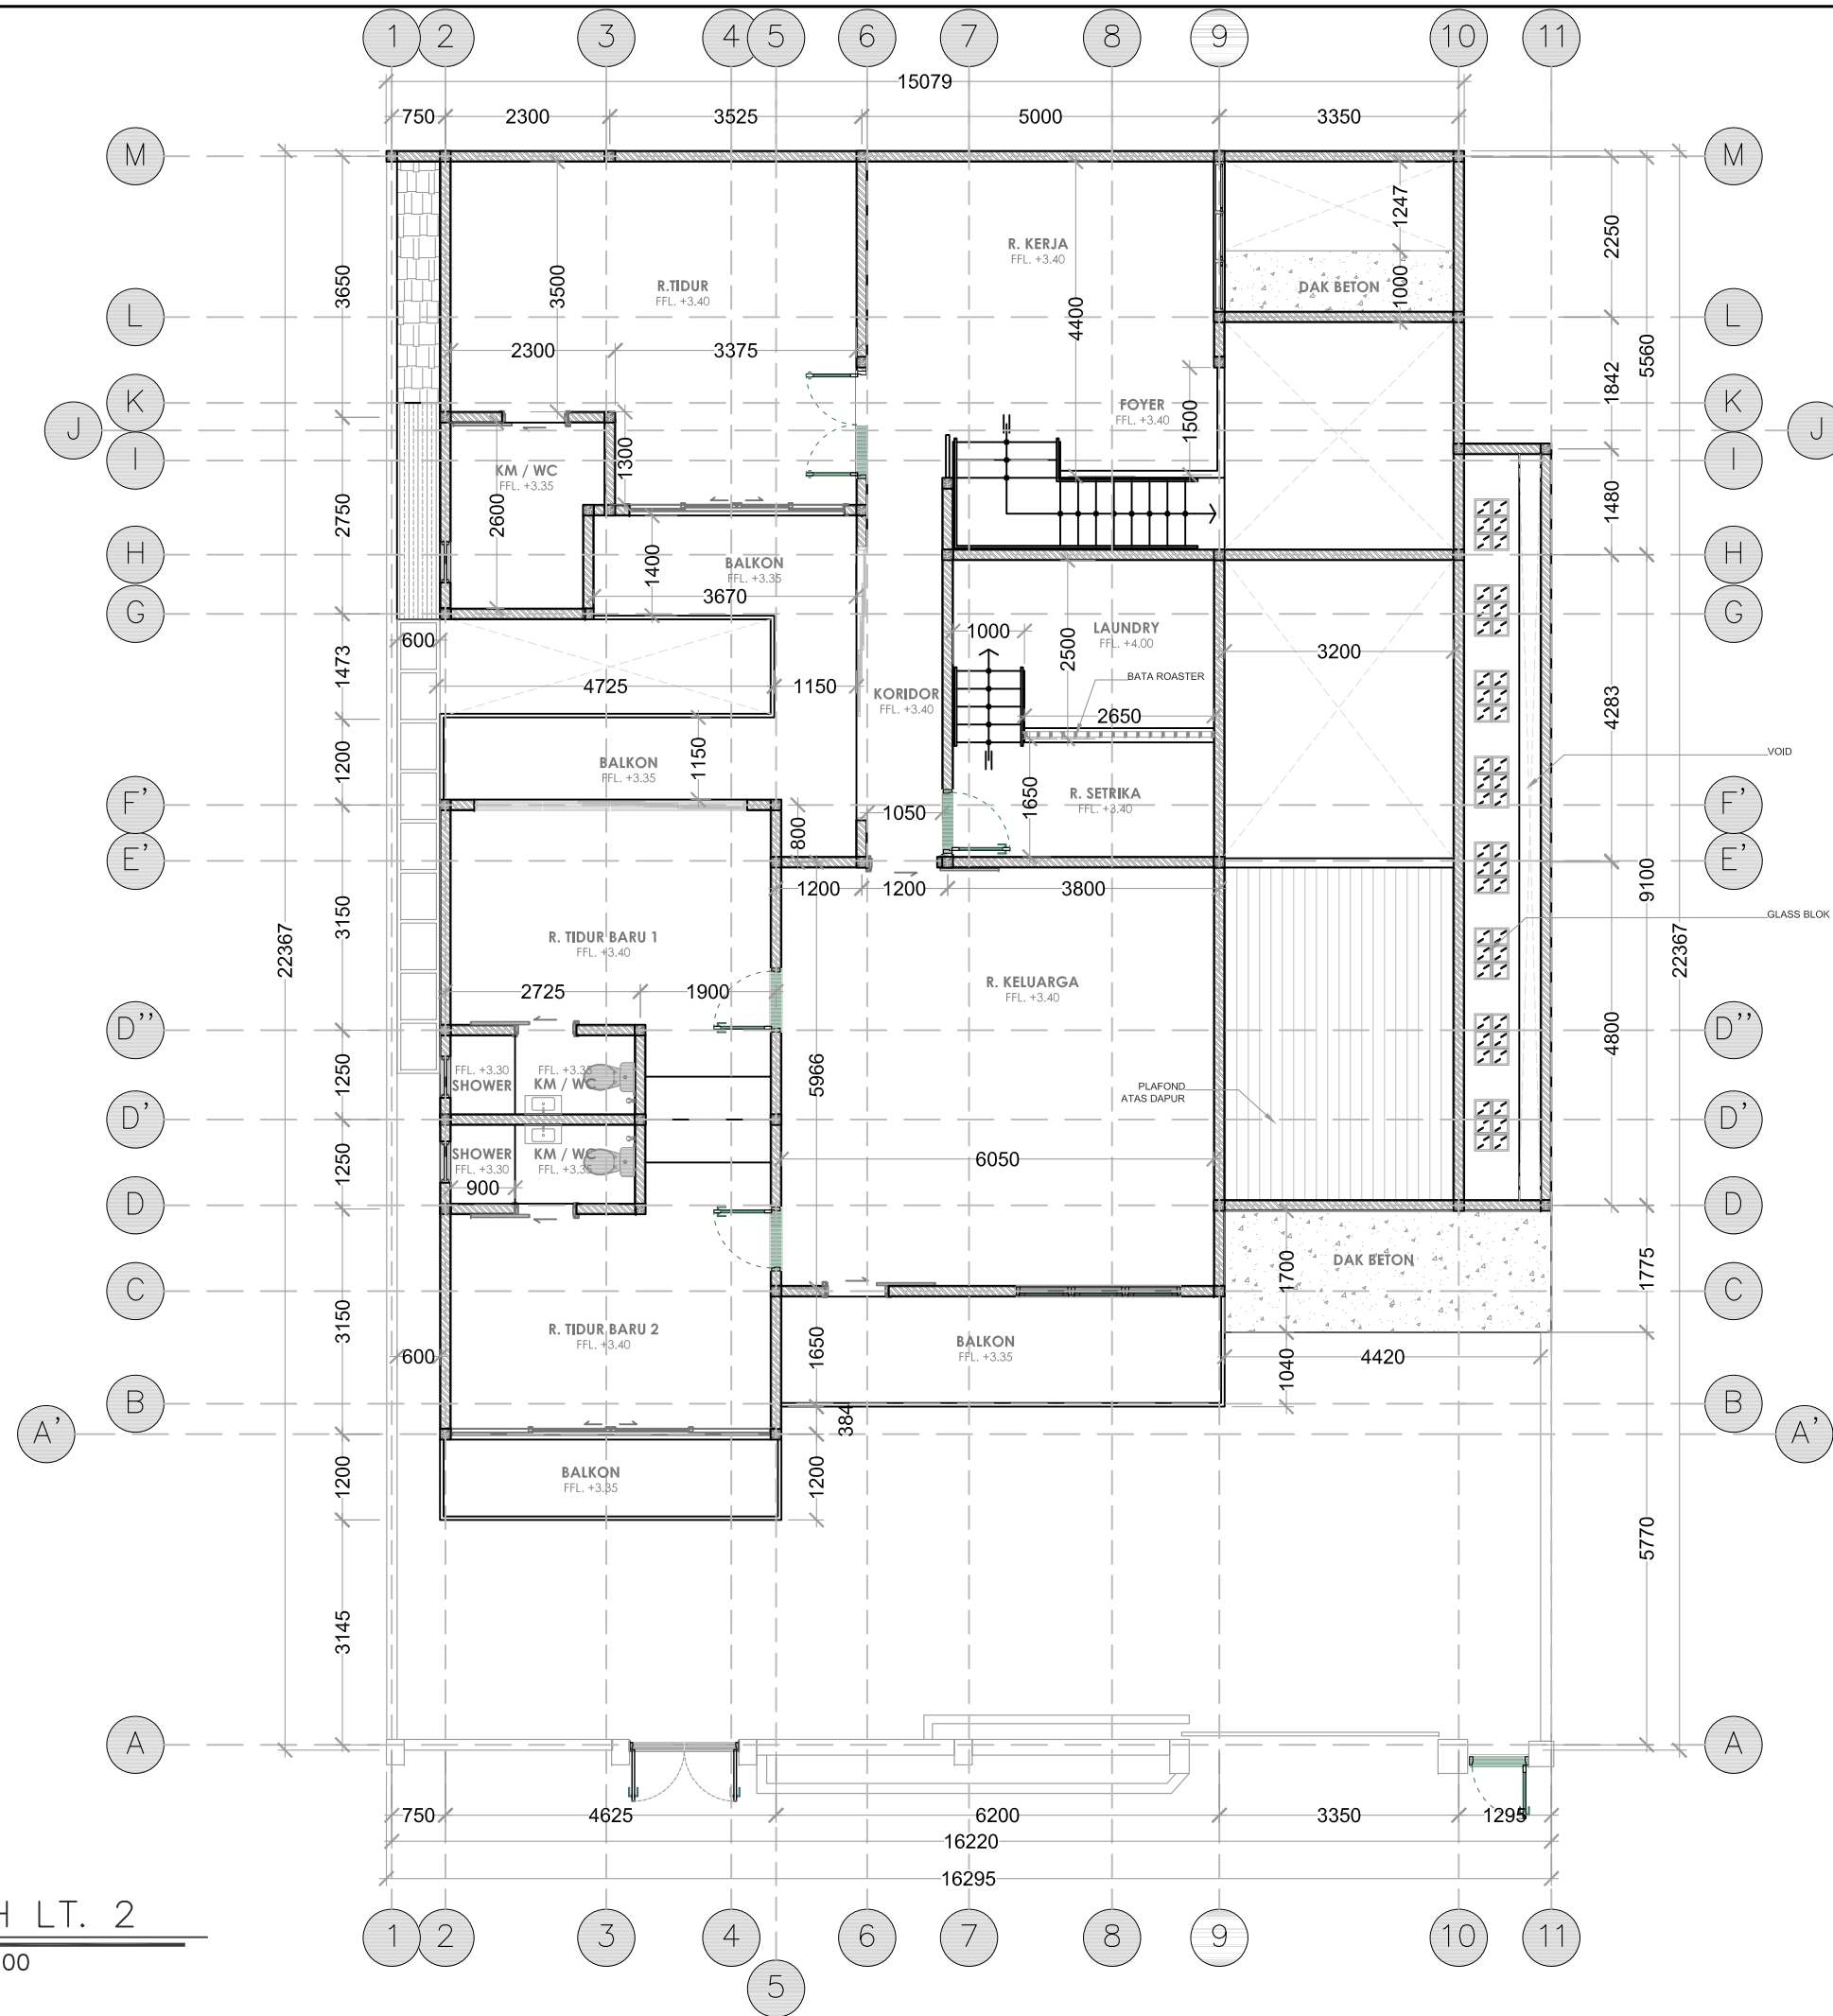

DENAH LT. 2
SKALA 1:100

KONSULTAN		
KONTRAKTOR		
PROYEK		
KETERANGAN		
REVISI		
	TGL	BLN
ARSITEK		
DIGAMBAR		
DIPERIKSA		
DISETUJUI		
NO. PROYEK		
-		
NAMA GAMBAR		
DENAH LANTAI 2		
SKALA 1 : 100		
AR-006		
SUBKAT	NO. LEMBAR	

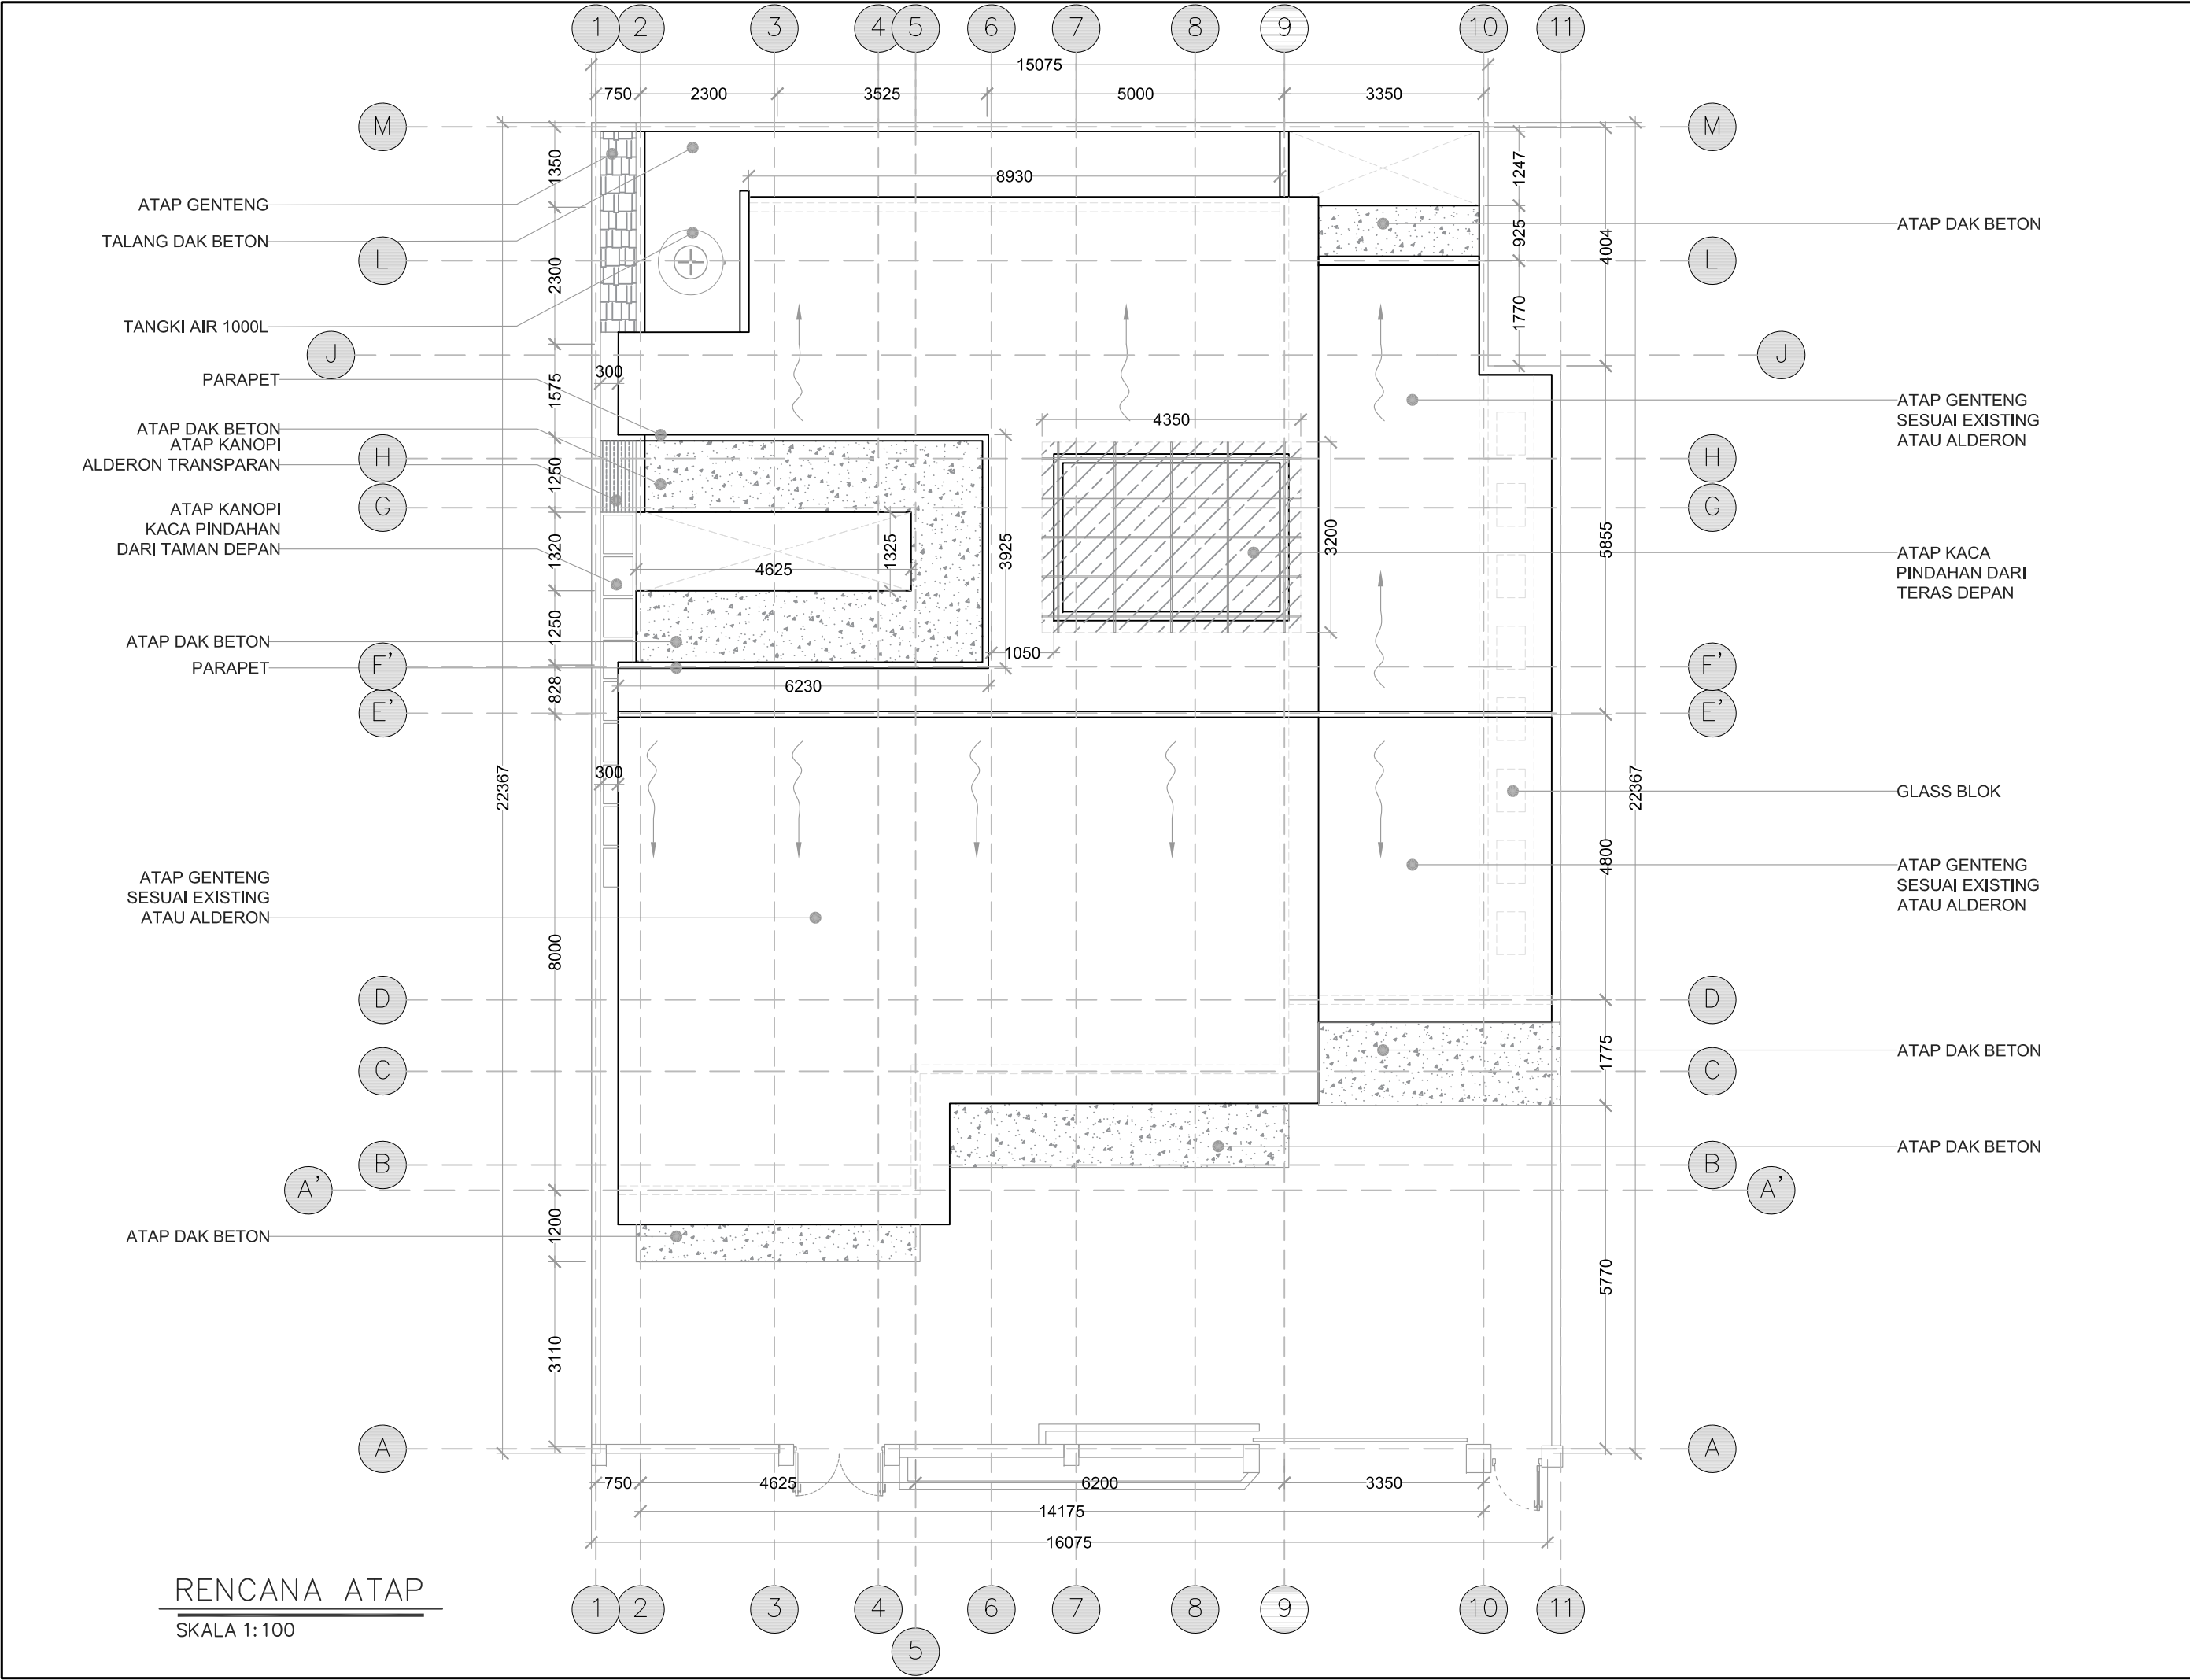

RENCANA ATAP
SKALA 1:100

KONSULTAN			
KONTRAKTOR			
PROYEK			
KETERANGAN			
REVISI		TGL	BLN
ARSITEK			
DIGAMBAR			
DIPERIKSA			
DISETUJUI			
NO. PROYEK			
-			
NAMA GAMBAR			
RENCANA ATAP			
SKALA 1 : 100			
AR-007			
SUBKAT		NO. LEMBAR	



PERSPEKTIF
SKALA NTS

KONSULTAN				
KONTRAKTOR				
PROYEK				
KETERANGAN				
REVISI		TGL	BLN	THN
ARSITEK				
DIGAMBAR				
DIPERIKSA				
DISETUUJUI				
NO. PROYEK				
-				
NAMA GAMBAR				
PERSPEKTIF				
SKALA				
NTS				
AR-000		0	0	0
SUBKAT		NO. LEMBAR		



PERSPEKTIF

SKALA NTS

KONSULTAN				
KONTRAKTOR				
PROYEK				
KETERANGAN				
REVISI		TGL	BLN	THN
ARSITEK				
DIGAMBAR				
DIPERIKSA				
DISETUJUI				
NO. PROYEK				
-				
NAMA GAMBAR				
PERSPEKTIF				
SKALA				
NTS				
AR-000		0	0	0
SUBKAT		NO. LEMBAR		



PERSPEKTIF


SKALA NTS

KONSULTAN				
KONTRAKTOR				
PROYEK				
KETERANGAN				
REVISI		TGL	BLN	THN
ARSITEK				
DIGAMBAR				
DIPERIKSA				
DISETUUJUI				
NO. PROYEK				
-				
NAMA GAMBAR				
PERSPEKTIF				
SKALA				
NTS				
AR-000		0	0	0
SUBKAT		NO. LEMBAR		



PERSPEKTIF
SKALA NTS

KONSULTAN				
KONTRAKTOR				
PROYEK				
KETERANGAN				
REVISI		TGL	BLN	THN
ARSITEK				
DIGAMBAR				
DIPERIKSA				
DISETUUJUI				
NO. PROYEK				
-				
NAMA GAMBAR				
PERSPEKTIF				
SKALA				
NTS				
AR-000		0	0	0
SUBKAT		NO. LEMBAR		

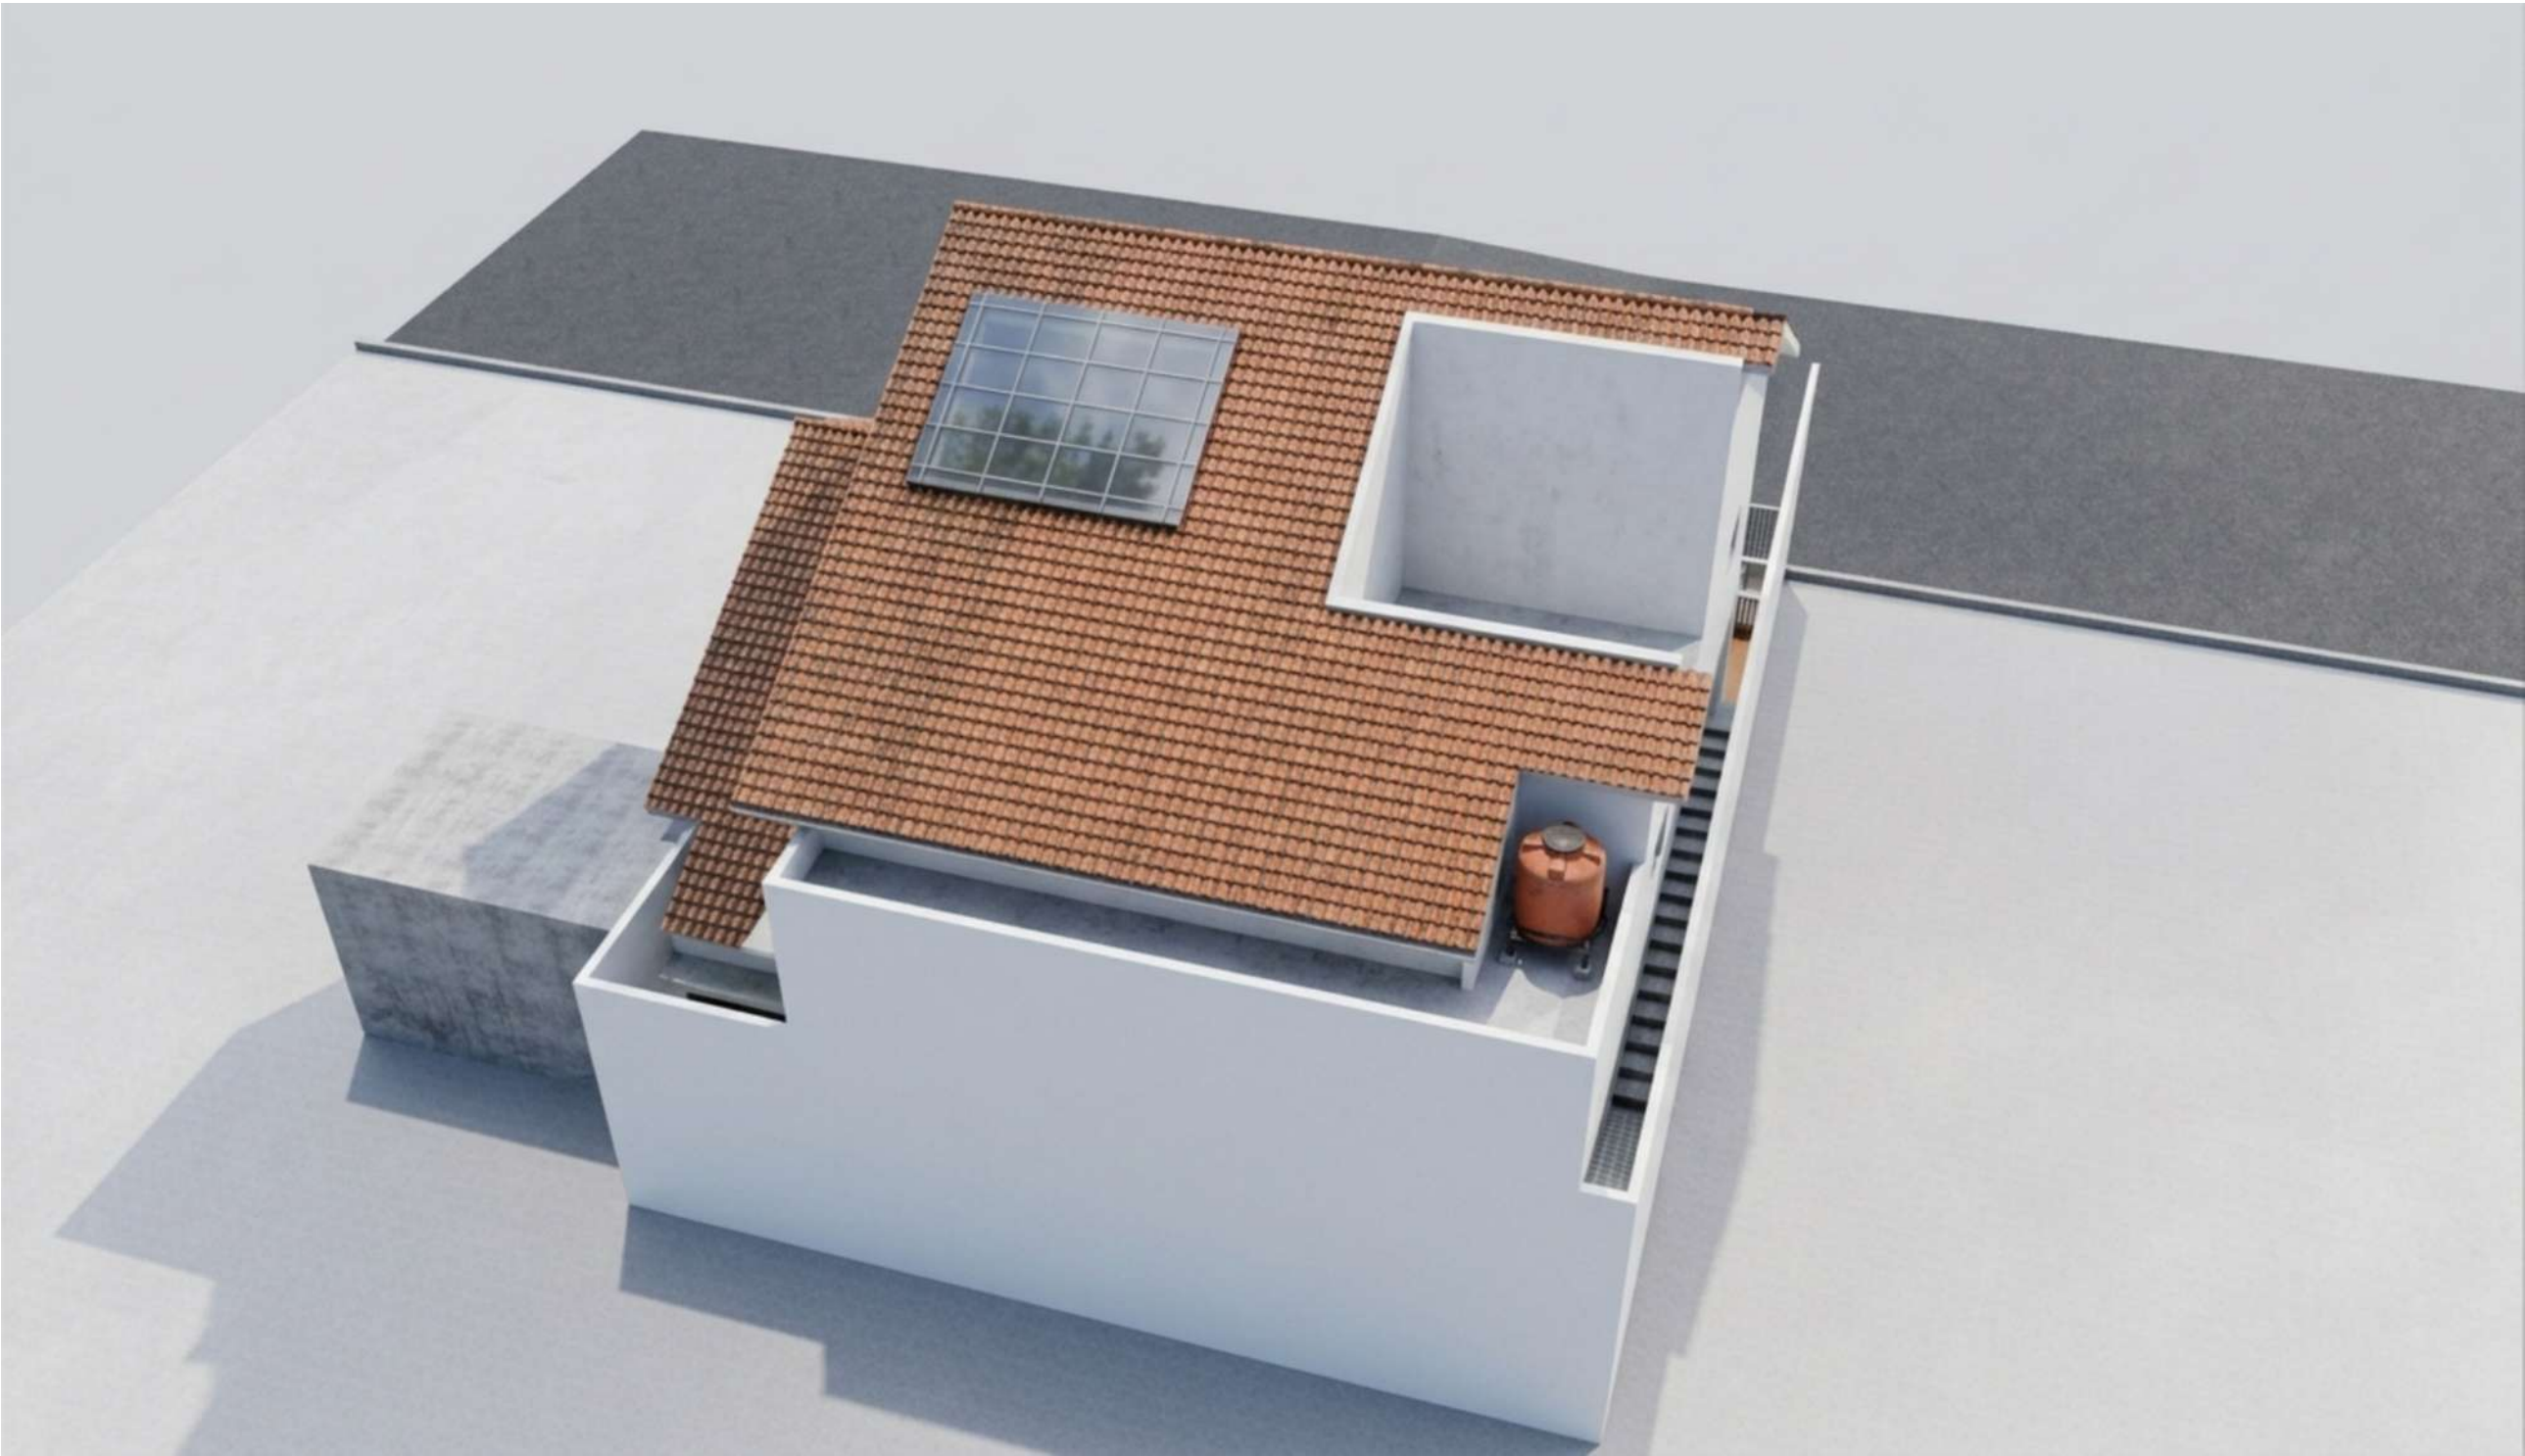

PERSPEKTIF

SKALA NTS

KONSULTAN				
KONTRAKTOR				
PROYEK				
KETERANGAN				
REVISI		TGL	BLN	THN
ARSITEK				
DIGAMBAR				
DIPERIKSA				
DISETUJUI				
NO. PROYEK				
-				
NAMA GAMBAR				
PERSPEKTIF				
SKALA				
NTS				
AR-000		0	0	0
SUBKAT		NO. LEMBAR		



PERSPEKTIF

SKALA NTS

KONSULTAN				
KONTRAKTOR				
PROYEK				
KETERANGAN				
REVISI		TGL	BLN	THN
ARSITEK				
DIGAMBAR				
DIPERIKSA				
DISETUJUI				
NO. PROYEK				
-				
NAMA GAMBAR				
PERSPEKTIF				
SKALA				
NTS				
AR-000		0	0	0
SUBKAT		NO. LEMBAR		



PERSPEKTIF

SKALA NTS

KONSULTAN				
KONTRAKTOR				
PROYEK				
KETERANGAN				
REVISI		TGL	BLN	THN
ARSITEK				
DIGAMBAR				
DIPERIKSA				
DISETUUJUI				
NO. PROYEK				
-				
NAMA GAMBAR				
PERSPEKTIF				
SKALA				
NTS				
AR-000				
SUBKAT		NO. LEMBAR		



PERSPEKTIF
SKALA NTS

KONSULTAN				
KONTRAKTOR				
PROYEK				
KETERANGAN				
REVISI		TGL	BLN	THN
ARSITEK				
DIGAMBAR				
DIPERIKSA				
DISETUUJUI				
NO. PROYEK				
-				
NAMA GAMBAR				
PERSPEKTIF				
SKALA				
NTS				
AR-000				
SUBKAT		NO. LEMBAR		



PERSPEKTIF

SKALA NTS

KONSULTAN				
KONTRAKTOR				
PROYEK				
KETERANGAN				
REVISI		TGL	BLN	THN
ARSITEK				
DIGAMBAR				
DIPERIKSA				
DISETUUJUI				
NO. PROYEK				
-				
NAMA GAMBAR				
PERSPEKTIF				
SKALA				
NTS				
AR-000		0	0	0
SUBKAT		NO. LEMBAR		



PERSPEKTIF

SKALA NTS

KONSULTAN				
KONTRAKTOR				
PROYEK				
KETERANGAN				
REVISI		TGL	BLN	THN
ARSITEK				
DIGAMBAR				
DIPERIKSA				
DISETUIJUI				
NO. PROYEK				
-				
NAMA GAMBAR				
PERSPEKTIF				
SKALA				
NTS				
AR-000		0	0	0
SUBKAT		NO. LEMBAR		



PERSPEKTIF

SKALA NTS

KONSULTAN				
KONTRAKTOR				
PROYEK				
KETERANGAN				
REVISI		TGL	BLN	THN
ARSITEK				
DIGAMBAR				
DIPERIKSA				
DISETUIJUI				
NO. PROYEK				
-				
NAMA GAMBAR				
PERSPEKTIF				
SKALA				
NTS				
AR-000		0	0	0
SUBKAT		NO. LEMBAR		