

DOKUMEN GAMBAR PROPOSAL



PEMBANGUNAN RUMAH KAVLING JALAN JOE
JAGAKARSA
JAKARTA SELATAN



LUAS LAHAN

862.2 M²


GSB

101.9 M²


JL. JOE

LAHAN EXISTING

SKALA 1:150

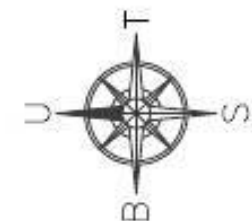


KONSULTAN			
KONTRAKTOR			
PROYEK			
TOWN HOUSE JALAN JOE JAGAKARSA JAKARTA SELATAN			
KETERANGAN			
REVISI			
ARSITEK			
DISAMBAH			
DIPERIKSA			
DIBETULUJ			
NO. PROYEK			
NAMA GAMBAR			
LAHAN EXISTING			
SKALA			
1 : 150			
AR-001			
SUBKAT		NO. LEMBAR	

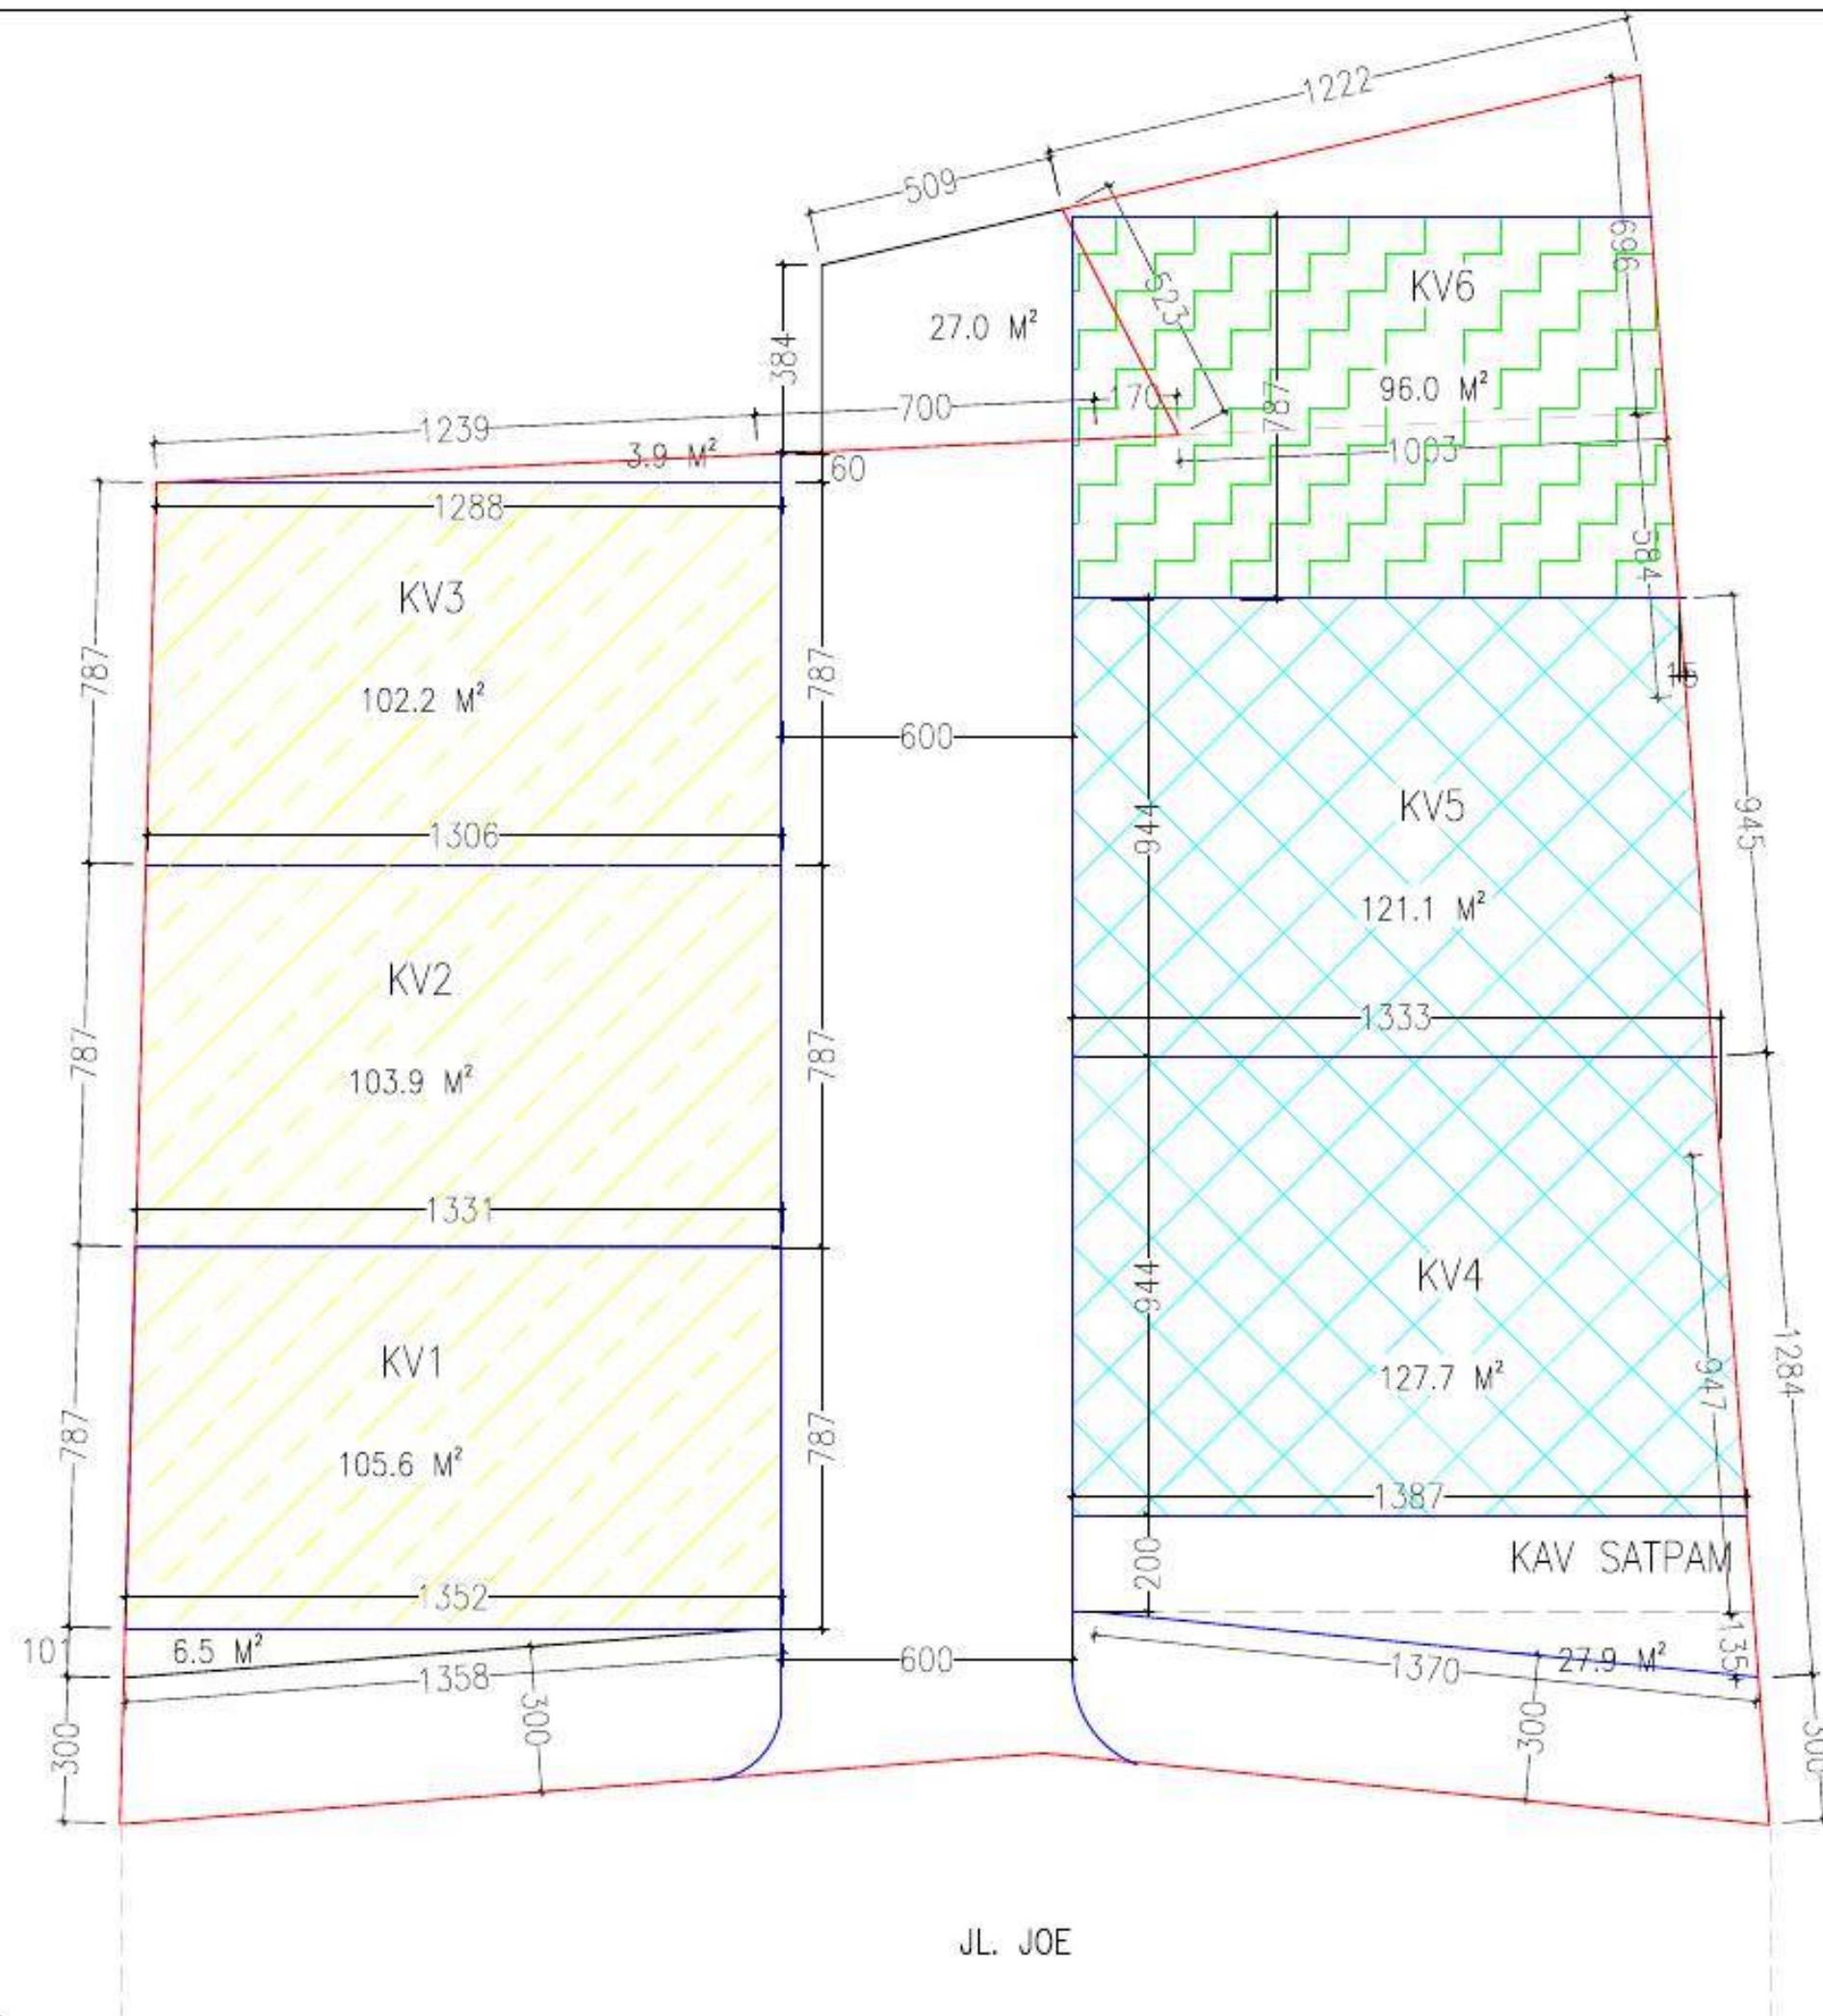

SITE PLAN
SKALA 1:150

JL. JOE

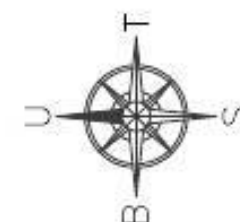


KONSULTAN	
KONTRAKTOR	
PROYEK	
TOWN HOUSE JALAN JOE JAGAKARSA JAKARTA SELATAN	
KETERANGAN	
REVISI	
NO.	REVISI
1	
2	
3	
4	
5	
6	
7	
8	
9	
10	
ARSITEK	
DISAMBAH	
DIPERIKSA	
DIBETULUJ	
NO. PROYEK	
NAMA GAMBAR	
SITE PLAN	
SKALA 1 : 150	
AR-002	
SUBKAT	NO. LEMBAR




SITE PLAN
SKALA 1:150

KONSULTAN	
KONTRAKTOR	
PROYEK	
TOWN HOUSE JALAN JOE JAGAKARSA JAKARTA SELATAN	
KETERANGAN	
REVISI	NO. KRS
ARSITEK	
DIKAMBAR	
DIPERIKSA	
DIBETULUJ	
NO. PROYEK	
NAMA GAMBAR	
SITE PLAN	
SKALA	1 : 150
AR-003	
SUBKAT	NO. LEMBAR

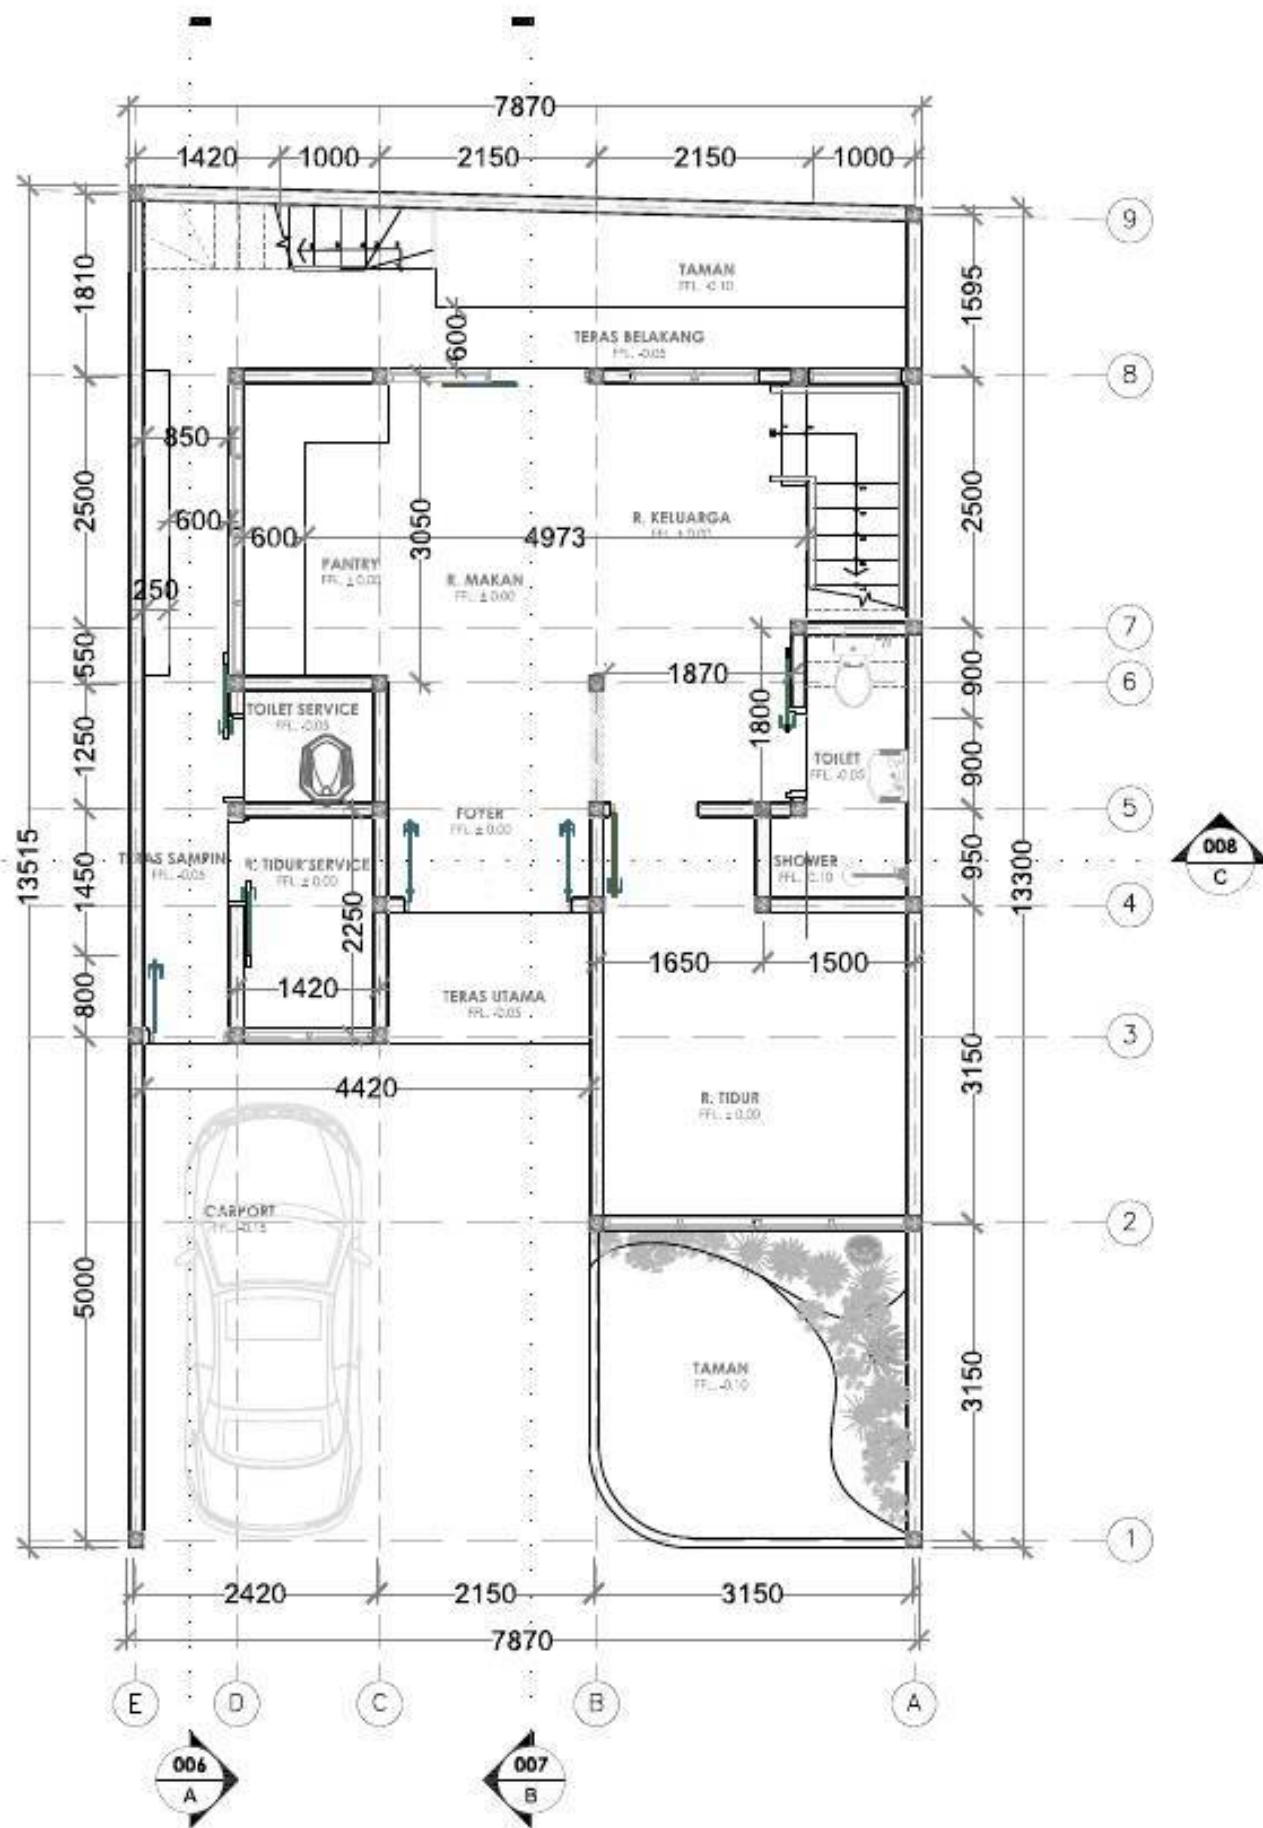

DENAH LANTAI DASAR


SKALA 1: 75

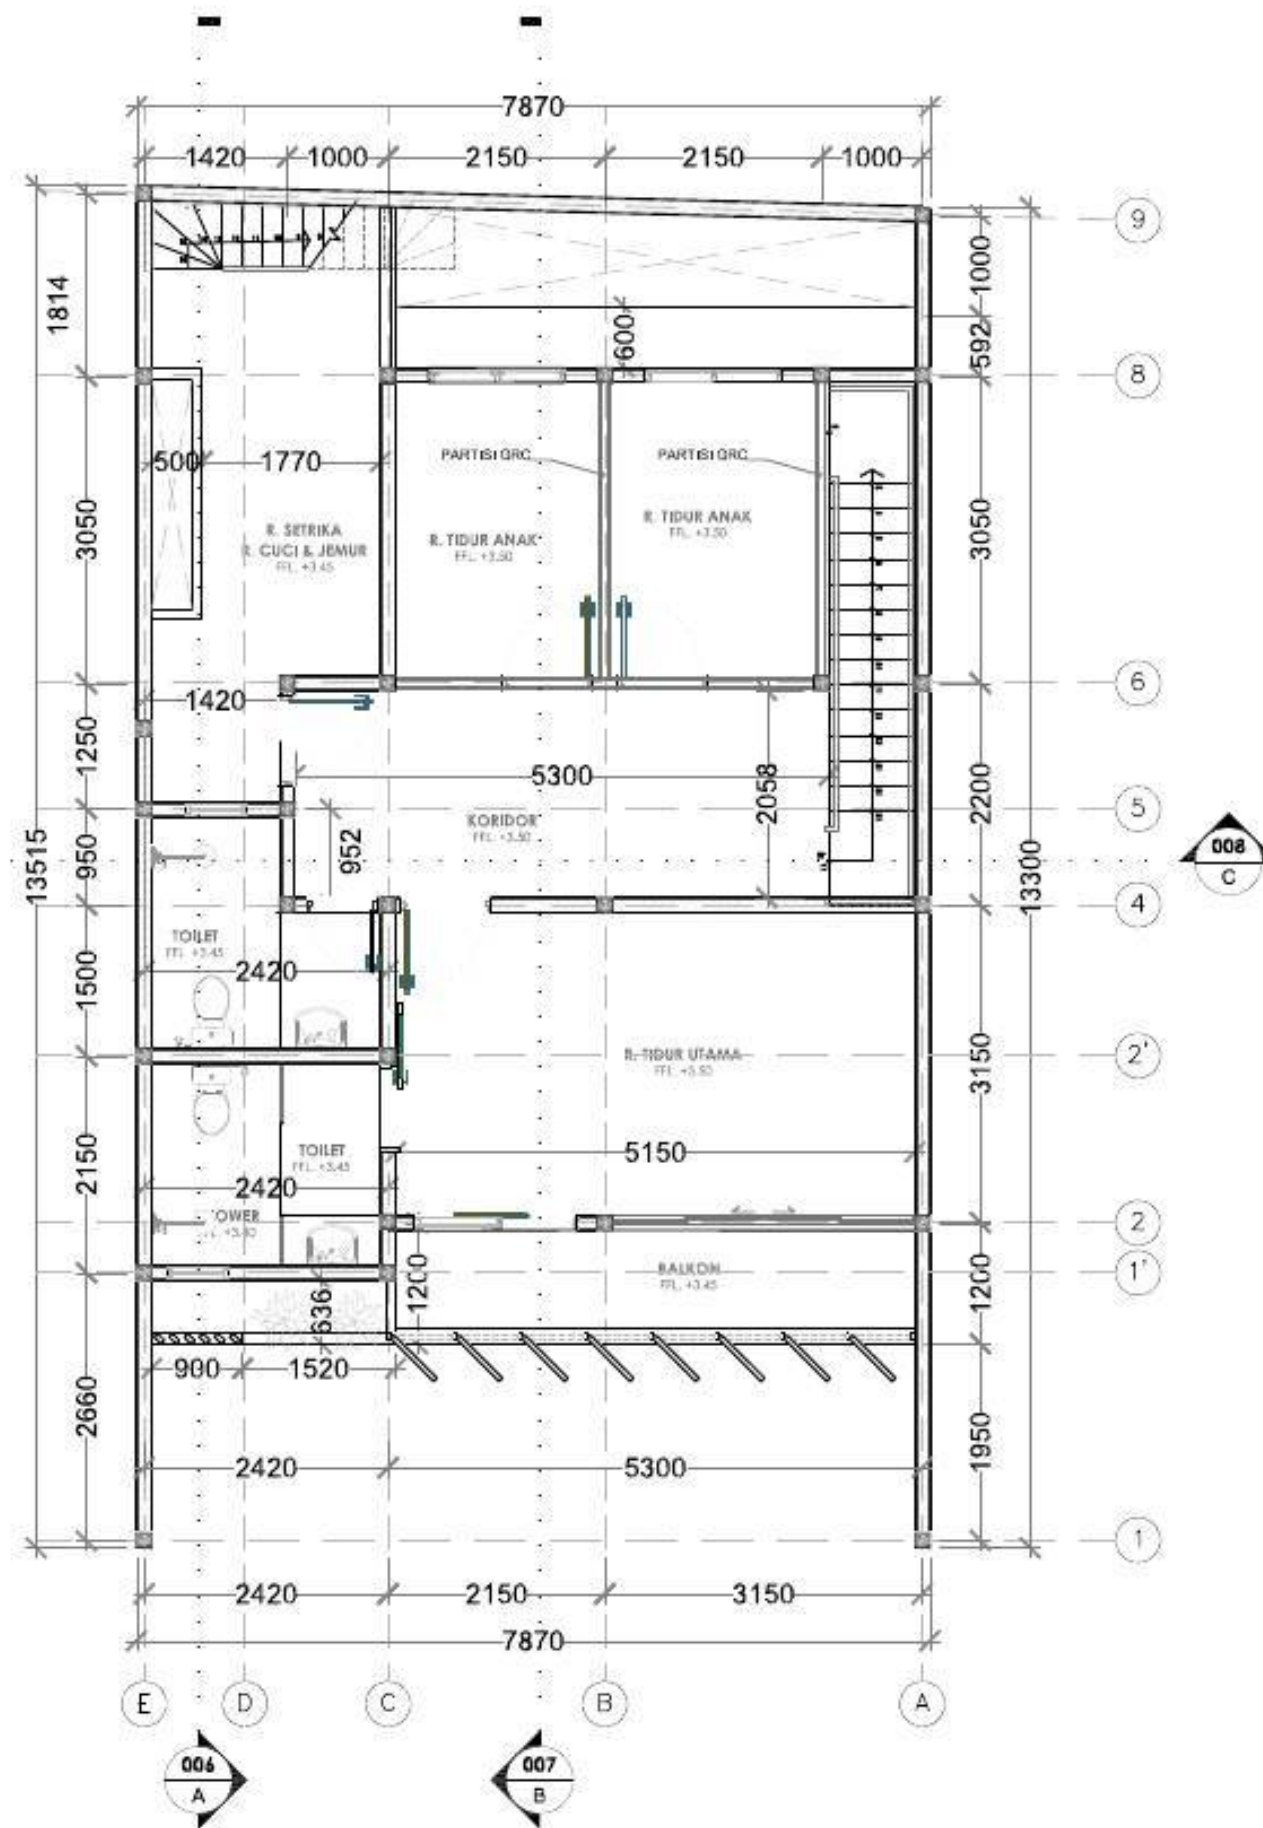

DENAH LANTAI ATAS


SKALA 1: 75

KONSULTAN	
KONTRAKTOR	
PROYEK	TOWN HOUSE JALAN JOE JAGAKARSA JAKARTA SELATAN
KETERANGAN	
REVISI	
ARSITEK	
DIBANGUN	
DIPERIKSA	
DIBETULI	
NO. PROYEK	
NAMA GAMBAR	DENAH KAVLING 1
SKALA	1 : 75
AR-004	
SUBKAT	NO. LEMBAR

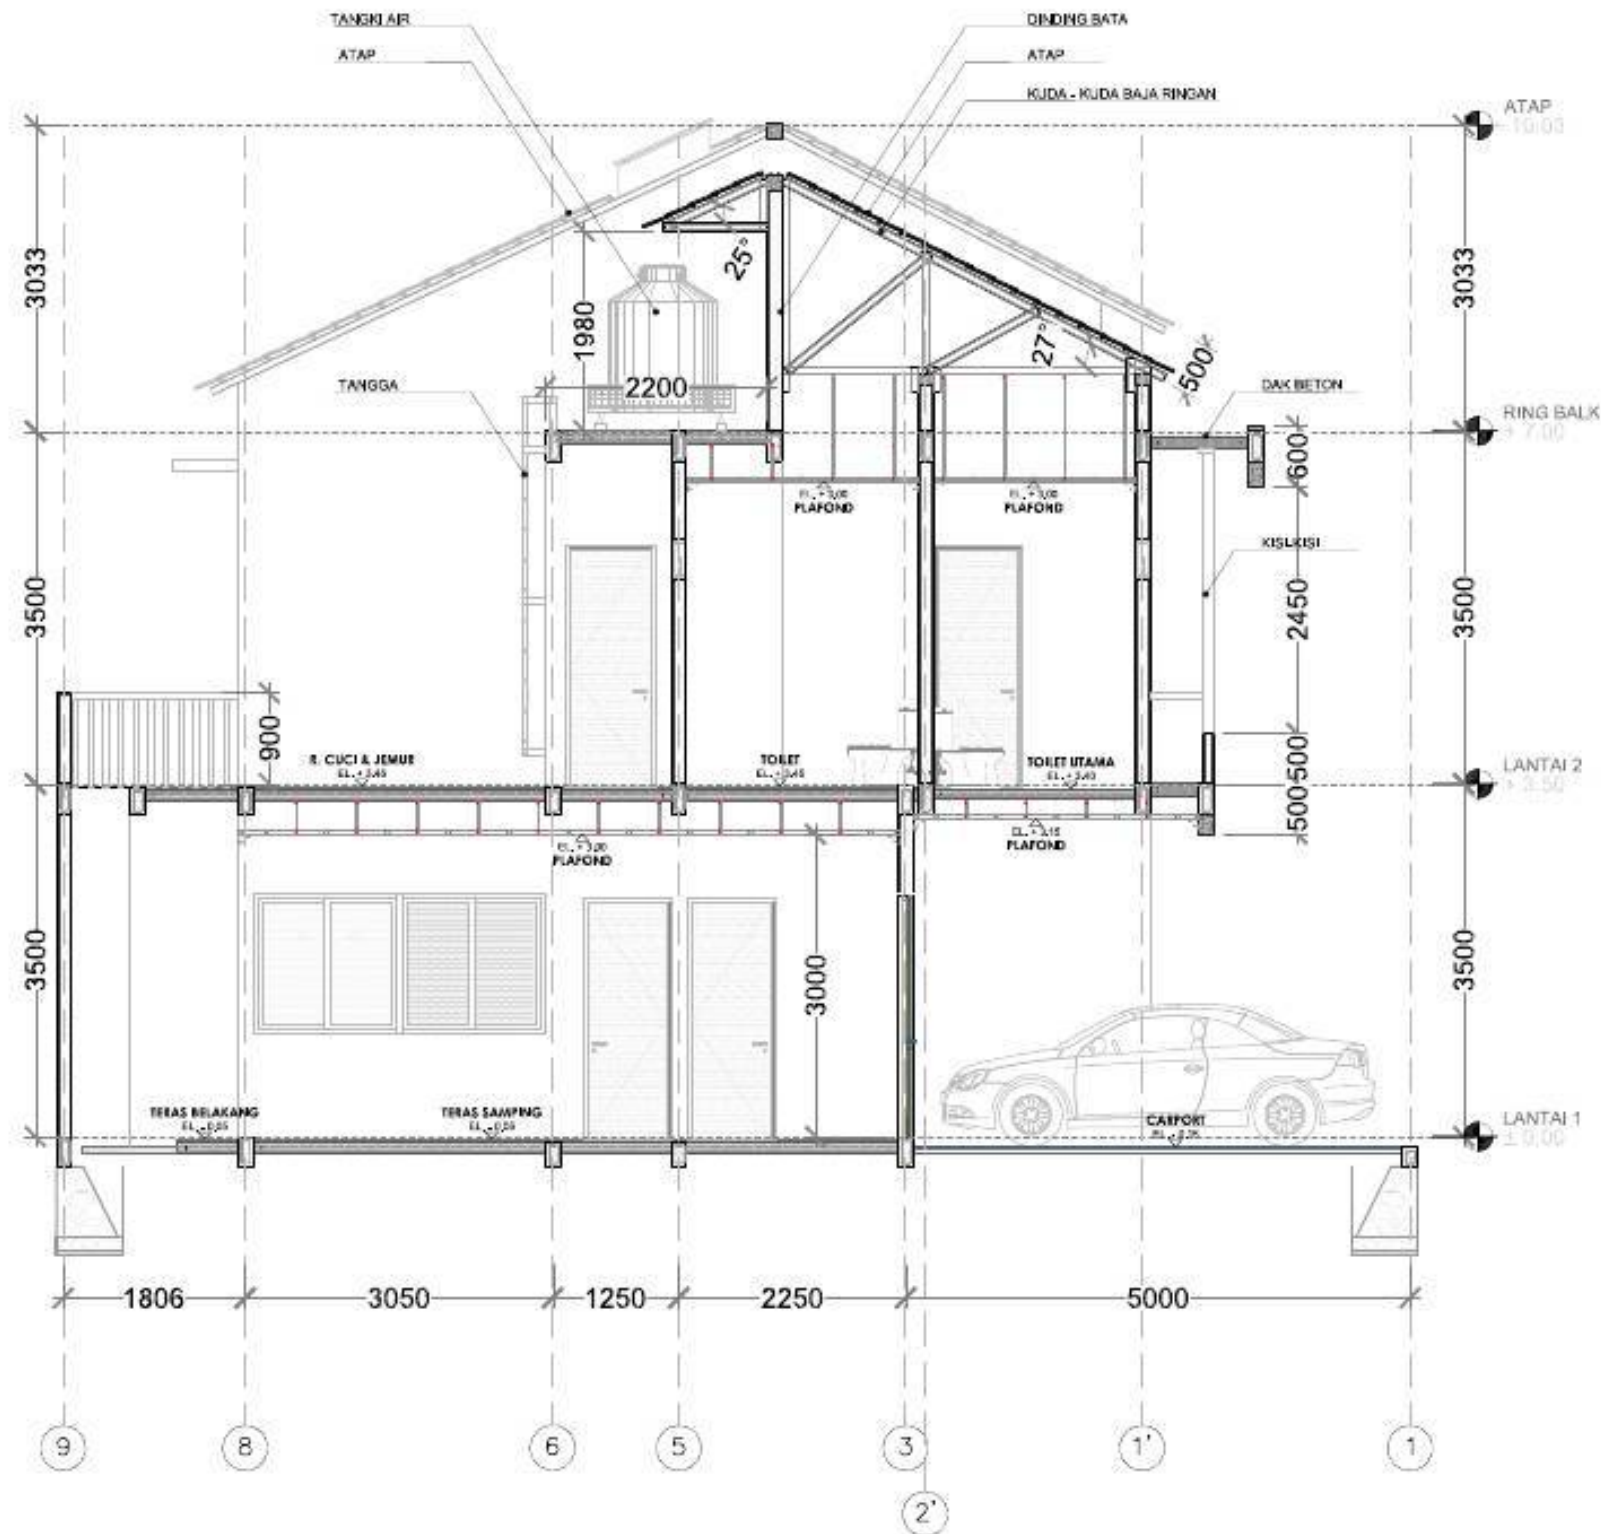


POTONGAN A - A
SKALA 1: 75

KONSULTAN	
KONTRAKTOR	
PROYEK	
TOWN HOUSE JALAN JOE JAGAKARSA JAKARTA SELATAN	
KETERANGAN	
REVISI	NO. DOK. DES. 1102
ARSITEK	
DIKAMBAR	
DIPERIKSA	
DIBETULI	
NO. PROYEK	
NAMA GAMBAR	
POTONGAN A - A KAVLING 1	
SKALA	1 : 75
AR-006	
SUBKAT	NO. LEMBAR

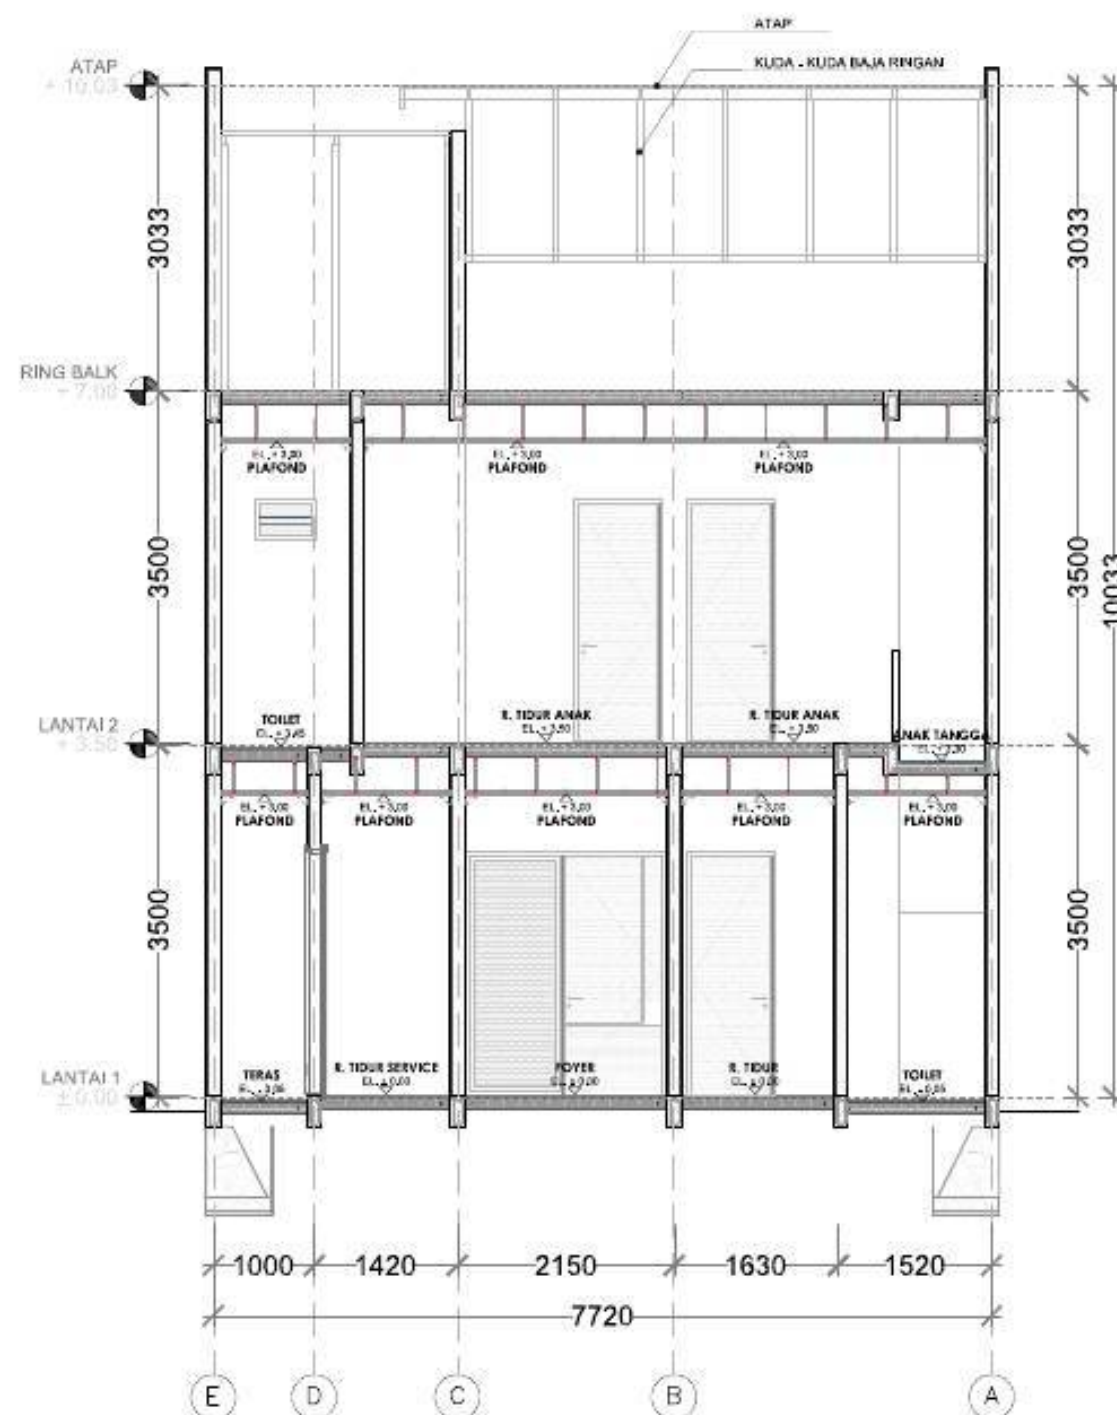


POTONGAN C - C
SKALA 1: 75

KONSULTAN			
KONTRAKTOR			
PROYEK			
TOWN HOUSE JALAN JOE JAGAKARSA JAKARTA SELATAN			
KETERANGAN			
REVISI			
		TGL	DR
ARSITEK			
DIBANGUN			
DIPERIKSA			
DIBETULI			
NO. PROYEK			
-			
NAMA GAMBAR			
POTONGAN C - C KAVLING 1			
SKALA			
1 : 75			
AR-008			
SUBKAT	NO. LEMBAR		

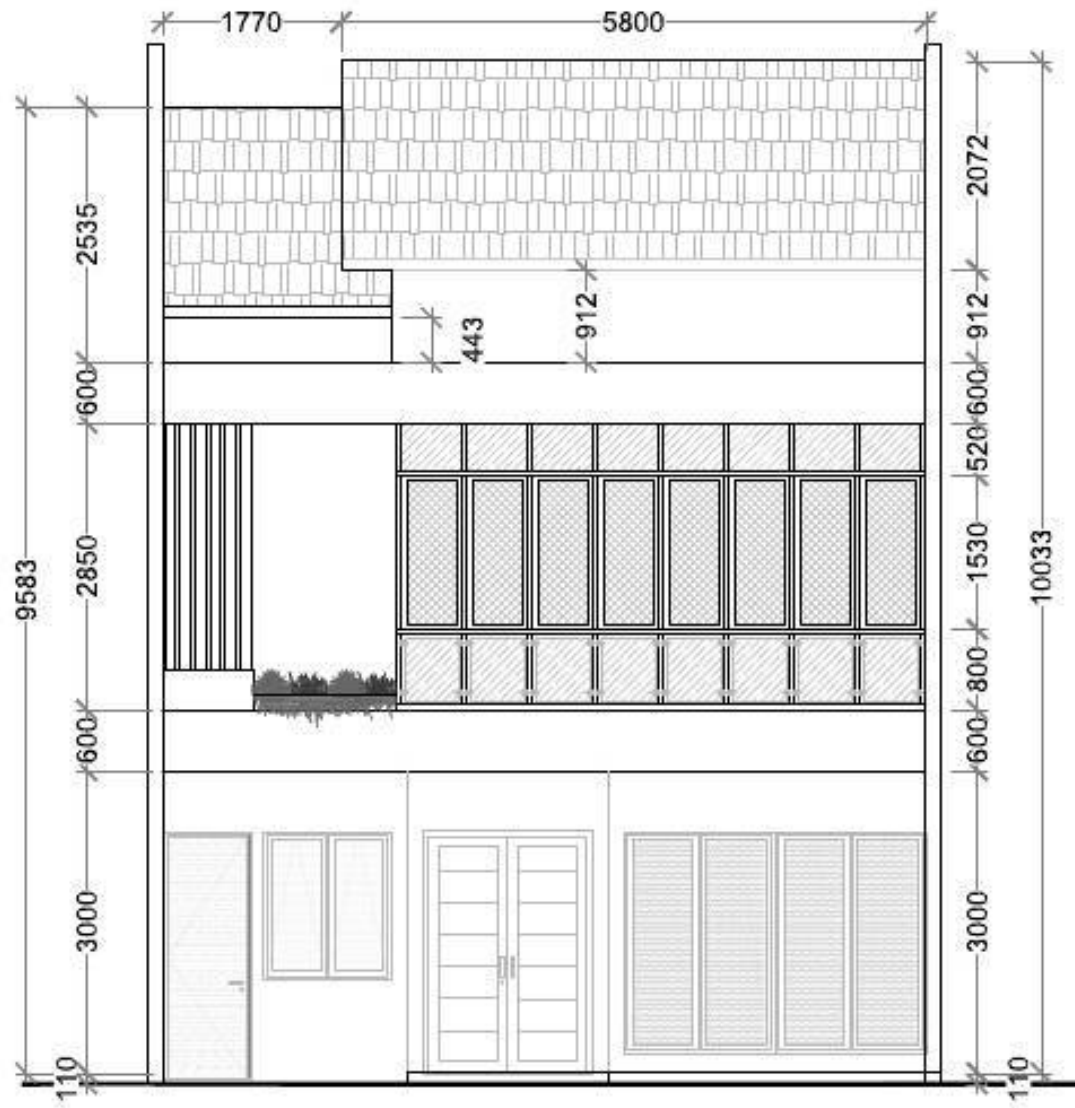

TAMPAK DEPAN


SKALA 1: 75

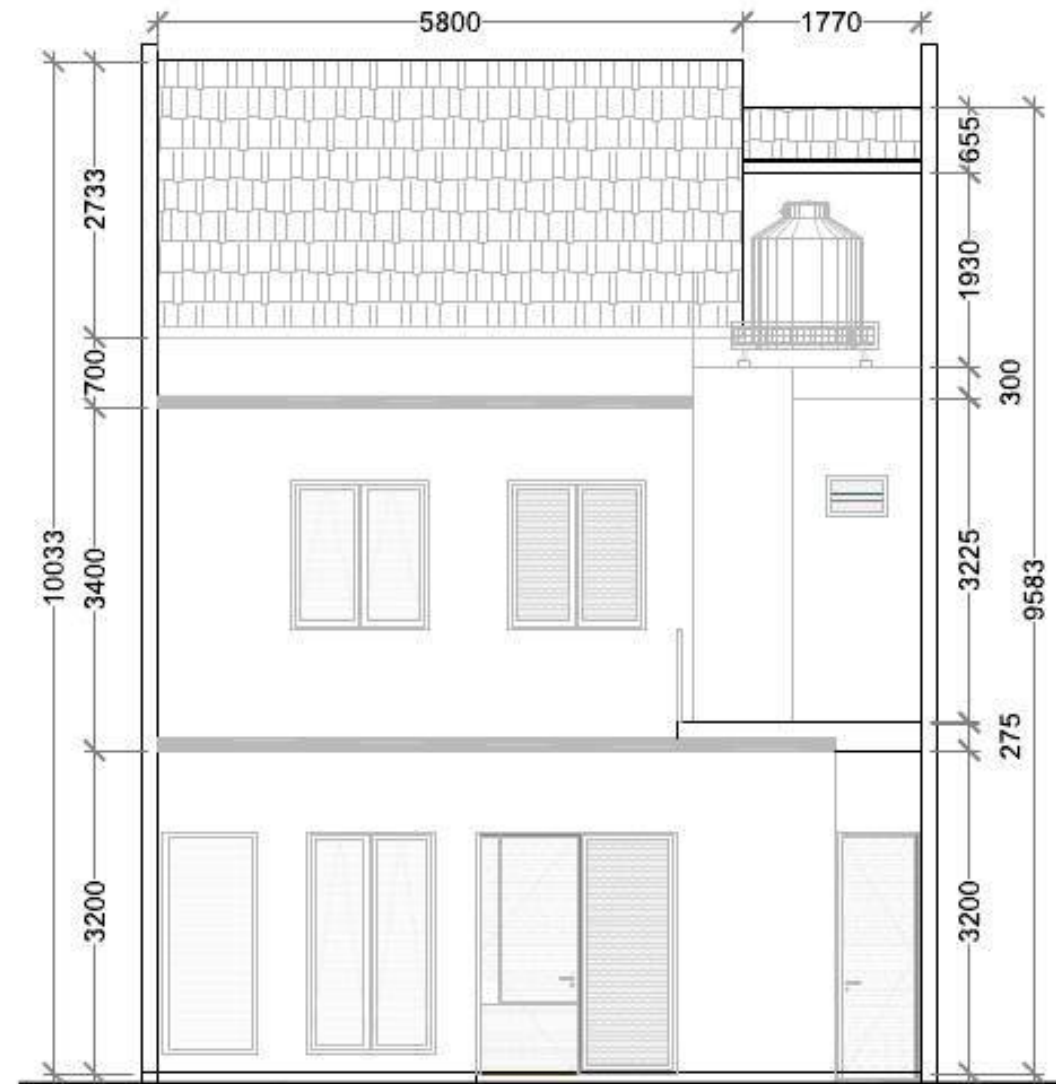

TAMPAK BELAKANG


SKALA 1: 75

KONSULTAN	
KONTRAKTOR	
PROYEK	
TOWN HOUSE JALAN JOE JAGAKARSA JAKARTA SELATAN	
KETERANGAN	
REVISI	NO. KRS
ARSITEK	
DIKAMBAR	
DIPERIKSA	
DIBETULI	
NO. PROYEK	
NAMA GAMBAR	
TAMPAK KAVLING 1	
SKALA 1 : 75	
AR-009	
SUBKAT	NO. LEMBAR

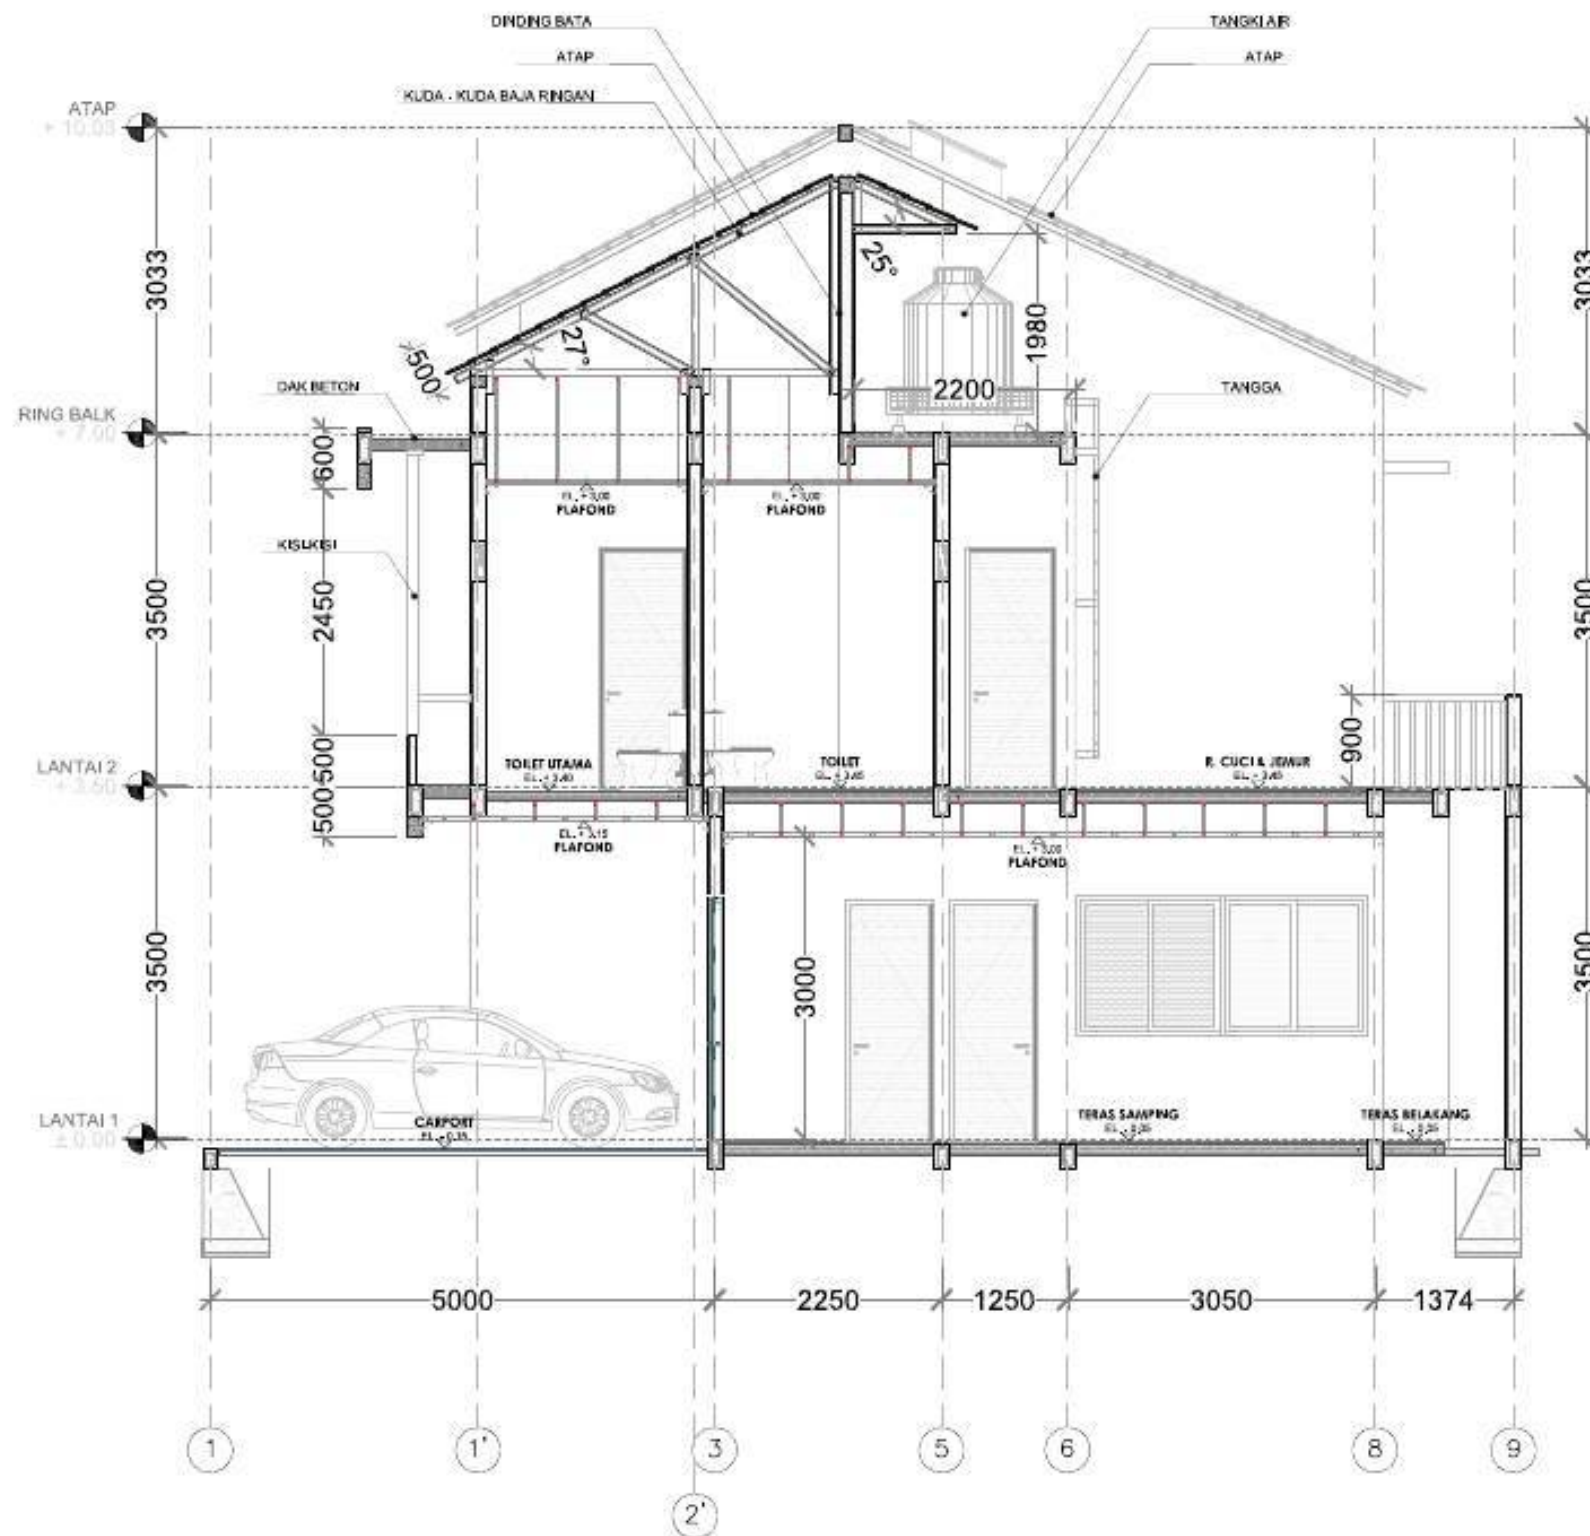


POTONGAN A - A
SKALA 1: 75

KONSULTAN	
KONTRAKTOR	
PROYEK	
TOWN HOUSE JALAN JOE JAGAKARSA JAKARTA SELATAN	
KETERANGAN	
REVISI	NO. DOK. DES. 1102
ARSITEK	
DIKAMBAR	
DIPERIKSA	
DIBETULI	
NO. PROYEK	
-	
NAMA GAMBAR	
POTONGAN A - A KAVLING 2	
SKALA	
1 : 75	
AR-012	
SUBKAT	NO. LEMBAR

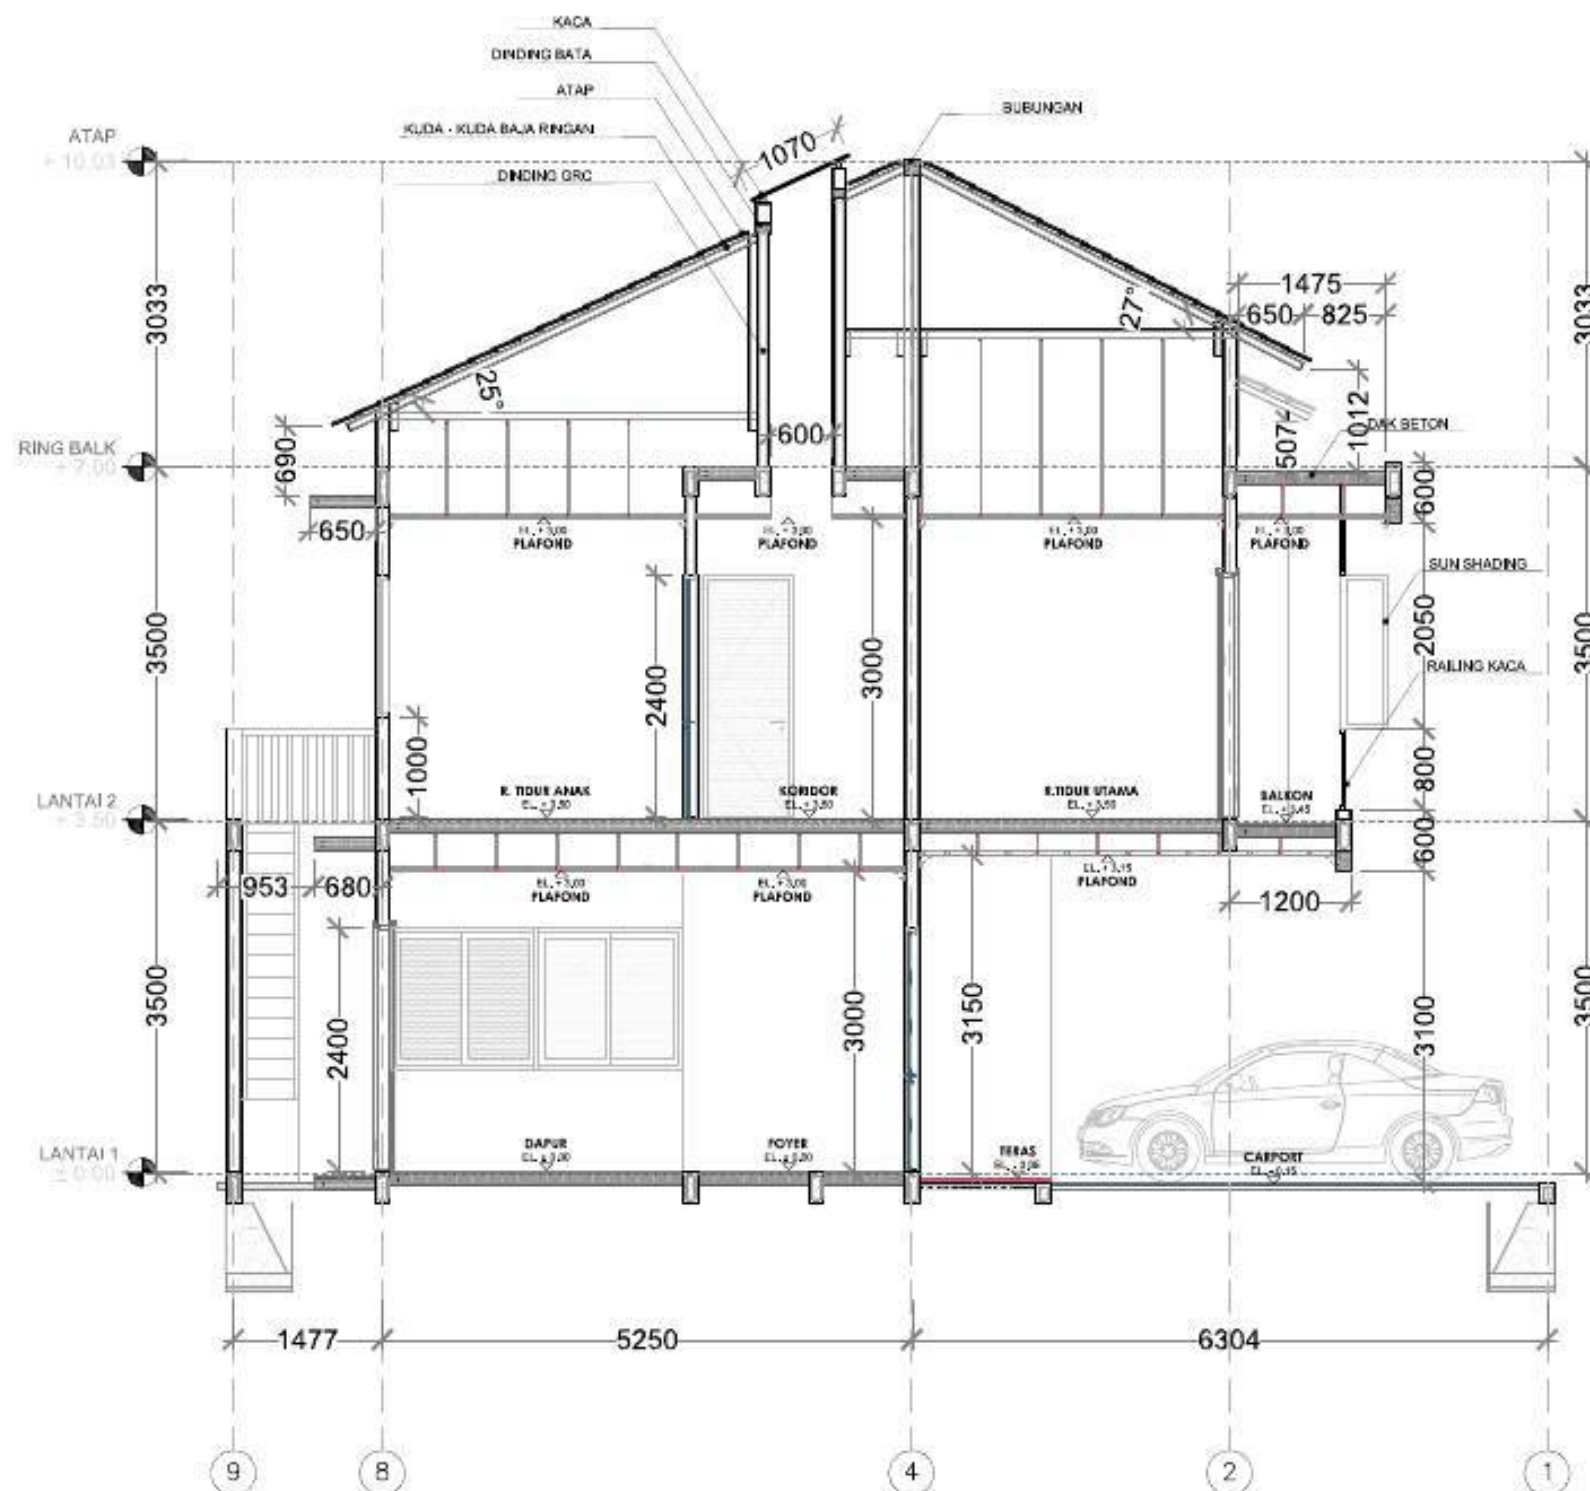


POTONGAN B - B
SKALA 1: 75

KONSULTAN	
KONTRAKTOR	
PROYEK	
TOWN HOUSE JALAN JOE JAGAKARSA JAKARTA SELATAN	
KETERANGAN	
REVISI	NO. DOK. DES. 1102
ARSITEK	
DIKAMBAR	
DIPERIKSA	
DIBETULU	
NO. PROYEK	
NAMA GAMBAR	
POTONGAN B - B KAVLING 2	
SKALA	1 : 75
AR-013	
SUBKAT	NO. LEMBAR

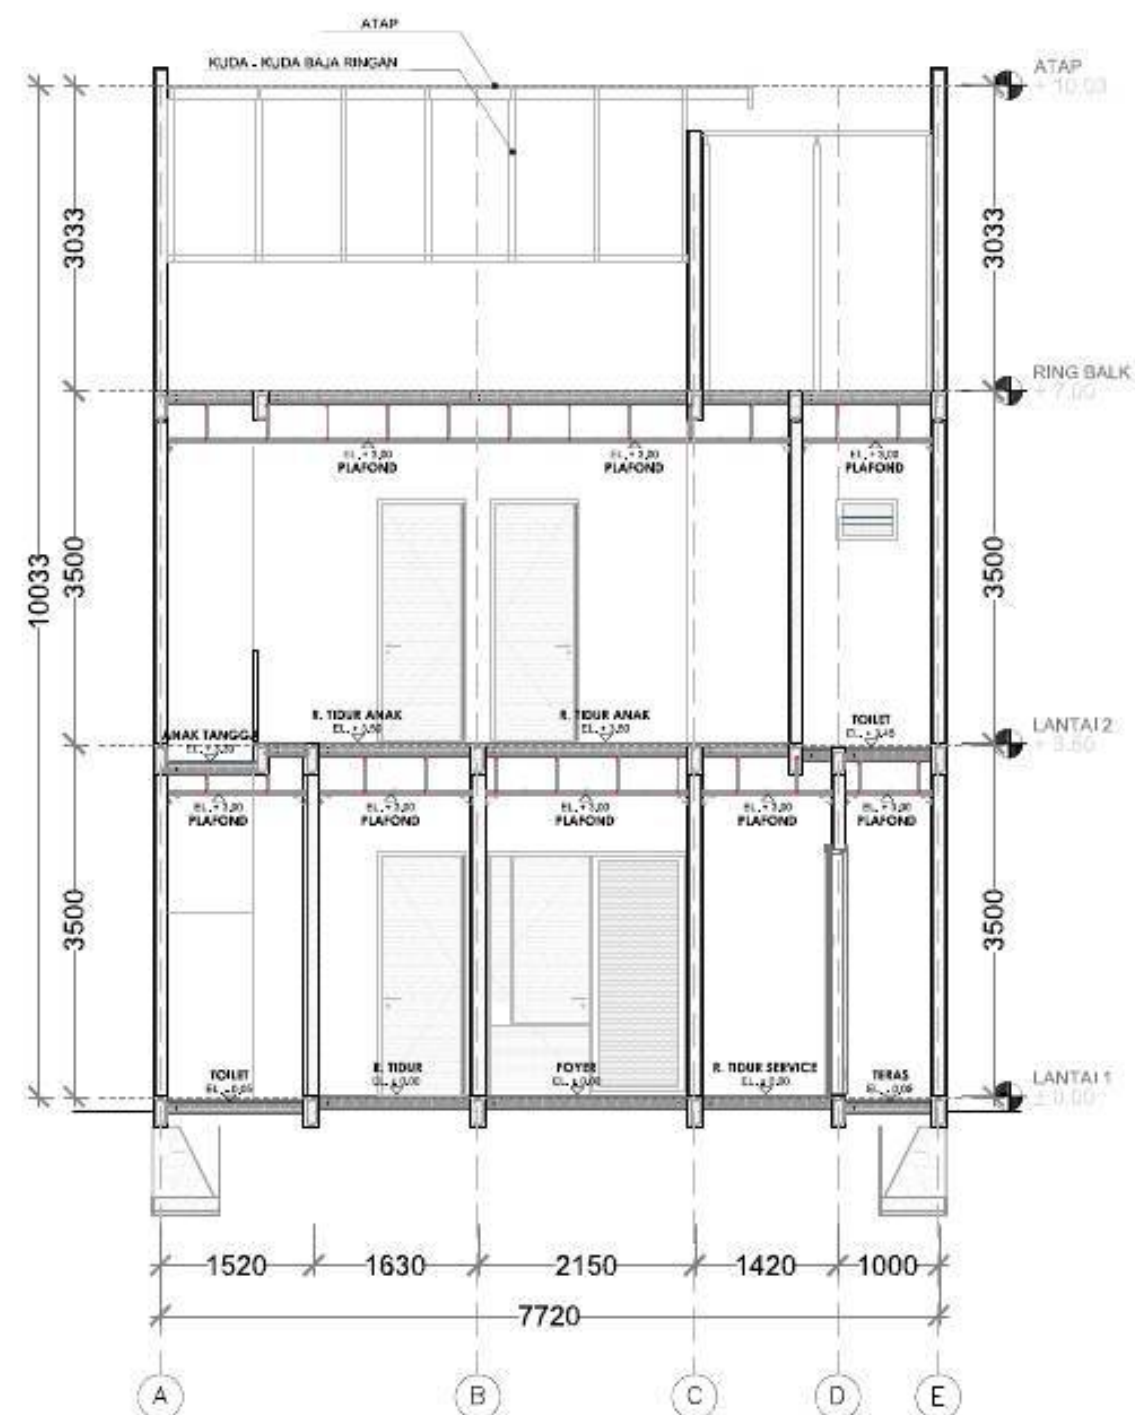


POTONGAN C - C
SKALA 1: 75

KONSULTAN				
KONTRAKTOR				
PROYEK				
TOWN HOUSE JALAN JOE JAGAKARSA JAKARTA SELATAN				
KETERANGAN				
REVISI				
		TGL	DIK	TRD
ARSITEK				
DOKUMENTASIR				
DIPERIKSA				
DIBETULI				
NO. PROYEK				
NAMA GAMBAR				
POTONGAN C - C KAVLING 2				
SKALA				
1 : 75				
AR-014				
SUBKAT		NO. LEMBAR		

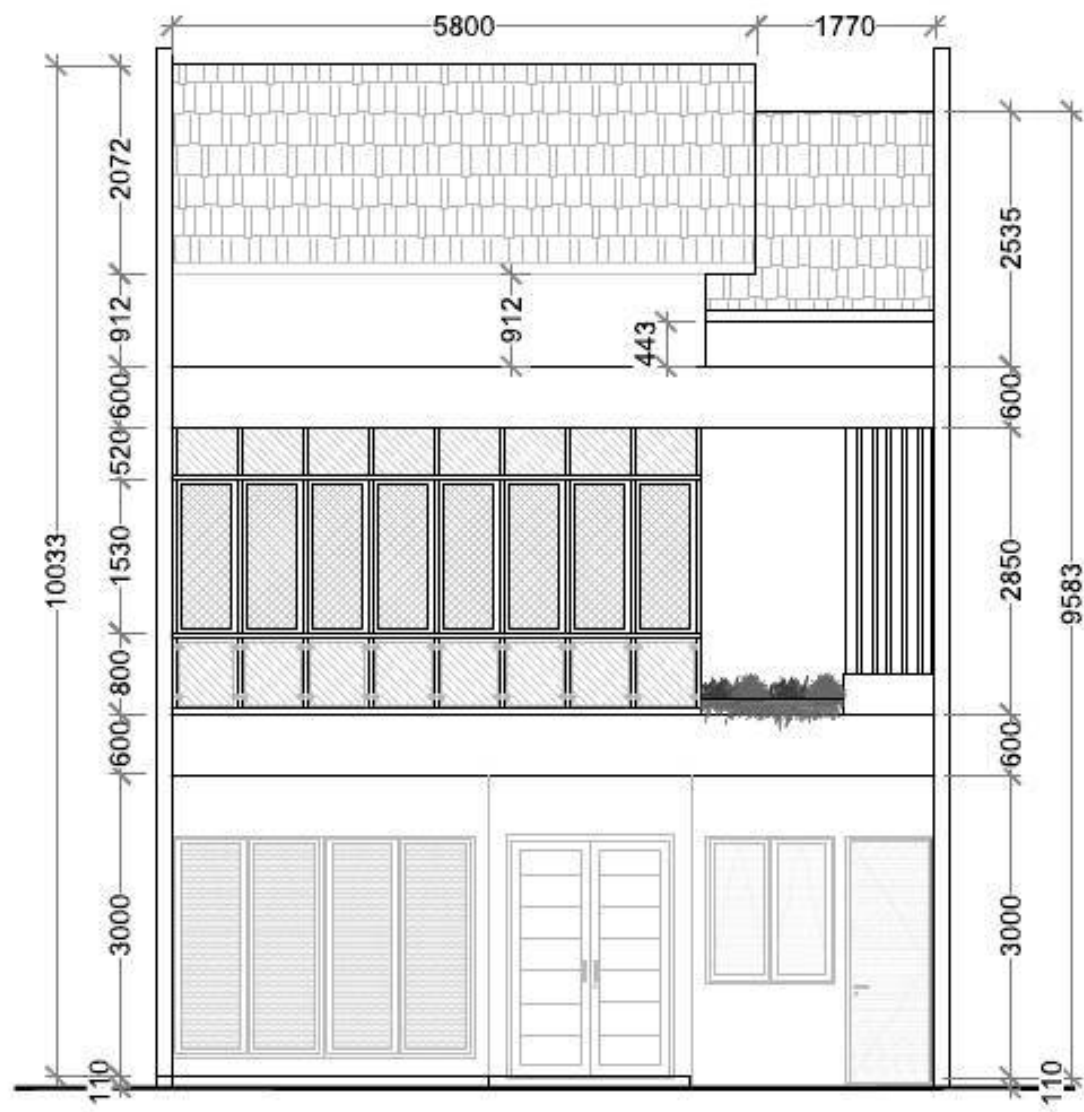

TAMPAK DEPAN

SKALA 1: 75

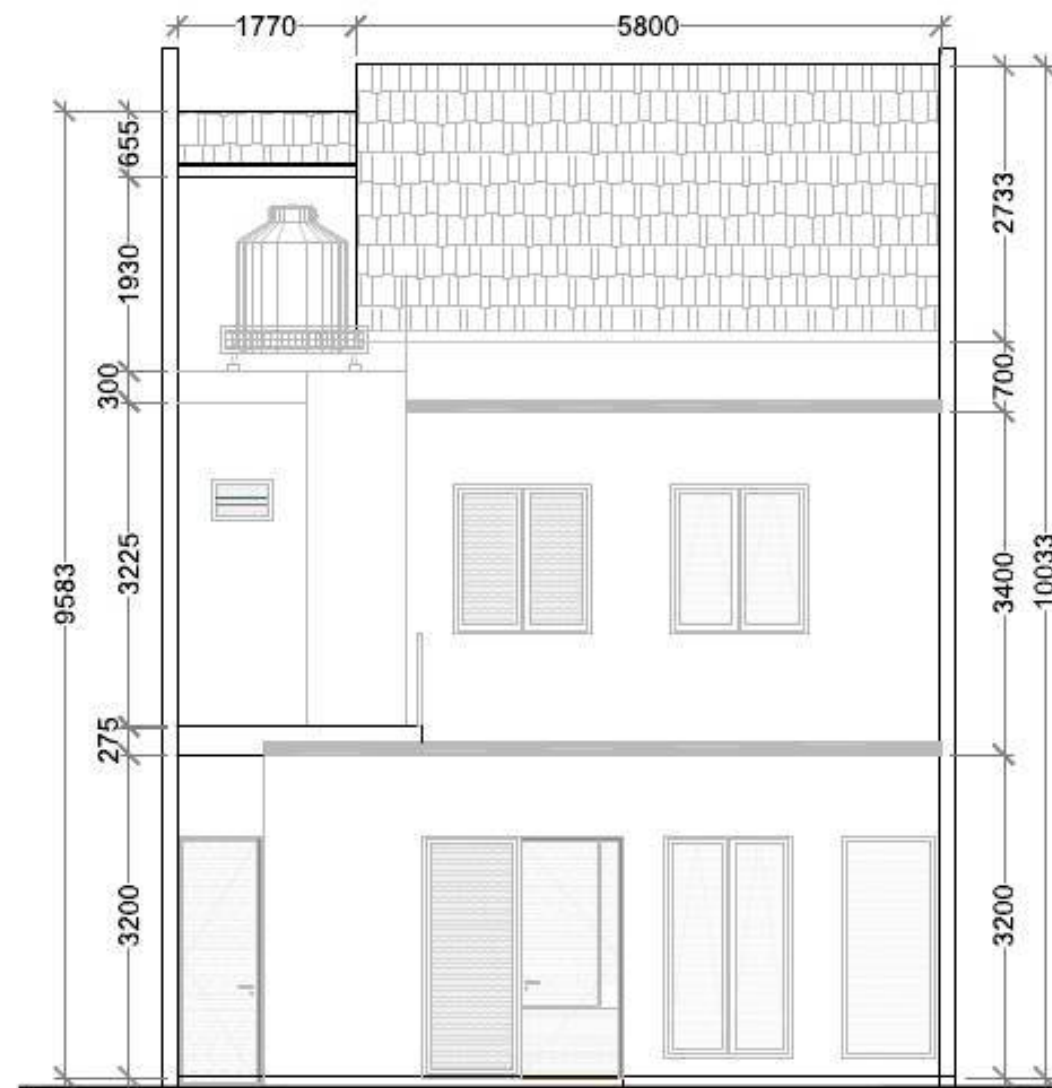


TAMPAK BELAKANG

SKALA 1: 75

KONSULTAN	
KONTRAKTOR	
PROYEK	
TOWN HOUSE JALAN JOE JAGAKARSA JAKARTA SELATAN	
KETERANGAN	
REVISI	NO. DOK. DES. TITIK
ARSITEK	
DIKAMBAR	
DIPERIKSA	
DIBETULUJ	
NO. PROYEK	
NAMA GAMBAR	
TAMPAK KAVLING 2	
SKALA 1 : 75	
AR-015	
SUBKAT	NO. LEMBAR




NO. LEMBAR

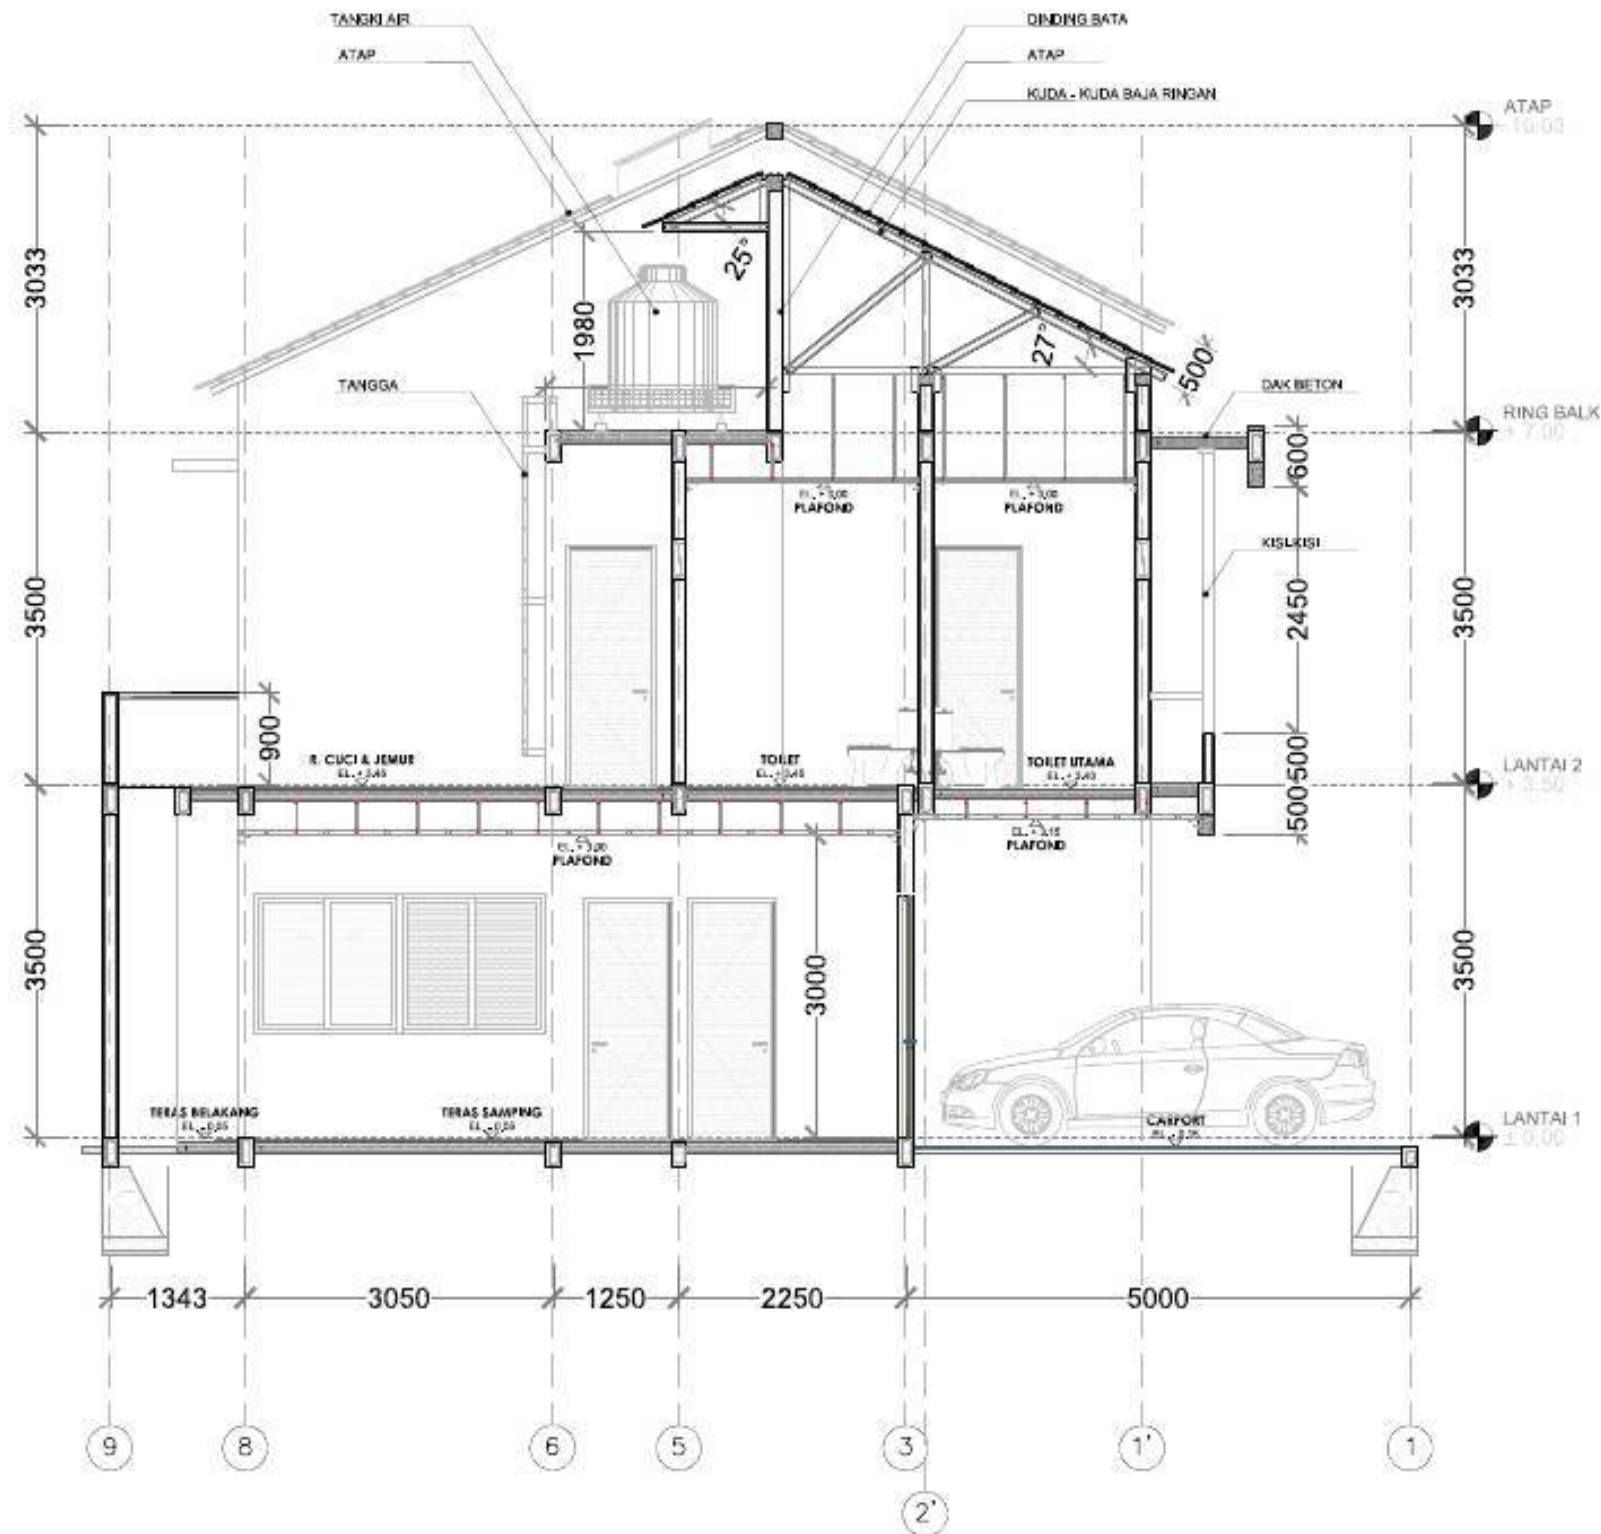

POTONGAN A - A
SKALA 1: 75

KONSULTAN	
KONTRAKTOR	
PROYEK	
TOWN HOUSE JALAN JOE JAGAKARSA JAKARTA SELATAN	
KETERANGAN	
REVISI	
NO. PROYEK	
NAMA GAMBAR	
POTONGAN A - A KAVLING 3	
SKALA	
1 : 75	
AR-018	
SUBKAT	NO. LEMBAR

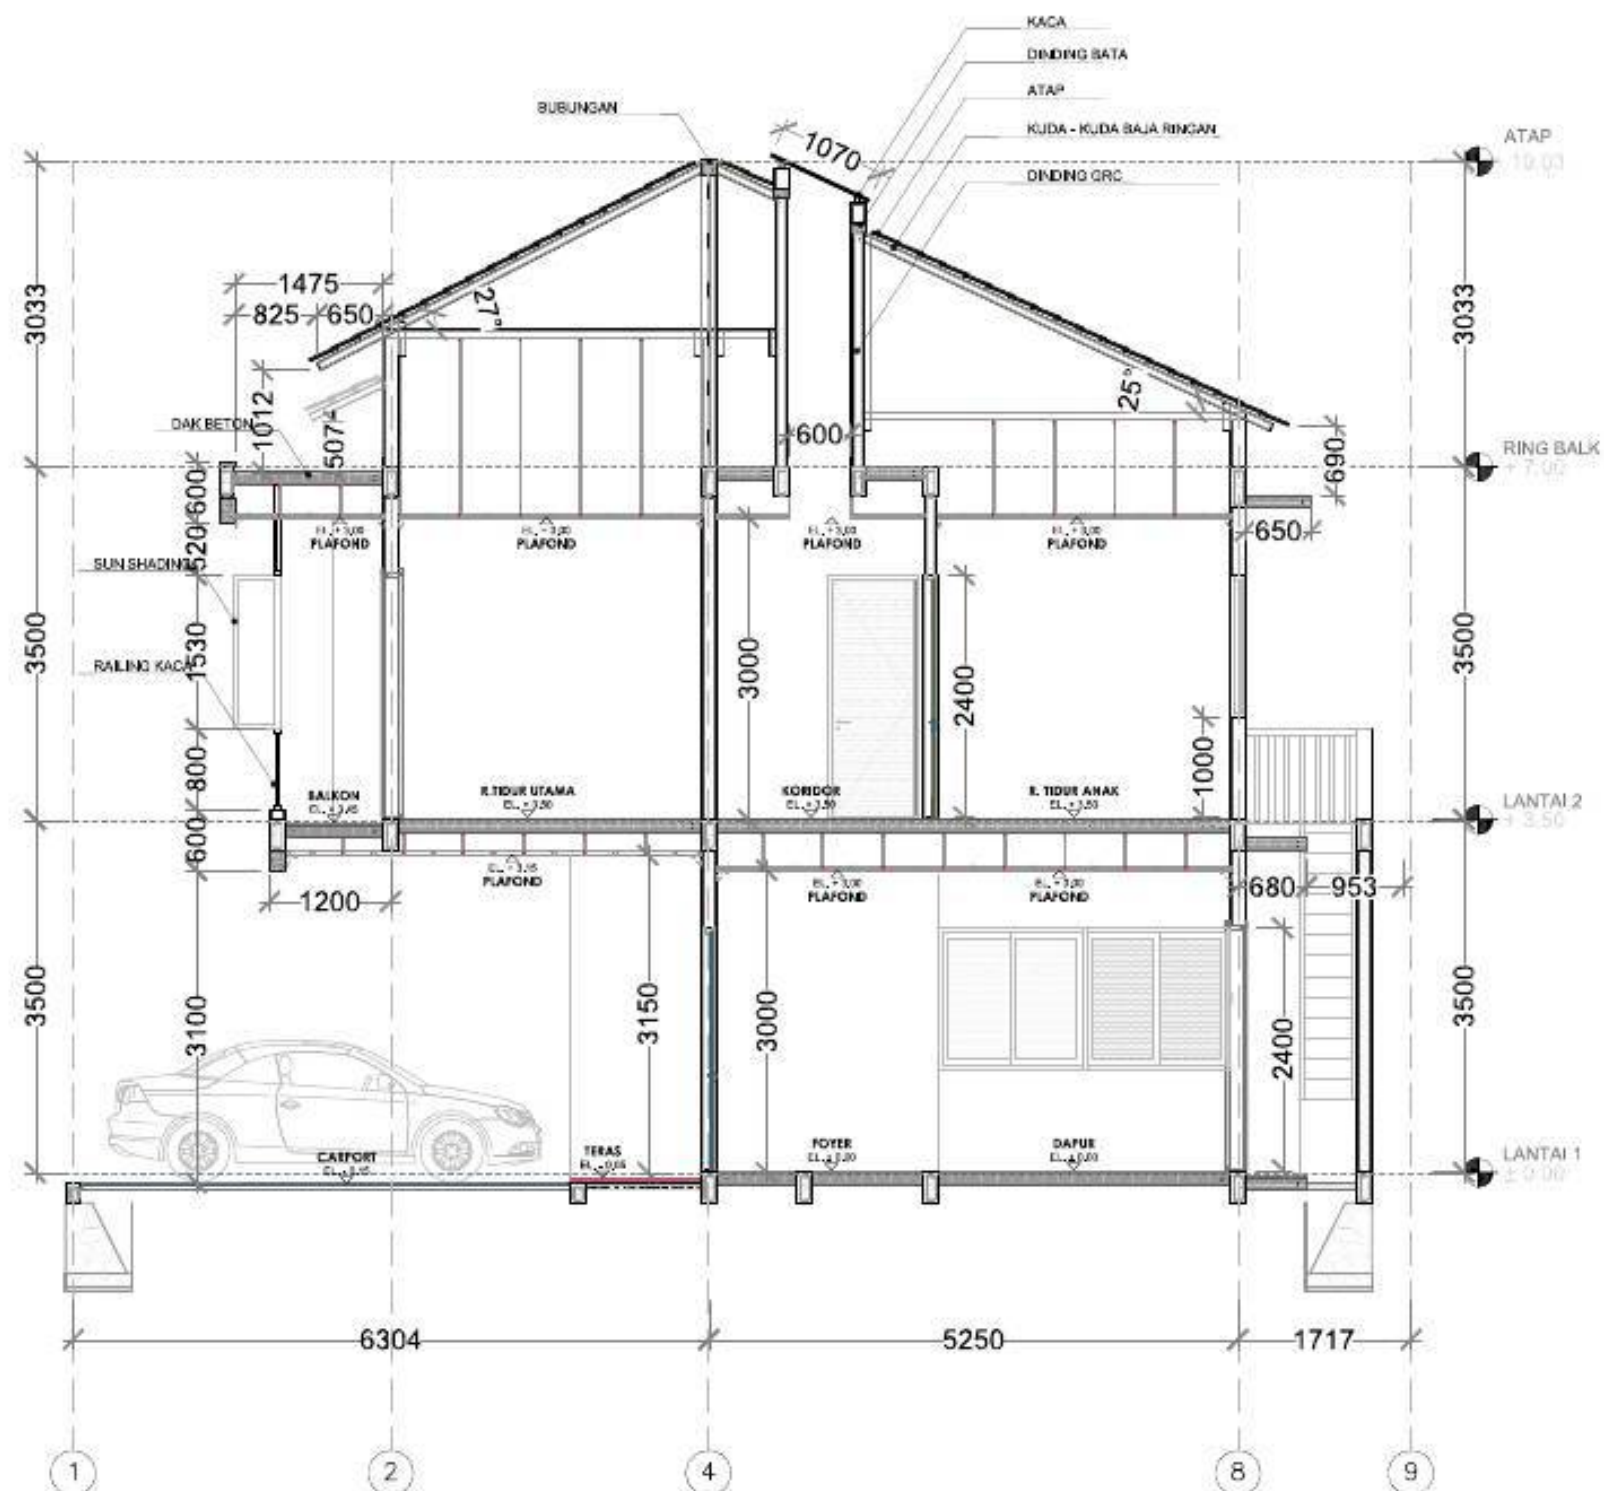


POTONGAN B - B
SKALA 1: 75


KONSULTAN			
KONTRAKTOR			
PROYEK			
TOWN HOUSE JALAN JOE JAGAKARSA JAKARTA SELATAN			
KETERANGAN			
REVISI			
		NO.	REVISI
ARSITEK			
DIBANGUN			
DIPERIKSA			
DIBETULKAN			
NO. PROYEK			
NAMA GAMBAR			
POTONGAN B - B KAVLING 3			
SKALA		1 : 75	
AR-019			
SUBKAT	NO. LEMBAR		



NO. LEMBAR

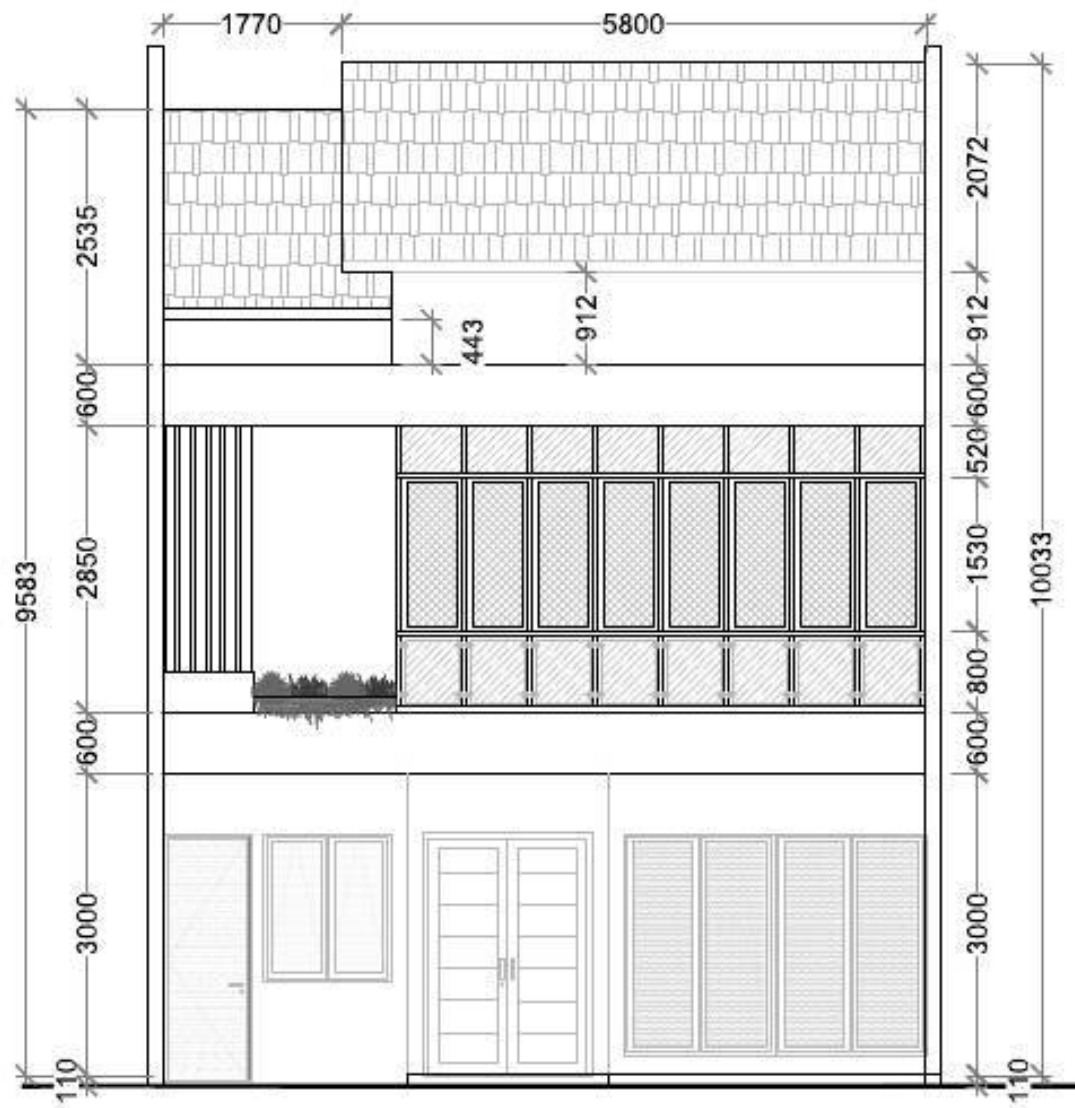


TAMPAK DEPAN
SKALA 1: 75

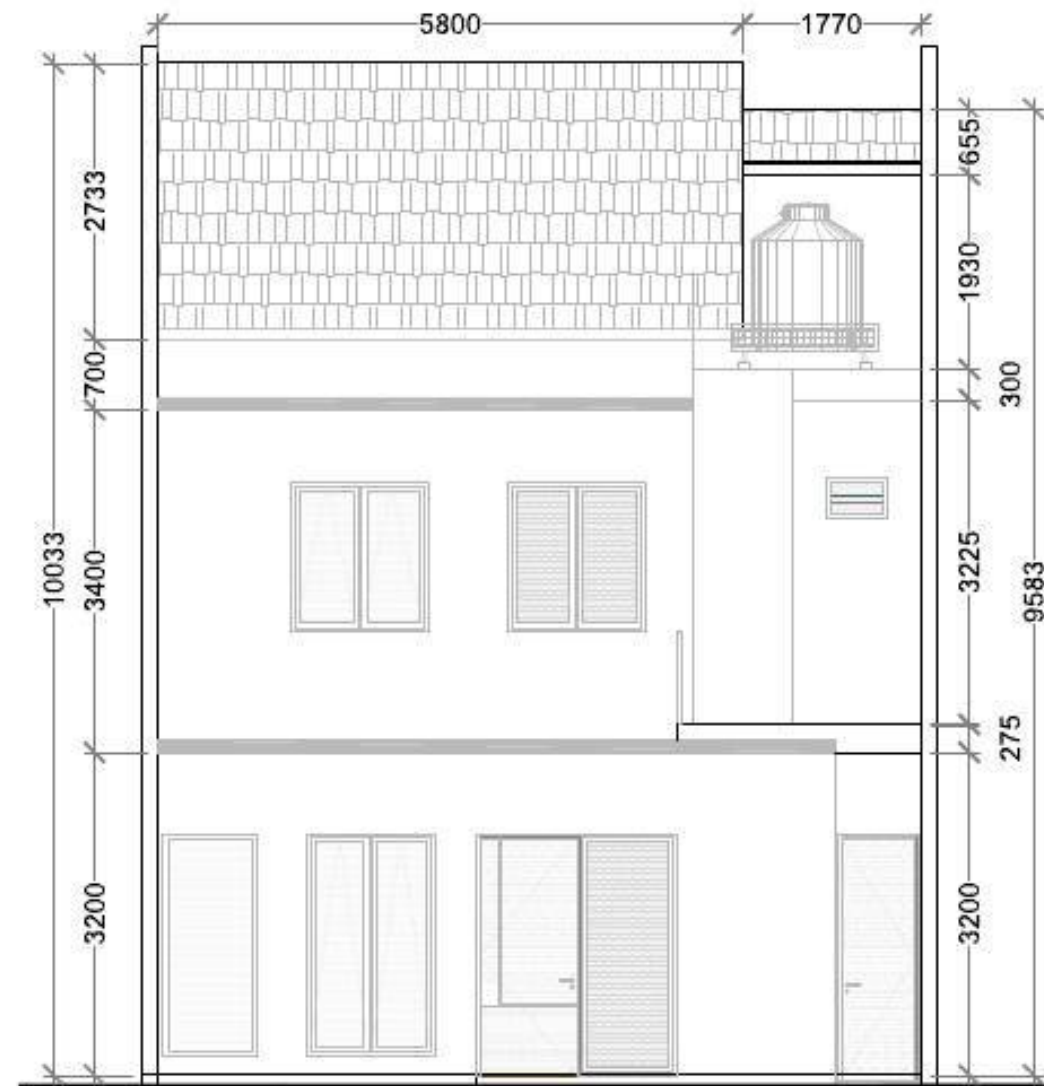


TAMPAK BELAKANG
SKALA 1: 75

KONSULTAN	
KONTRAKTOR	
PROYEK	
TOWN HOUSE JALAN JOE JAGAKARSA JAKARTA SELATAN	
KETERANGAN	
REVISI	NO. KRS
ARSITEK	
DIKAMBAR	
DIPERIKSA	
DIBETULUJ	
NO. PROYEK	
NAMA GAMBAR	
TAMPAK KAVLING 3	
SKALA	1 : 75
AR-021	
SUBKAT	NO. LEMBAR

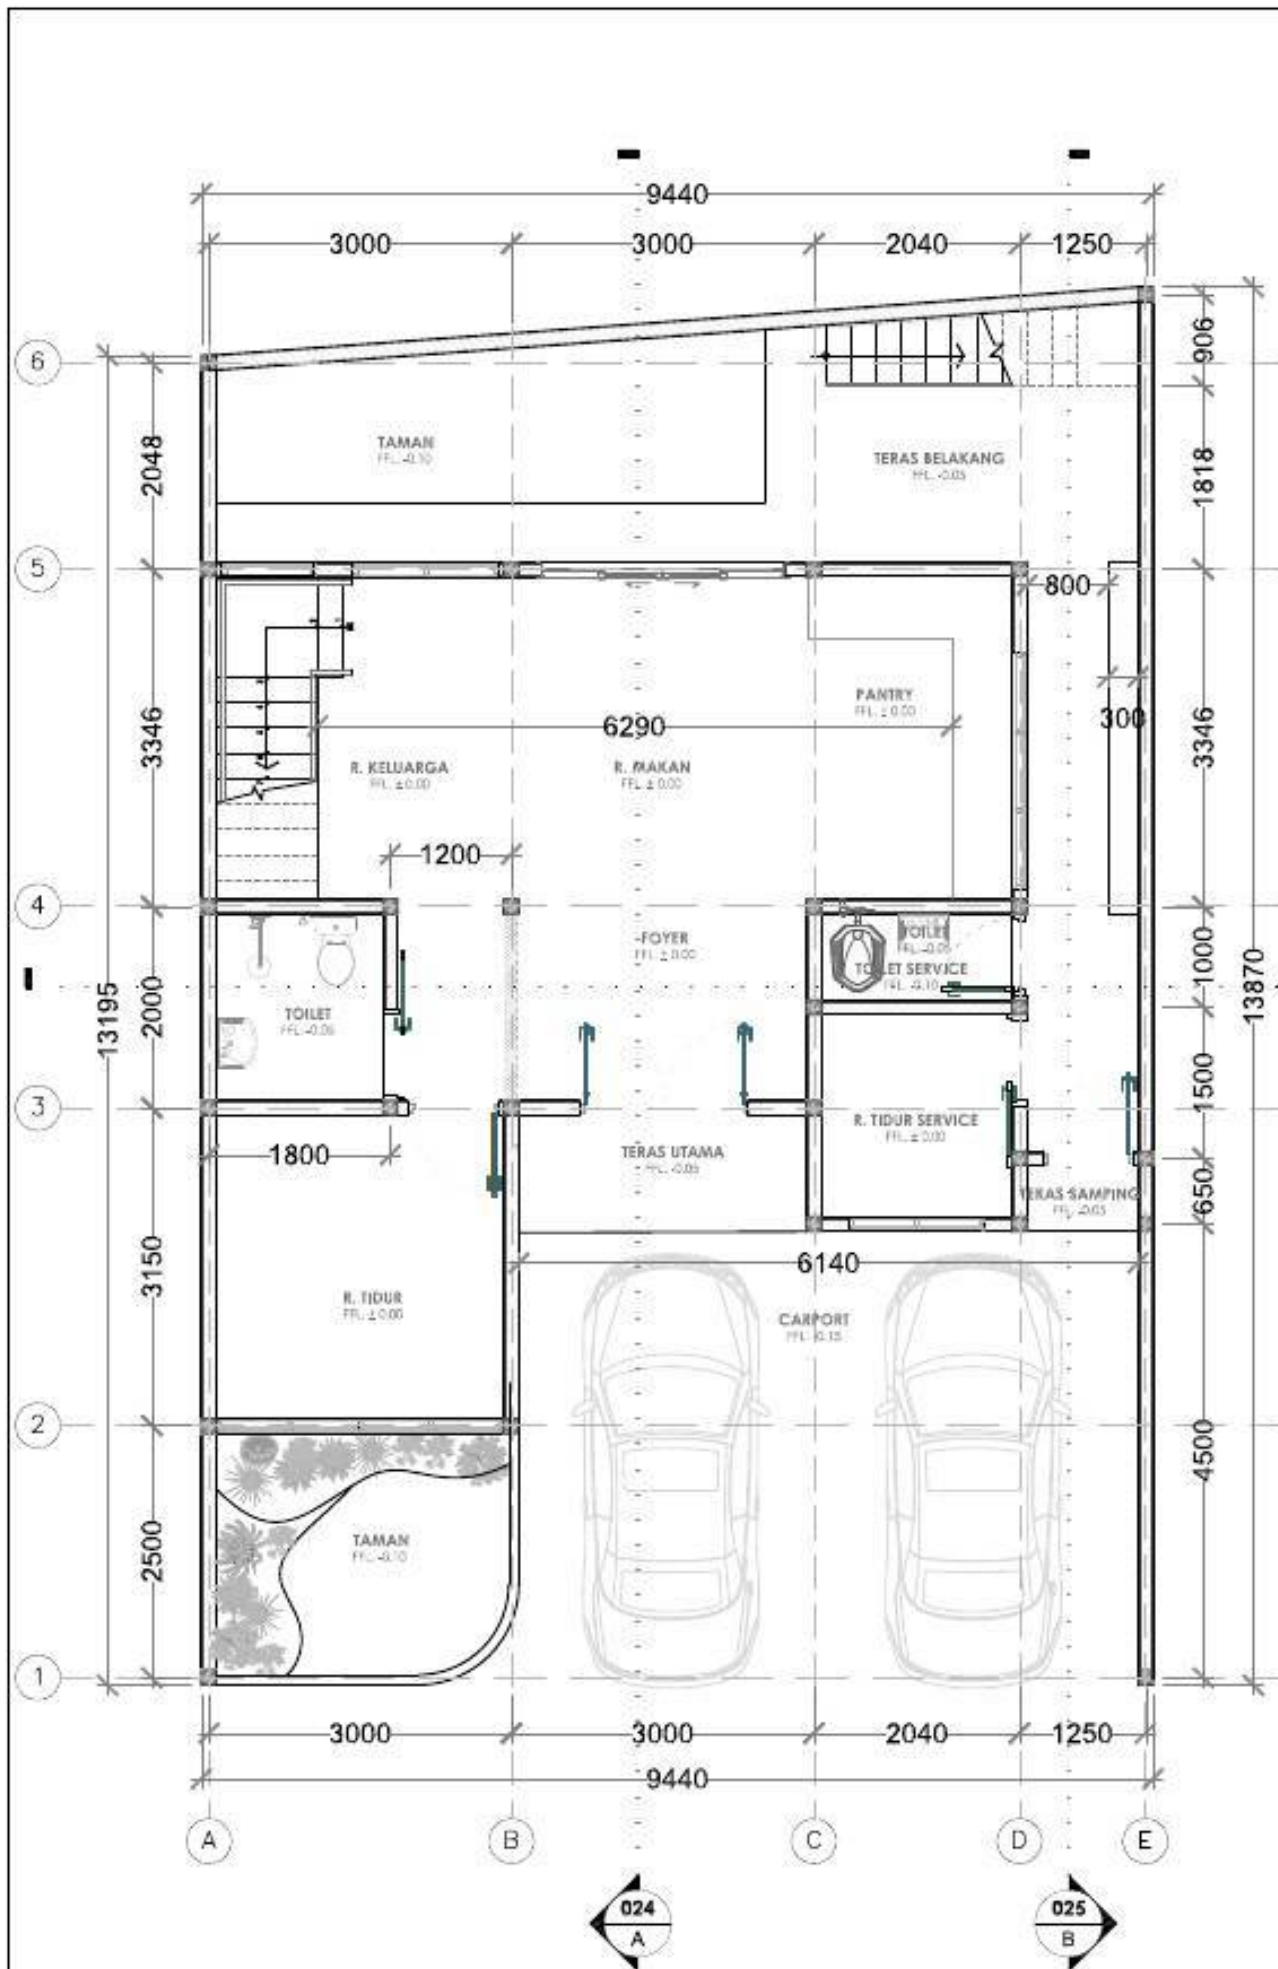


DENAH LANTAI DASAR
SKALA 1: 75

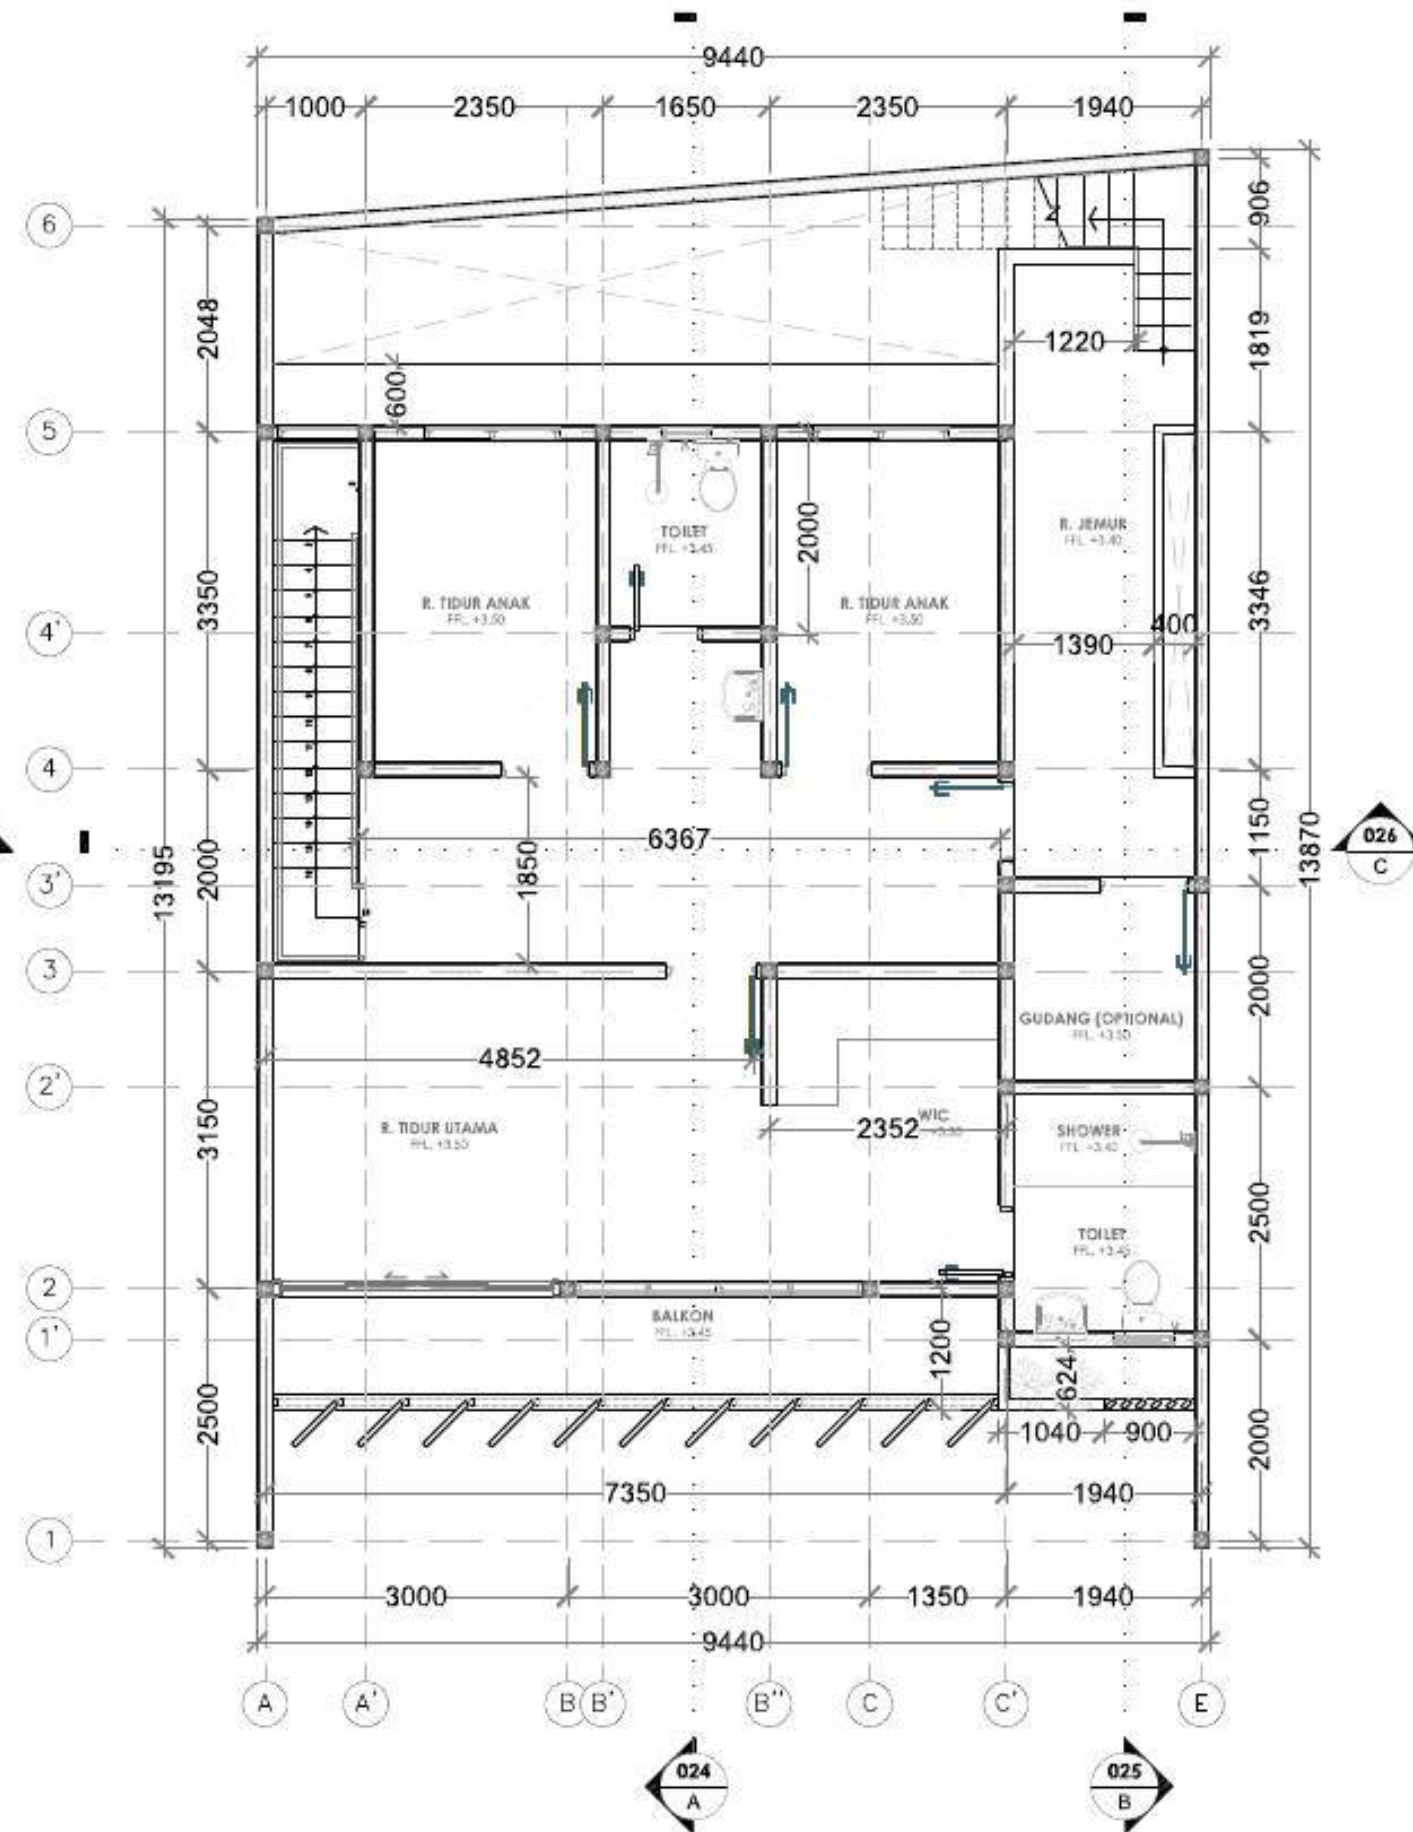


DENAH LANTAI ATAS
SKALA 1: 75

KONSULTAN	
KONTRAKTOR	
PROYEK	TOWN HOUSE JALAN JOE JAGAKARSA JAKARTA SELATAN
KETERANGAN	
REVISI	
ARSITEK	
DOKUMEN	
DIPERIKSA	
DIBETULI	
NO. PROYEK	
NAMA GAMBAR	DENAH KAVLING 4
SKALA	1 : 75
SUBKAT	AR-022
NO. LEMBAR	

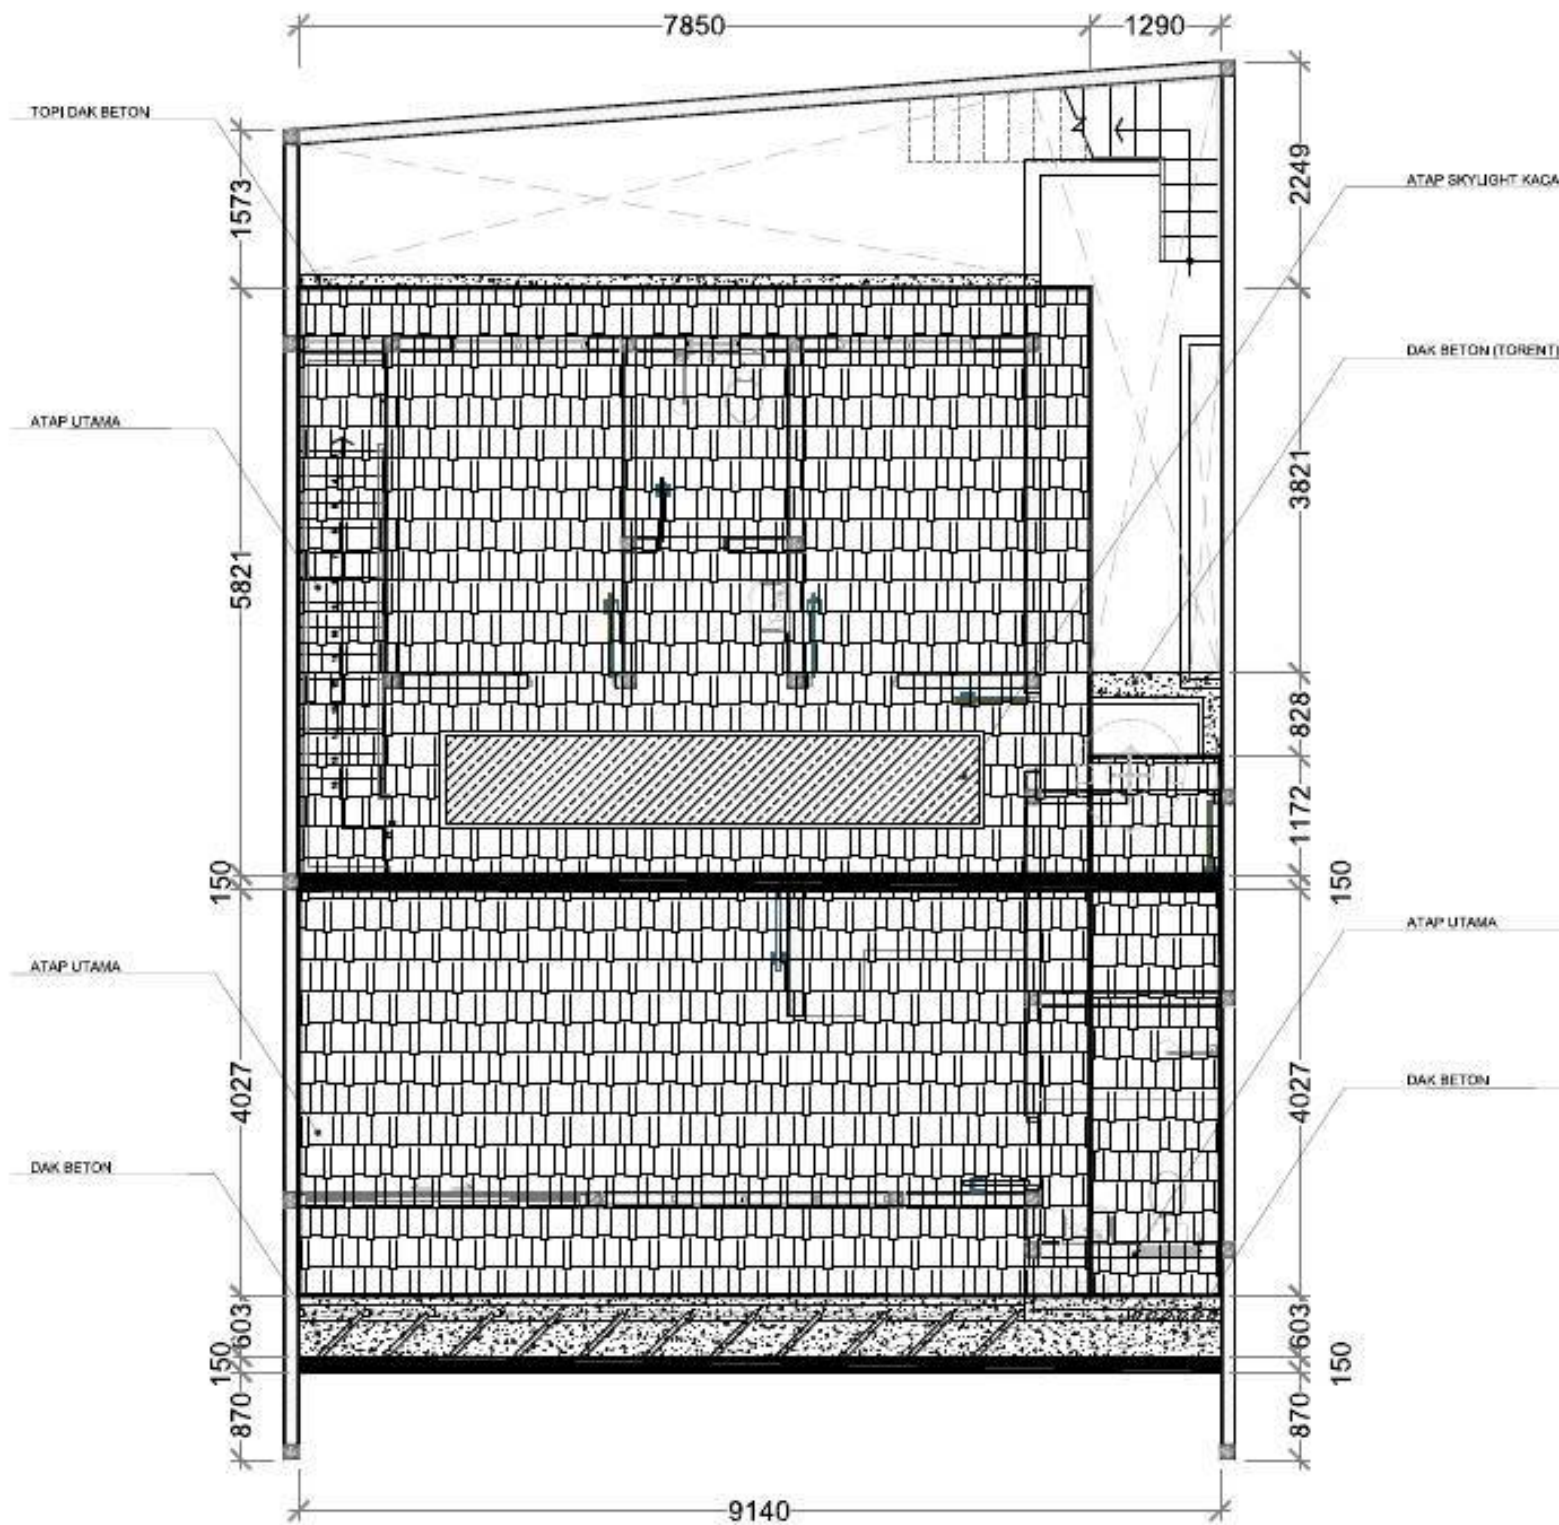


RENCANA ATAP
SKALA 1: 75

KONSULTAN		
KONTRAKTOR		
PROYEK		
TOWN HOUSE JALAN JOE JAGAKARSA JAKARTA SELATAN		
KETERANGAN		
REVISI		
	NO.	REVISI
ARSITEK		
DISAMBAH		
DIPERIKSA		
DIBETULU		
NO. PROYEK		
NAMA GAMBAR		
RENCANA ATAP KAVLING 4		
SKALA		
1 : 75		
AR-023		
SUBKAT	NO. LEMBAR	

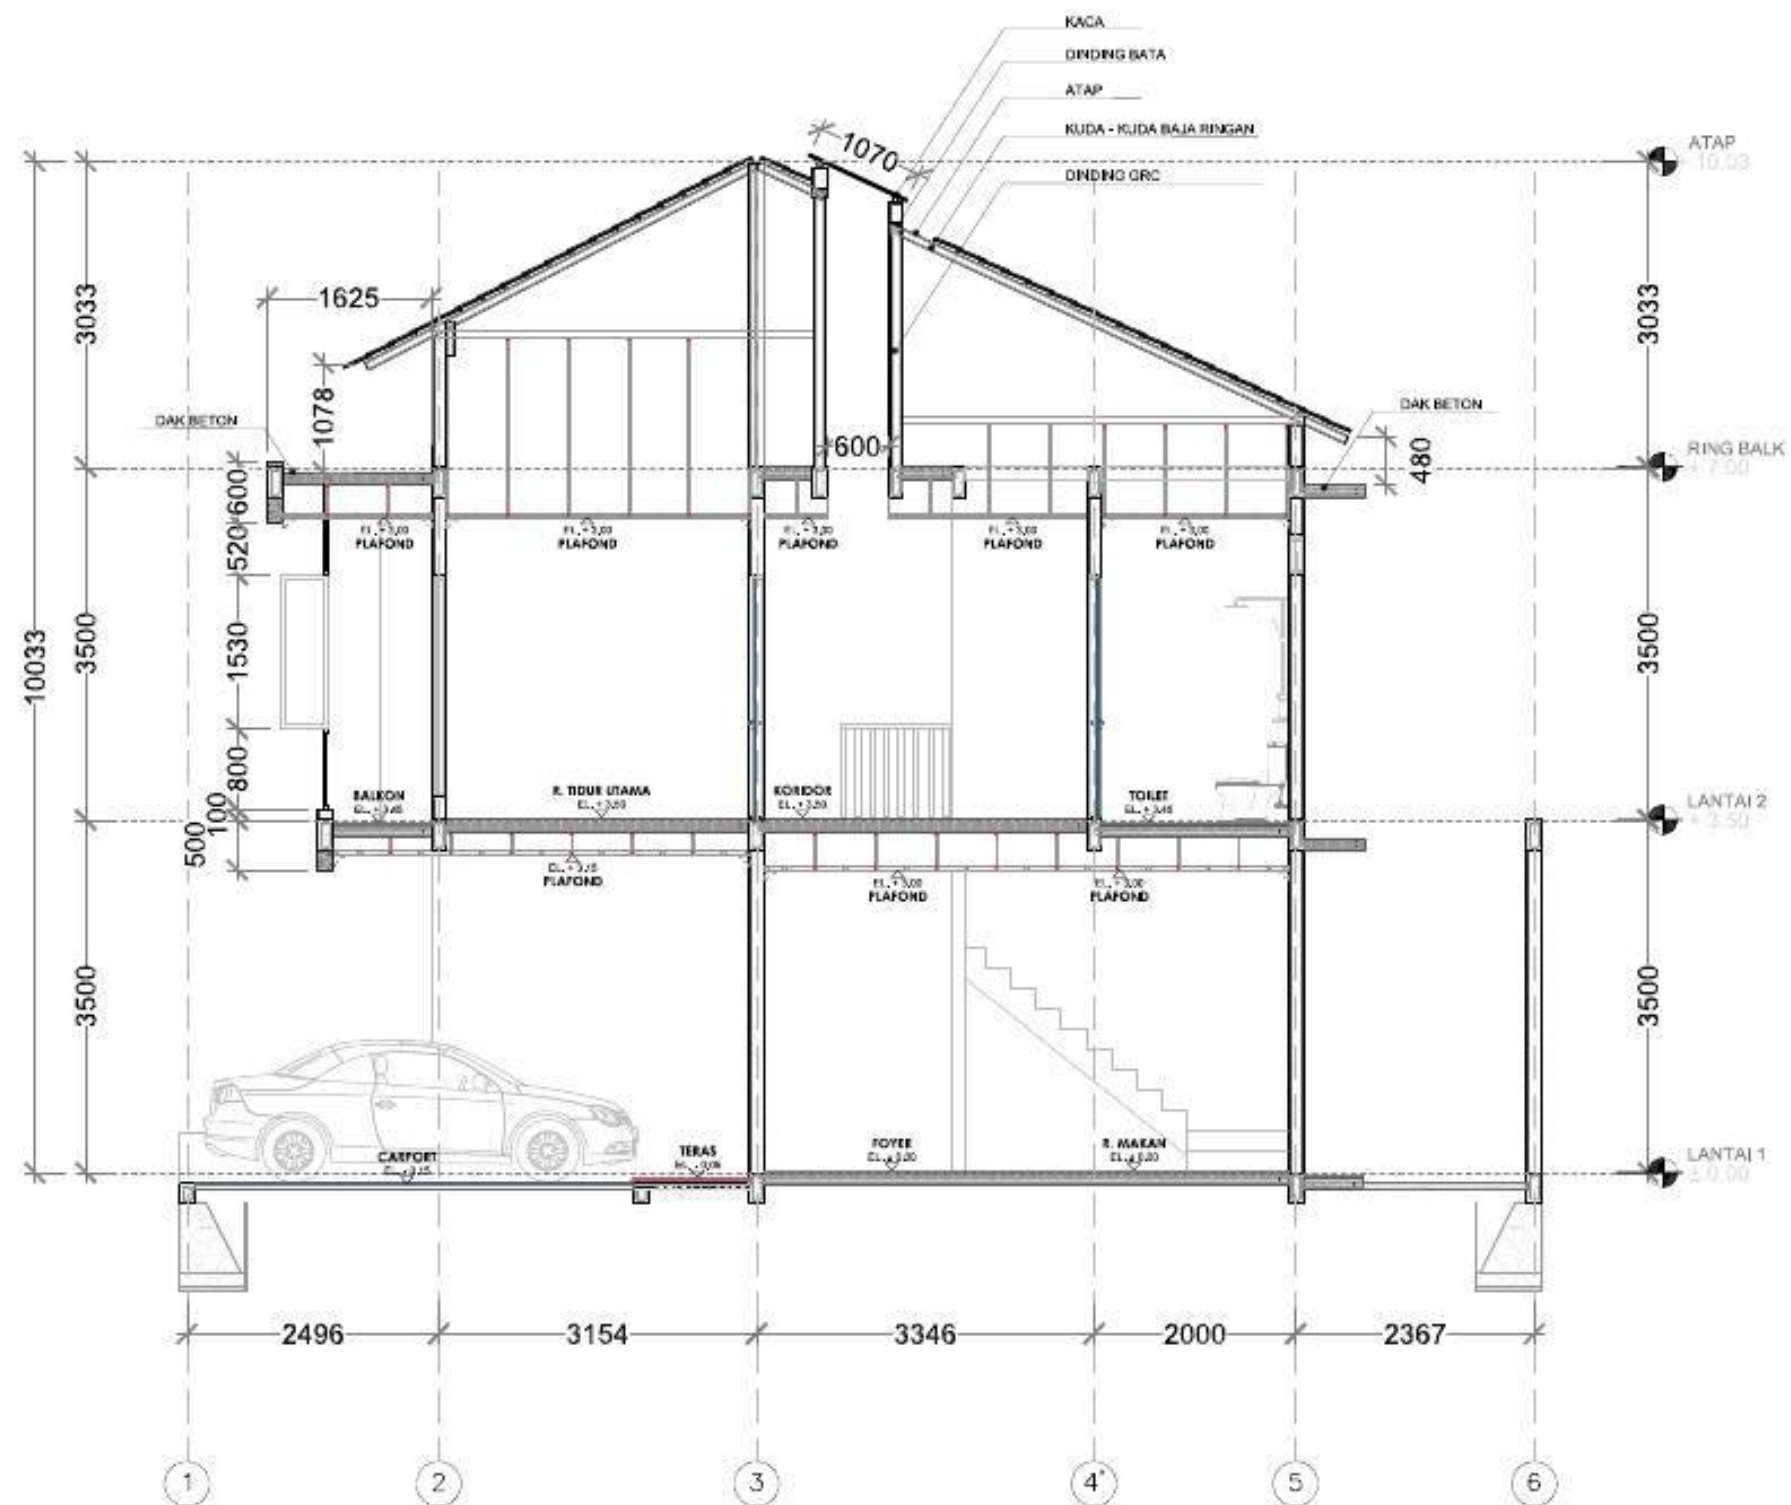


POTONGAN A - A
SKALA 1: 75

KONSULTAN	
KONTRAKTOR	
PROYEK	TOWN HOUSE JALAN JOE JAGAKARSA JAKARTA SELATAN
KETERANGAN	
REVISI	
NO. PROYEK	
NAMA GAMBAR	POTONGAN A - A KAVLING 4
SKALA	1 : 75
SUBKAT	AR-024
NO. LEMBAR	

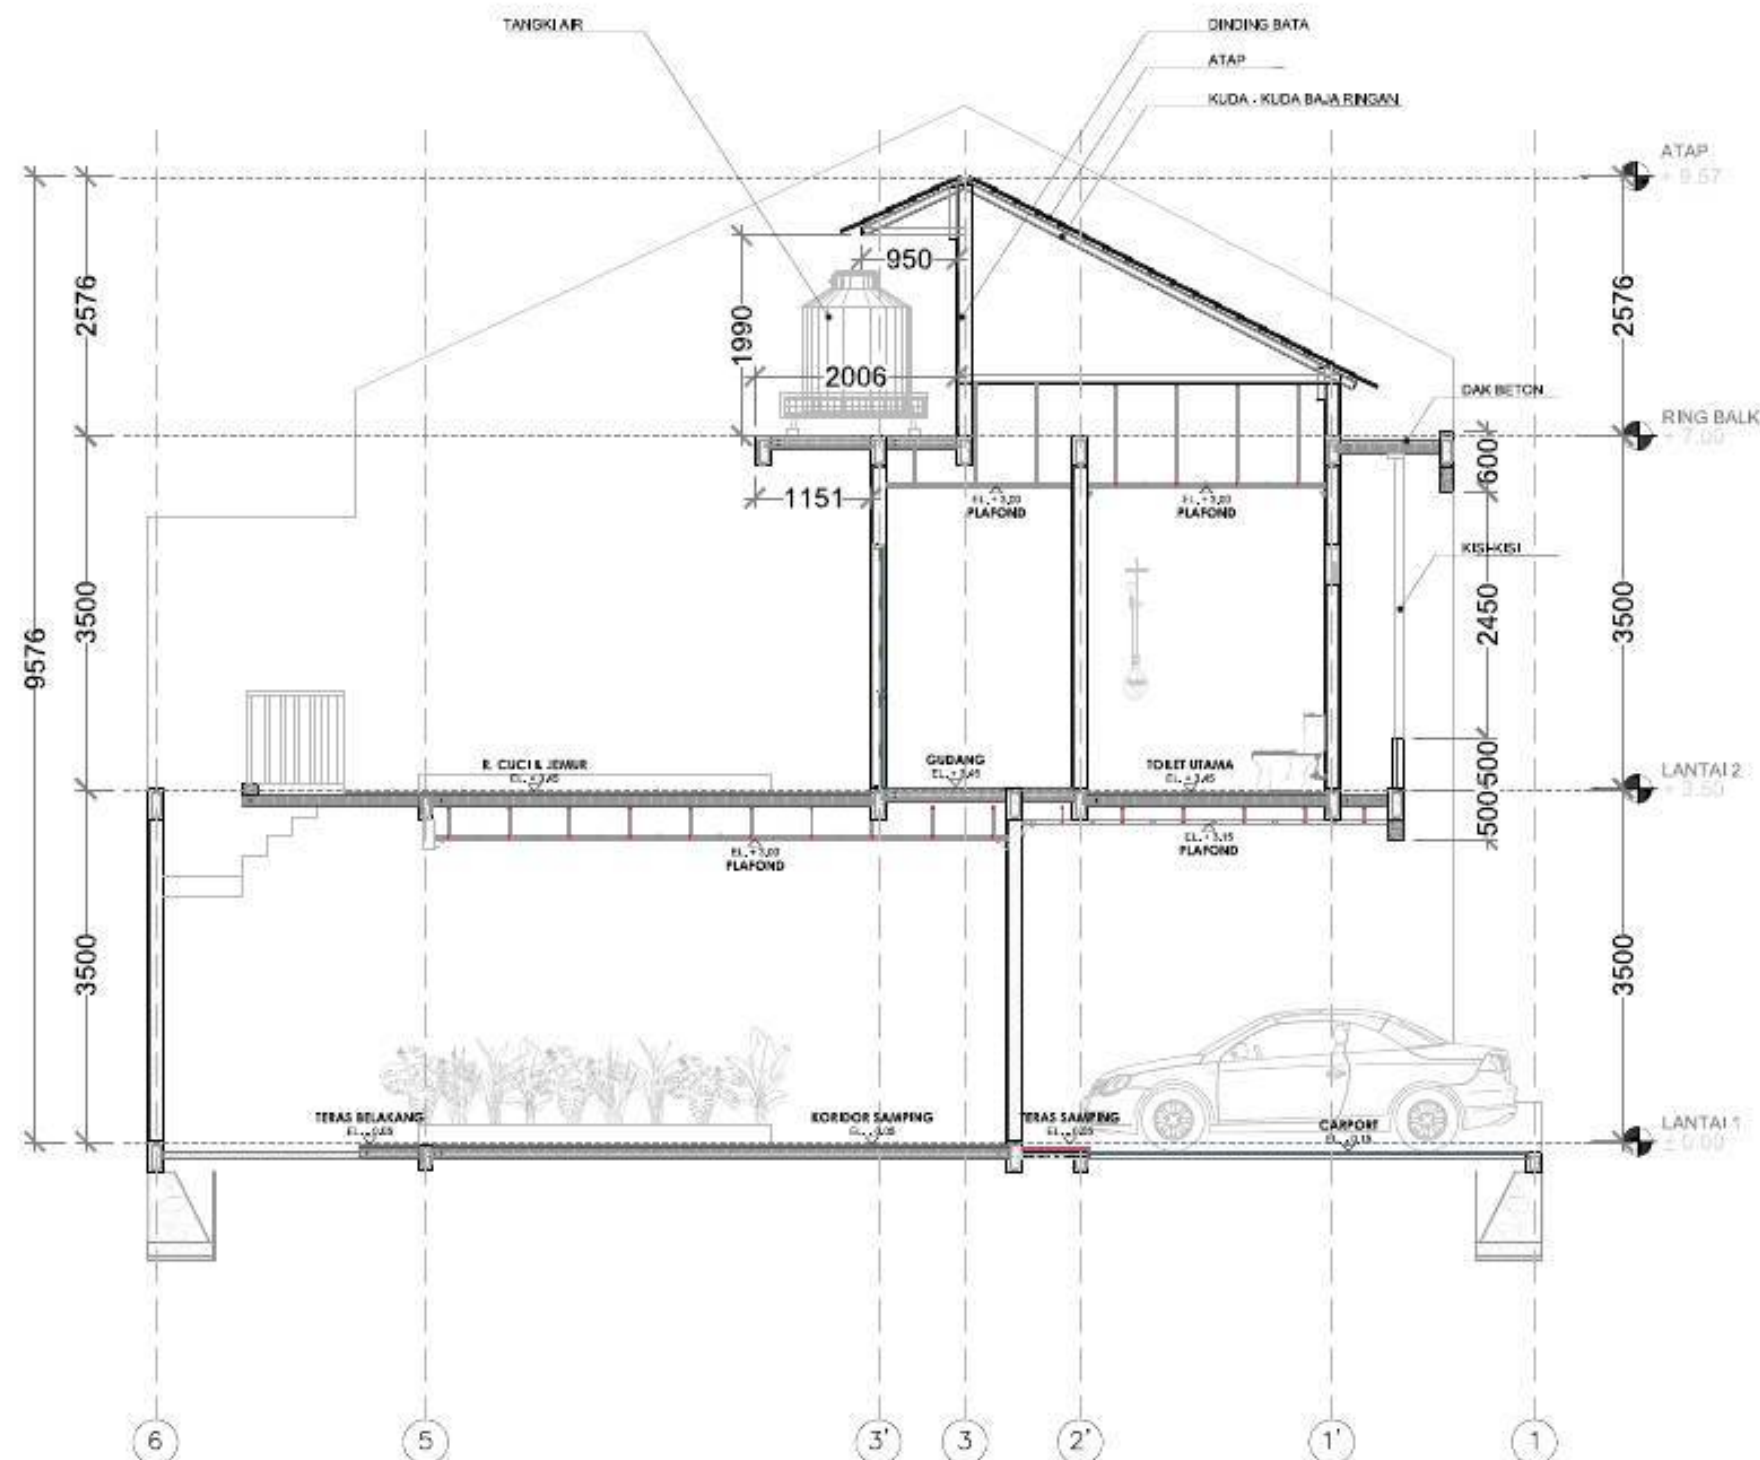


POTONGAN B - B
SKALA 1: 75

KONSULTAN	
KONTRAKTOR	
PROYEK	
TOWN HOUSE JALAN JOE JAGAKARSA JAKARTA SELATAN	
KETERANGAN	
REVISI	
NO.	REVISI
1	
2	
3	
4	
5	
6	
ARSITEK	
DISAMBAH	
DIPERIKSA	
DIBETULI	
NO. PROYEK	
NAMA GAMBAR	
POTONGAN B - B KAVLING 1	
SKALA	
1 : 75	
AR-025	
SUBKAT	NO. LEMBAR

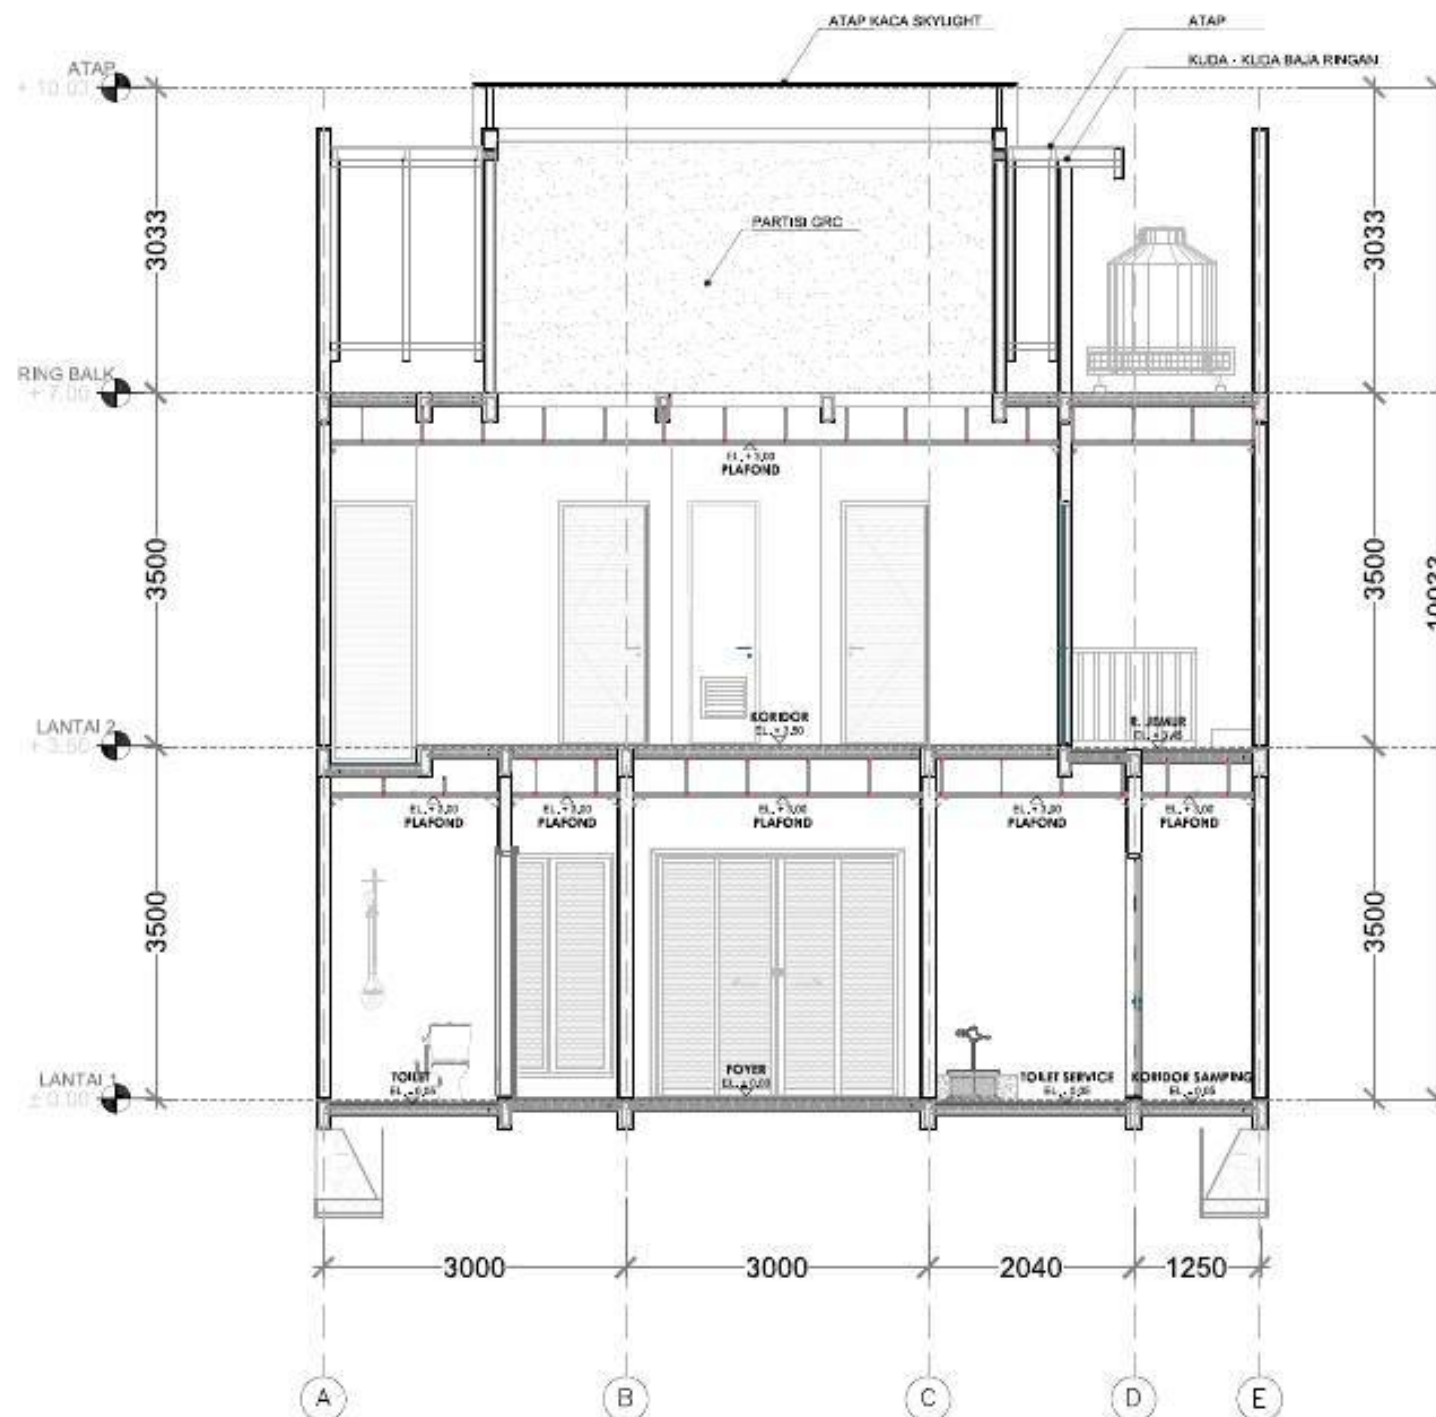


POTONGAN C - C
SKALA 1: 75

KONSULTAN	
KONTRAKTOR	
PROYEK	
TOWN HOUSE JALAN JOE JAGAKARSA JAKARTA SELATAN	
KETERANGAN	
REVISI	
NO.	REVISI
1	
2	
3	
4	
5	
6	
7	
8	
9	
10	
ARSITEK	
DISAMBAH	
DIPERIKSA	
DIBETULI	
NO. PROYEK	
NAMA GAMBAR	
POTONGAN C - C KAVLING 4	
SKALA	
1 : 75	
AR-026	
SUBKAT	NO. LEMBAR

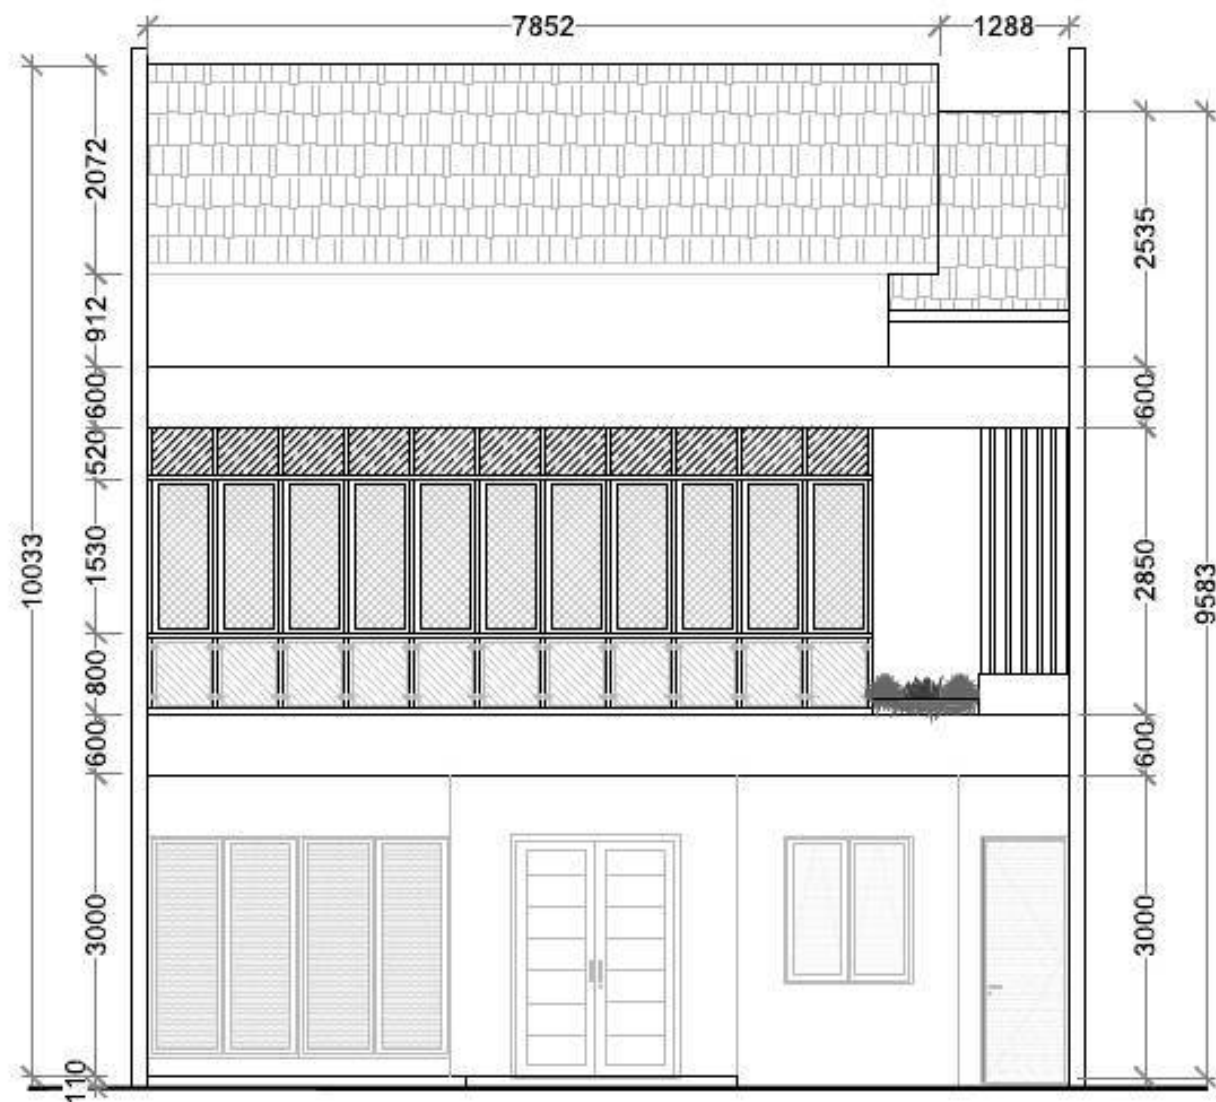

TAMPAK DEPAN



SKALA 1: 75

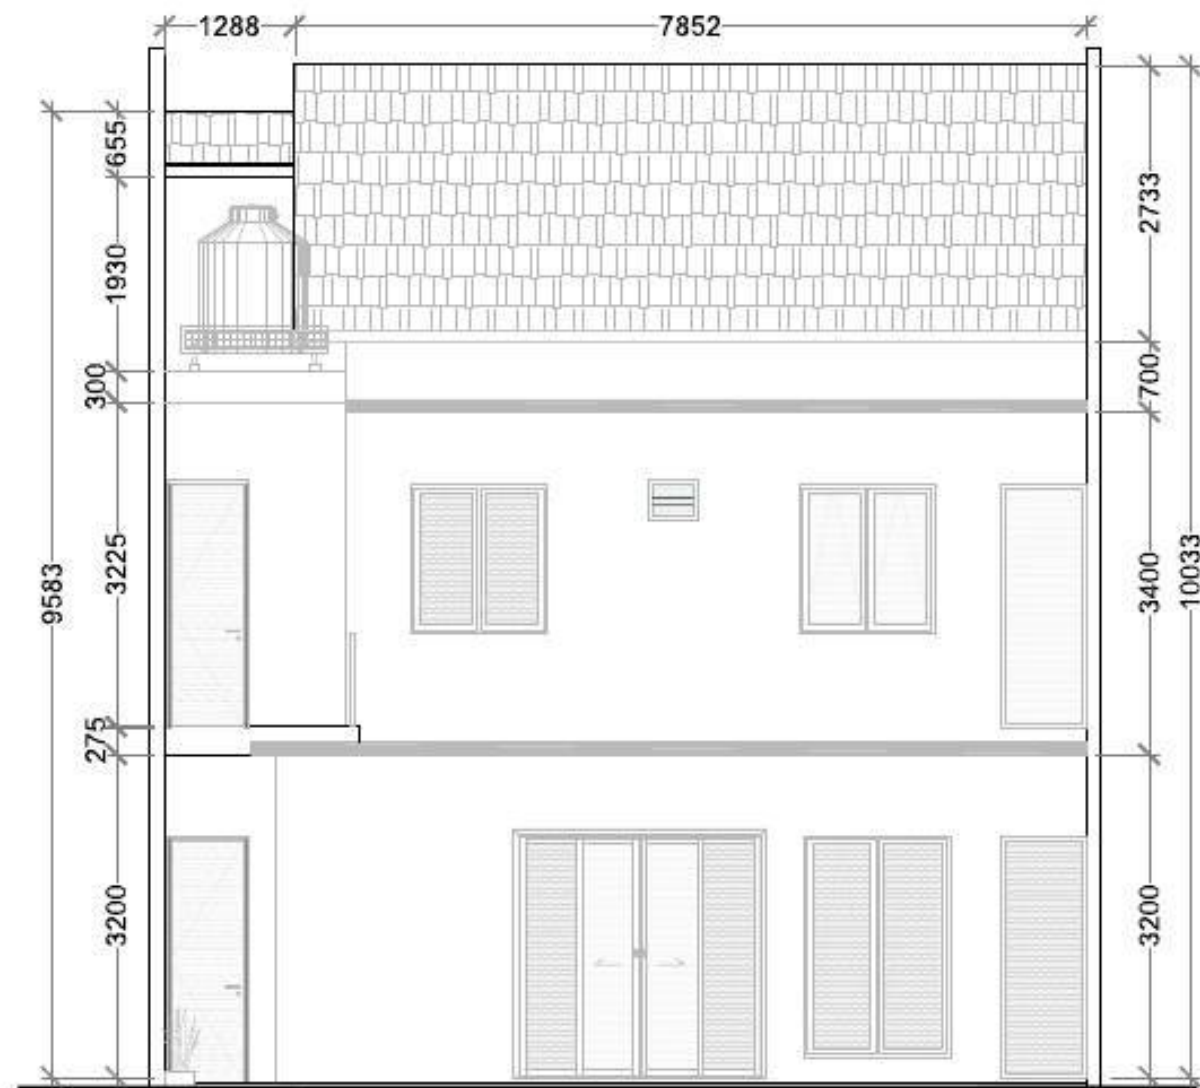


TAMPAK BELAKANG

SKALA 1: 75

KONSULTAN	
KONTRAKTOR	
PROYEK	
TOWN HOUSE JALAN JOE JAGAKARSA JAKARTA SELATAN	
KETERANGAN	
REVISI	NO. DSK. TH. 2
ARSITEK	
DIKAMBAR	
DIPERIKSA	
DIBETULI	
NO. PROYEK	
NAMA GAMBAR	
TAMPAK KAVLING 4	
SKALA	1 : 75
AR-027	
SUBKAT	NO. LEMBAR

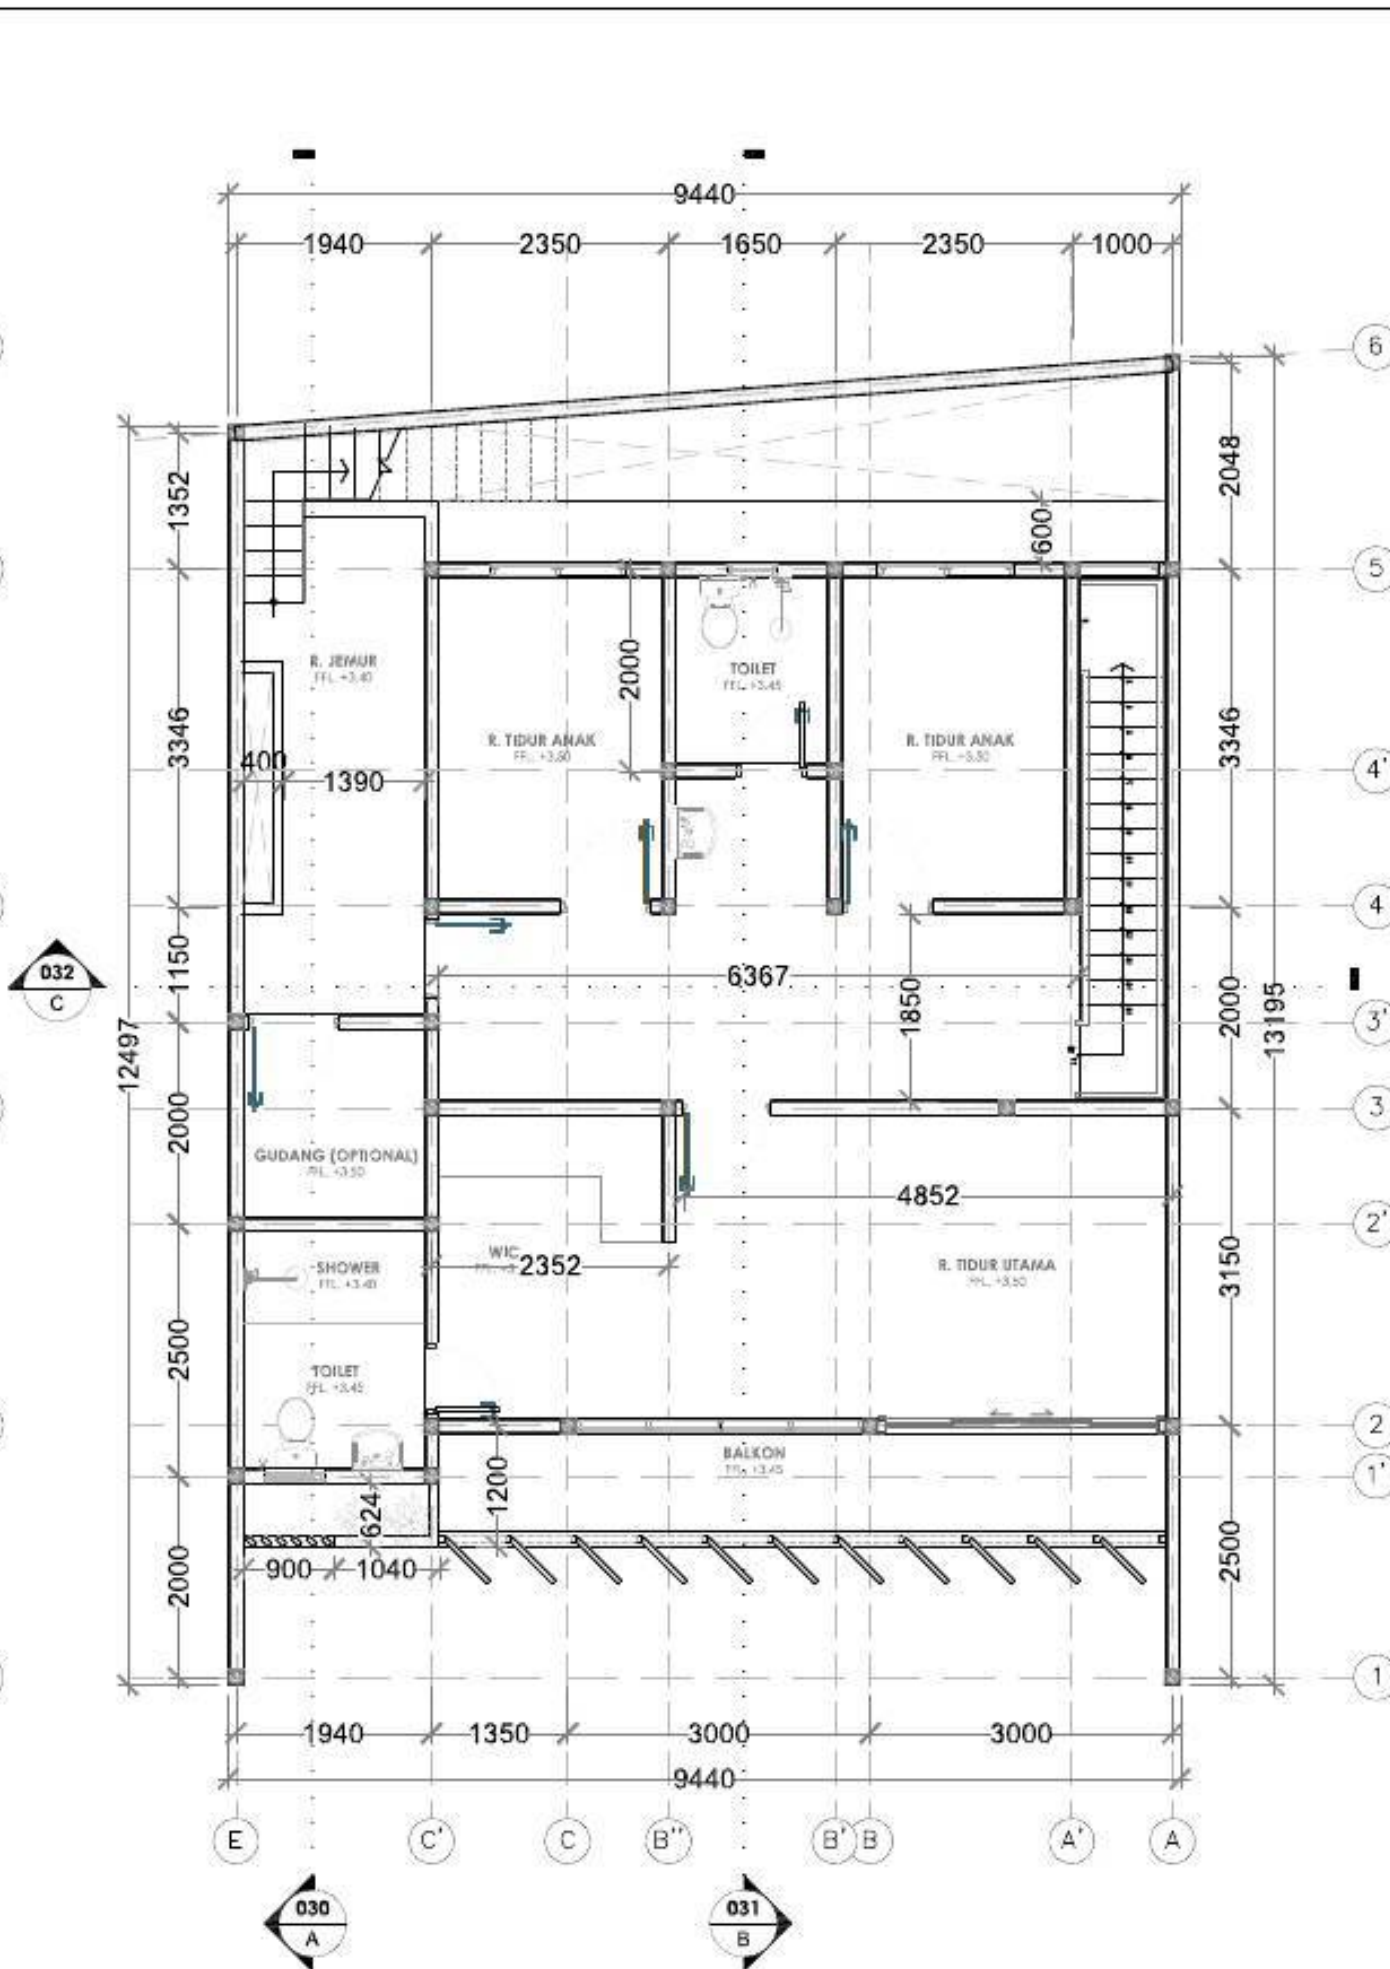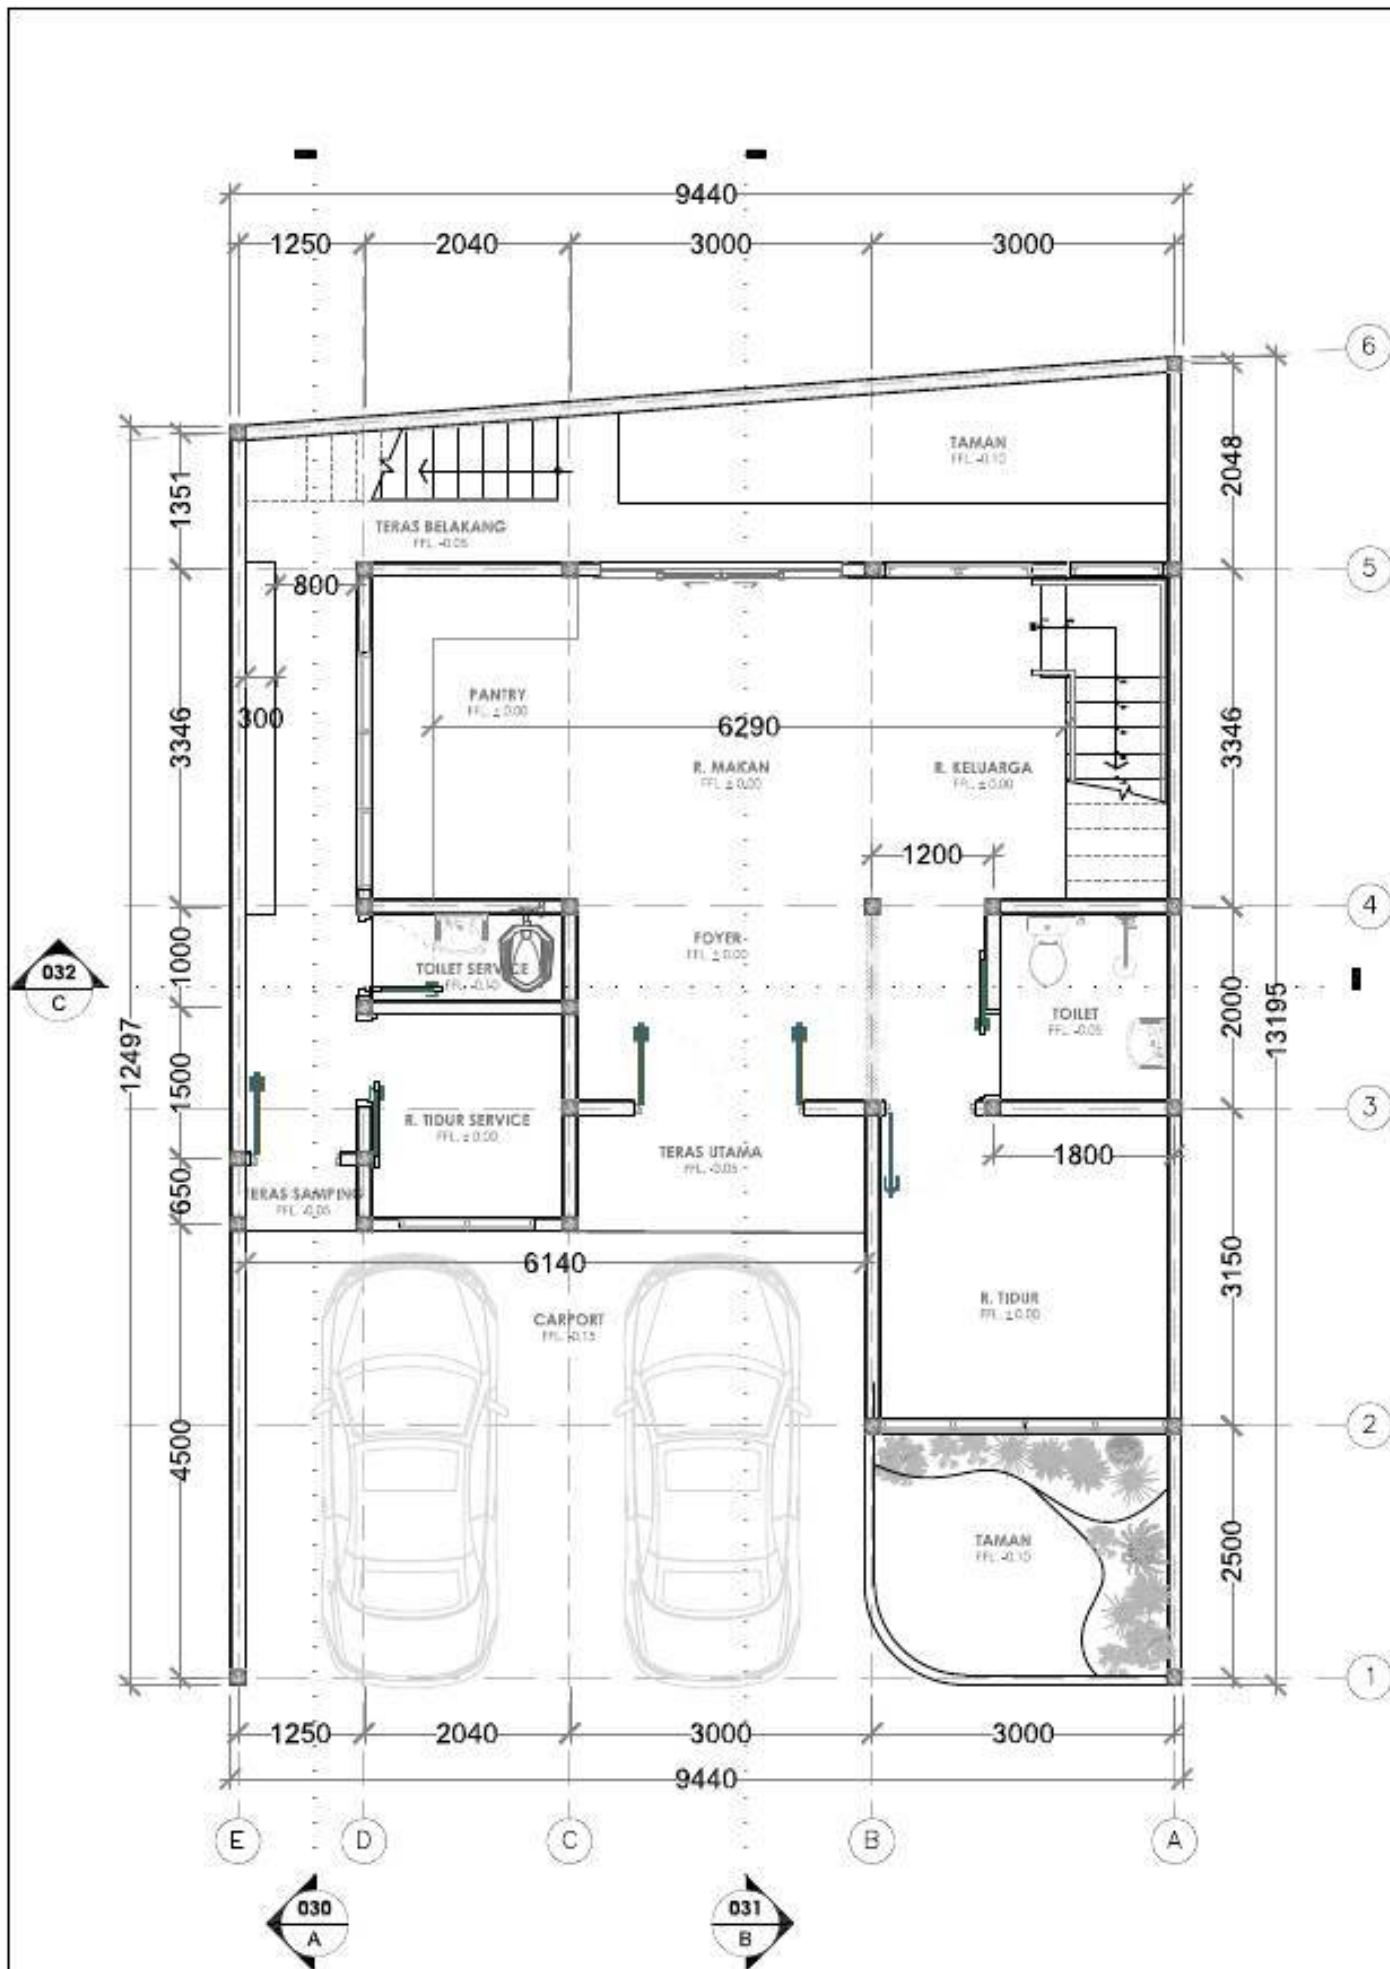


KONSULTAN	
KONTRAKTOR	
PROYEK	TOWN HOUSE JALAN JOE JAGAKARSA JAKARTA SELATAN
KETERANGAN	
REVISI	
ARSITEK	
DIKAMBAR	
DIPERIKSA	
DIBETULI	
NO. PROYEK	
NAMA GAMBAR	DENAH KAVLING 5
SKALA	1 : 75
SUBKAT	AR-028
NO. LEMBAR	

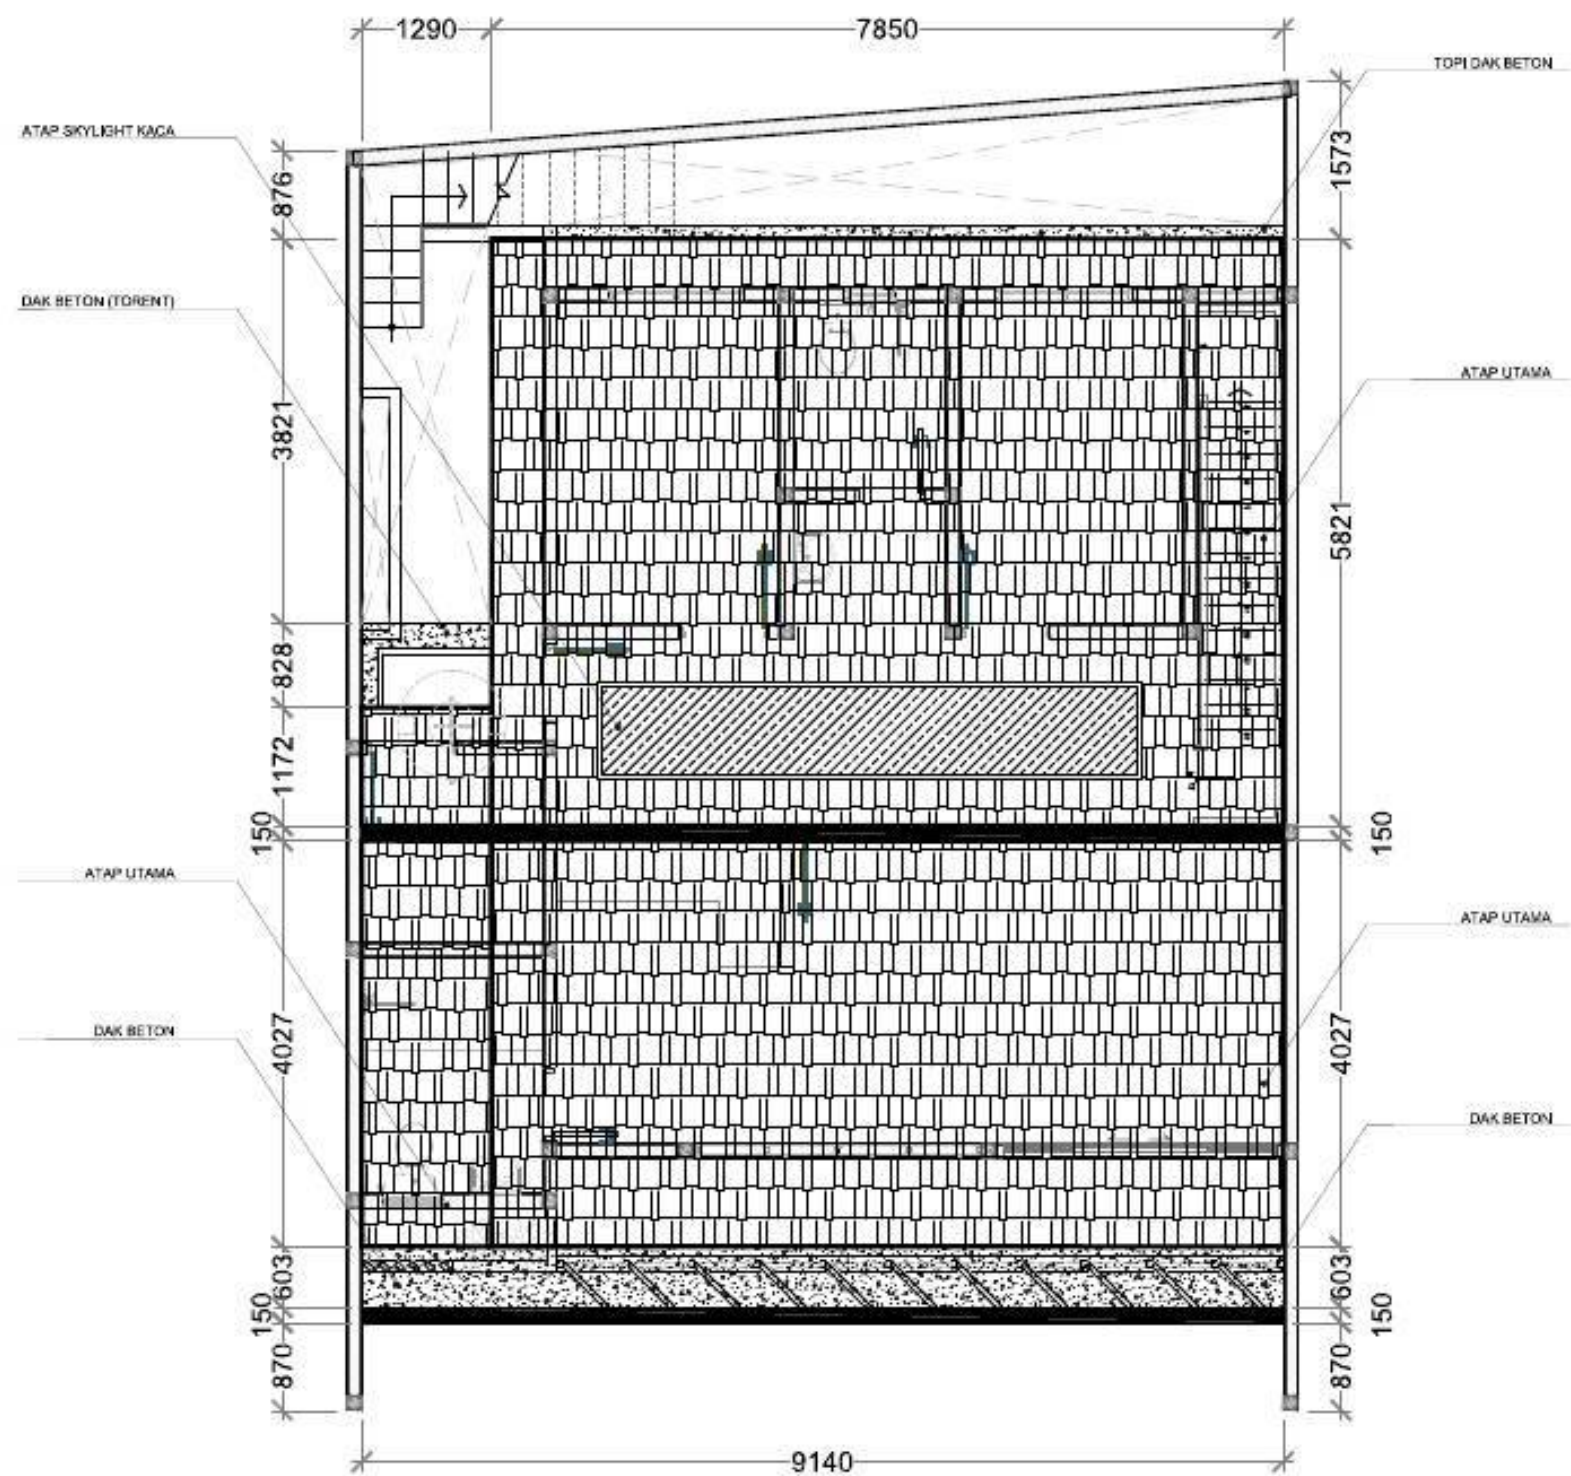


RENCANA ATAP
SKALA 1: 75

KONSULTAN			
KONTRAKTOR			
PROYEK			
TOWN HOUSE JALAN JOE JAGAKARSA JAKARTA SELATAN			
KETERANGAN			
REVISI			
		NO.	REVISI
ARSITEK			
DISAMBAH			
DIPERIKSA			
DIBETULU			
NO. PROYEK			
NAMA GAMBAR			
RENCANA ATAP KAVLING 5			
SKALA			
1 : 75			
AR-029			
SUBKAT	NO. LEMBAR		

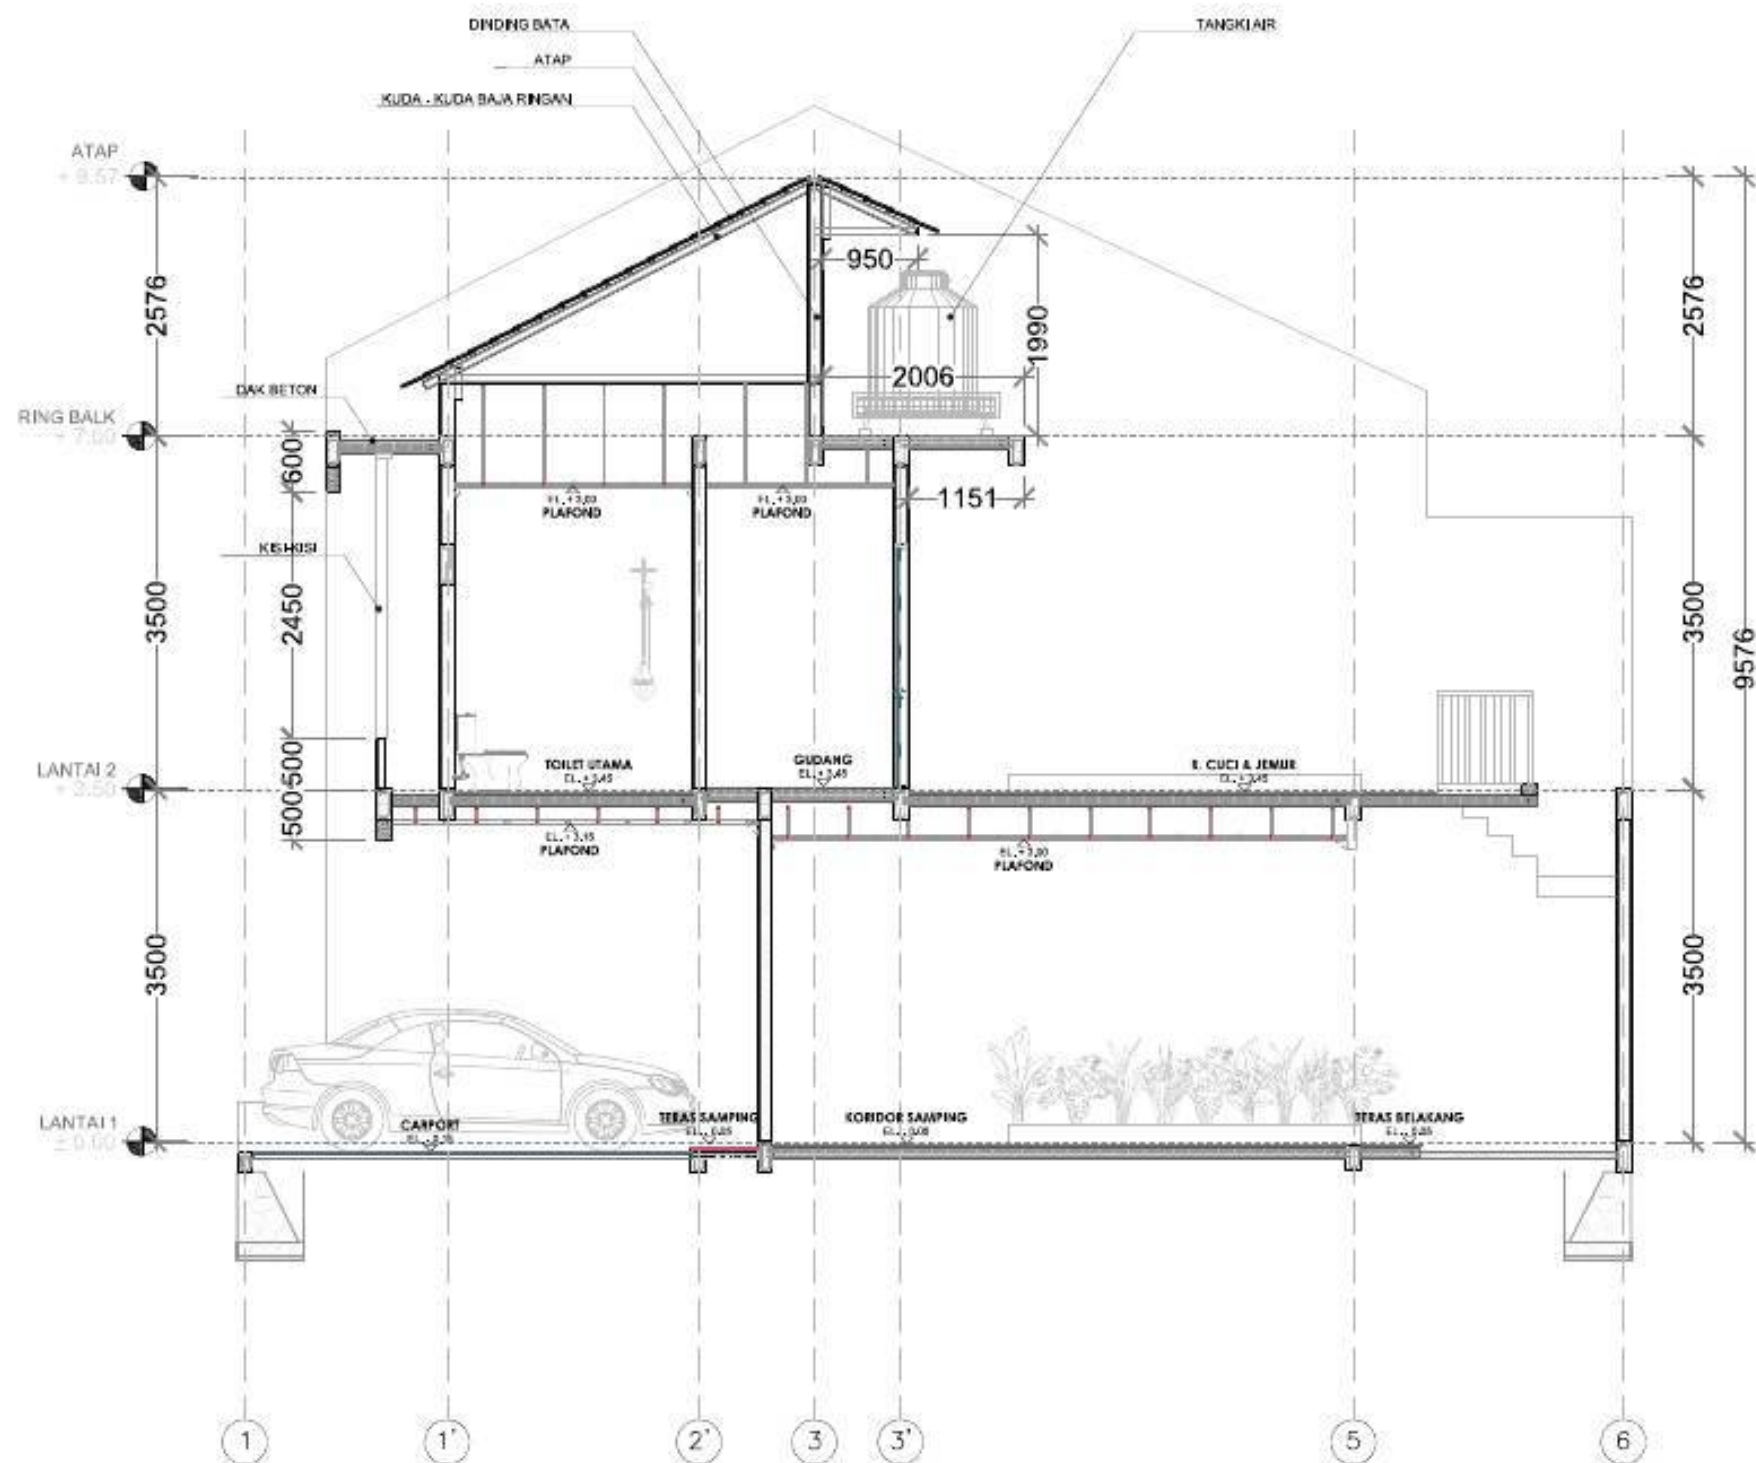


POTONGAN A - A
SKALA 1: 75

KONSULTAN	
KONTRAKTOR	
PROYEK	
TOWN HOUSE JALAN JOE JAGAKARSA JAKARTA SELATAN	
KETERANGAN	
REVISI	NO. DOK. DES. TITIK
ARSITEK	
DIBANGUN	
DIPERIKSA	
DIBETULKAN	
NO. PROYEK	
NAMA GAMBAR	
POTONGAN A - A KAVLING 5	
SKALA	1 : 75
AR-030	
SUBKAT	NO. LEMBAR

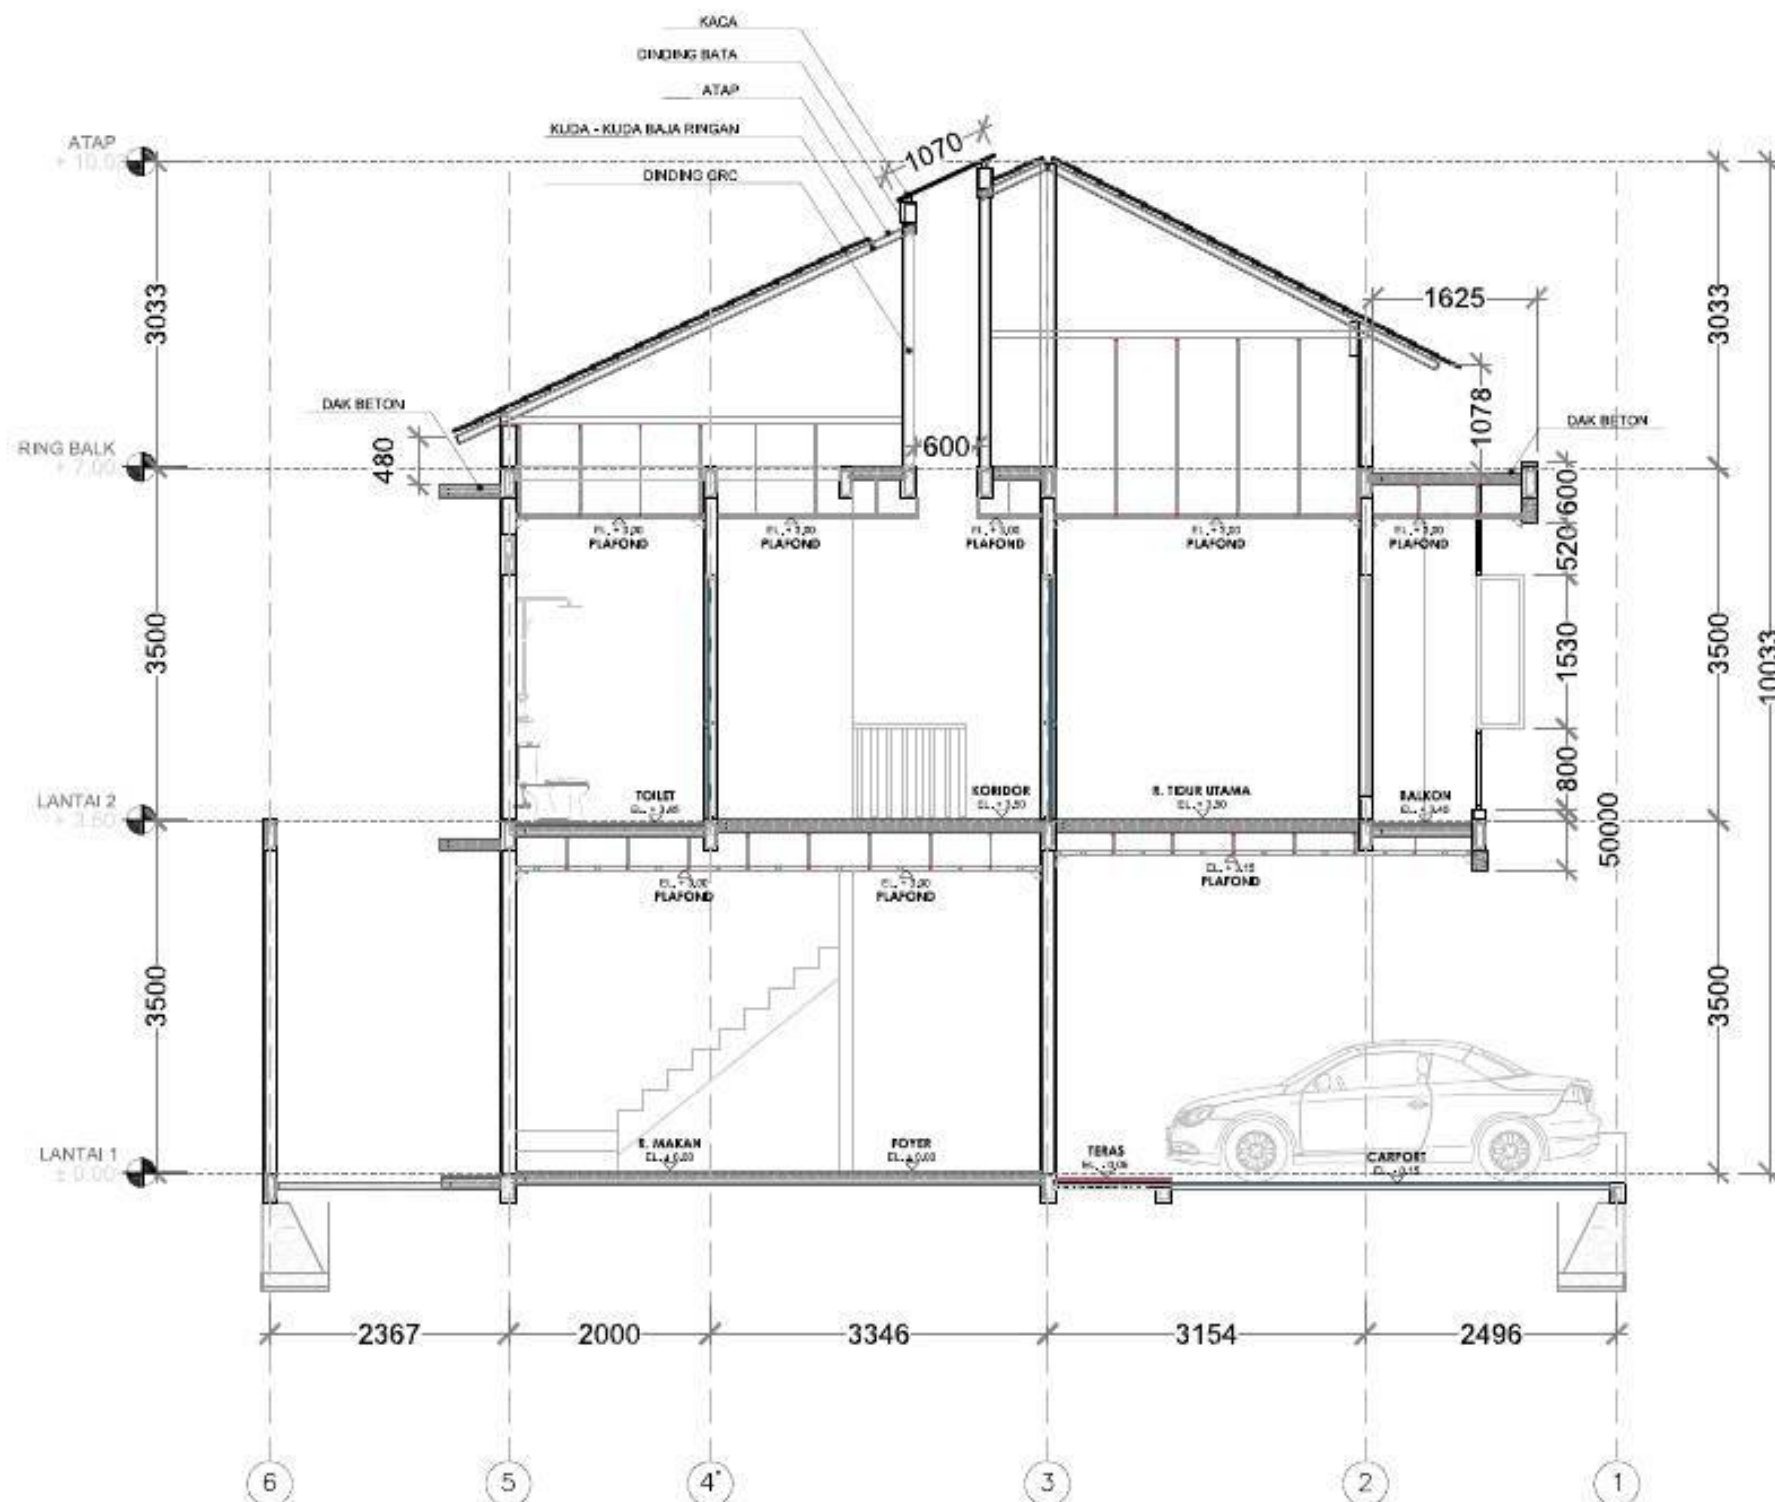



POTONGAN B - B
SKALA 1: 75

KONSULTAN	
KONTRAKTOR	
PROYEK	
TOWN HOUSE JALAN JOE JAGAKARSA JAKARTA SELATAN	
KETERANGAN	
REVISI	TOU, SEN, THA
ARSITEK	
DOKUMENTASIR	
DIPERIKSA	
DIBETULI	
NO. PROYEK	
-	
NAMA GAMBAR	
POTONGAN B - B KAVLING 5	
SKALA	
1 : 75	
AR-031	
SUBKAT	NO. LEMBAR

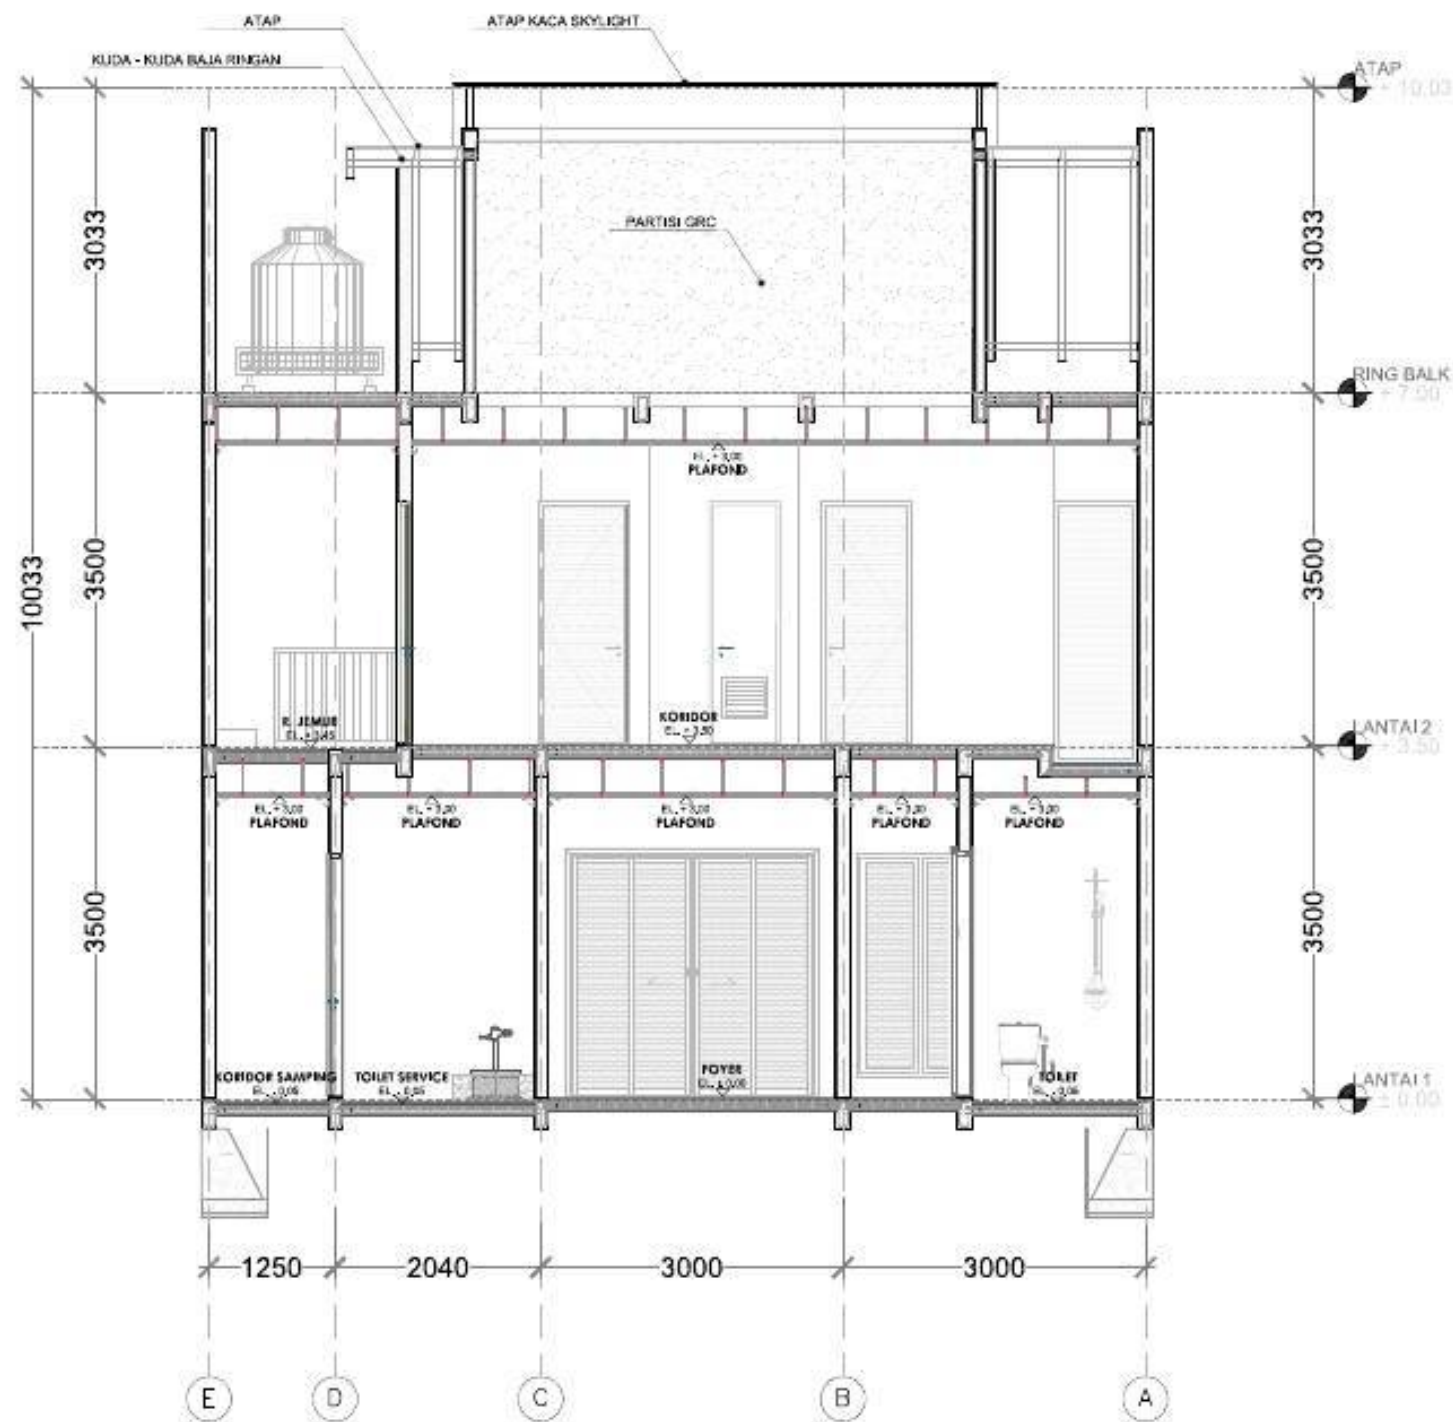


POTONGAN C - C
SKALA 1: 75


KONSULTAN	
KONTRAKTOR	
PROYEK	TOWN HOUSE JALAN JOE JAGAKARSA JAKARTA SELATAN
KETERANGAN	
REVISI	NO. DES. THP
ARSITEK	
DIKAMBAR	
DIPERIKSA	
DIBETULI	
NO. PROYEK	
NAMA GAMBAR	POTONGAN C - C KAVLING 5
SKALA	1 : 75
AR-032	
SUBKAT	NO. LEMBAR

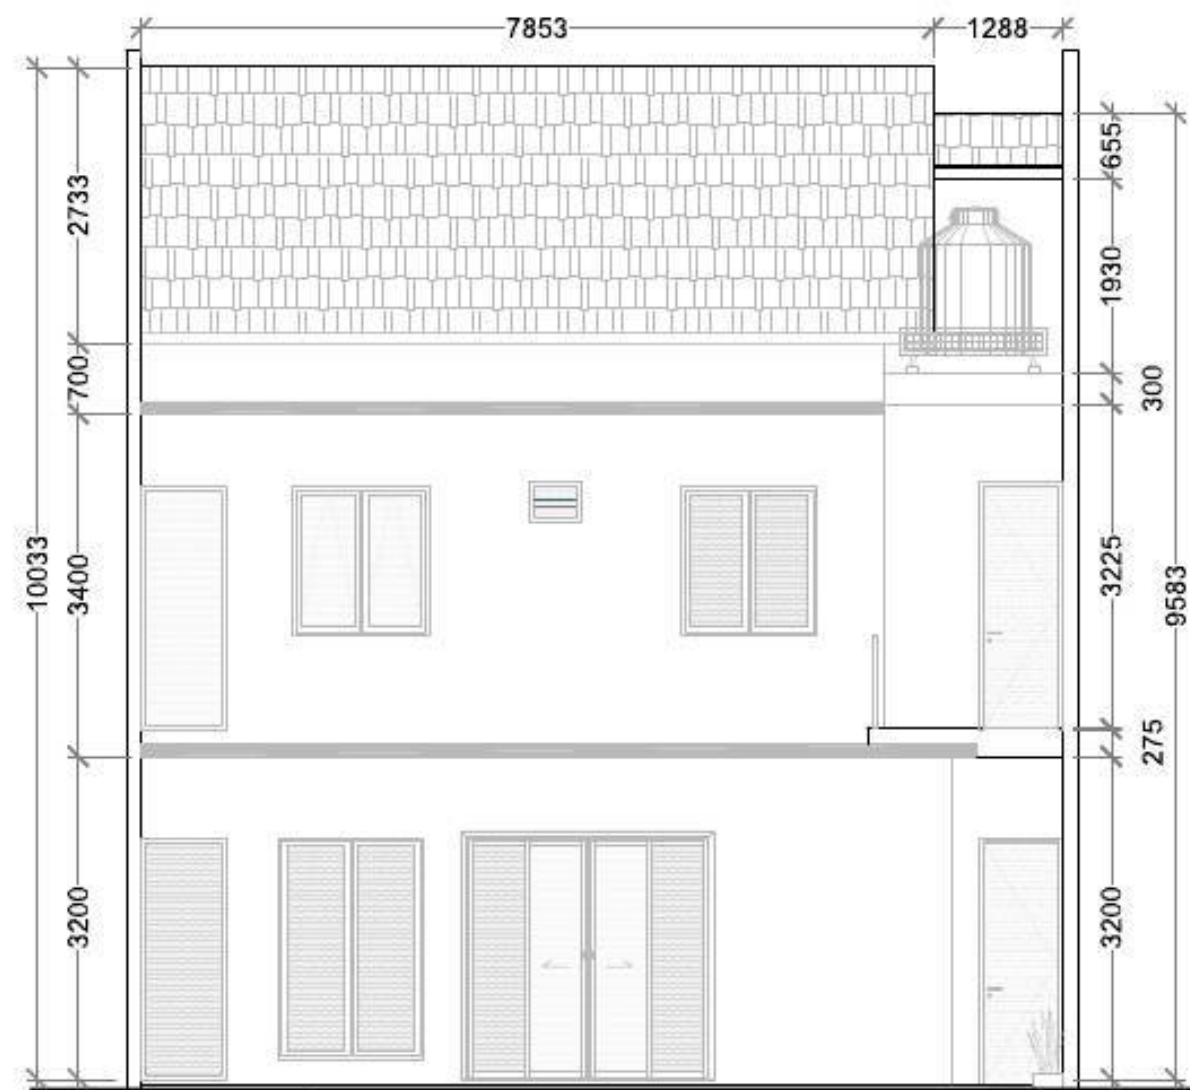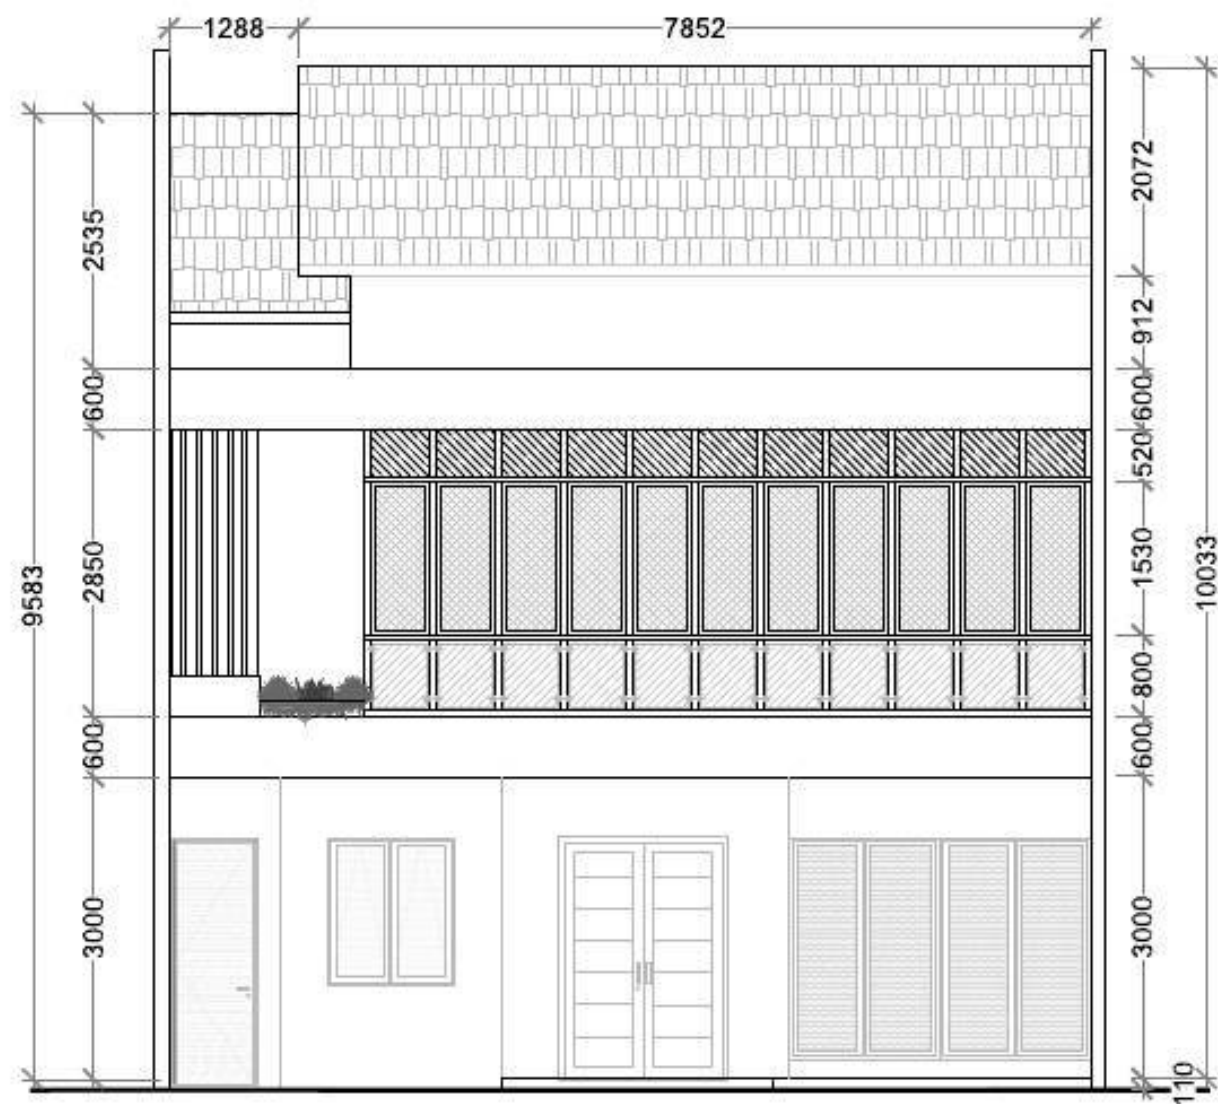

KONSULTAN

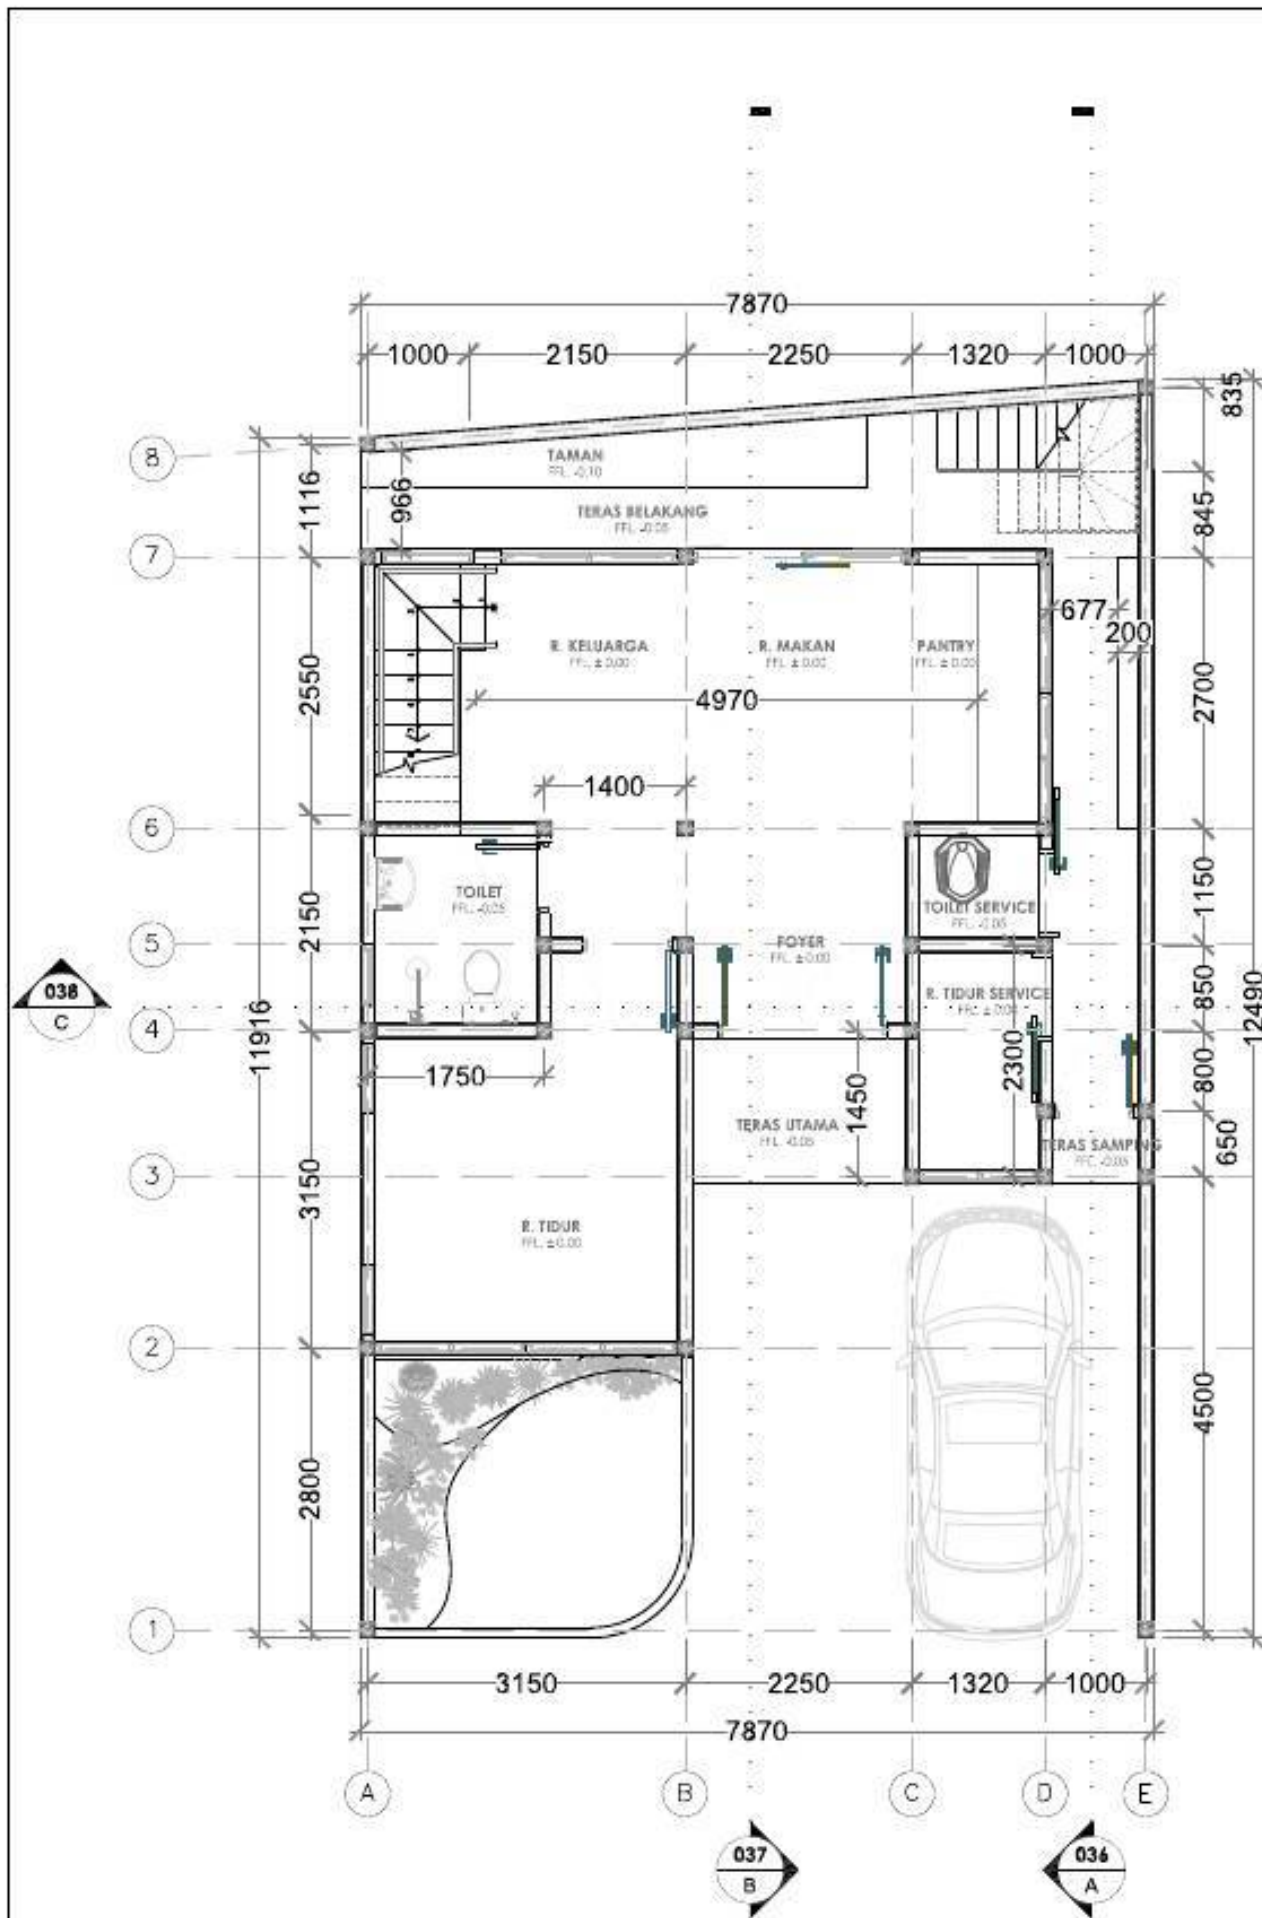

DENAH LANTAI DASAR
SKALA 1: 75

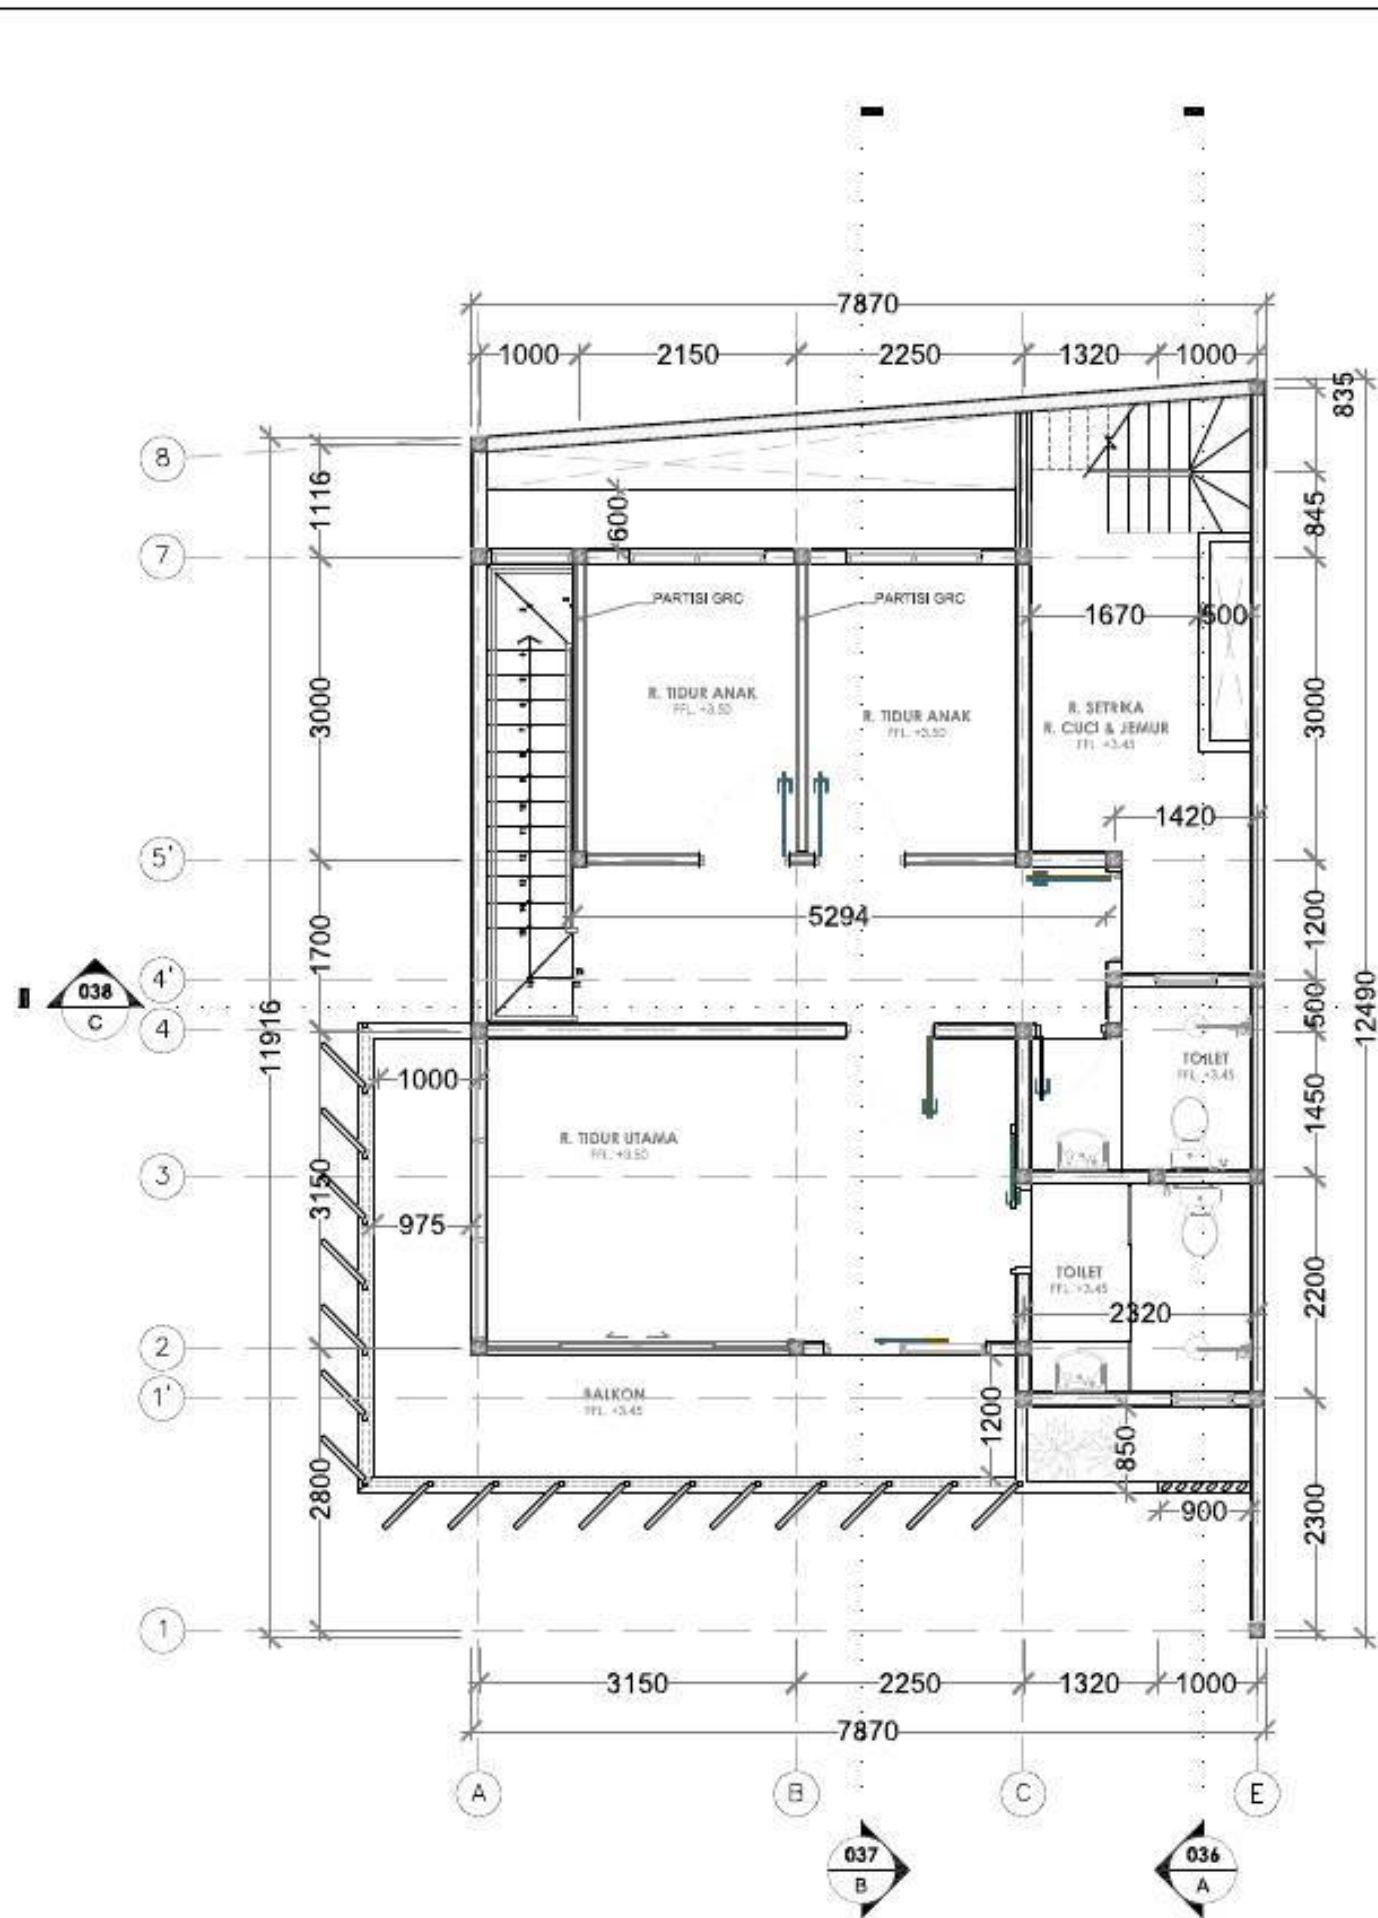


DENAH LANTAI ATAS
SKALA 1: 75

KONSULTAN	
KONTRAKTOR	
PROYEK	TOWN HOUSE JALAN JOE JAGAKARSA JAKARTA SELATAN
KETERANGAN	
REVISI	
ARSITEK	
DOKUMENTASIR	
DIPERIKSA	
DIBETULKAN	
NO. PROYEK	
NAMA GAMBAR	DENAH KAVLING 6
SKALA	1 : 75
AR-034	
SUBKAT	NO. LEMBAR



NO. LEMBAR

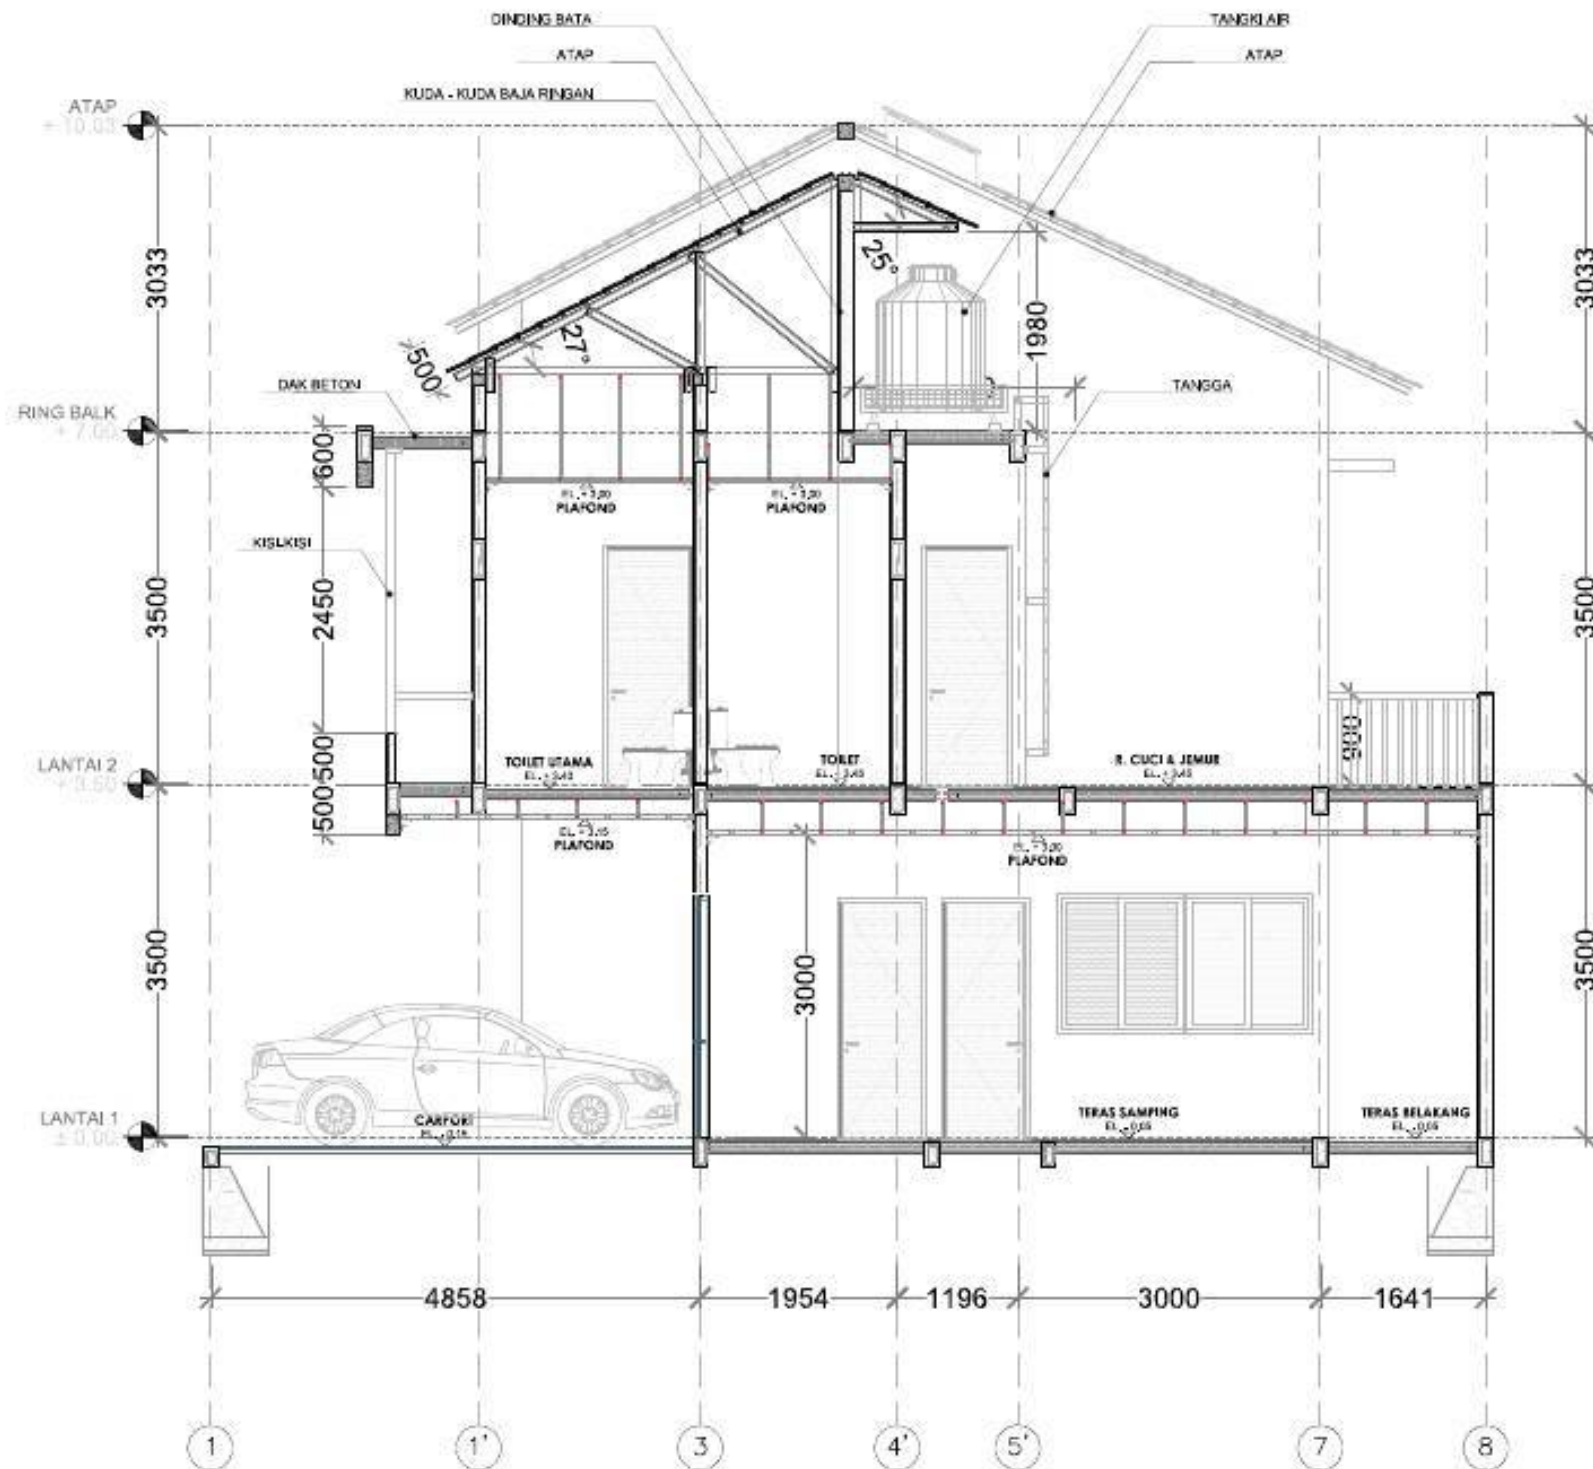


POTONGAN A - A
SKALA 1: 75

KONSULTAN	
KONTRAKTOR	
PROYEK	
TOWN HOUSE JALAN JOE JAGAKARSA JAKARTA SELATAN	
KETERANGAN	
REVISI	NO. DOK. DES. 1102
ANOTASI	
DIBANGUN	
DIPERIKSA	
DIBETULI	
NO. PROYEK	
-	
NAMA GAMBAR	
POTONGAN A - A KAVLING 6	
SKALA	
1 : 75	
AR-036	
SUBKAT	NO. LEMBAR




POTONGAN B - B
SKALA 1: 75

KONSULTAN	
KONTRAKTOR	
PROYEK	TOWN HOUSE JALAN JOE JAGAKARSA JAKARTA SELATAN
KETERANGAN	
REVISI	NO. DES. THP
ARSITEK	
DIKAMBAR	
DIPERIKSA	
DIBETULI	
NO. PROYEK	
NAMA GAMBAR	POTONGAN B - B KAVLING 6
SKALA	1 : 75
AR-037	
SUBKAT	NO. LEMBAR

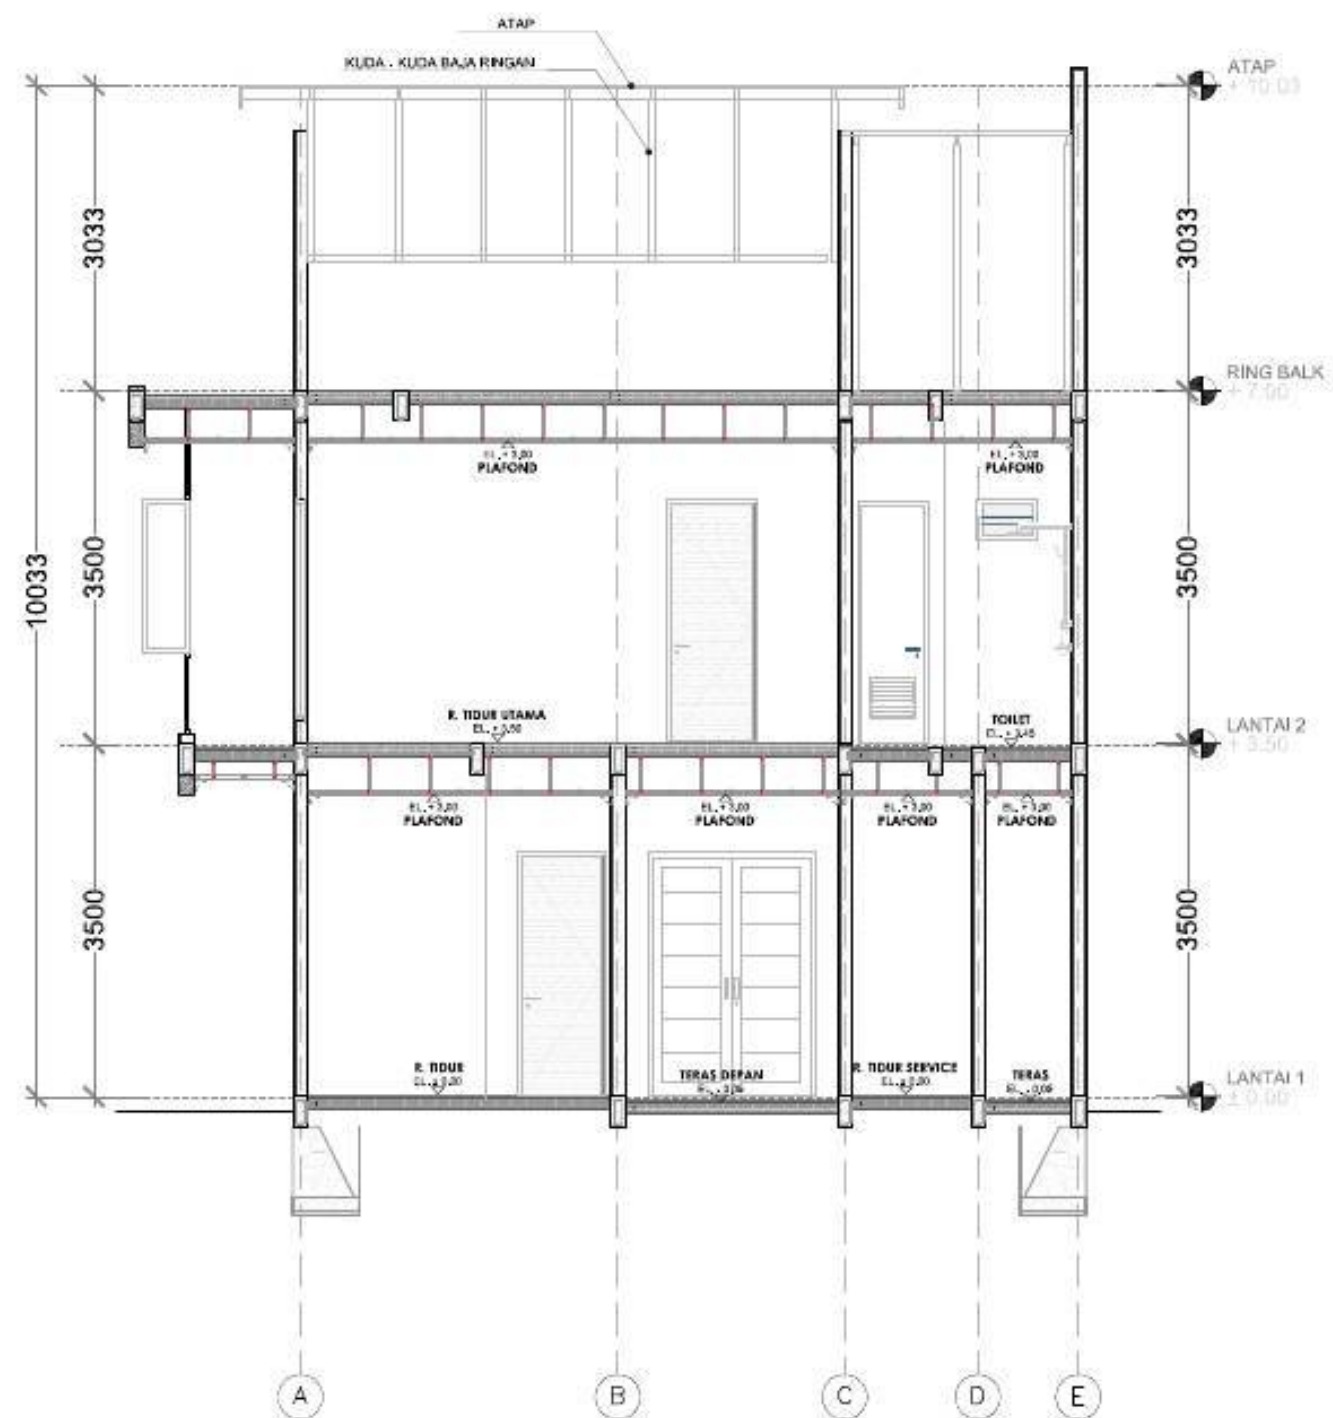


POTONGAN C - C
SKALA 1: 75

KONSULTAN			
KONTRAKTOR			
PROYEK			
TOWN HOUSE JALAN JOE JAGAKARSA JAKARTA SELATAN			
KETERANGAN			
REVISI			
ARSITEK			
DOKUMENTASIR			
DIPERIKSA			
DIBETULKAN			
NO. PROYEK			
NAMA GAMBAR			
POTONGAN C - C KAVLING 6			
SKALA			
1 : 75			
AR-038			
SUBKAT		NO. LEMBAR	

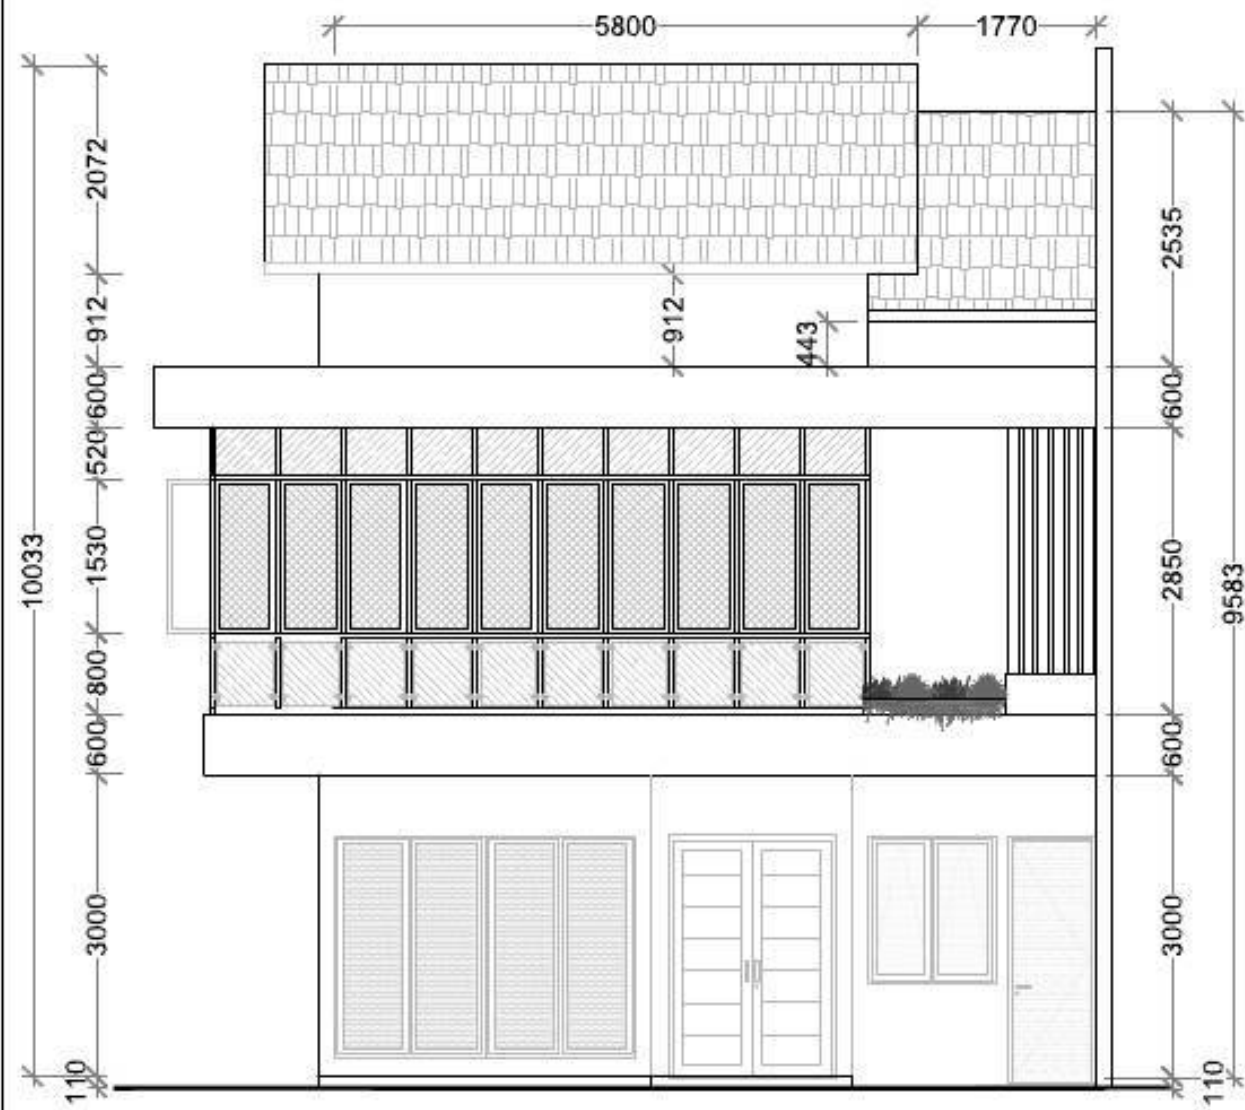

TAMPAK DEPAN


SKALA 1: 75

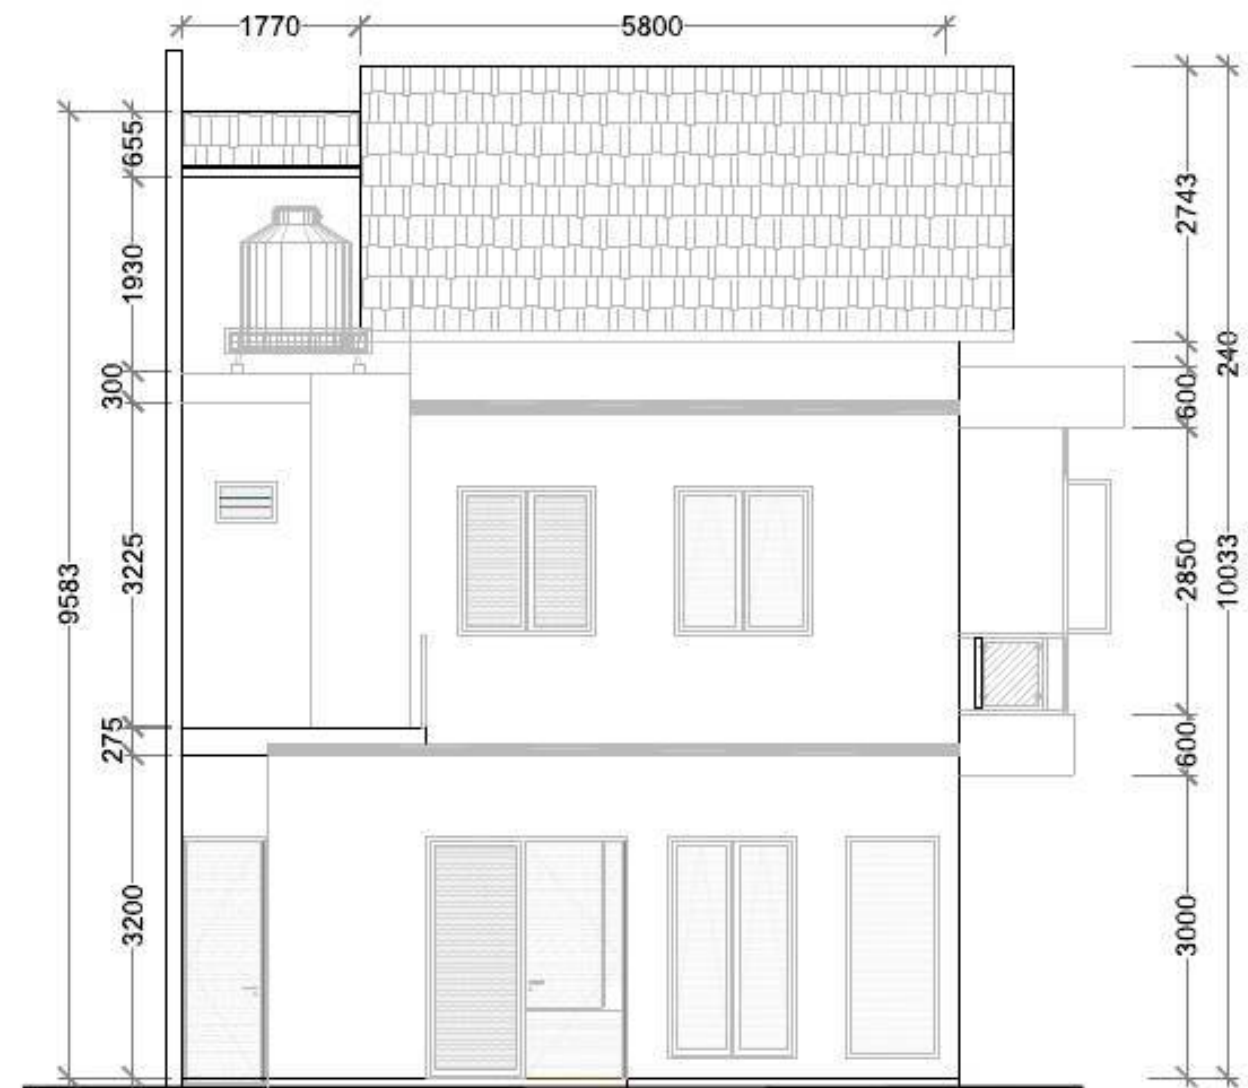

TAMPAK BELAKANG


SKALA 1: 75

KONSULTAN	
KONTRAKTOR	
PROYEK	
TOWN HOUSE JALAN JOE JAGAKARSA JAKARTA SELATAN	
KETERANGAN	
REVISI	NO. DOK. DES. TITR.
ARSITEK	
DIKAMBAR	
DIPERIKSA	
DIBETULI	
NO. PROYEK	
NAMA GAMBAR	
TAMPAK KAVLING 6	
SKALA 1 : 75	
AR-039	
SUBKAT	NO. LEMBAR

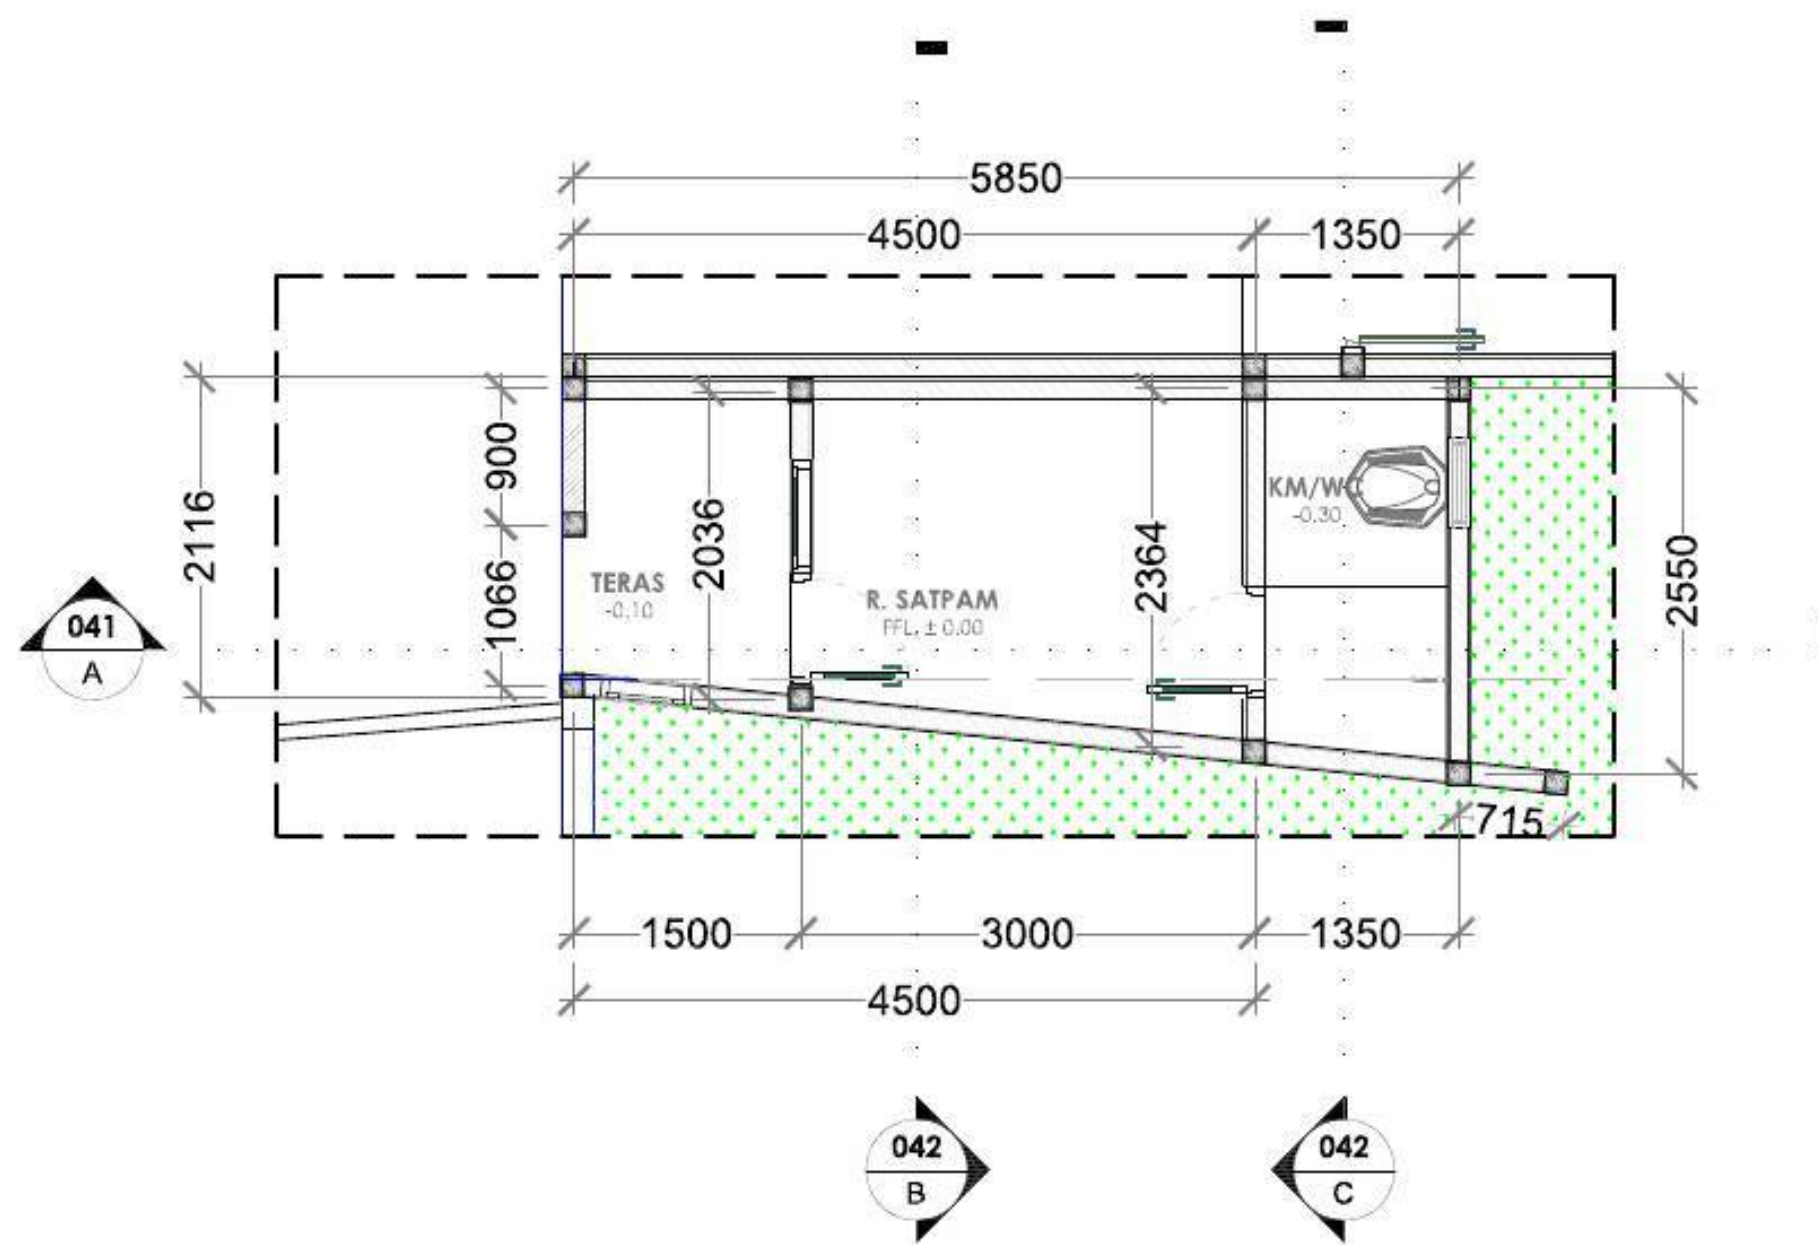


DENAH RG. SATPAM
SKALA 1: 50

KONSULTAN			
KONTRAKTOR			
PROYEK			
TOWN HOUSE JALAN JOE JAGAKARSA JAKARTA SELATAN			
KETERANGAN			
REVISI			
ARSITEK			
DISAMBAH			
DIPERIKSA			
DIBETULU			
NO. PROYEK			
NAMA GAMBAR			
DENAH RG. SATPAM			
SKALA			
1 : 50			
AR-040			
SUBKAT		NO. LEMBAR	

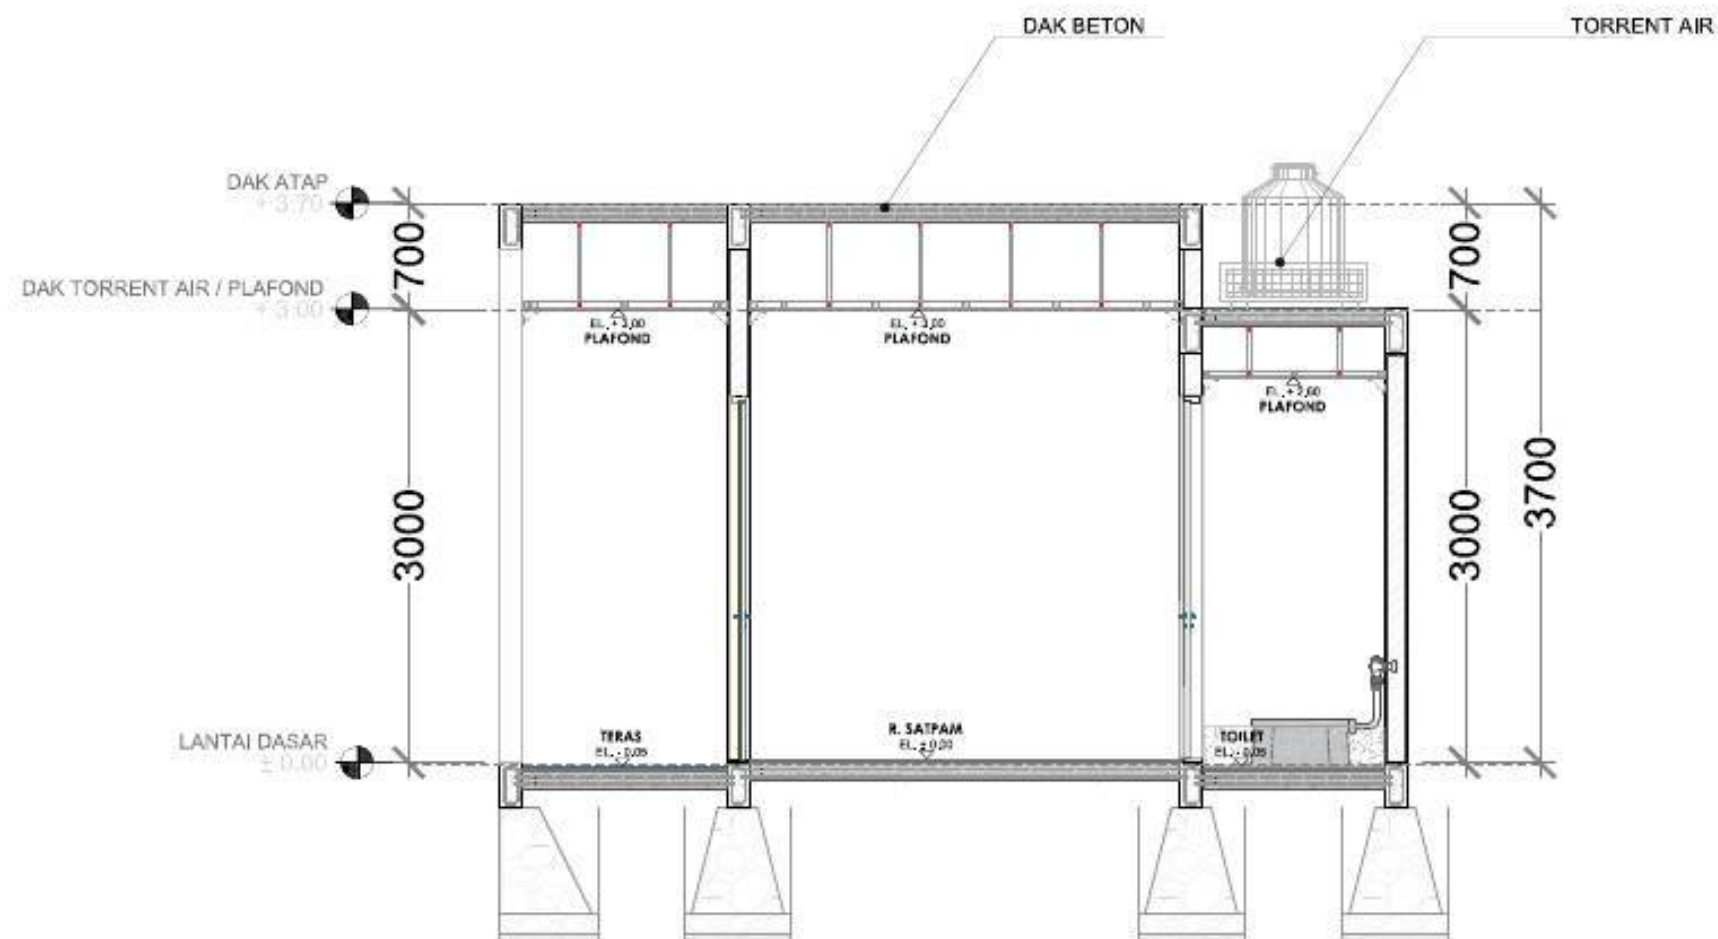


POTONGAN A - A
SKALA 1: 50

KONSULTAN			
KONTRAKTOR			
PROYEK			
TOWN HOUSE JALAN JOE JAGAKARSA JAKARTA SELATAN			
KETERANGAN			
REVISI			
ARSITEK			
DISAMBAH			
DIPERIKSA			
DIBETULI			
NO. PROYEK			
NAMA GAMBAR			
POTONGAN A - A RG. SATPAM			
SKALA			
1 : 50			
AR-041			
SUBKAT		NO. LEMBAR	

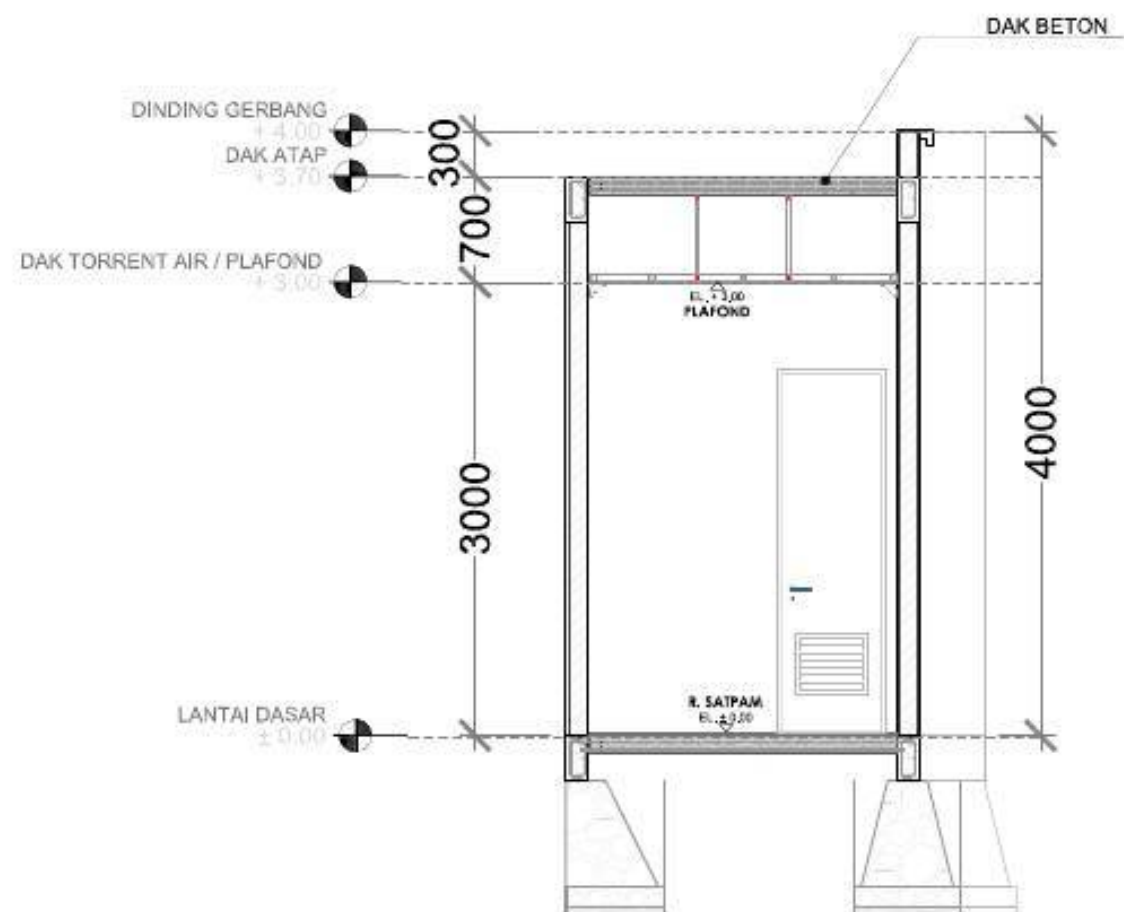

POTONGAN B — B
SKALA 1: 50

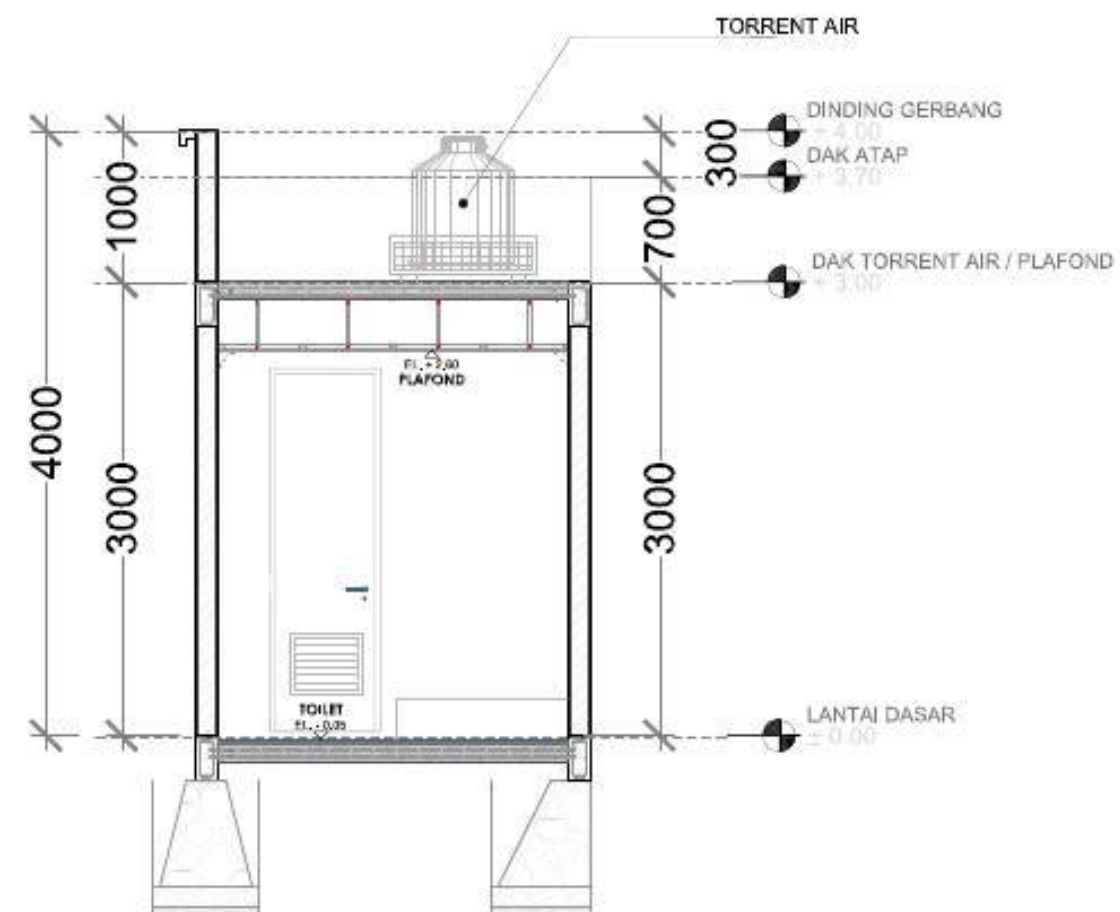

POTONGAN C — C
SKALA 1: 50

KONSULTAN			
KONTRAKTOR			
PROYEK			
TOWN HOUSE JALAN JOE JAGAKARSA JAKARTA SELATAN			
KETERANGAN			
REVISI			
ARSITEK			
DISAMBAH			
DIPERIKSA			
DIBETULI			
NO. PROYEK			
NAMA GAMBAR			
POTONGAN B & C RG. SATPAM			
SKALA			
1 : 50			
AR-042			
SUBKAT		NO. LEMBAR	



PERSPEKTIF
SKALA NTS

KONSULTAN		
KONTRAKTOR		
PROYEK		
TOWN HOUSE JALAN JOE JAGAKARSA JAKARTA SELATAN		
KETERANGAN		
REVISI	TGL. DES. THP.	
ANOTASI		
DIKAMBAR		
DIPERIKSA		
DIBETULKAN		
NO. PROYEK		
NAMA GAMBAR		
PERSPEKTIF		
SKALA NTS		
AR-043		
SUBKAT	NO. LEMBAR	



PERSPEKTIF
SKALA:NTS

KONSULTAN			
KONTRAKTOR			
PROYEK			
TOWN HOUSE JALAN JOE JAGAKARSA JAKARTA SELATAN			
KETERANGAN			
REVISI			
	NO.	REVISI	TH
ARSITEK			
DOKUMENTASI			
DIPERIKSA			
DIBETULI			
NO. PROYEK			
NAMA GAMBAR			
PERSPEKTIF			
SKALA			
NTS			
AR-045			
SUBKAT		NO. LEMBAR	



KONSULTAN			
KONTRAKTOR			
PROYEK			
TOWN HOUSE JALAN JOE JAGAKARSA JAKARTA SELATAN			
KETERANGAN			
REVISI	TGL. DES. THP.		
ARSITEK			
DIKAMBAR			
DIPERIKSA			
DIBETULU			
NO. PROYEK			
-			
NAMA GAMBAR			
PERSPEKTIF			
SKALA			
NTS			
AR-046			
SUBKAT		NO. LEMBAR	



PERSPEKTIF
SKALA:NTS

KONSULTAN			
KONTRAKTOR			
PROYEK			
TOWN HOUSE JALAN JOE JAGAKARSA JAKARTA SELATAN			
KETERANGAN			
REVISI	NO.	DATE	BY
ARSITEK			
DOKUMENTASI			
DIPERIKSA			
DIBETULI			
NO. PROYEK			
NAMA GAMBAR			
PERSPEKTIF			
SKALA: NTS			
AR-047			
SUBKAT		NO. LEMBAR	



PERSPEKTIF
SKALA: NTS

KONSULTAN			
KONTRAKTOR			
PROYEK			
TOWN HOUSE JALAN JOE JAGAKARSA JAKARTA SELATAN			
KETERANGAN			
REVISI			
	NO.	DESKRIPSI	STATUS
ARSITEK			
DOKUMENTASI			
DIPERIKSA			
DIBETULKAN			
NO. PROYEK			
NAMA GAMBAR			
PERSPEKTIF			
SKALA			
NTS			
AR-048			
SUBKAT		NO. LEMBAR	



PERSPEKTIF
SKALA:NTS

KONSULTAN			
KONTRAKTOR			
PROYEK TOWN HOUSE JALAN JOE JAGAKARSA JAKARTA SELATAN			
KETERANGAN			
REVISI		TGL. DES. THA	
ANOTASI			
DIBANGUN			
DIPERIKSA			
DIBETULKAN			
NO. PROYEK			
NAMA GAMBAR			
PERSPEKTIF			
SKALA		NTS	
AR-049			
SUBKAT	NO. LEMBAR		



PERSPEKTIF
SKALA NTS

KONSULTAN	
KONTRAKTOR	
PROYEK	
TOWN HOUSE JALAN JOE JAGAKARSA JAKARTA SELATAN	
KETERANGAN	
REVISI	NO. DOK. DES. TITIK
ARSITEK	
DIKASABAR	
DIPERIKSA	
DIBETULUJ	
NO. PROYEK	
NAMA GAMBAR	
PERSPEKTIF	
SKALA	NTS
AR-050	
SUBKAT	NO. LEMBAR