


DOKUMEN GAMBAR PROPOSAL




PEMBANGUNAN RUMAH KAVLING JALAN JOE
JAGAKARSA
JAKARTA SELATAN

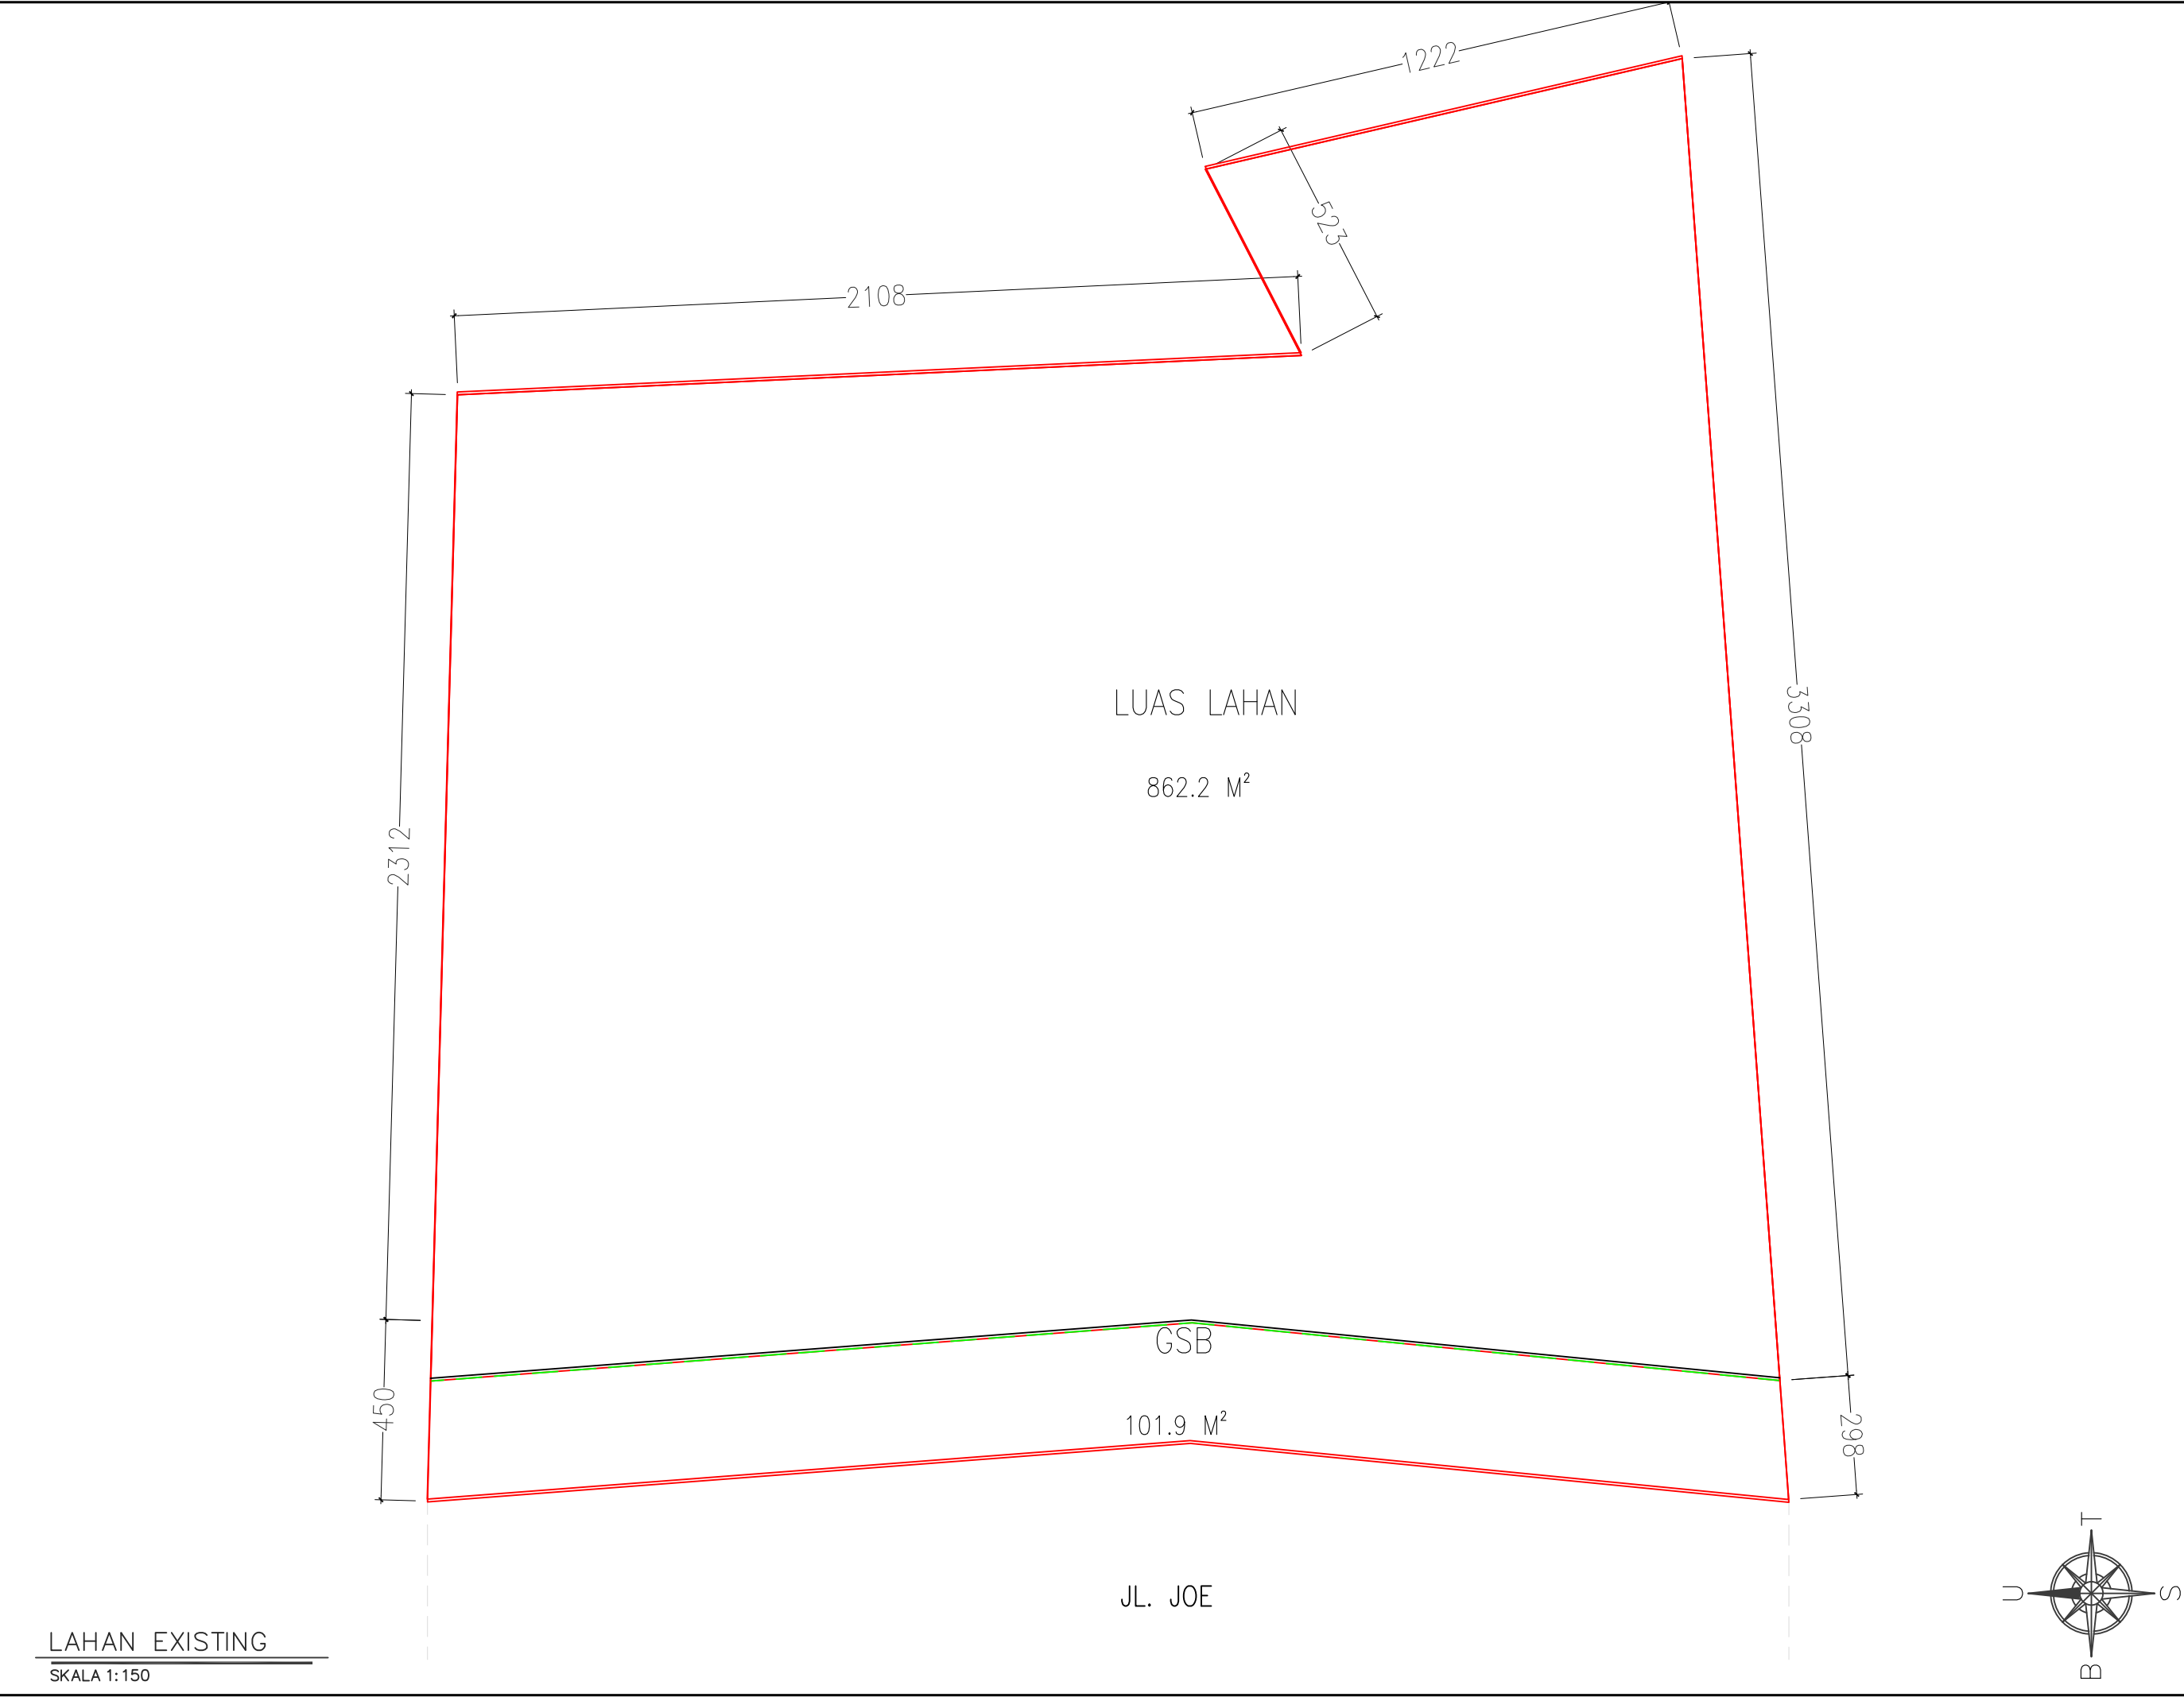


LAHAN EXISTING


SKALA 1:150

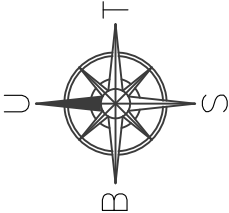


KONSULTAN			
KONTRAKTOR			
PROYEK			
TOWN HOUSE JALAN JOE JAGAKARSA JAKARTA SELATAN			
KETERANGAN			
REVISI		TGL	BLN
ARSITEK			
DIGAMBAR			
DIPERIKSA			
DISETUJUI			
NO. PROYEK			
-			
NAMA GAMBAR			
LAHAN EXISTING			
SKALA			
1 : 150			
AR-001			
SUBKAT	NO. LEMBAR		

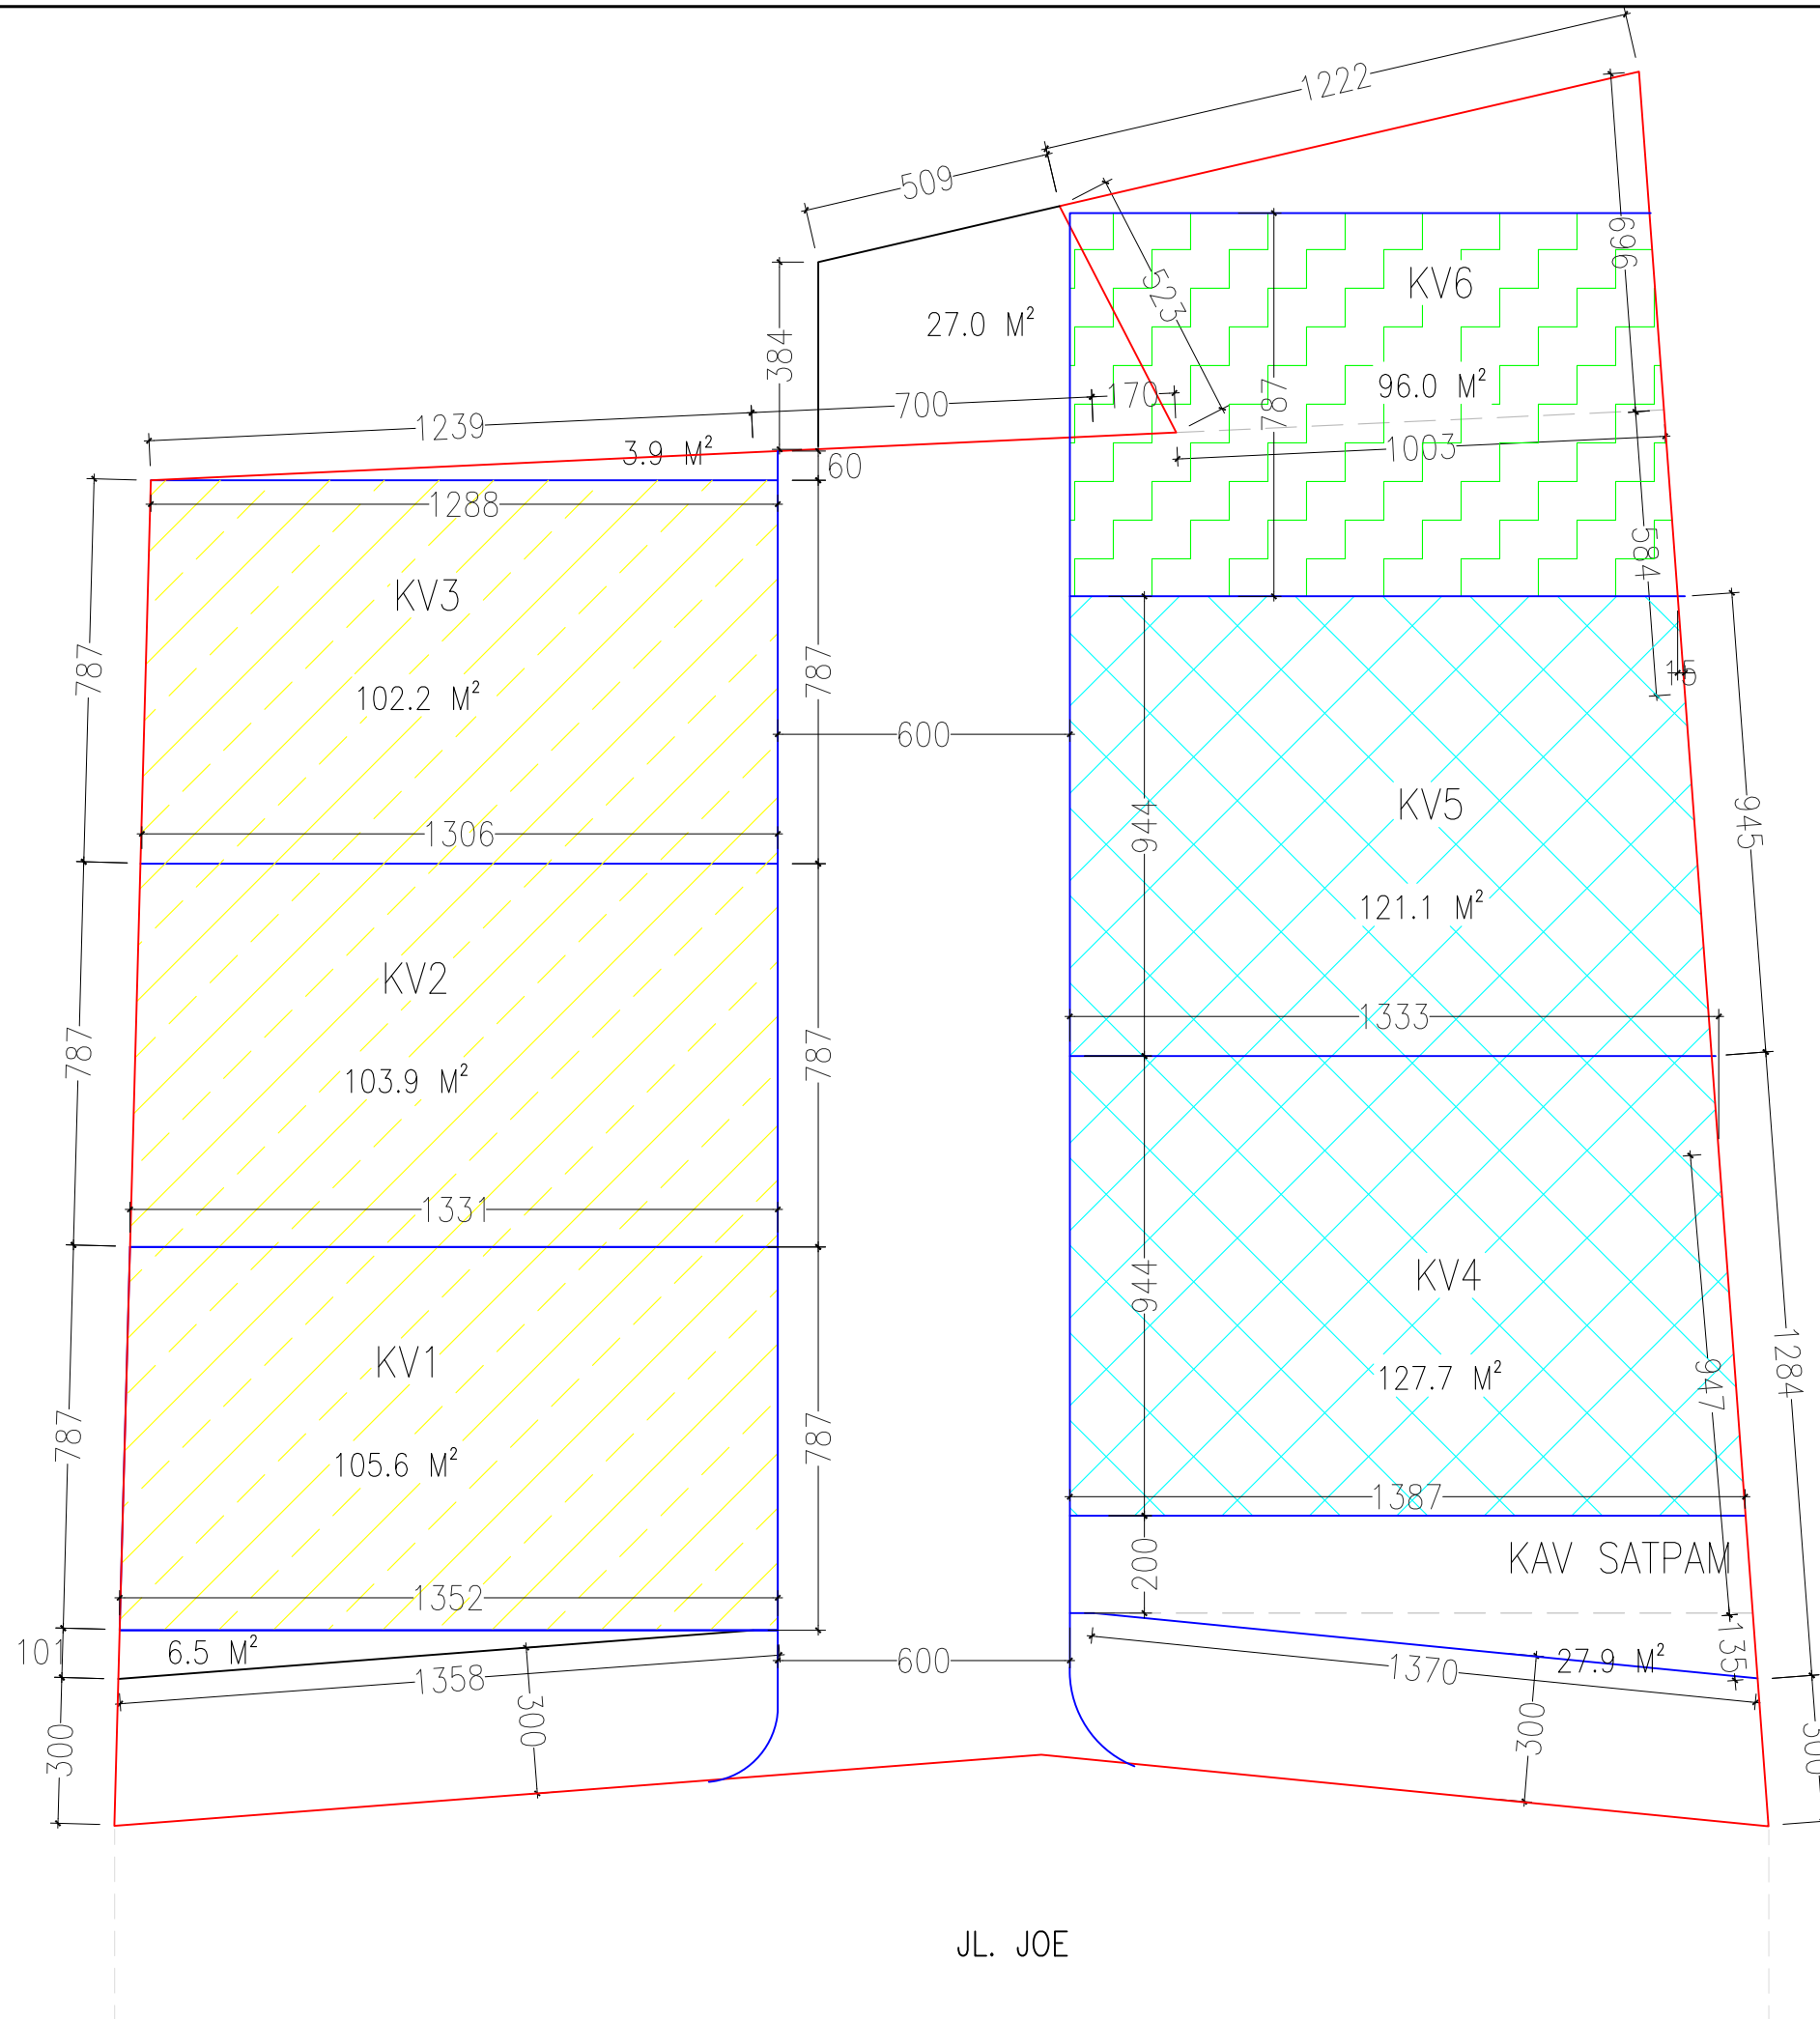


SITE PLAN
SKALA 1:150

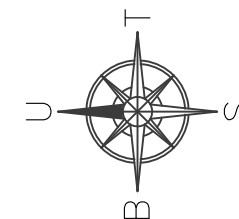

KONSULTAN			
KONTRAKTOR			
PROYEK			
TOWN HOUSE JALAN JOE JAGAKARSA JAKARTA SELATAN			
KETERANGAN			
REVISI		TGL	BLN
ARSITEK			
DIGAMBAR			
DIPERIKSA			
DISETUJUI			
NO. PROYEK		-	
NAMA GAMBAR		SITE PLAN	
SKALA		1 : 150	
SUBKAT		AR-002	
NO. LEMBAR			

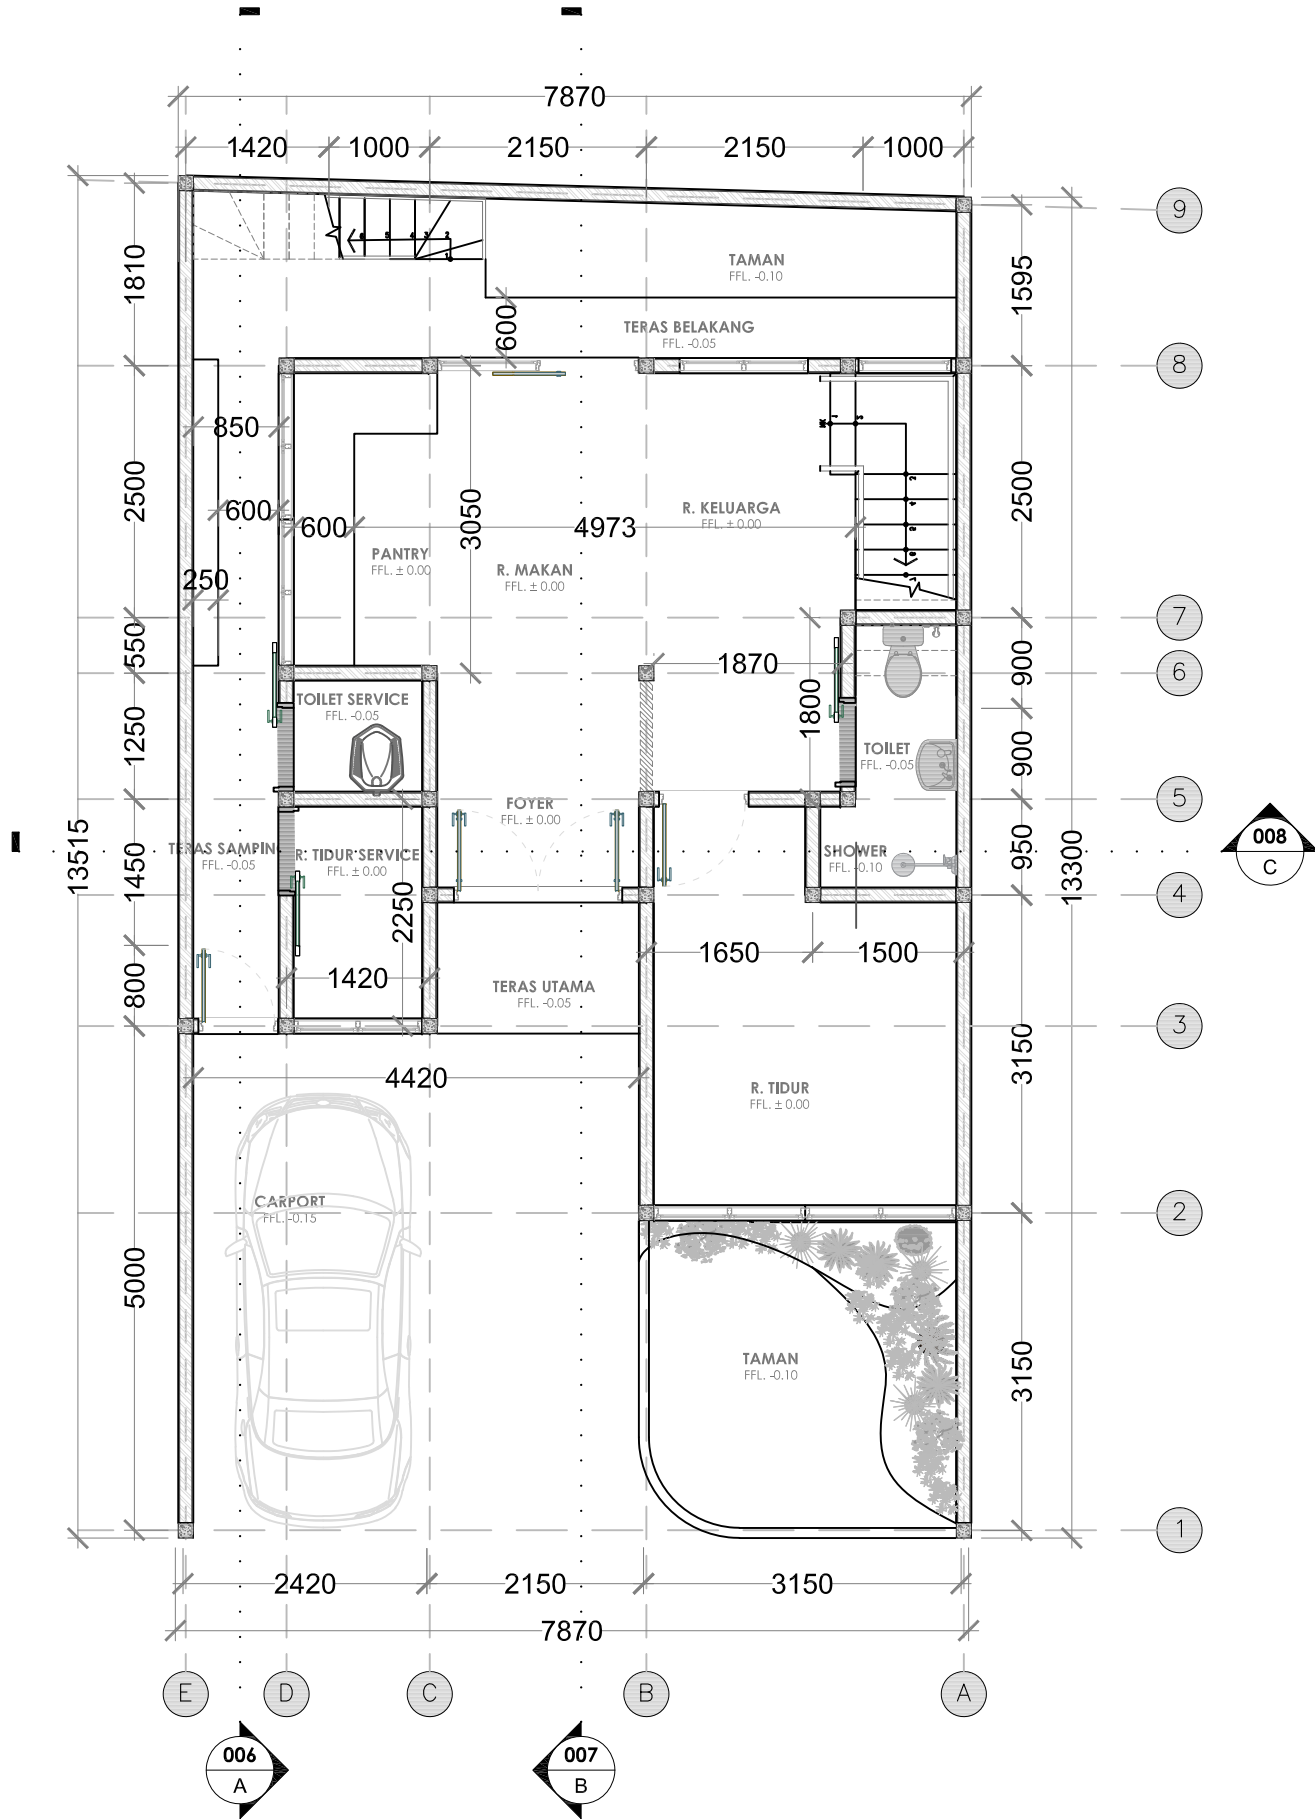

DENAH LANTAI DASAR
SKALA 1: 75

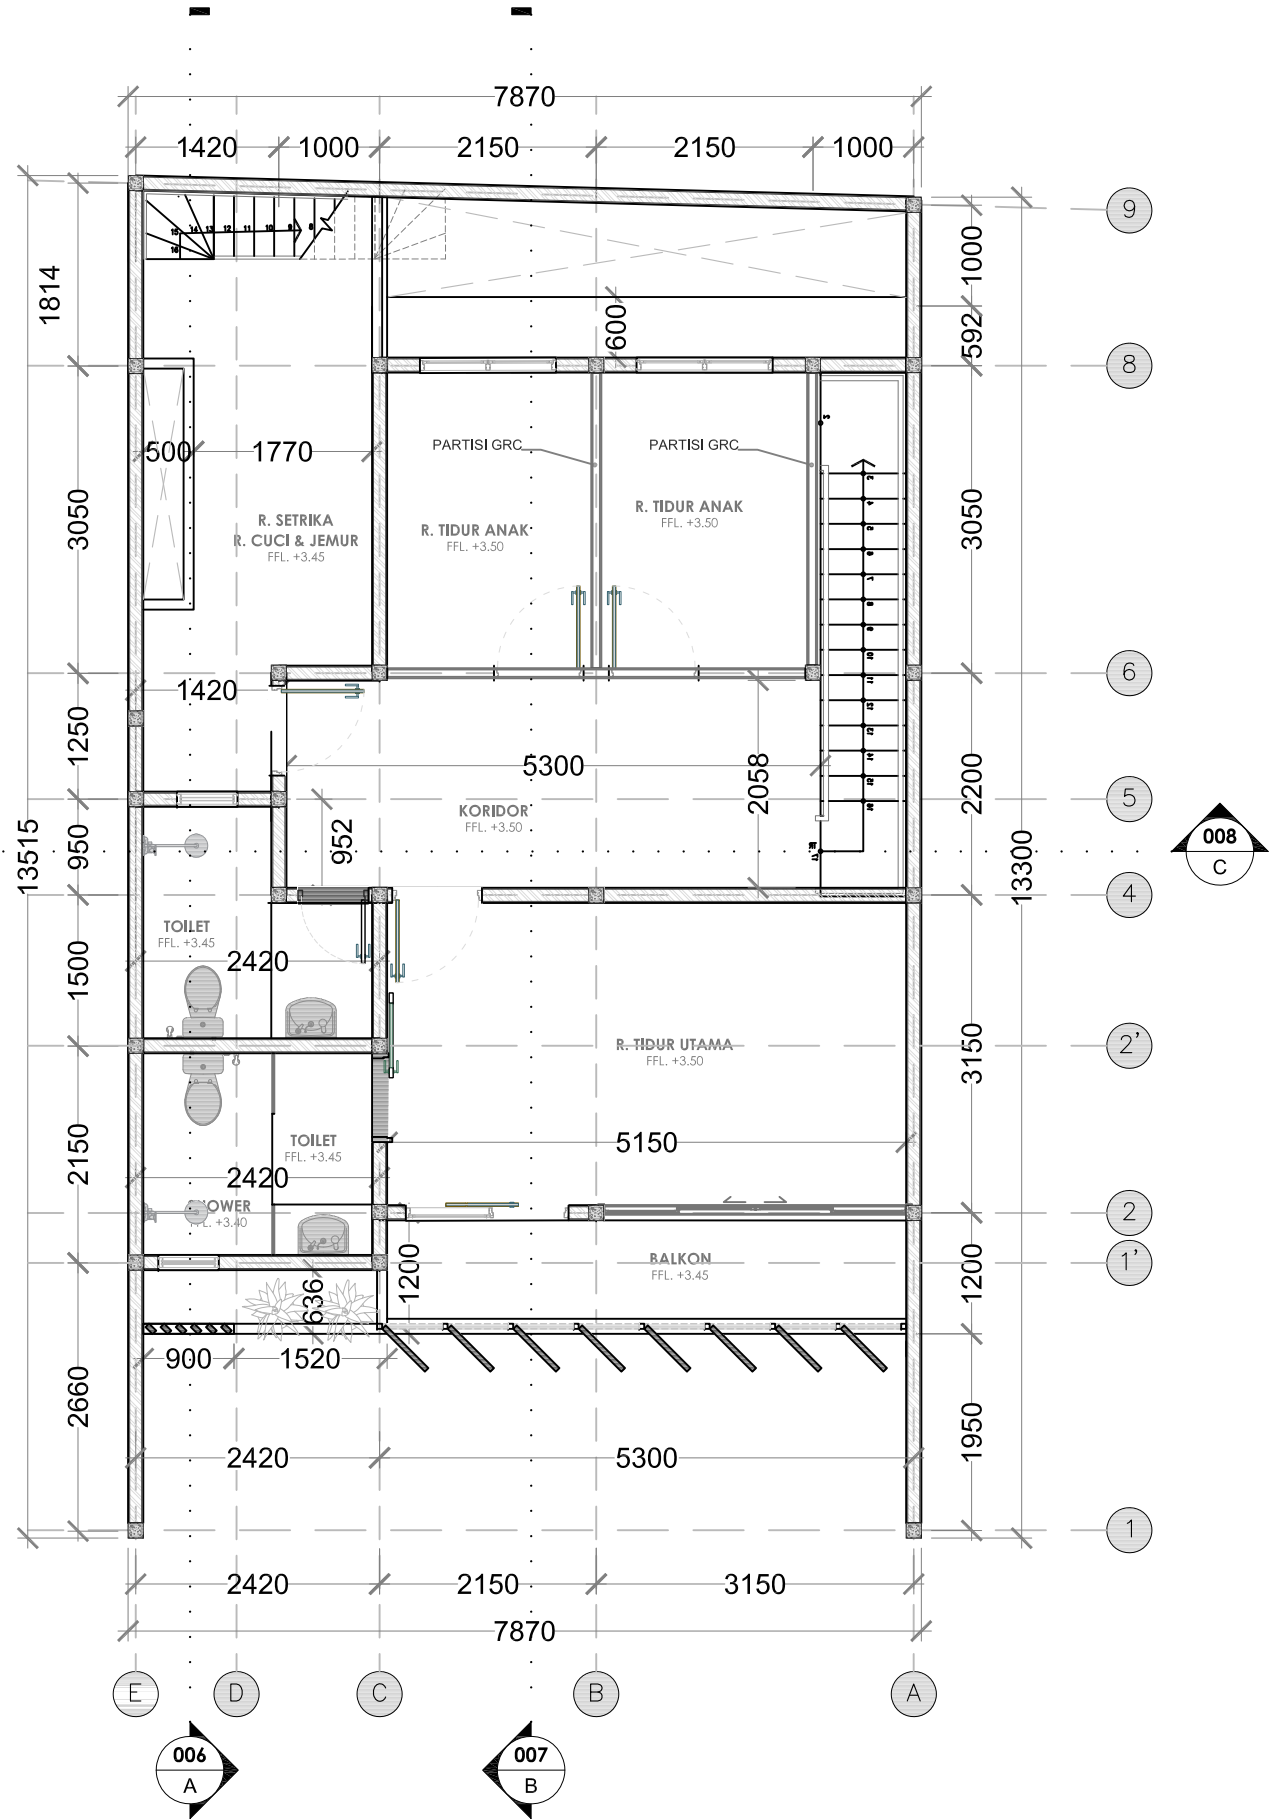

DENAH LANTAI ATAS
SKALA 1: 75


KONSULTAN			
KONTRAKTOR			
PROYEK			
TOWN HOUSE JALAN JOE JAGAKARSA JAKARTA SELATAN			
KETERANGAN			
REVISI			
ARSITEK			
DIGAMBAR			
DIPERIKSA			
DISETUJUI			
NO. PROYEK			
NAMA GAMBAR			
DENAH KAVLING 1			
SKALA			
1 : 75			
AR-004			
SUBKAT			
NO. LEMBAR			



NO. LEMBAR

POTONGAN A - A

SKALA 1: 75

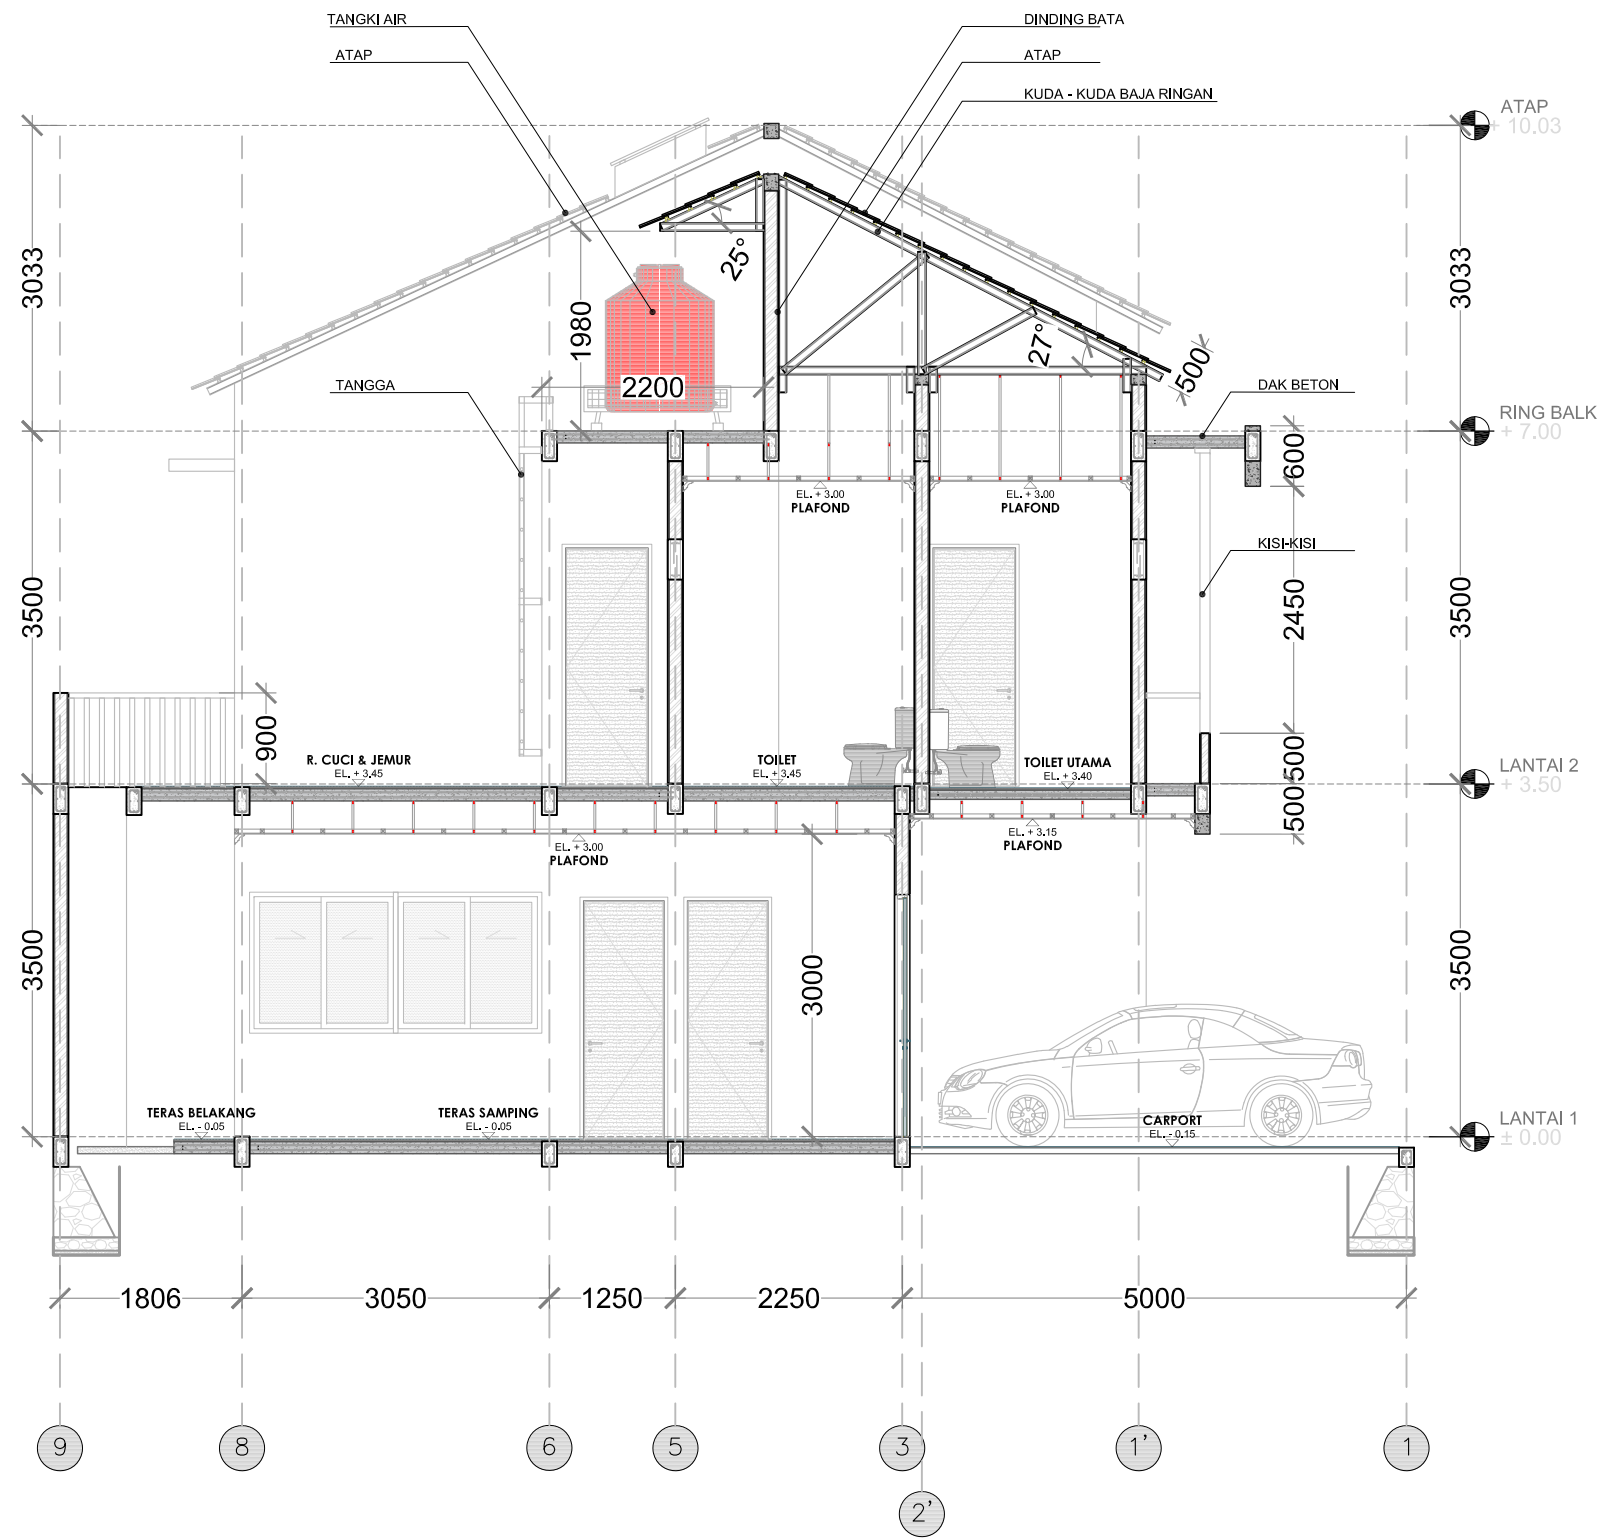

KONSULTAN

KONTRAKTOR

PROYEK

TOWN HOUSE
JALAN JOE
JAGAKARSA
JAKARTA SELATAN

KETERANGAN

REVISI

ARSITEK

DIGAMBAR

DIPERIKSA

DISETUJUI

NO. PROYEK

NAMA GAMBAR

POTONGAN A - A
KAVLING 1

SKALA

1 : 75


AR-006

SUBKAT

NO. LEMBAR

POTONGAN B - B

SKALA 1: 75

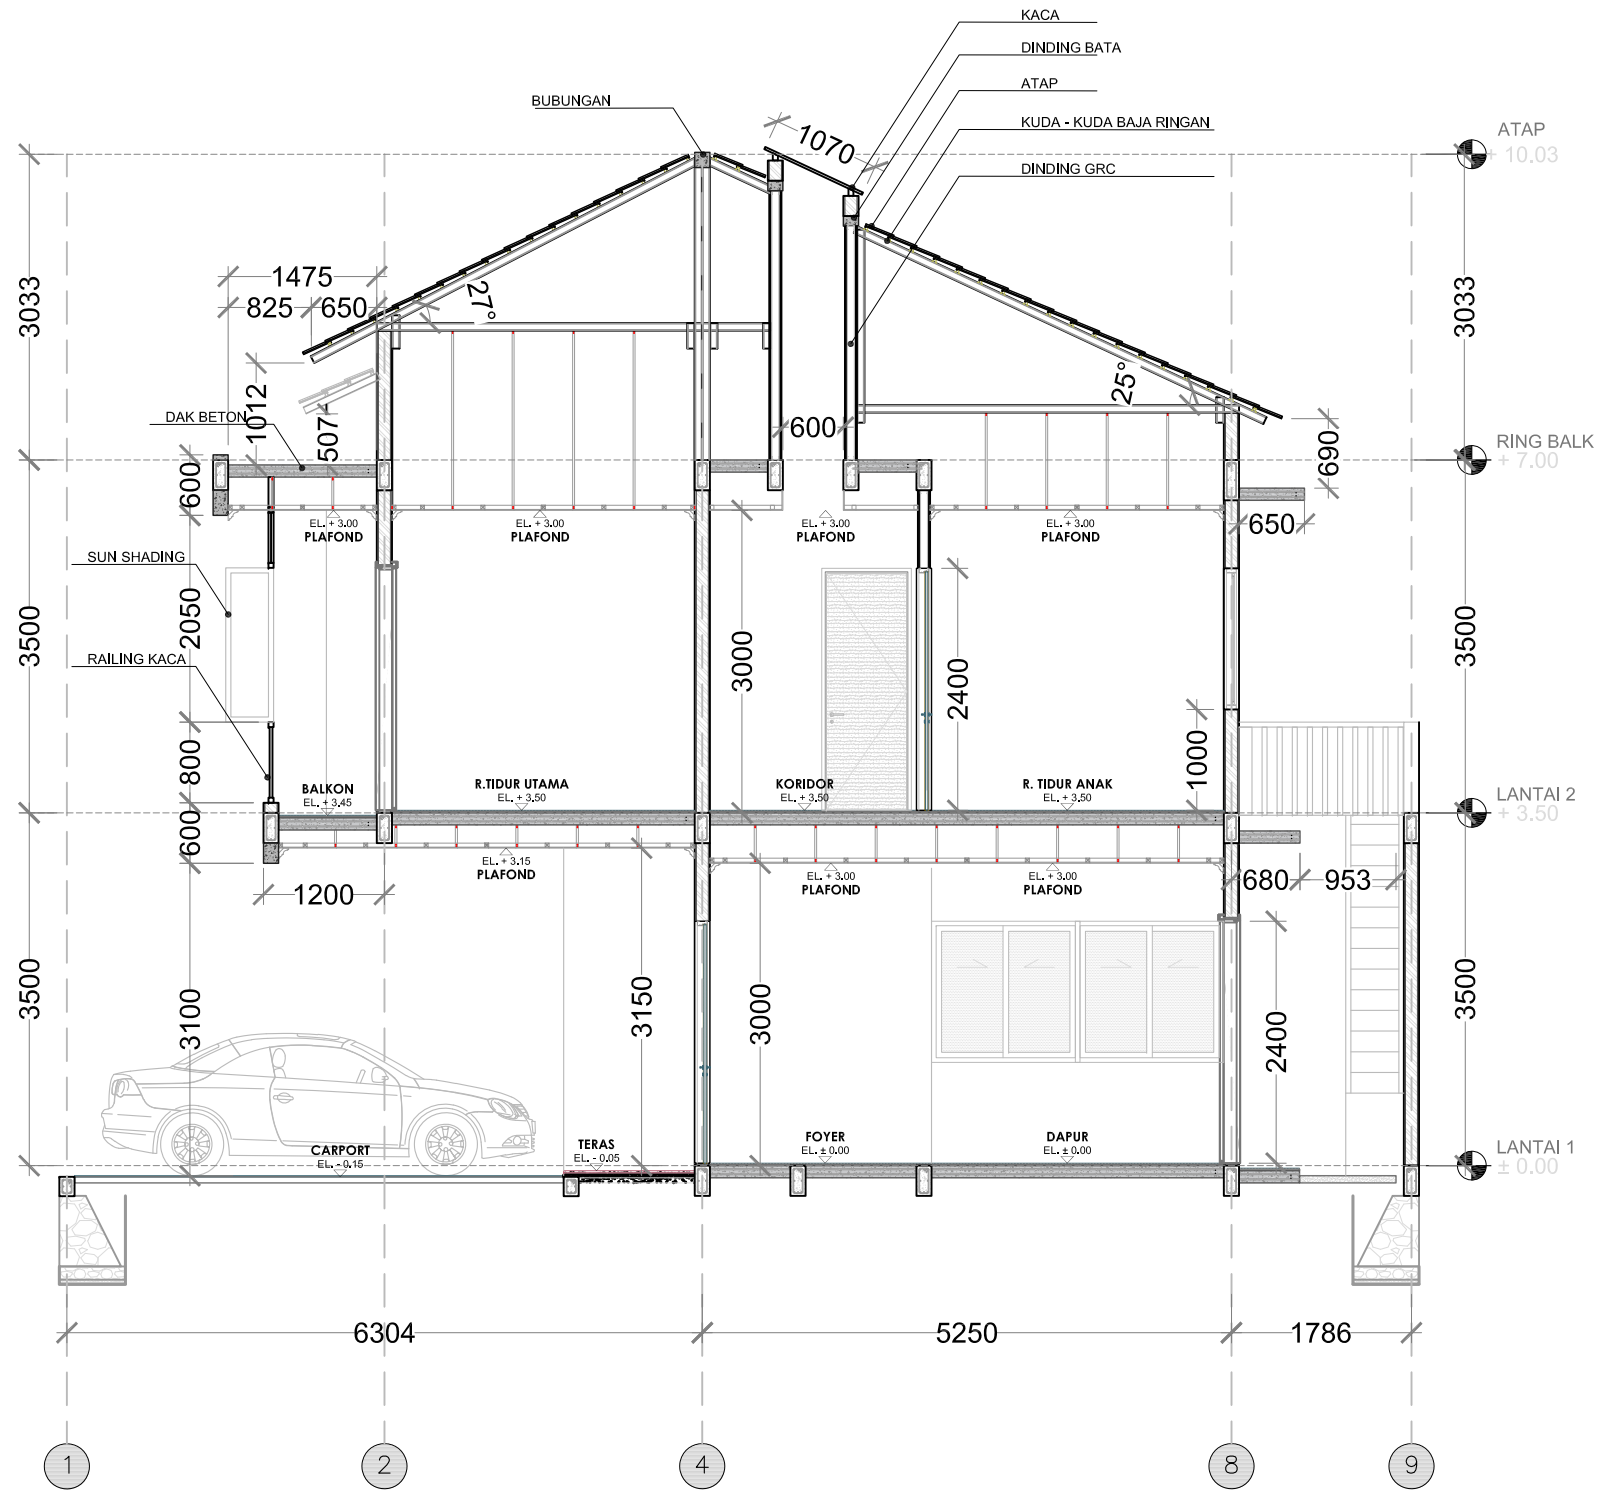

KONSULTAN

KONTRAKTOR

PROYEK

TOWN HOUSE
JALAN JOE
JAGAKARSA
JAKARTA SELATAN

KETERANGAN

REVISI

ARSITEK

DIGAMBAR

DIPERIKSA

DISETUJUI

NO. PROYEK

NAMA GAMBAR

POTONGAN B - B
KAVLING 1


SKALA

1 : 75

AR-007

SUBKAT

NO. LEMBAR

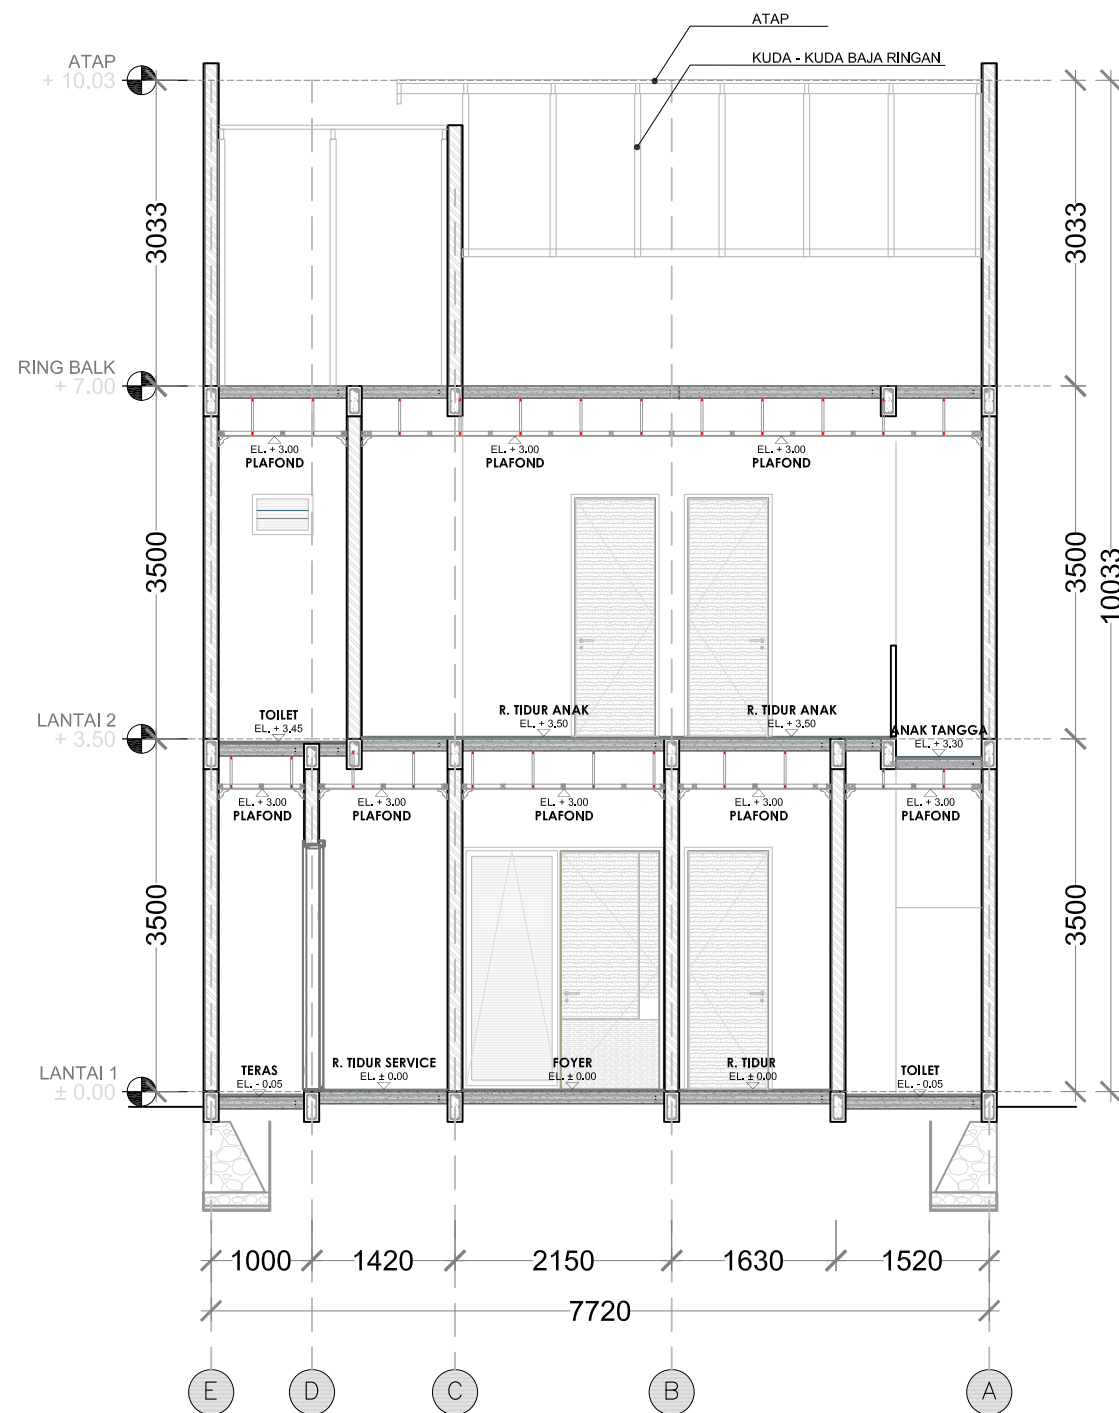

POTONGAN C - C
SKALA 1: 75

KONSULTAN

KONTRAKTOR

PROYEK

TOWN HOUSE
JALAN JOE
JAGAKARSA
JAKARTA SELATAN

KETERANGAN

REVISI

	TGL	BLN	THN

ARSITEK

DIGAMBAR

DIPERIKSA

DISETUJUI

NO. PROYEK

-

NAMA GAMBAR

POTONGAN C - C
KAVLING 1


SKALA

1 : 75

AR-008


SUBKAT

NO. LEMBAR

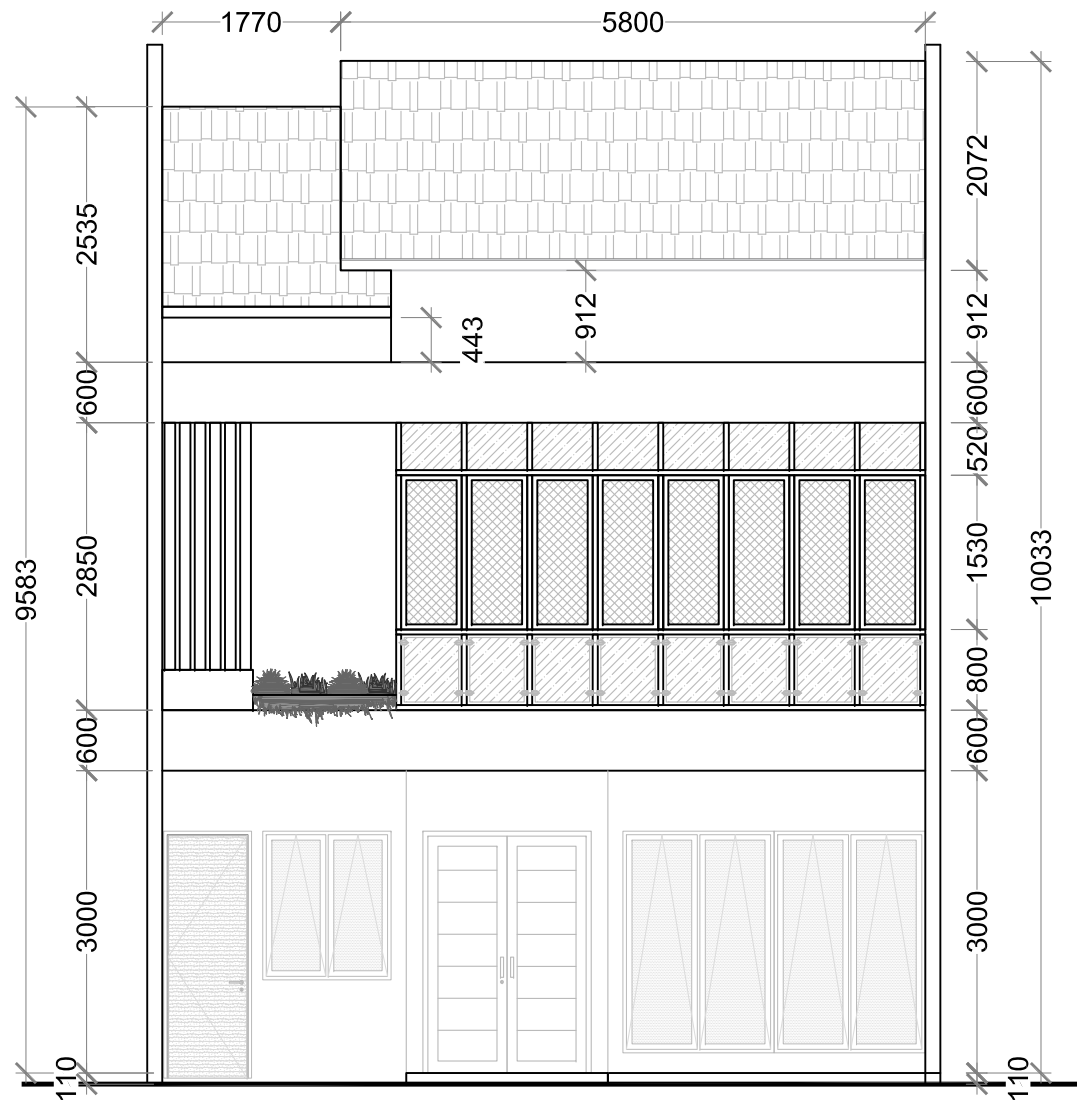

TAMPAK DEPAN

SKALA 1: 75

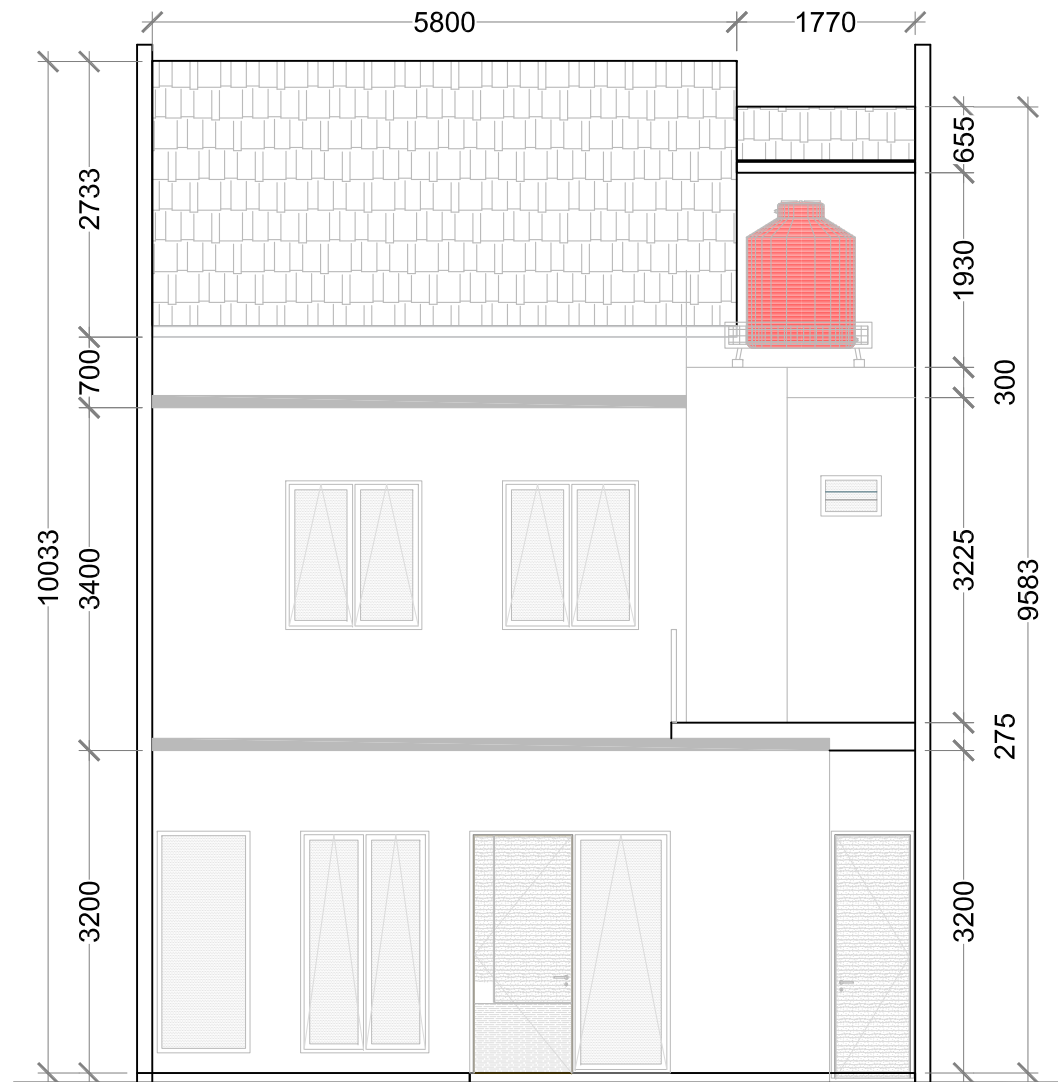

TAMPAK BELAKANG

SKALA 1: 75


KONSULTAN				
KONTRAKTOR				
PROYEK				
TOWN HOUSE JALAN JOE JAGAKARSA JAKARTA SELATAN				
KETERANGAN				
REVISI				
		TGL	BLN	THN
ARSITEK				
DIGAMBAR				
DIPERIKSA				
DISETUJUI				
NO. PROYEK				
-				
NAMA GAMBAR				
TAMPAK KAVLING 1				
SKALA				
1 : 75				
AR-009				
SUBKAT		NO. LEMBAR		



KONSULTAN				
KONTRAKTOR				
PROYEK				
TOWN HOUSE JALAN JOE JAGAKARSA JAKARTA SELATAN				
KETERANGAN				
REVISI		TGL	BLN	THN
ARSITEK				
DIGAMBAR				
DIPERIKSA				
DISETUJUI				
NO. PROYEK				
-				
NAMA GAMBAR				
DENAH KAVLING 2				
SKALA				
1 : 75				
AR		- 010		
SUBKAT		NO. LEMBAR		



NO. LEMBAR

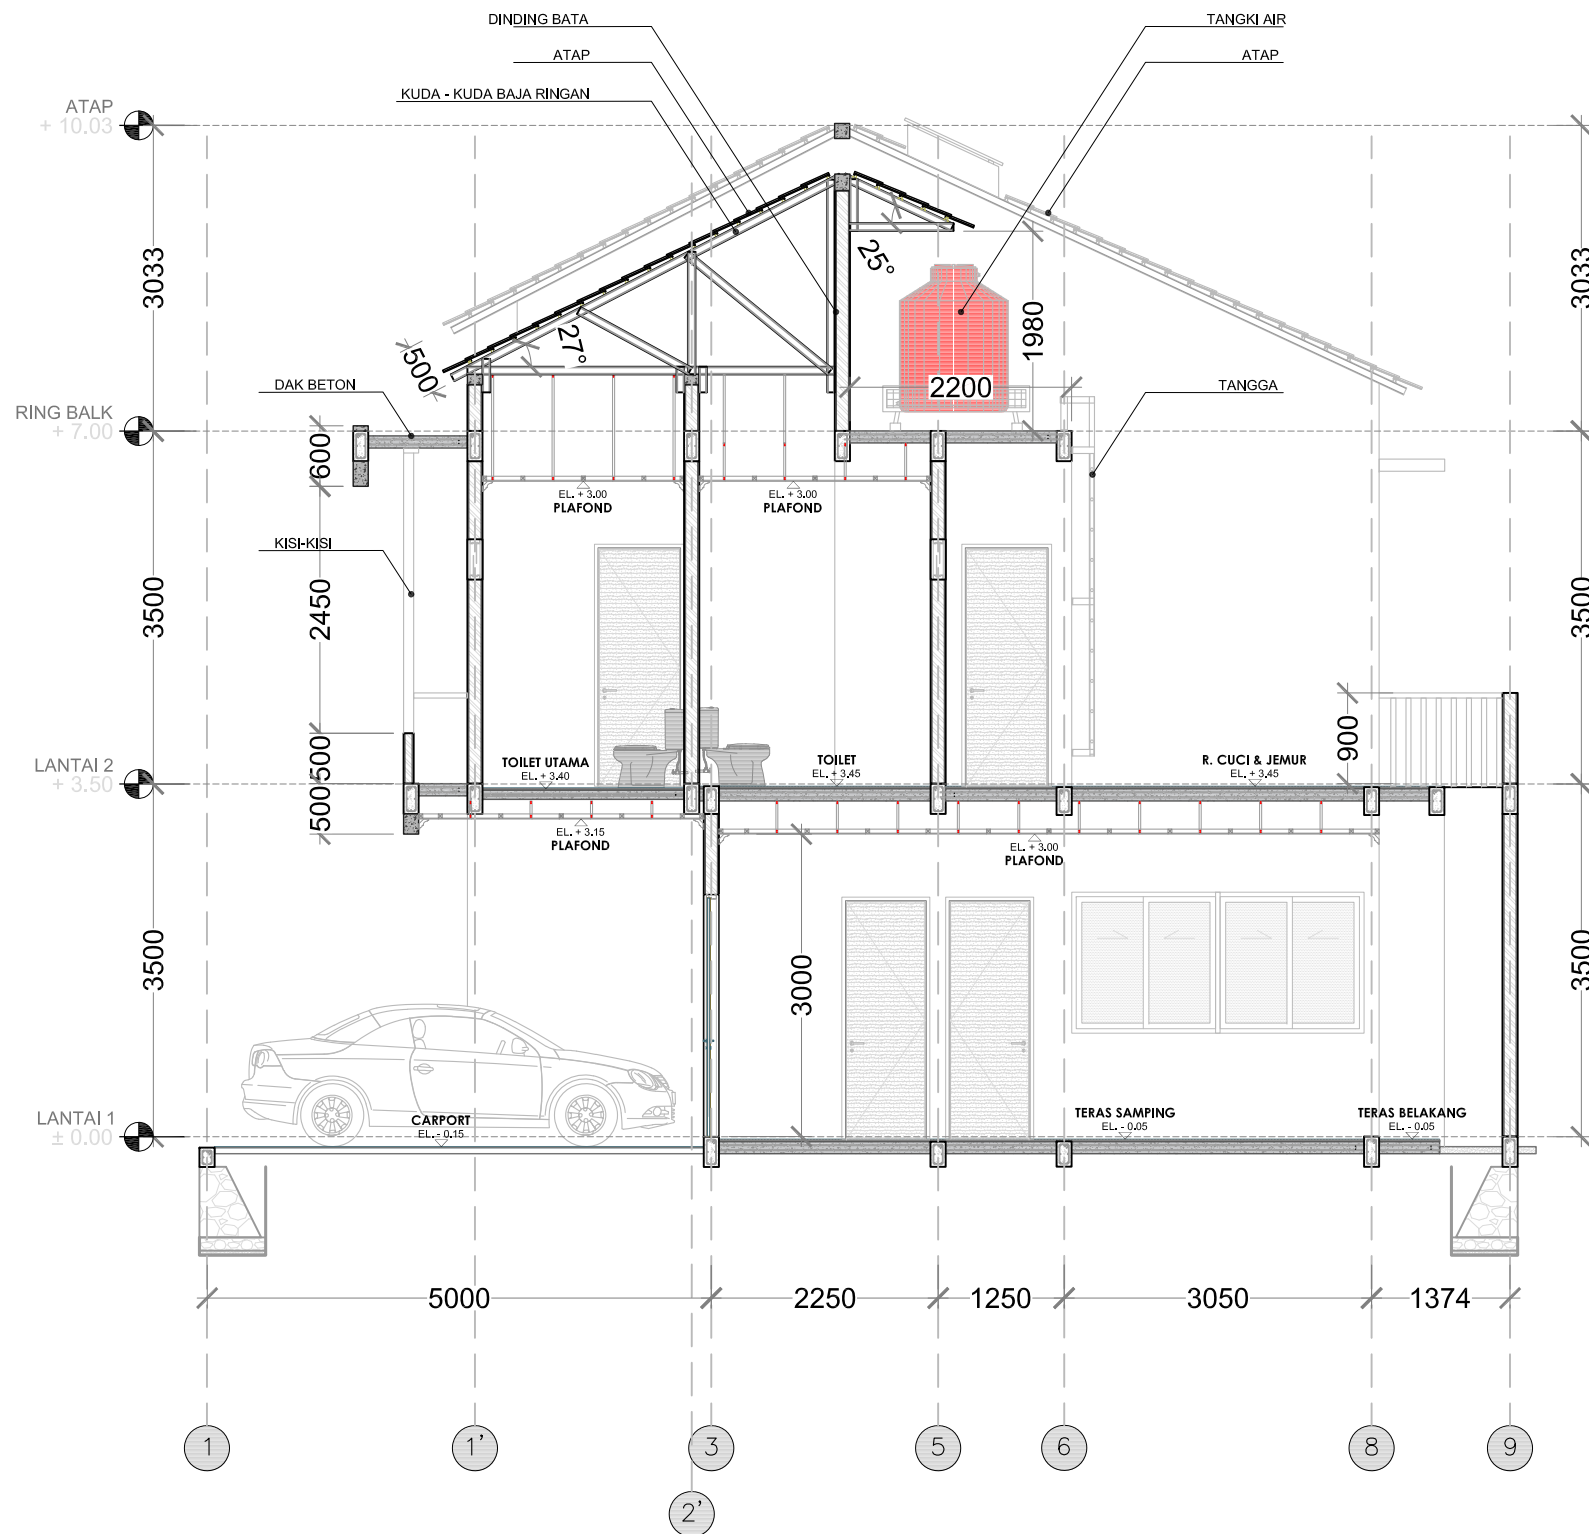


POTONGAN A - A
SKALA 1: 75

KONSULTAN			
KONTRAKTOR			
PROYEK			
TOWN HOUSE JALAN JOE JAGAKARSA JAKARTA SELATAN			
KETERANGAN			
REVISI			
		TGL	BLN
		THN	
ARSITEK			
DIGAMBAR			
DIPERIKSA			
DISETUJUI			
NO. PROYEK			
-			
NAMA GAMBAR			
POTONGAN A - A KAVLING 2			
SKALA			
1 : 75			
AR-012			
SUBKAT		NO. LEMBAR	

POTONGAN B - B

SKALA 1: 75

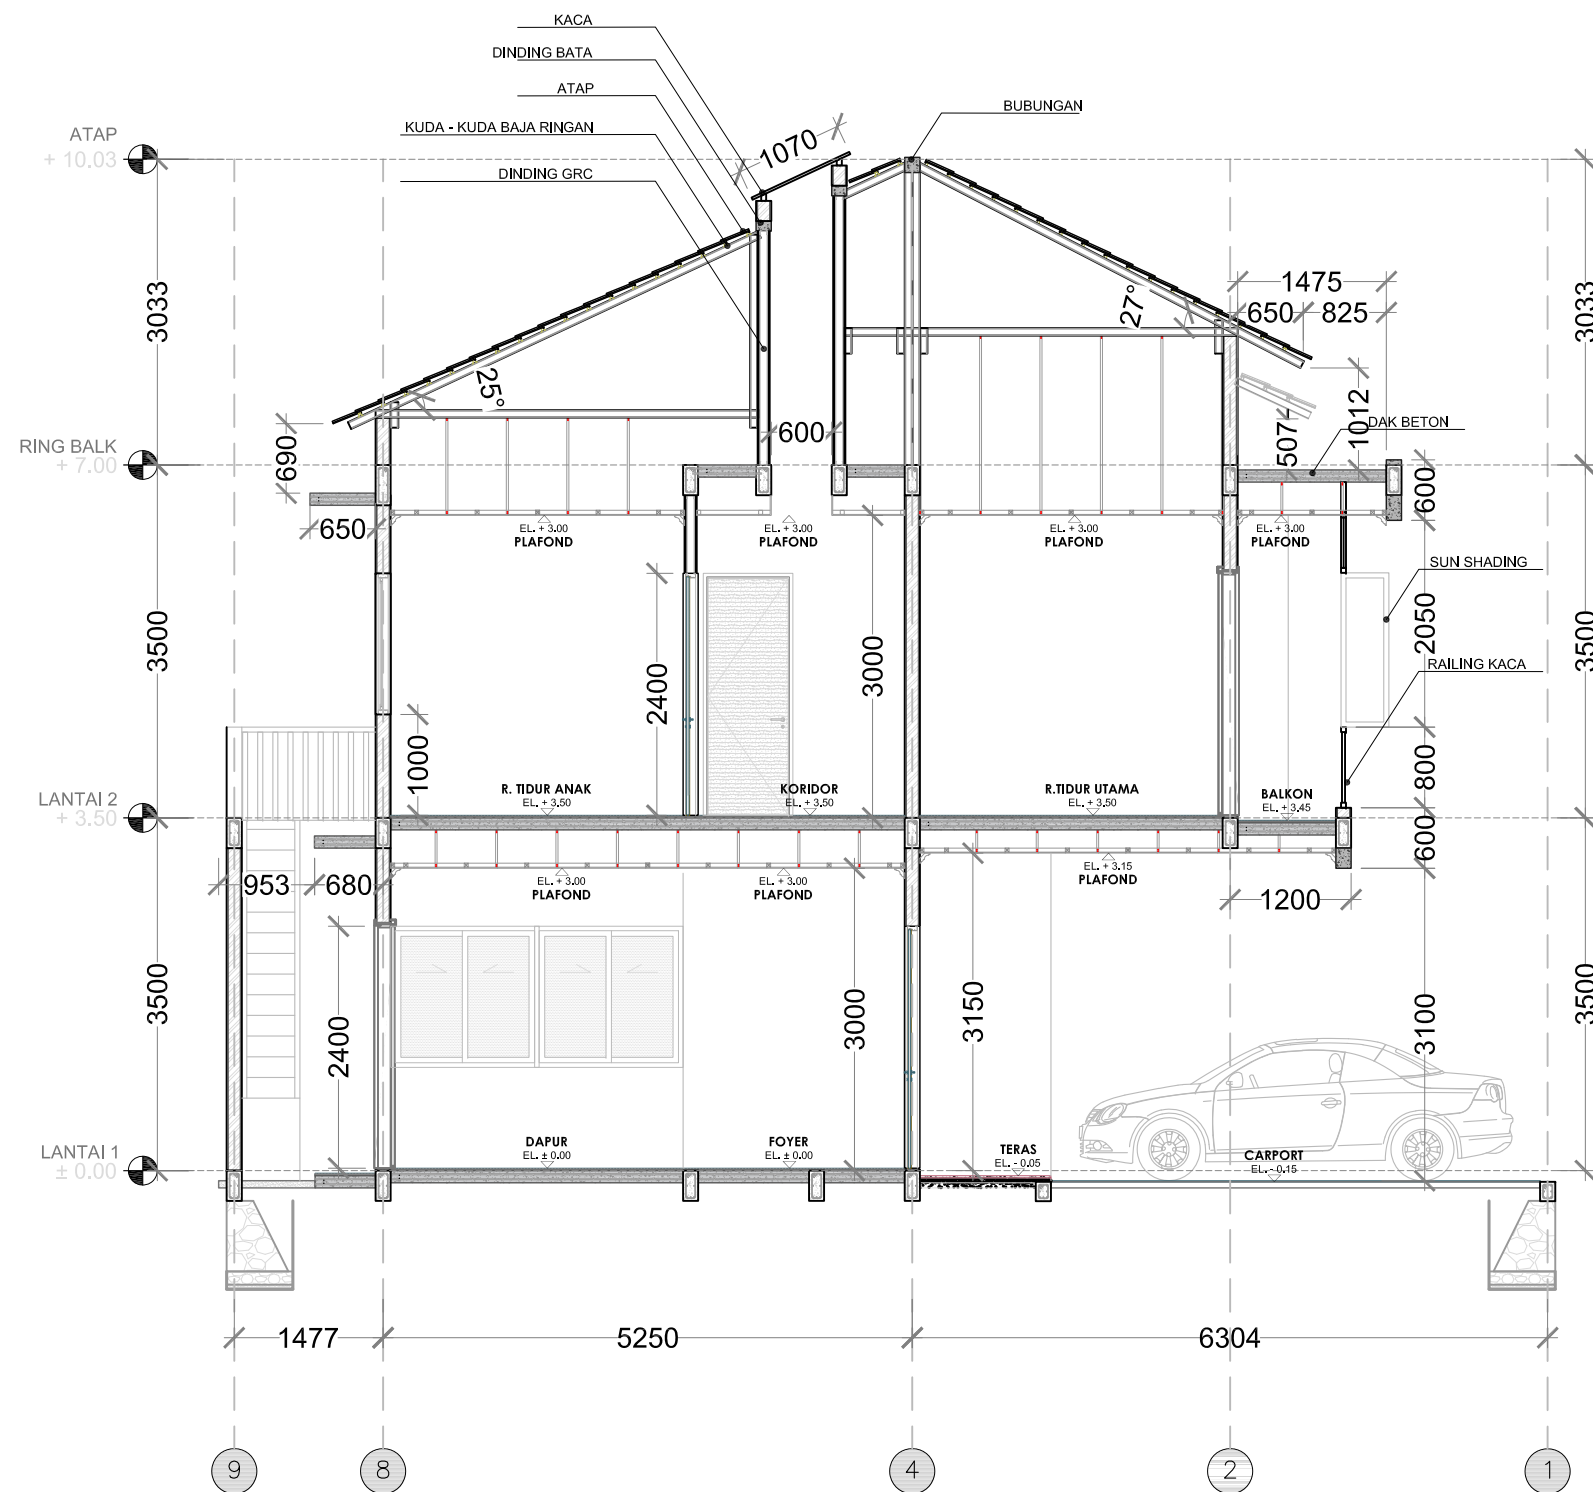

KONSULTAN

KONTRAKTOR

PROYEK

TOWN HOUSE
JALAN JOE
JAGAKARSA
JAKARTA SELATAN

KETERANGAN

REVISI

ARSITEK

DIGAMBAR

DIPERIKSA

DISETUJUI

NO. PROYEK

NAMA GAMBAR

POTONGAN B - B
KAVLING 2

SKALA

1 : 75


AR-013

SUBKAT

NO. LEMBAR

POTONGAN C - C

SKALA 1: 75

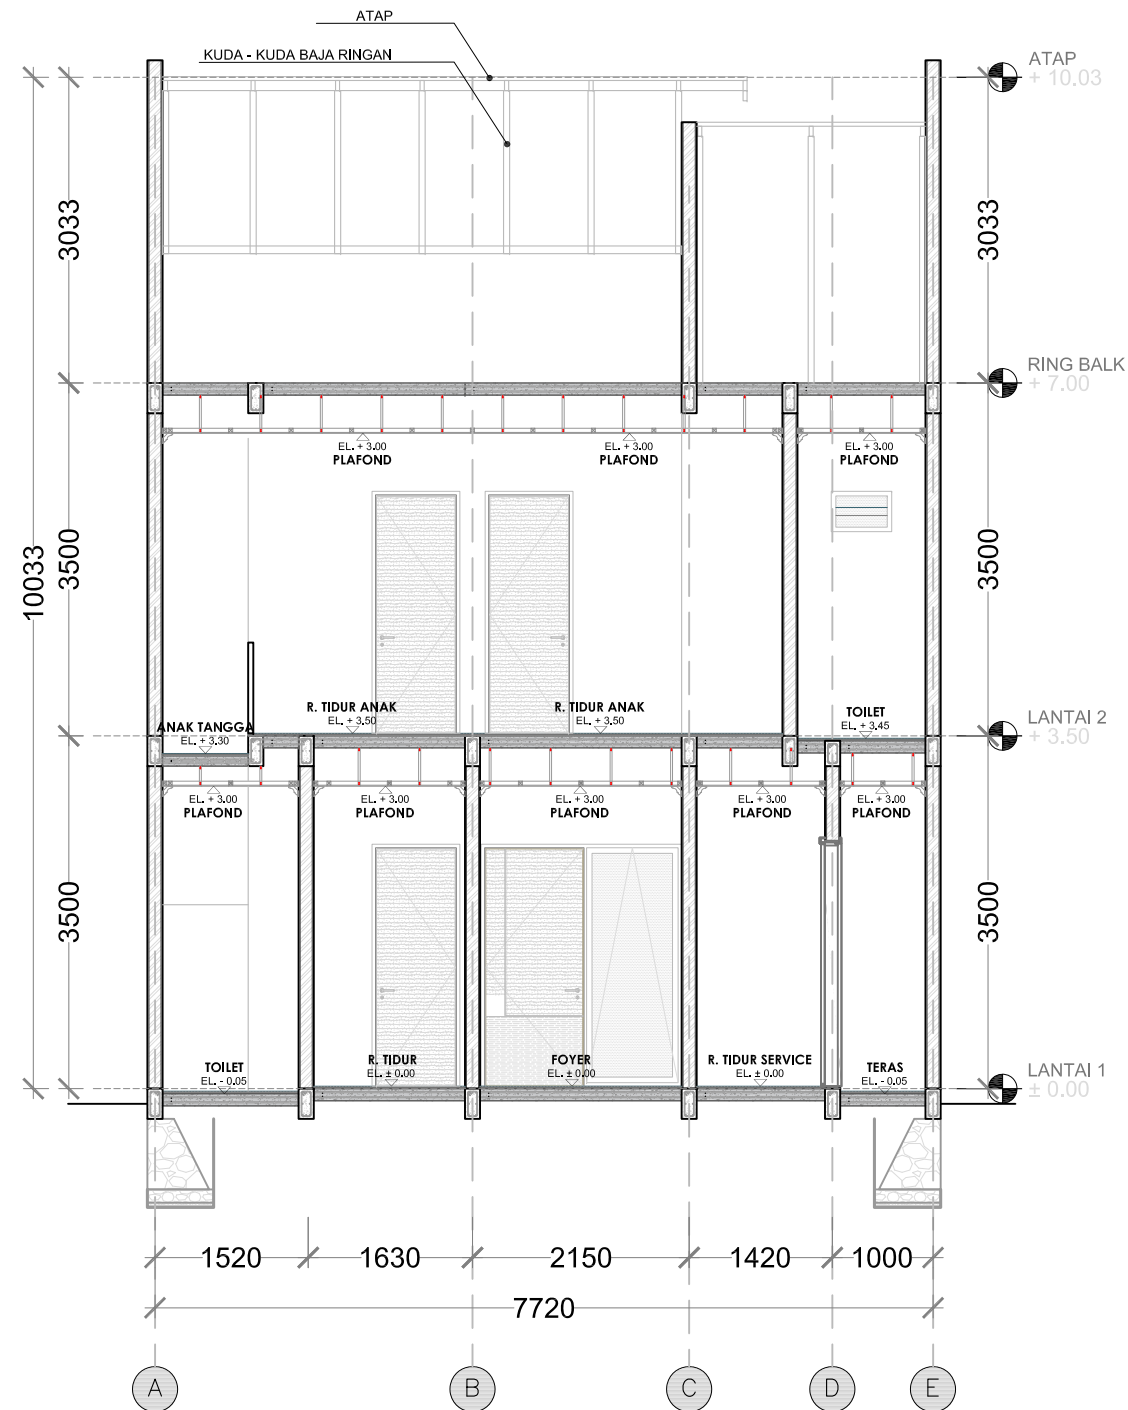

KONSULTAN

KONTRAKTOR

PROYEK

TOWN HOUSE
JALAN JOE
JAGAKARSA
JAKARTA SELATAN

KETERANGAN

REVISI

ARSITEK

DIGAMBAR

DIPERIKSA

DISETUJUI

NO. PROYEK

NAMA GAMBAR

POTONGAN C - C
KAVLING 2


SKALA

1 : 75

AR-014


SUBKAT

NO. LEMBAR

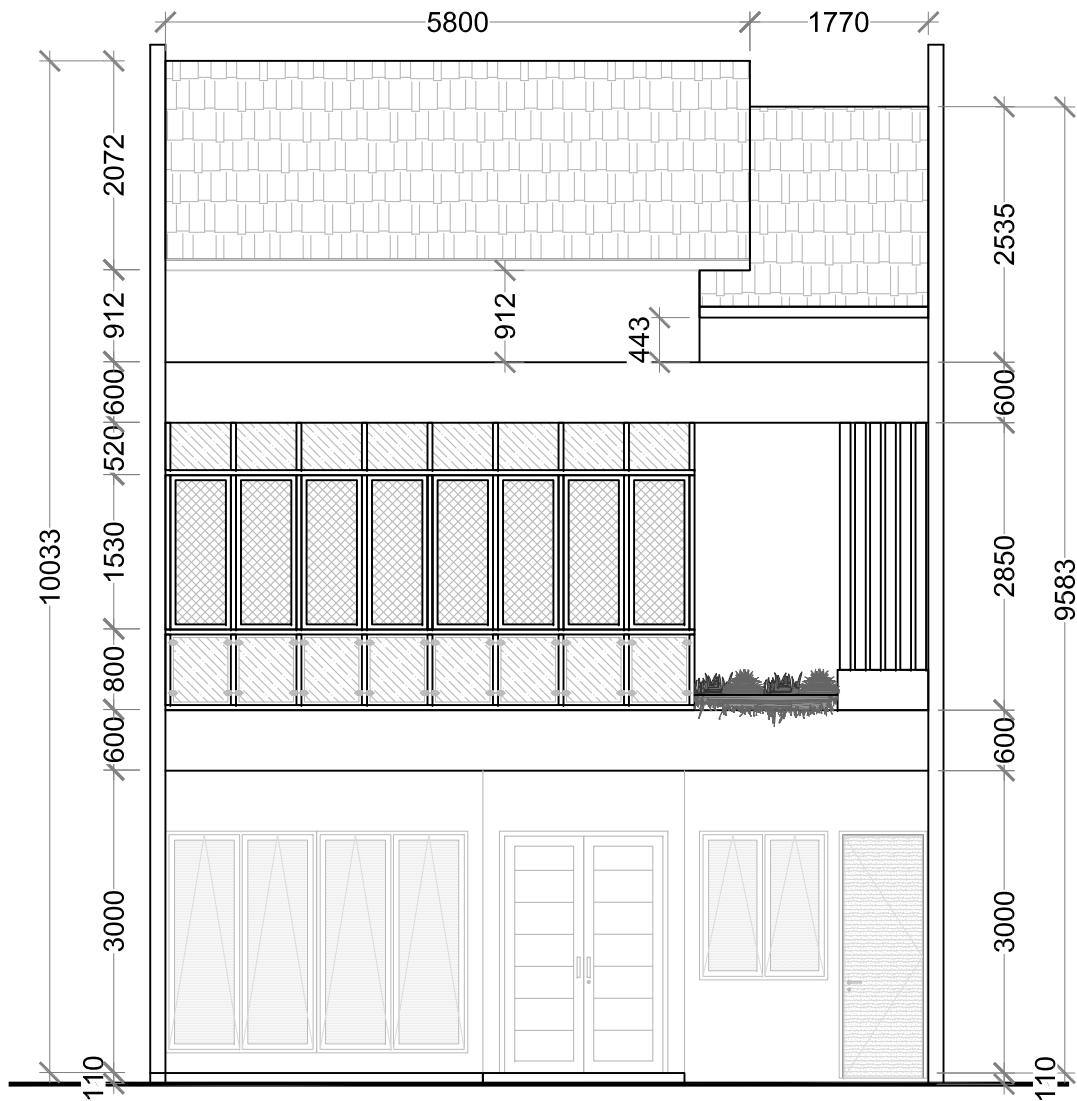

TAMPAK DEPAN

SKALA 1: 75

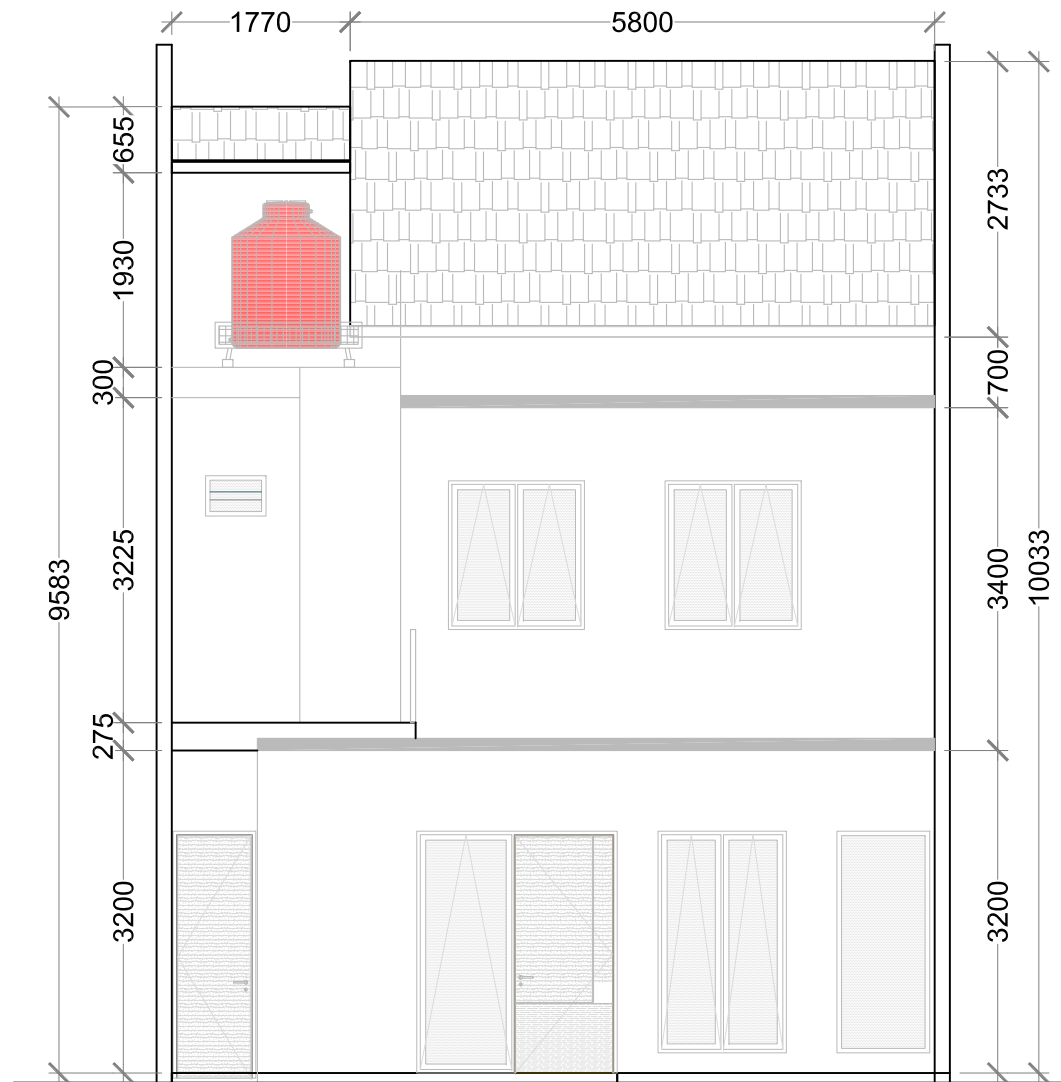

TAMPAK BELAKANG

SKALA 1: 75

KONSULTAN

KONTRAKTOR

PROYEK

TOWN HOUSE
JALAN JOE
JAGAKARSA
JAKARTA SELATAN

KETERANGAN

REVISI

ARSITEK

DIGAMBAR

DIPERIKSA

DISETUJUI

NO. PROYEK

NAMA GAMBAR

TAMPAK
KAVLING 2

SKALA

1 : 75

AR-015

SUBKAT

NO. LEMBAR




KONSULTAN				
KONTRAKTOR				
PROYEK TOWN HOUSE JALAN JOE JAGAKARSA JAKARTA SELATAN				
KETERANGAN				
REVISI				
		TGL	BLN	THN
ARSITEK				
DIGAMBAR				
DIPERIKSA				
DISETUJUI				
NO. PROYEK -				
NAMA GAMBAR DENAH KAVLING 3				
SKALA 1 : 75				
AR		- 016		
SUBKAT		NO. LEMBAR		



NO. LEMBAR

POTONGAN A - A

SKALA 1: 75

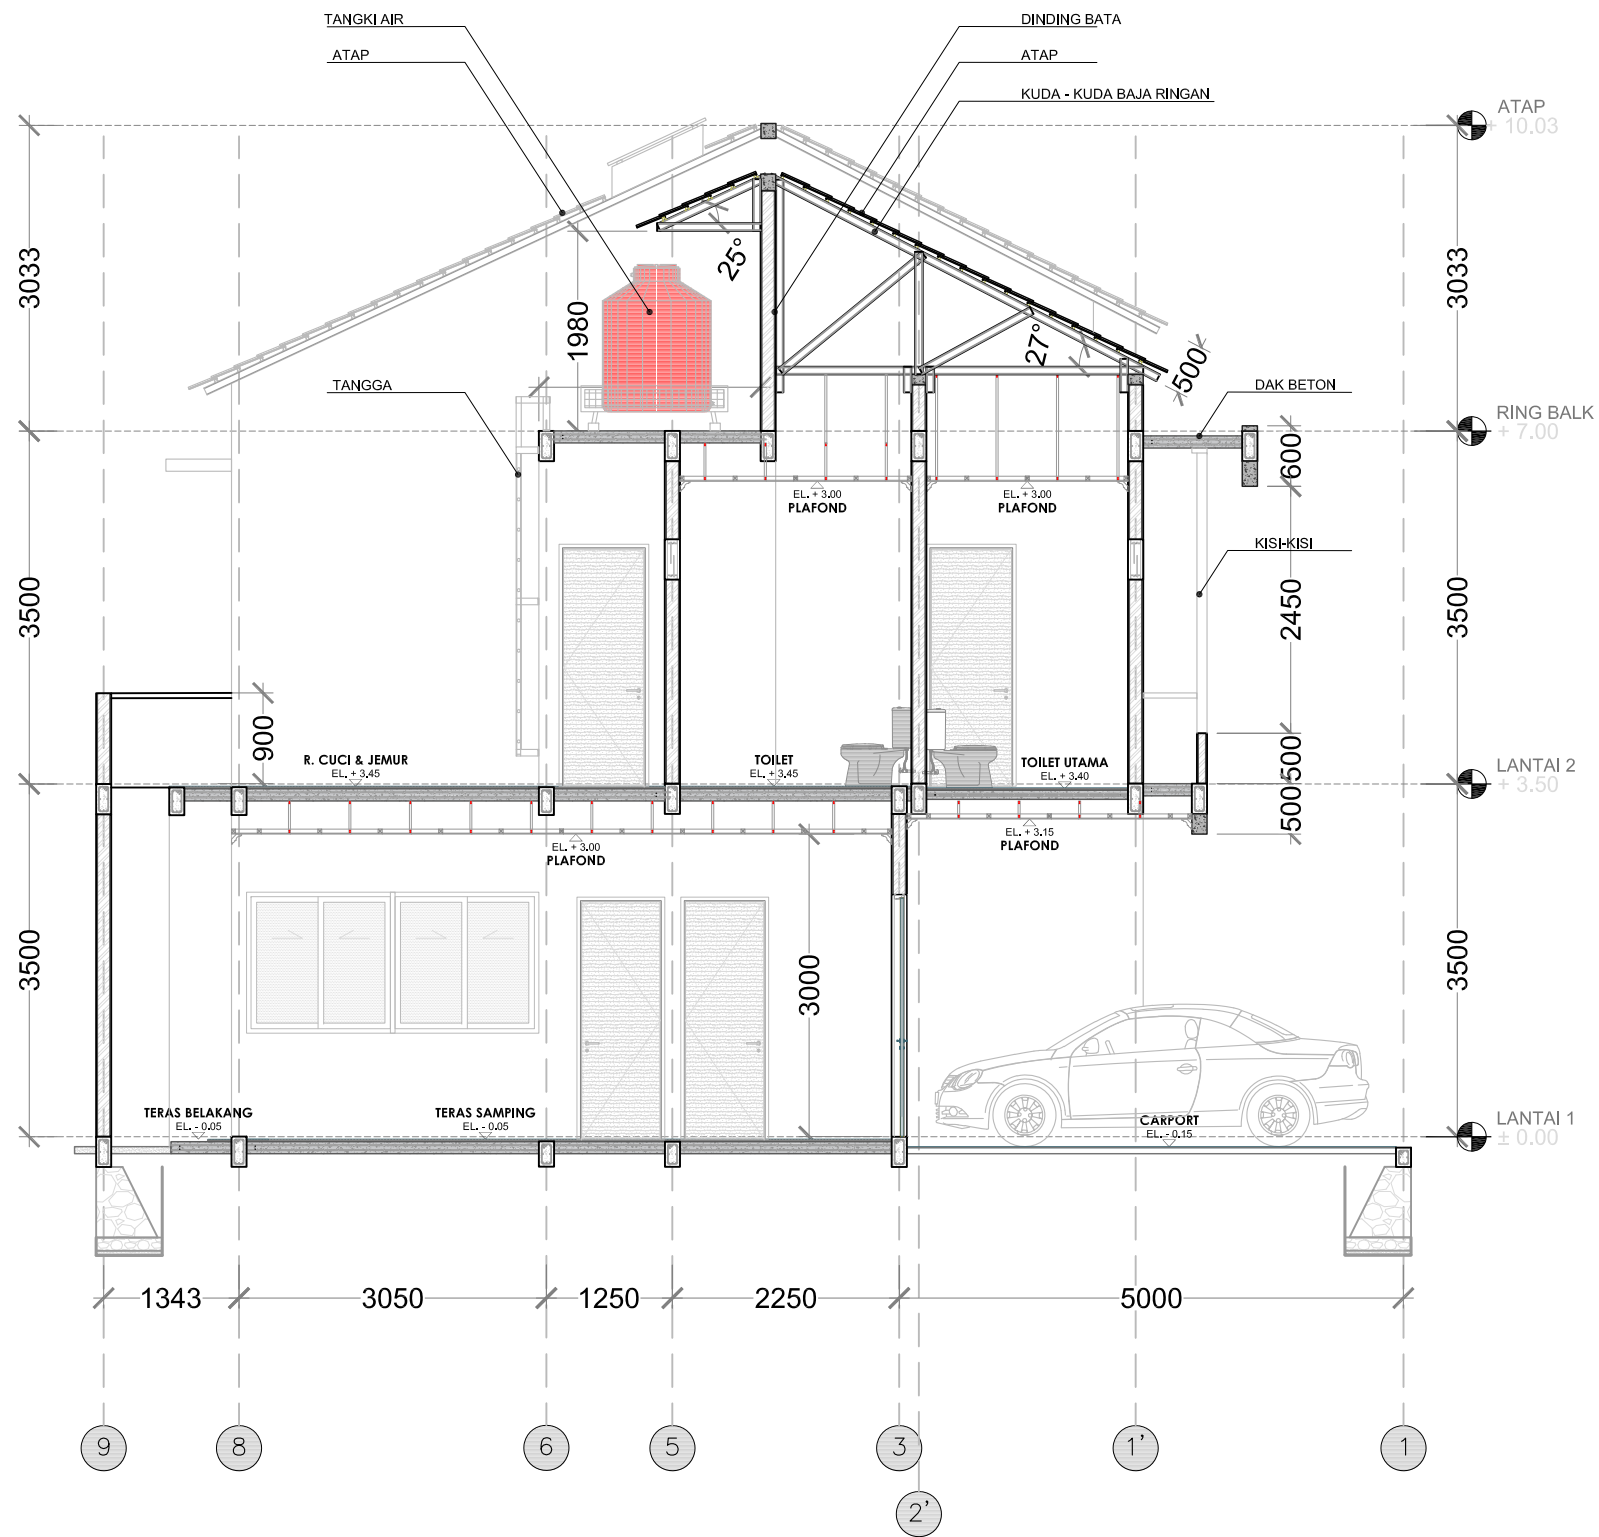

KONSULTAN

KONTRAKTOR

PROYEK

TOWN HOUSE
JALAN JOE
JAGAKARSA
JAKARTA SELATAN

KETERANGAN

REVISI

ARSITEK

DIGAMBAR

DIPERIKSA

DISETUJUI

NO. PROYEK

NAMA GAMBAR

POTONGAN A - A
KAVLING 3

SKALA

1 : 75


AR-018

SUBKAT

NO. LEMBAR

POTONGAN B - B

SKALA 1: 75

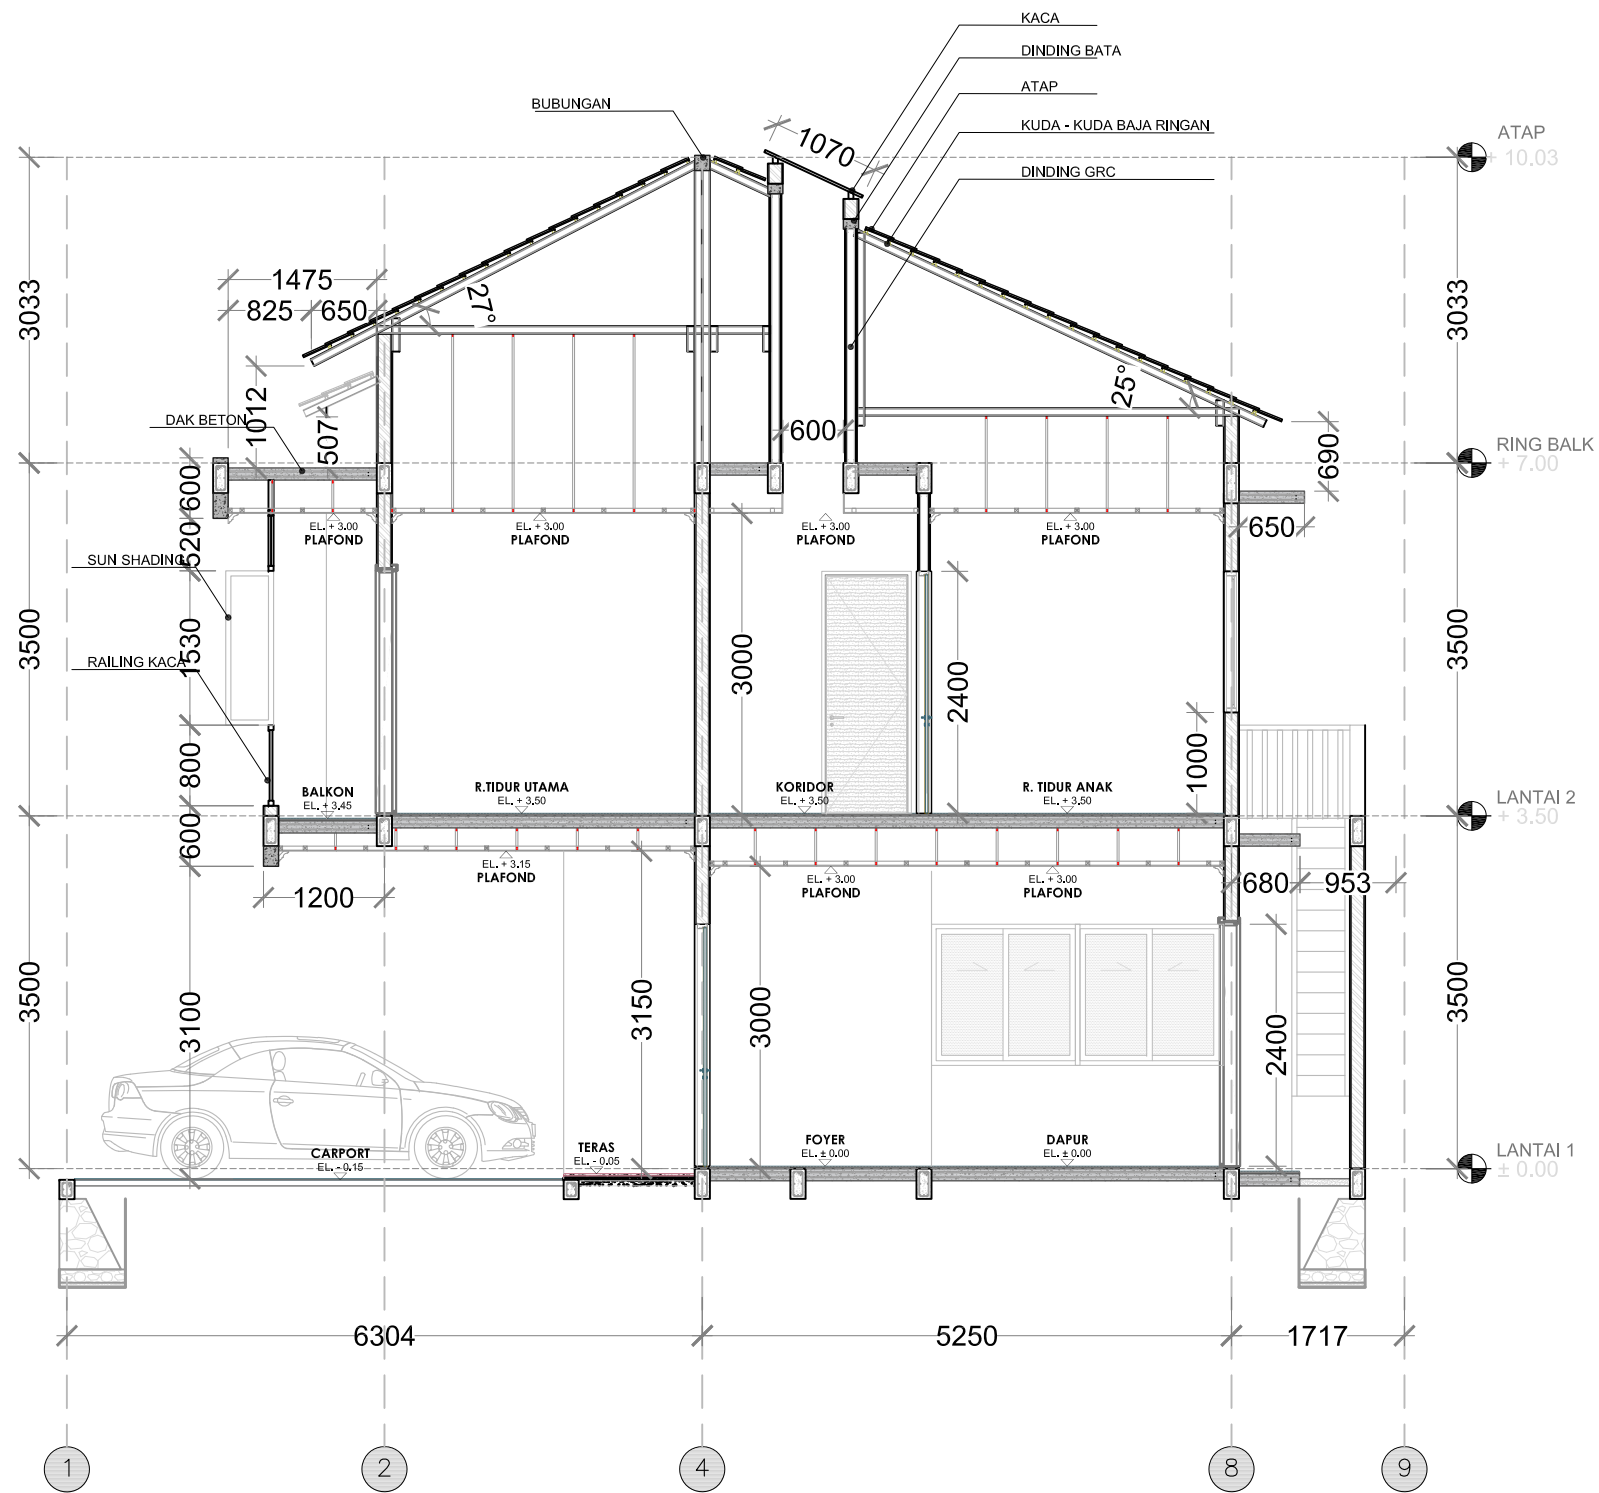

KONSULTAN

KONTRAKTOR

PROYEK

TOWN HOUSE
JALAN JOE
JAGAKARSA
JAKARTA SELATAN

KETERANGAN

REVISI

ARSITEK

DIGAMBAR

DIPERIKSA

DISETUJUI

NO. PROYEK

NAMA GAMBAR

POTONGAN B - B
KAVLING 3


SKALA

1 : 75

AR-019

SUBKAT


NO. LEMBAR

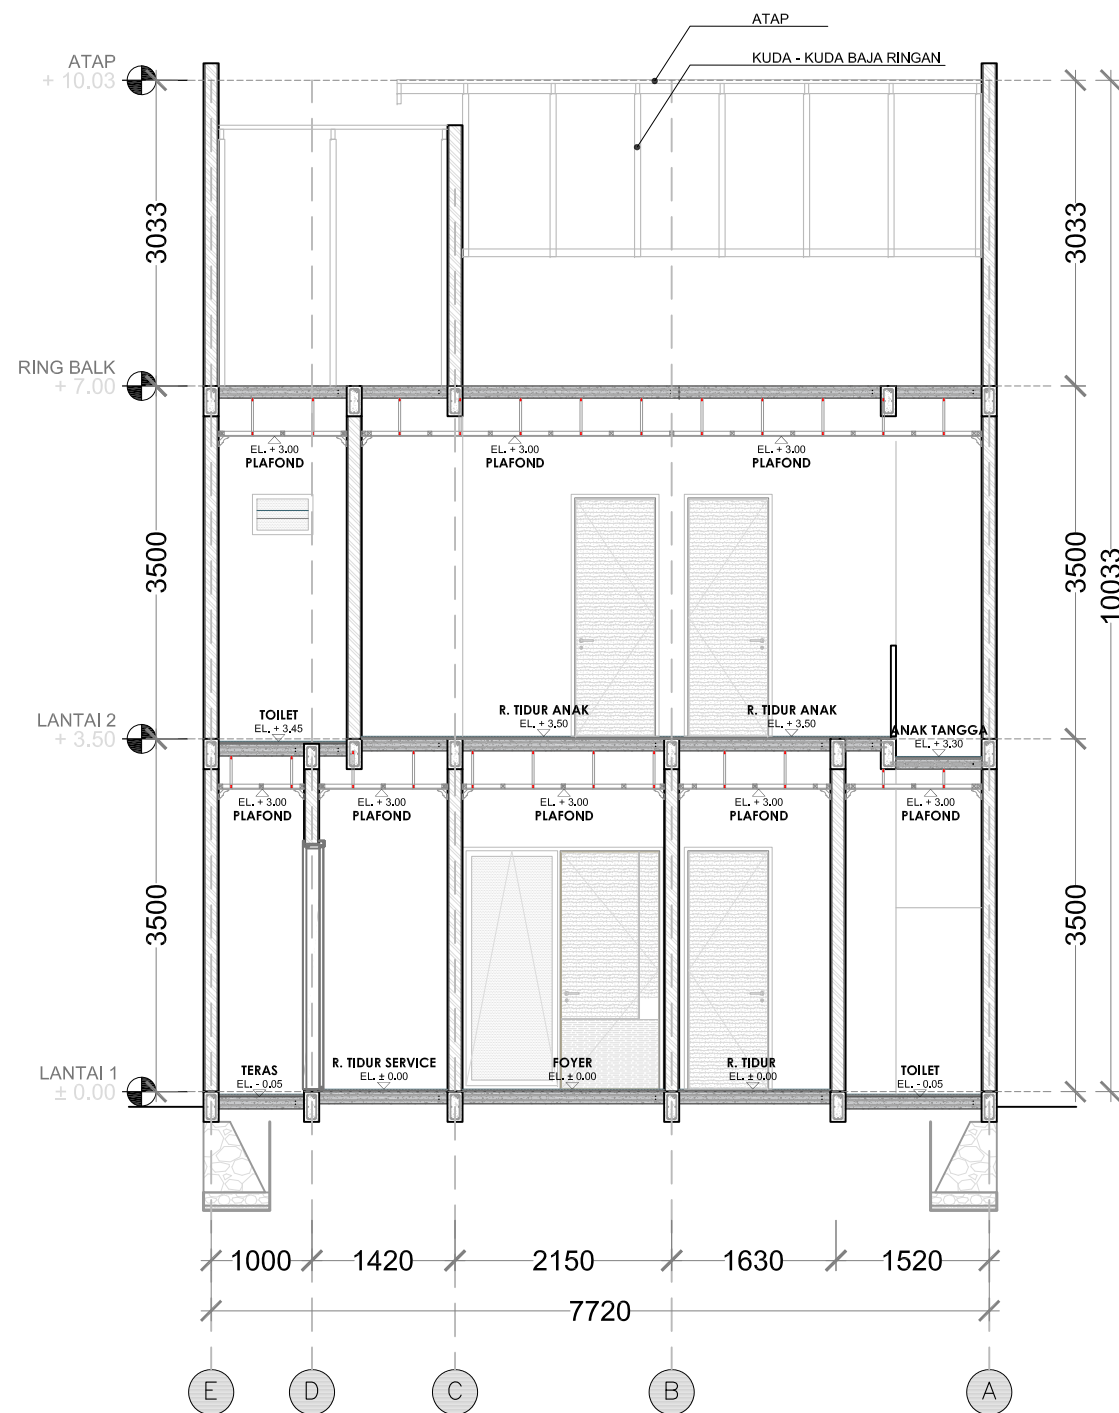

POTONGAN C - C


SKALA 1: 75

KONSULTAN				
KONTRAKTOR				
PROYEK				
TOWN HOUSE JALAN JOE JAGAKARSA JAKARTA SELATAN				
KETERANGAN				
REVISI		TGL		
		BLN	THN	
ARSITEK				
DIGAMBAR				
DIPERIKSA				
DISETUJUI				
NO. PROYEK				
-				
NAMA GAMBAR				
POTONGAN C - C KAVLING 3				
SKALA				
1 : 75				
AR		- 020		
SUBKAT		NO. LEMBAR		

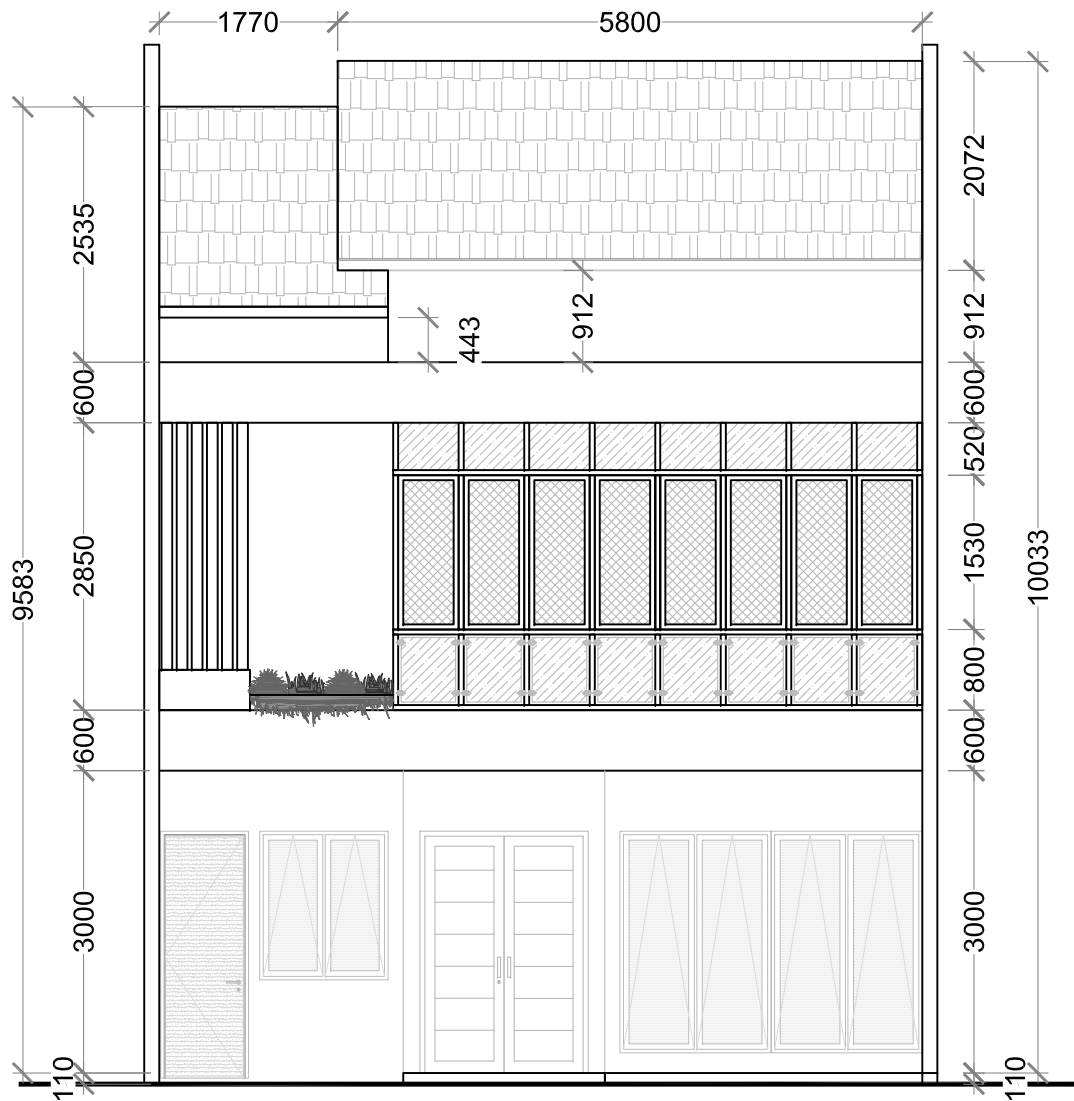

TAMPAK DEPAN

SKALA 1: 75

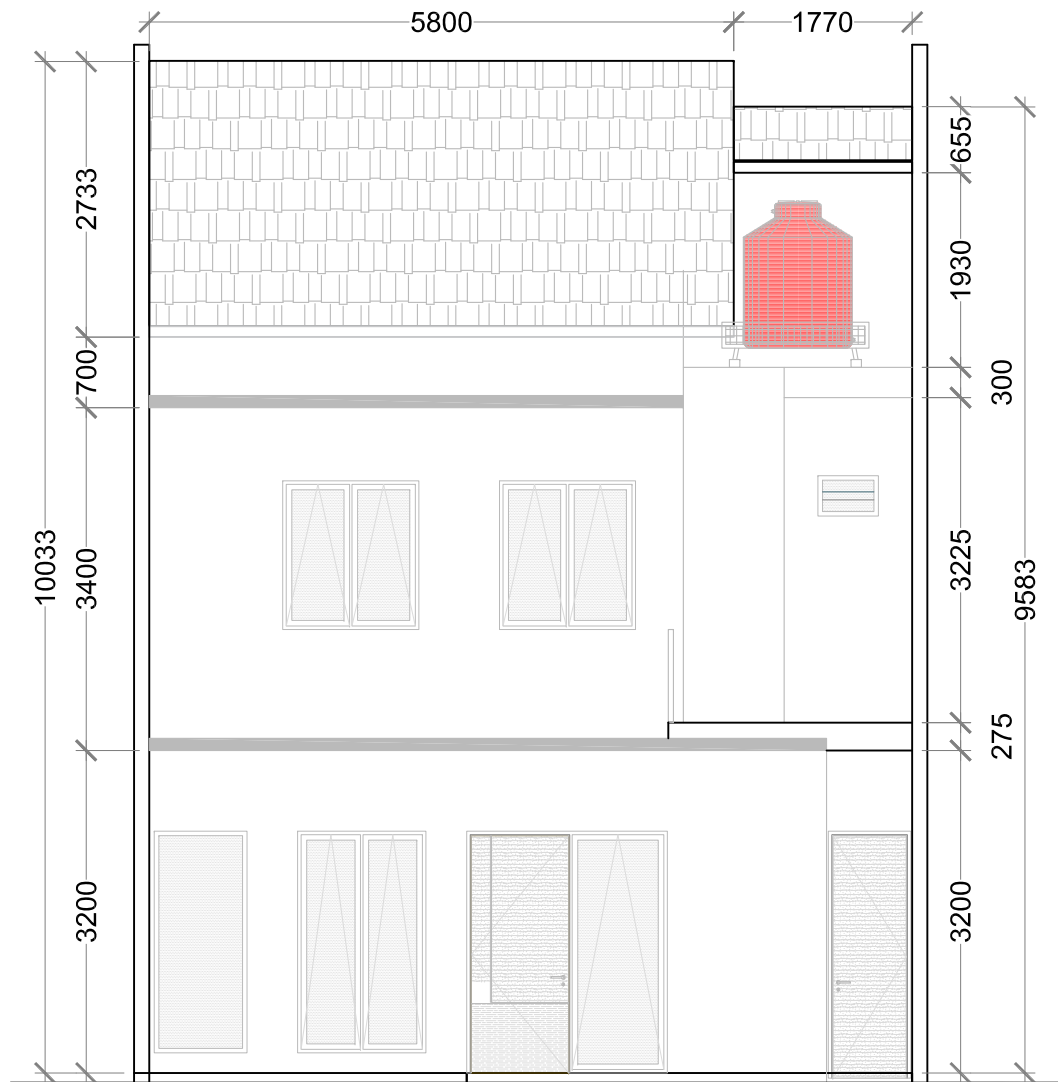

TAMPAK BELAKANG

SKALA 1: 75

KONSULTAN

KONTRAKTOR

PROYEK

TOWN HOUSE
JALAN JOE
JAGAKARSA
JAKARTA SELATAN

KETERANGAN

REVISI

	TGL	BLN	THN

ARSITEK

DIGAMBAR

DIPERIKSA

DISETUJUI

NO. PROYEK

NAMA GAMBAR

TAMPAK
KAVLING 3

SKALA


1 : 75

AR-021

SUBKAT NO. LEMBAR




KONSULTAN				
KONTRAKTOR				
PROYEK				
TOWN HOUSE JALAN JOE JAGAKARSA JAKARTA SELATAN				
KETERANGAN				
REVISI		TGL	BLN	THN
ARSITEK				
DIGAMBAR				
DIPERIKSA				
DISETUJUI				
NO. PROYEK				
-				
NAMA GAMBAR				
DENAH KAVLING 4				
SKALA				
1 : 75				
AR-022				
SUBKAT		NO. LEMBAR		

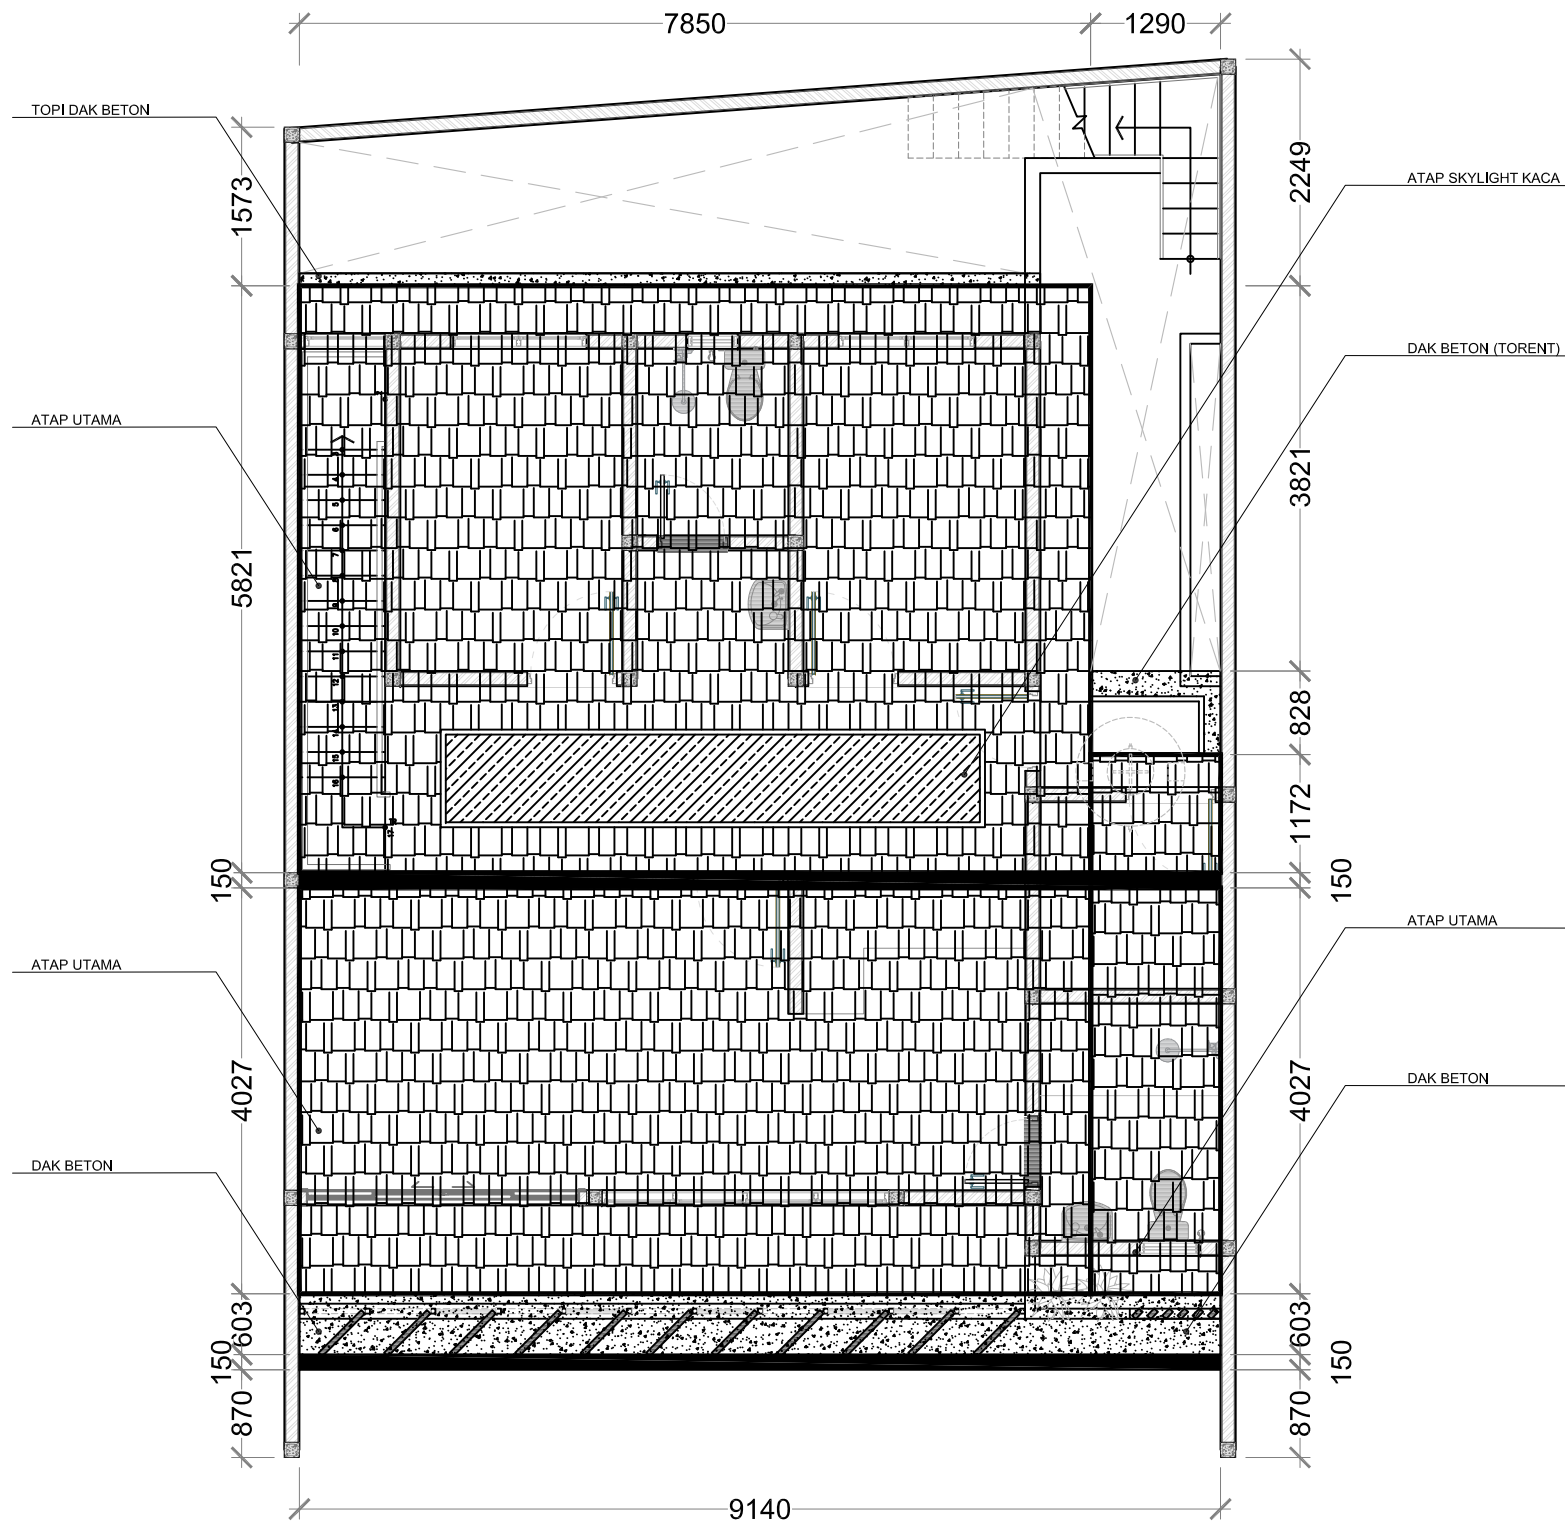

RENCANA ATAP
SKALA 1: 75

KONSULTAN			
KONTRAKTOR			
PROYEK			
TOWN HOUSE JALAN JOE JAGAKARSA JAKARTA SELATAN			
KETERANGAN			
REVISI		TGL	BLN
ARSITEK			
DIGAMBAR			
DIPERIKSA			
DISETUJUI			
NO. PROYEK			
-			
NAMA GAMBAR			
RENCANA ATAP KAVLING 4			
SKALA			
1 : 75			
AR-023			
SUBKAT	NO. LEMBAR		

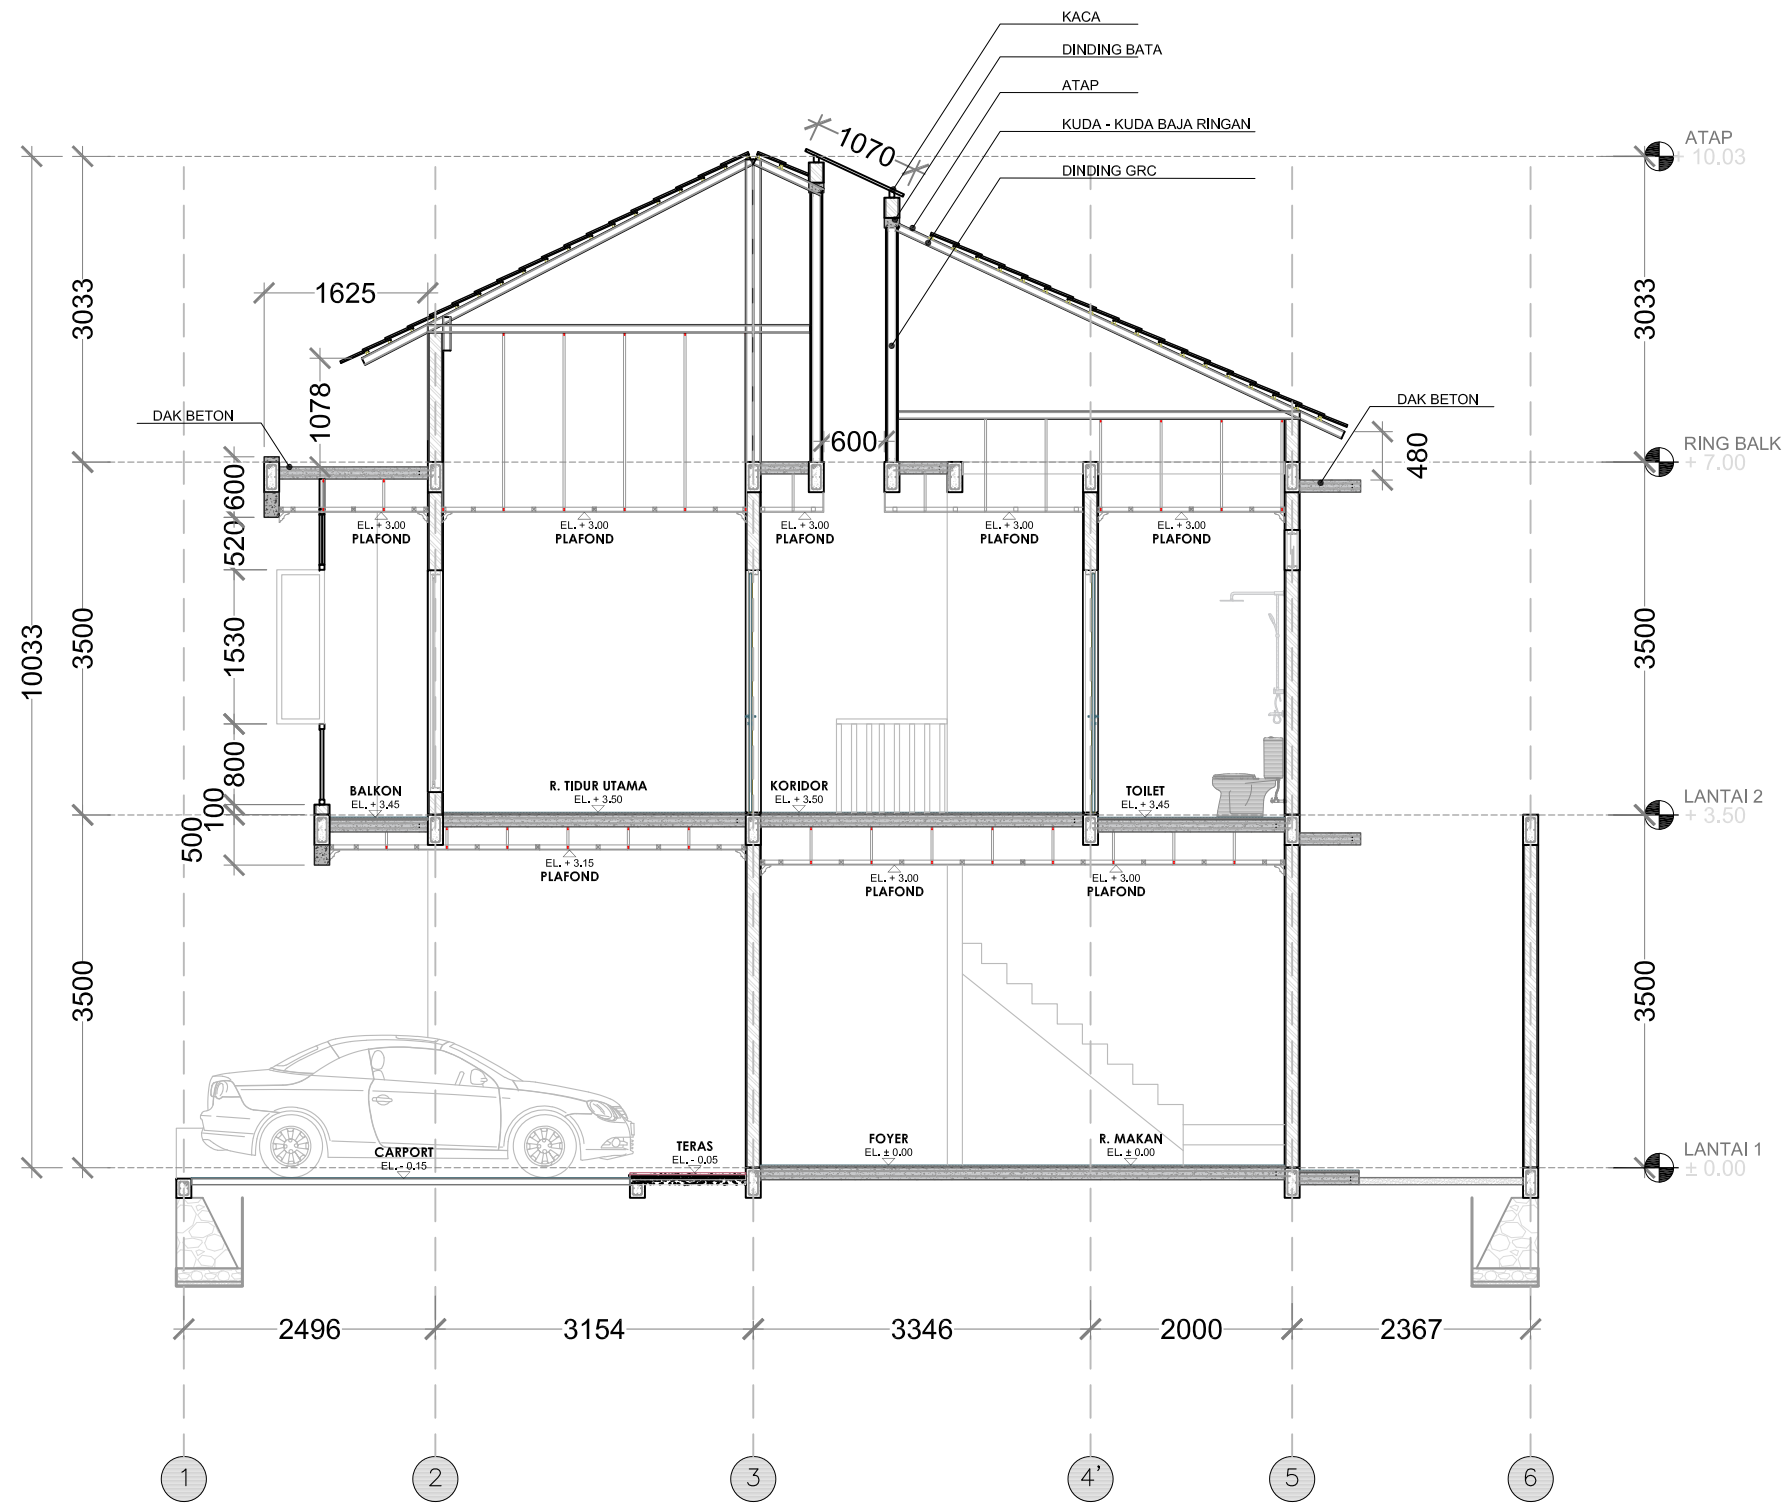


POTONGAN A - A
SKALA 1: 75


KONSULTAN			
KONTRAKTOR			
PROYEK			
TOWN HOUSE JALAN JOE JAGAKARSA JAKARTA SELATAN			
KETERANGAN			
REVISI			
	TGL	BLN	THN
ARSITEK			
DIGAMBAR			
DIPERIKSA			
DISETUJUI			
NO. PROYEK			
-			
NAMA GAMBAR			
POTONGAN A - A KAVLING 4			
SKALA			
1 : 75			
AR-024			
SUBKAT		NO. LEMBAR	

POTONGAN B - B

SKALA 1: 75

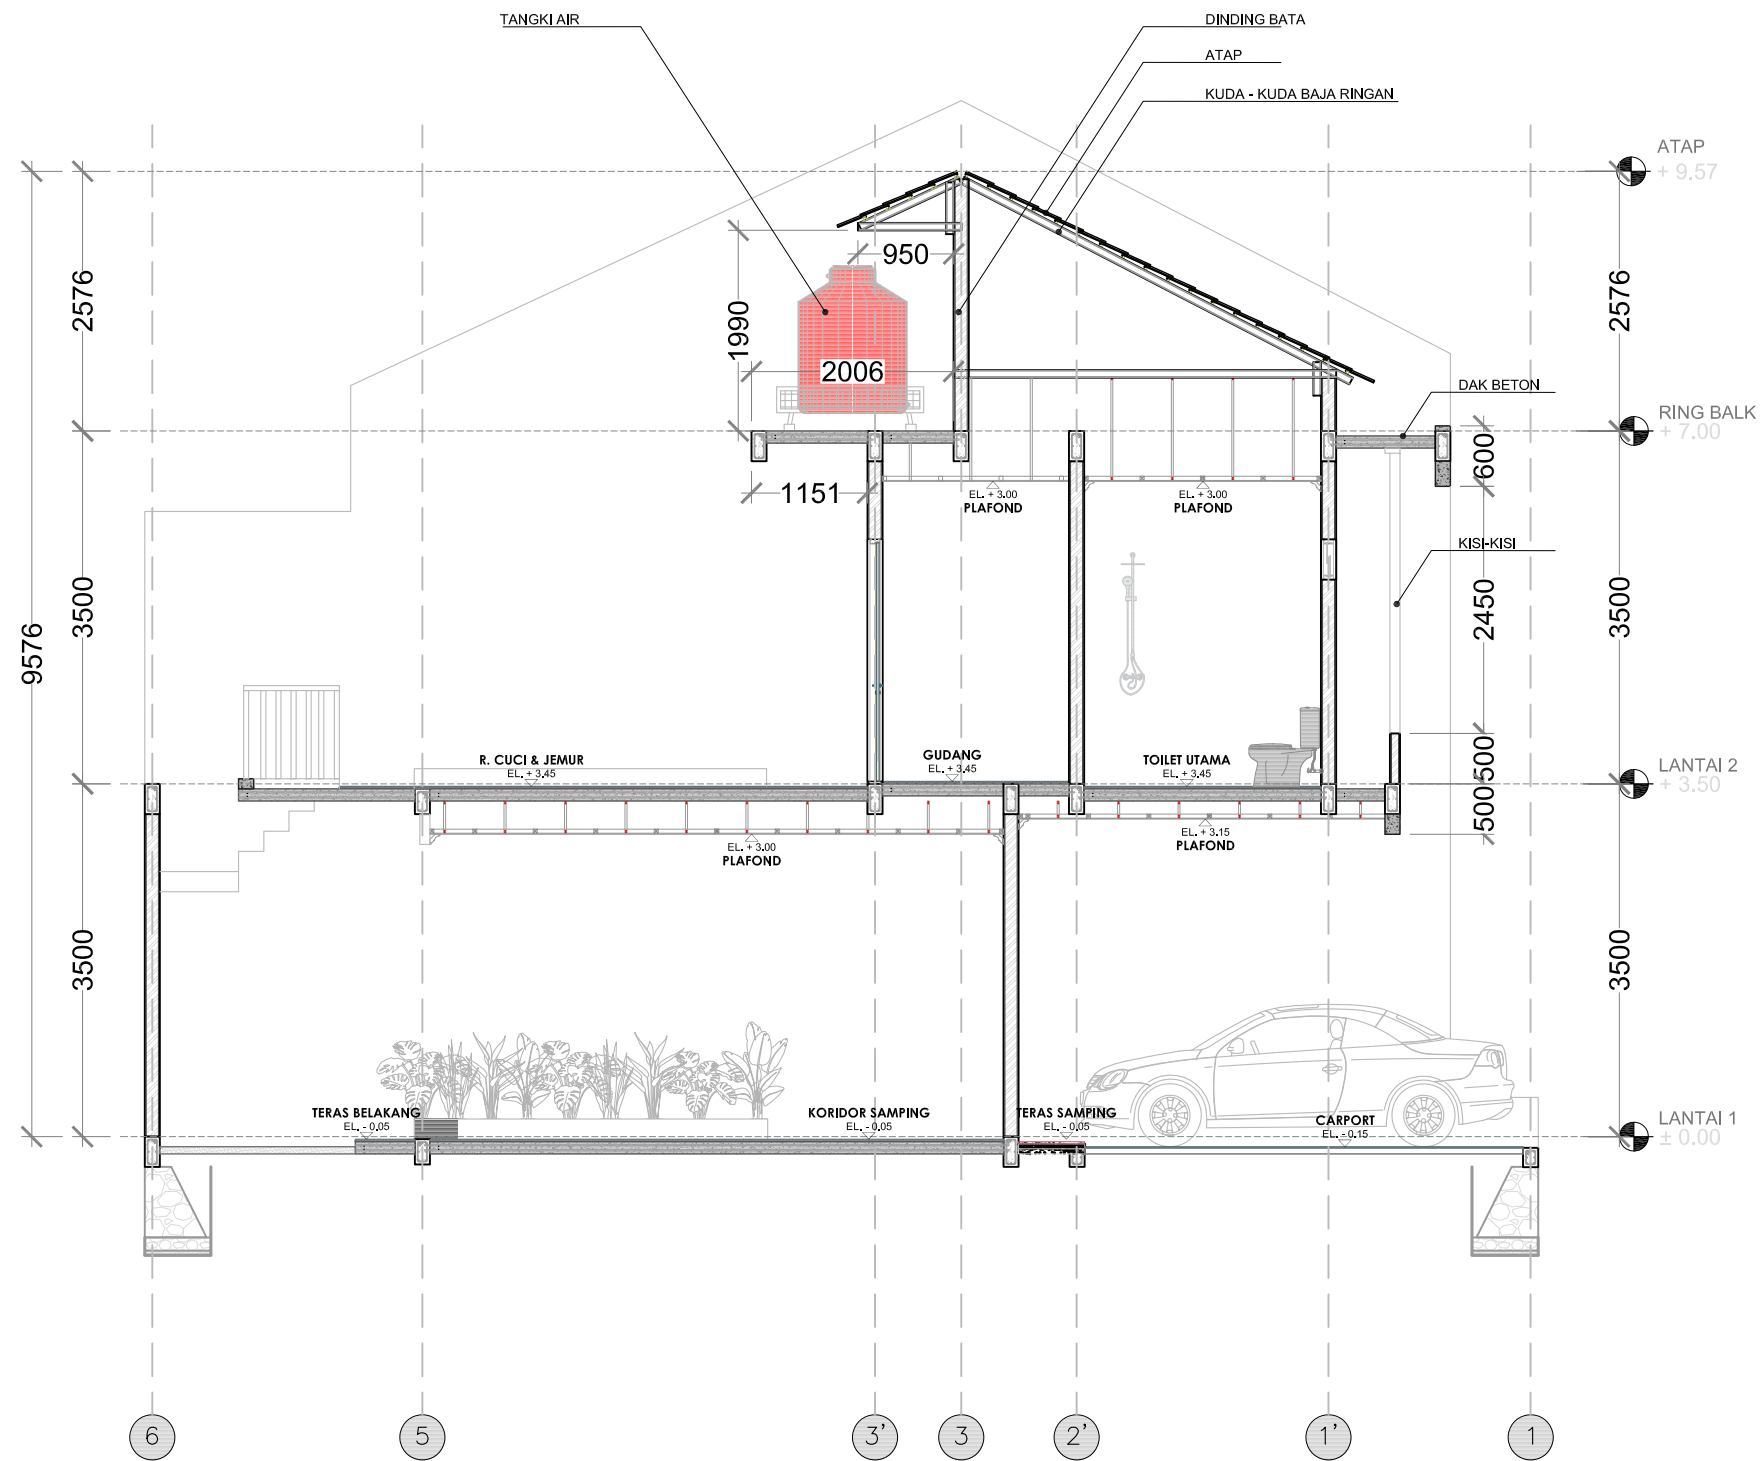


KONSULTAN			
KONTRAKTOR			
PROYEK			
TOWN HOUSE JALAN JOE JAGAKARSA JAKARTA SELATAN			
KETERANGAN			
REVISI			
		TGL	BLN
		THN	
ARSITEK			
DIGAMBAR			
DIPERIKSA			
DISETUJUI			
NO. PROYEK			
-			
NAMA GAMBAR			
POTONGAN B - B KAVLING 1			
SKALA			
1 : 75			
AR-025			
SUBKAT		NO. LEMBAR	

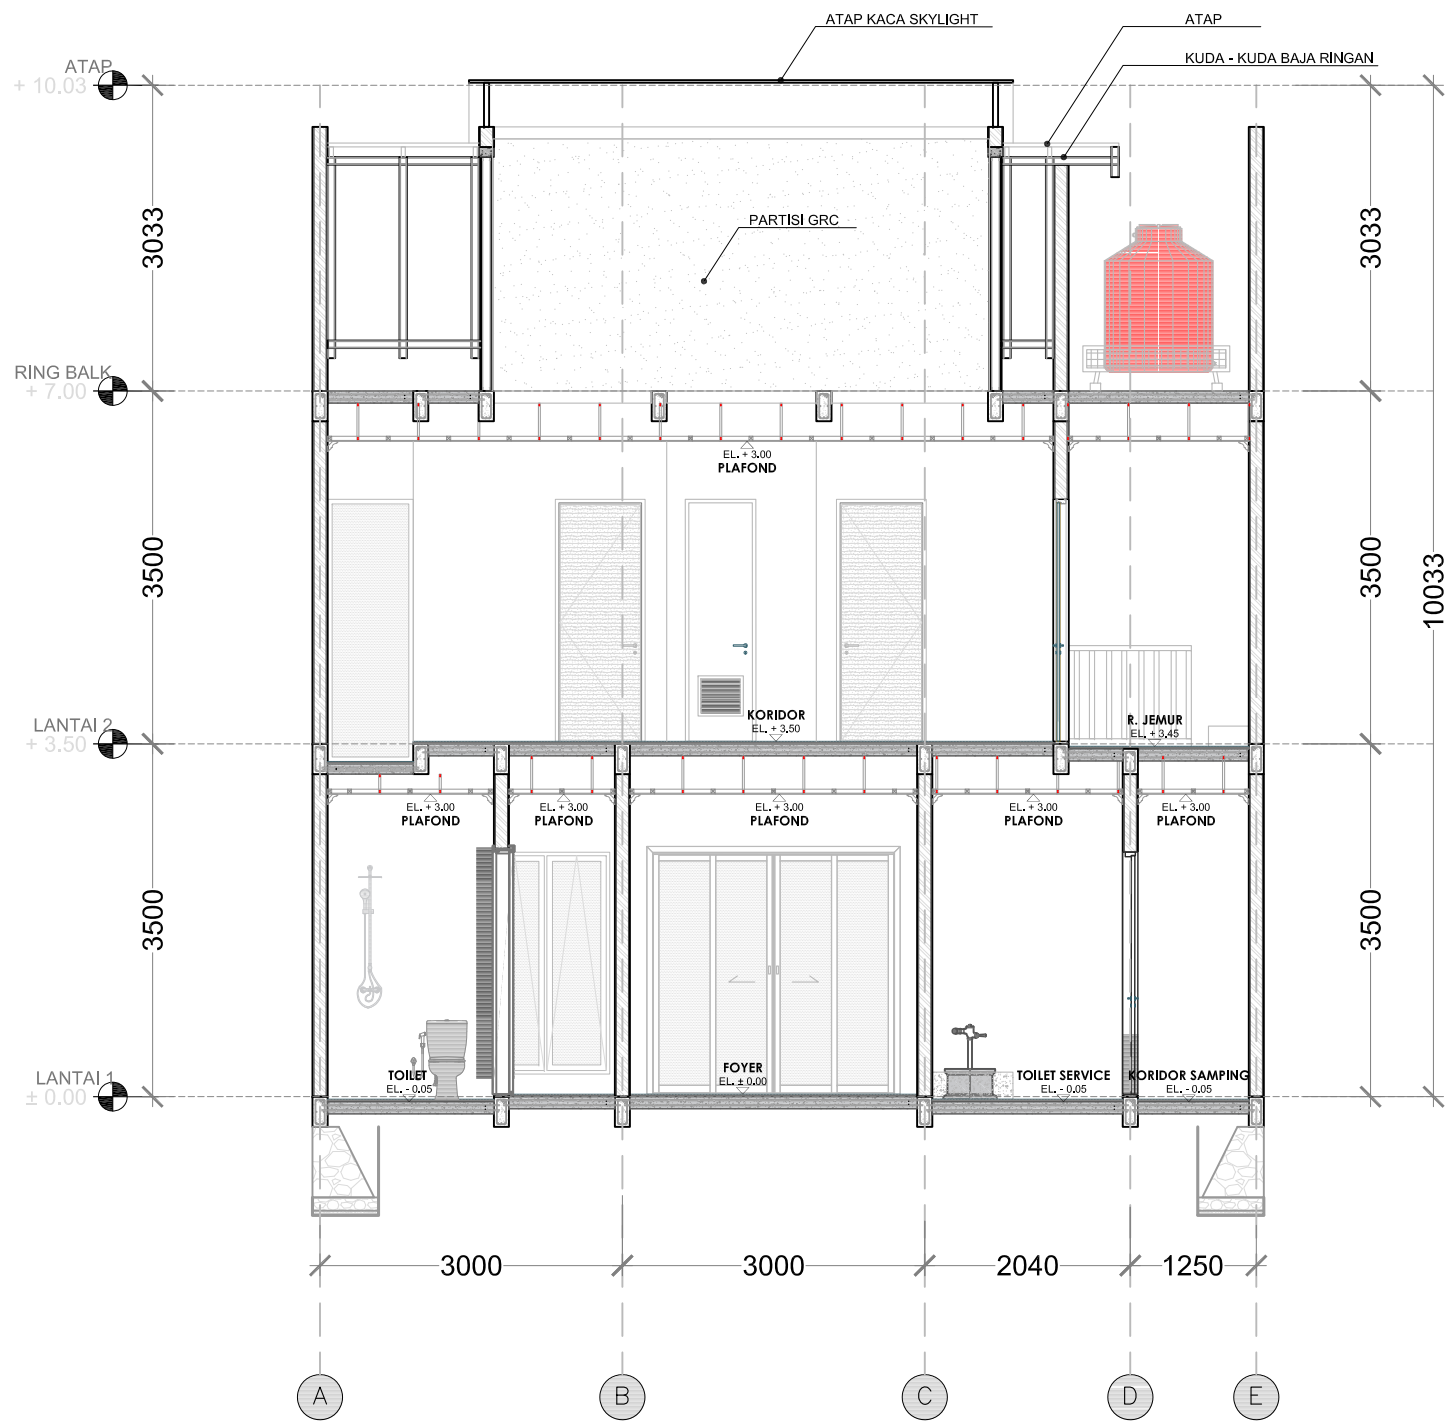


POTONGAN C - C
SKALA 1: 75

KONSULTAN			
KONTRAKTOR			
PROYEK			
TOWN HOUSE JALAN JOE JAGAKARSA JAKARTA SELATAN			
KETERANGAN			
REVISI			
	TGL	BLN	THN
ARSITEK			
DIGAMBAR			
DIPERIKSA			
DISETUJUI			
NO. PROYEK			
-			
NAMA GAMBAR			
POTONGAN C - C KAVLING 4			
SKALA			
1 : 75			
AR-026			
SUBKAT		NO. LEMBAR	

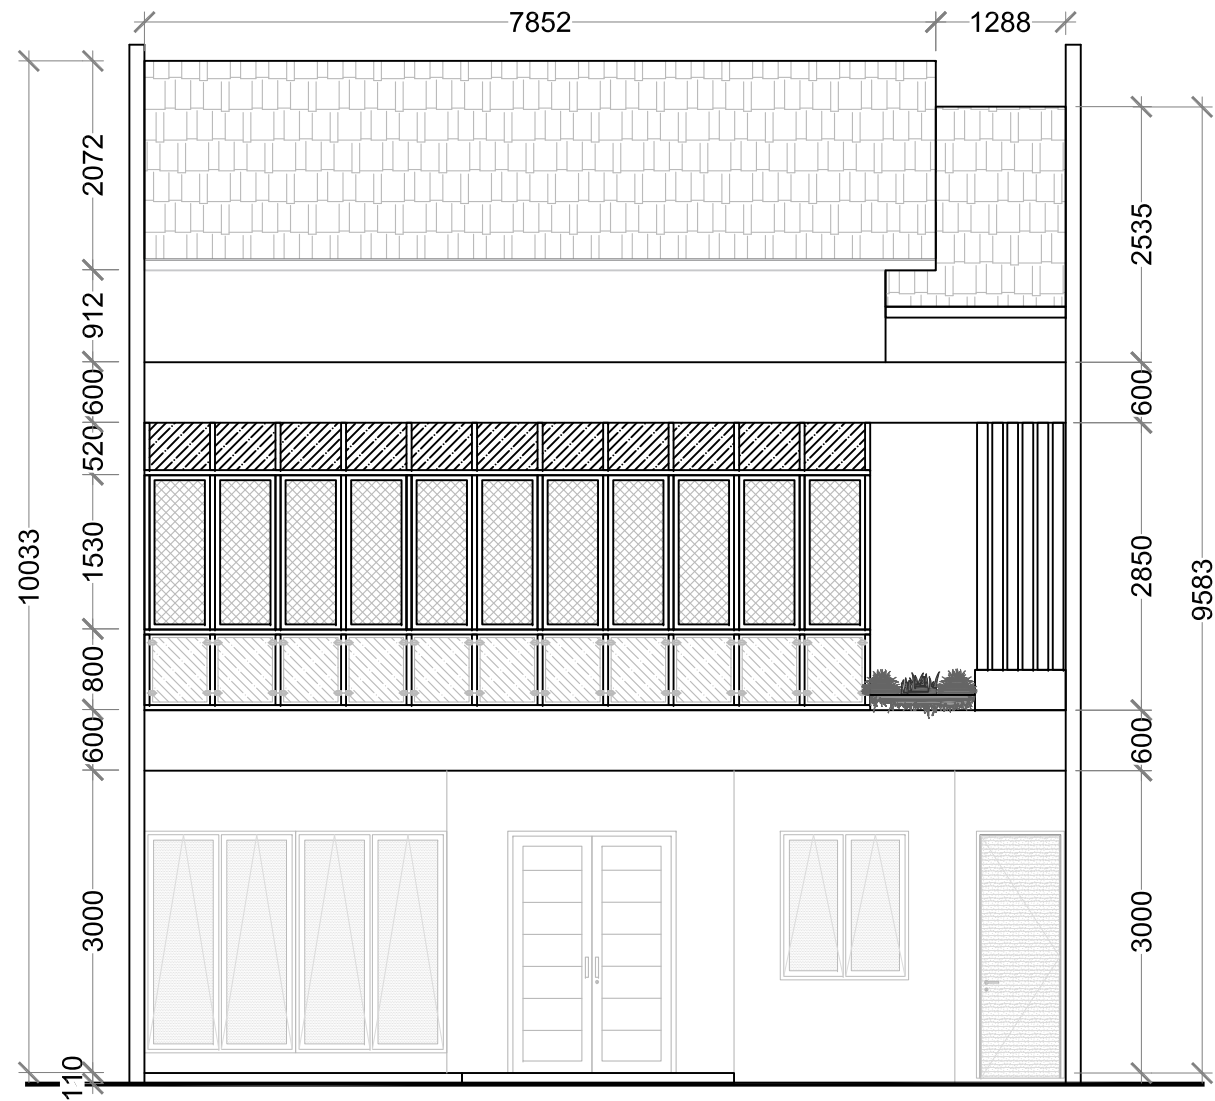


TAMPAK DEPAN
SKALA 1: 75

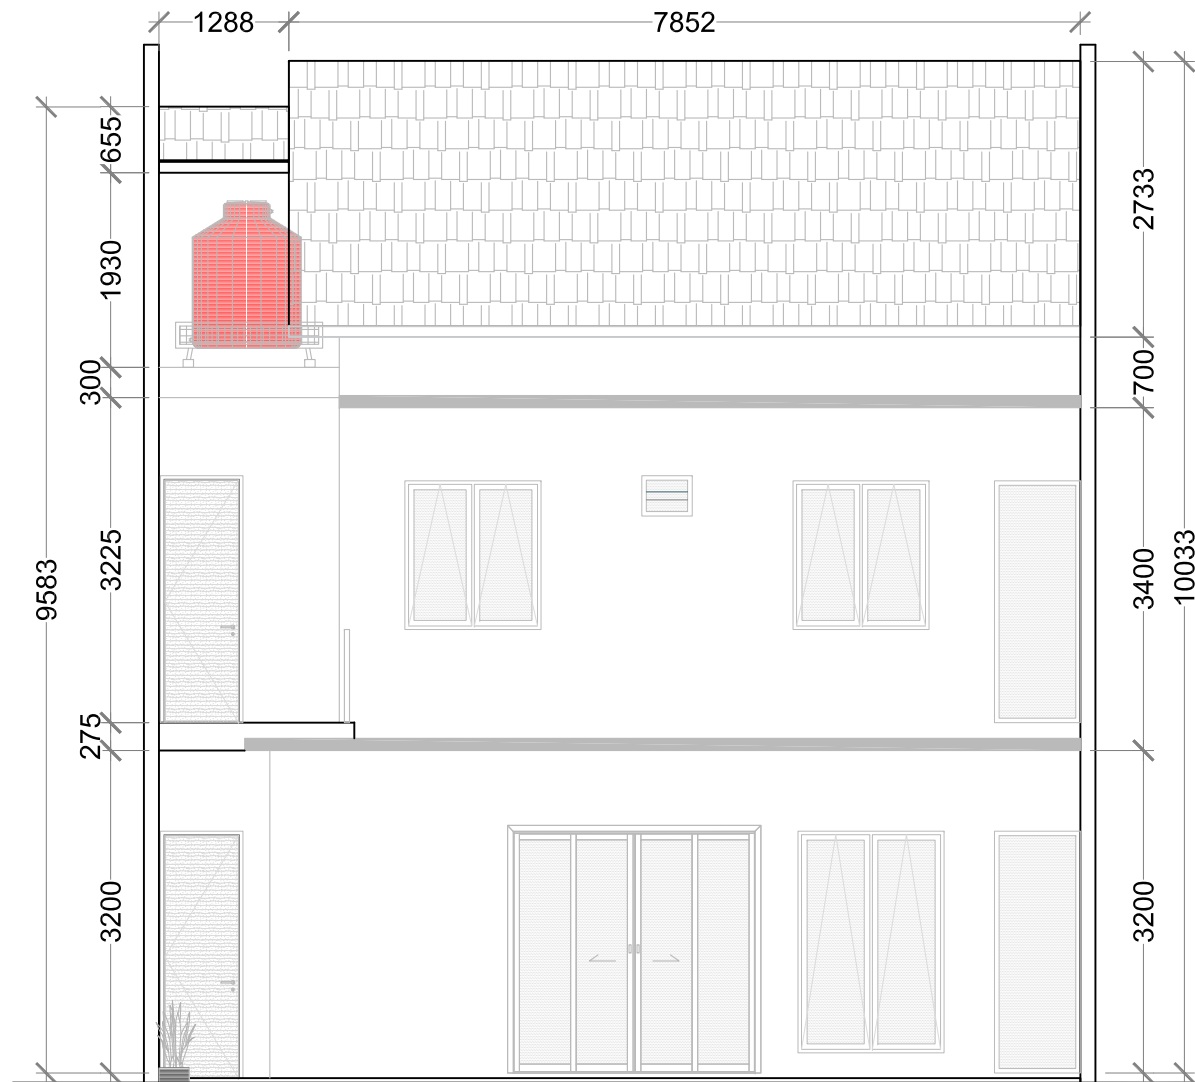


TAMPAK BELAKANG
SKALA 1: 75

KONSULTAN				
KONTRAKTOR				
PROYEK				
TOWN HOUSE JALAN JOE JAGAKARSA JAKARTA SELATAN				
KETERANGAN				
REVISI		TGL	BLN	THN
ARSITEK				
DIGAMBAR				
DIPERIKSA				
DISETUJUI				
NO. PROYEK				
-				
NAMA GAMBAR				
TAMPAK KAVLING 4				
SKALA				
1 : 75				
AR-027				
SUBKAT		NO. LEMBAR		

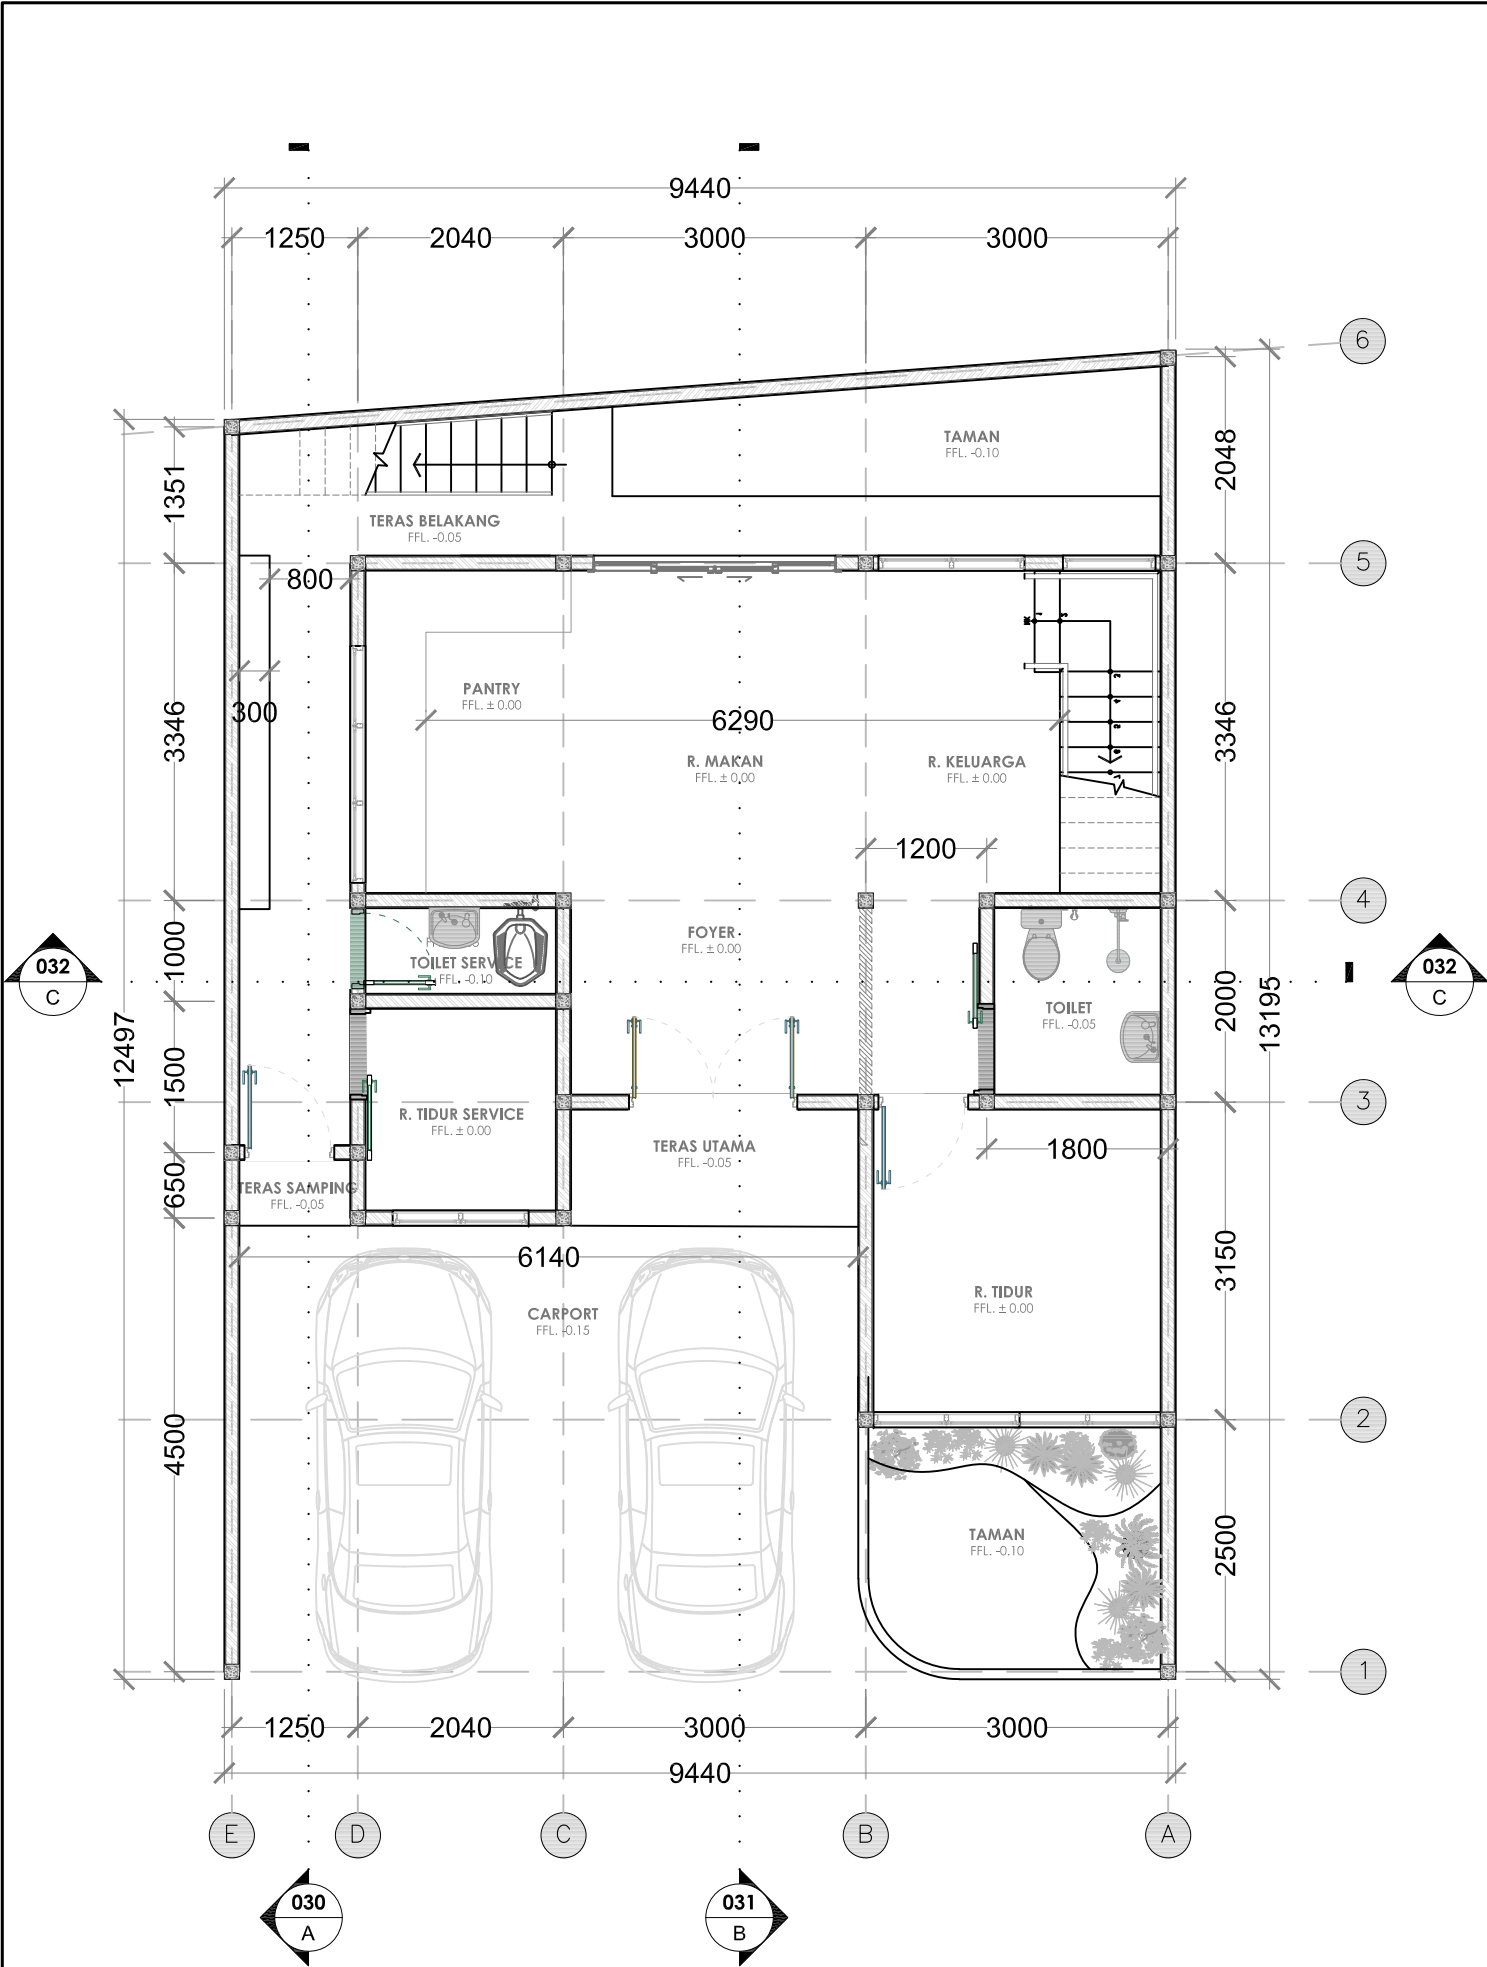

DENAH LANTAI DASAR
SKALA 1: 75

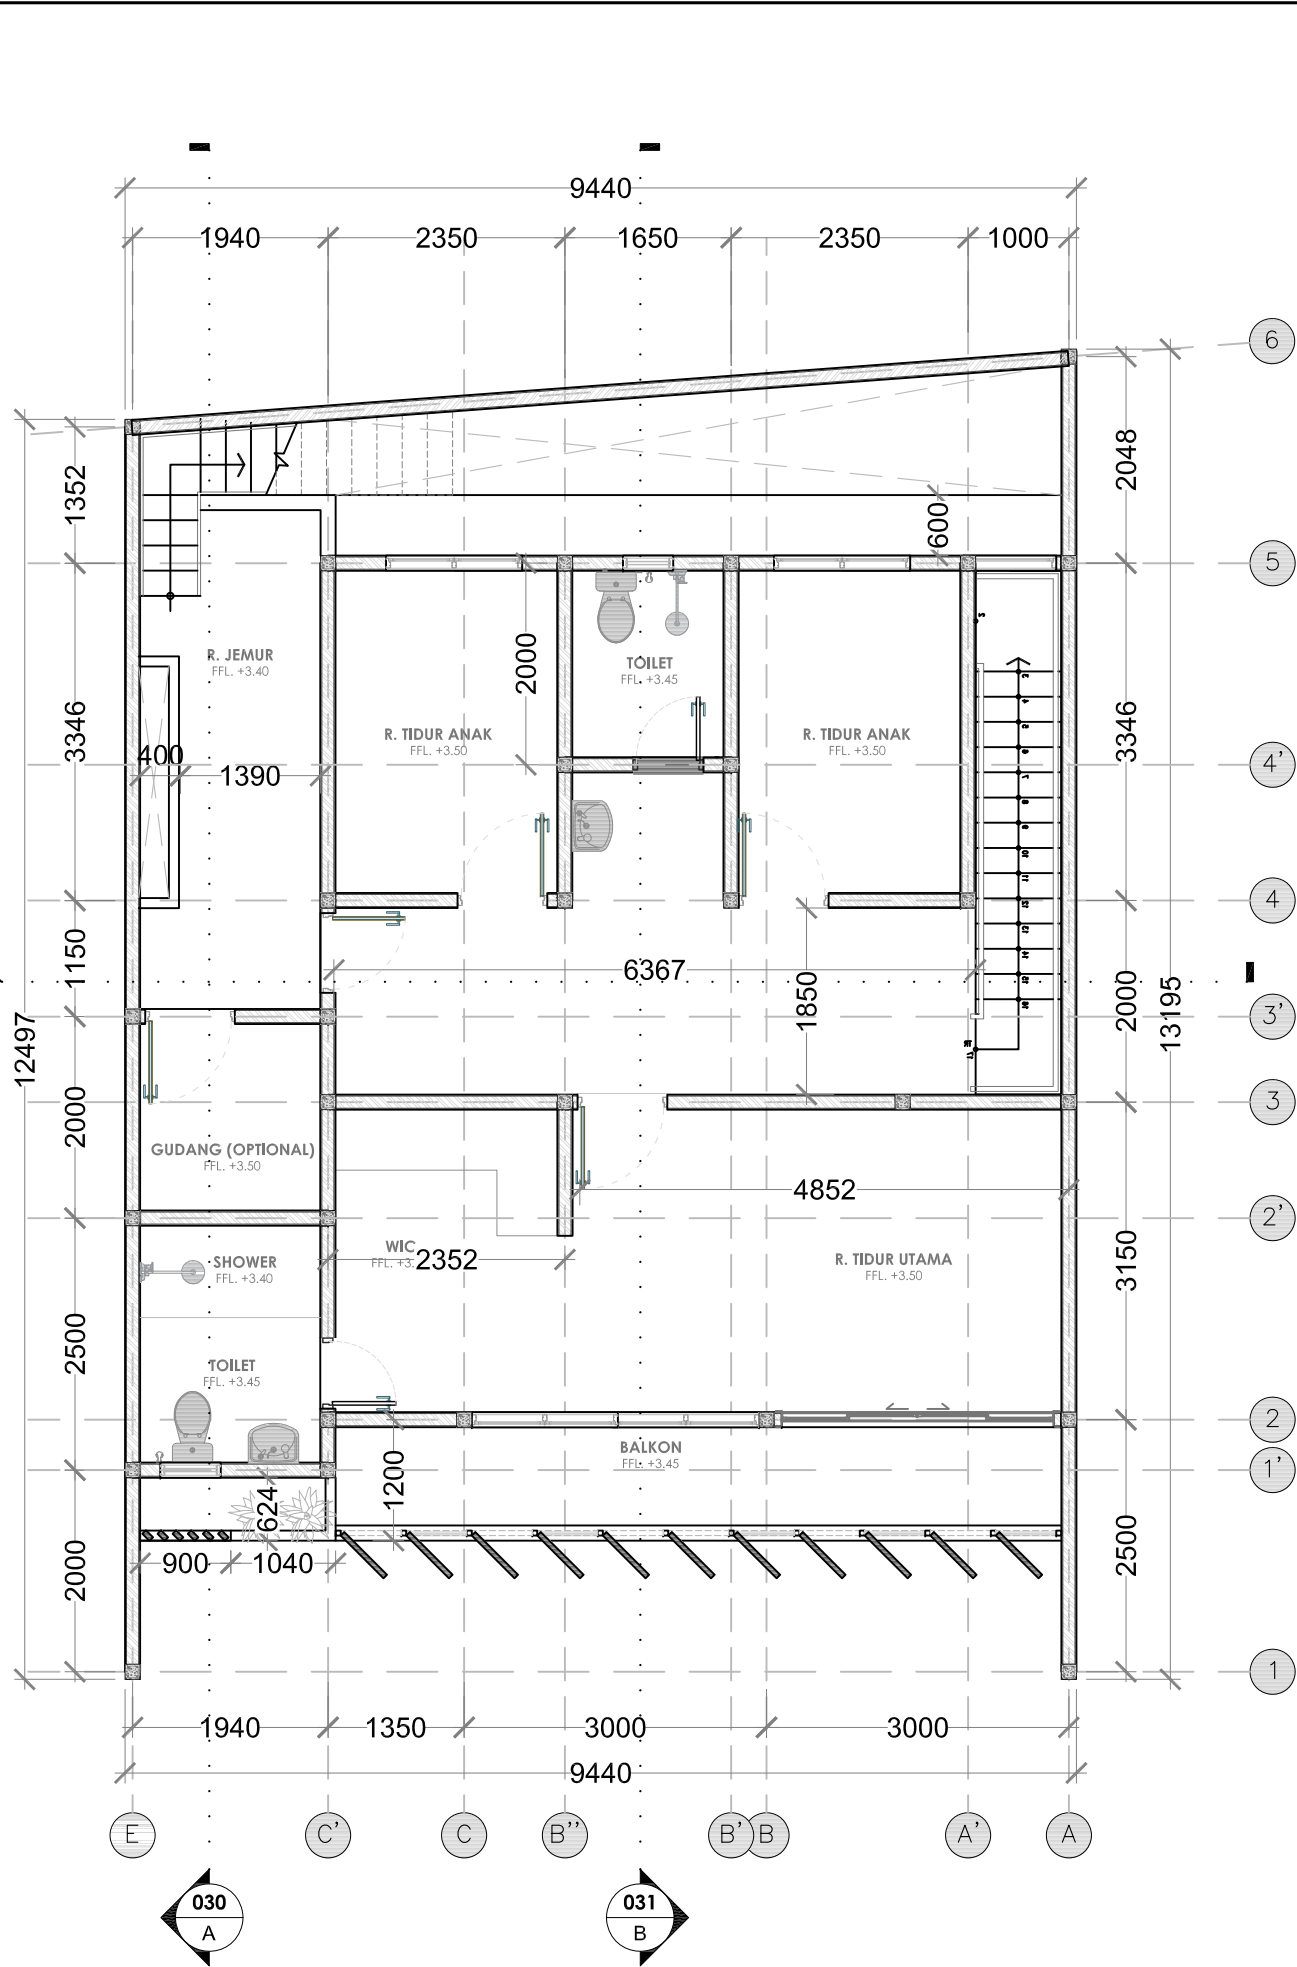

DENAH LANTAI ATAS
SKALA 1: 75

KONSULTAN

KONTRAKTOR

PROYEK

TOWN HOUSE
JALAN JOE
JAGAKARSA
JAKARTA SELATAN

KETERANGAN

REVISI

TGL

BLN

THN

ARSITEK

DIGAMBAR

DIPERIKSA

DISETUJUI

NO. PROYEK

NAMA GAMBAR

DENAH
KAVLING 5


SKALA

1 : 75

AR-028


SUBKAT

NO. LEMBAR

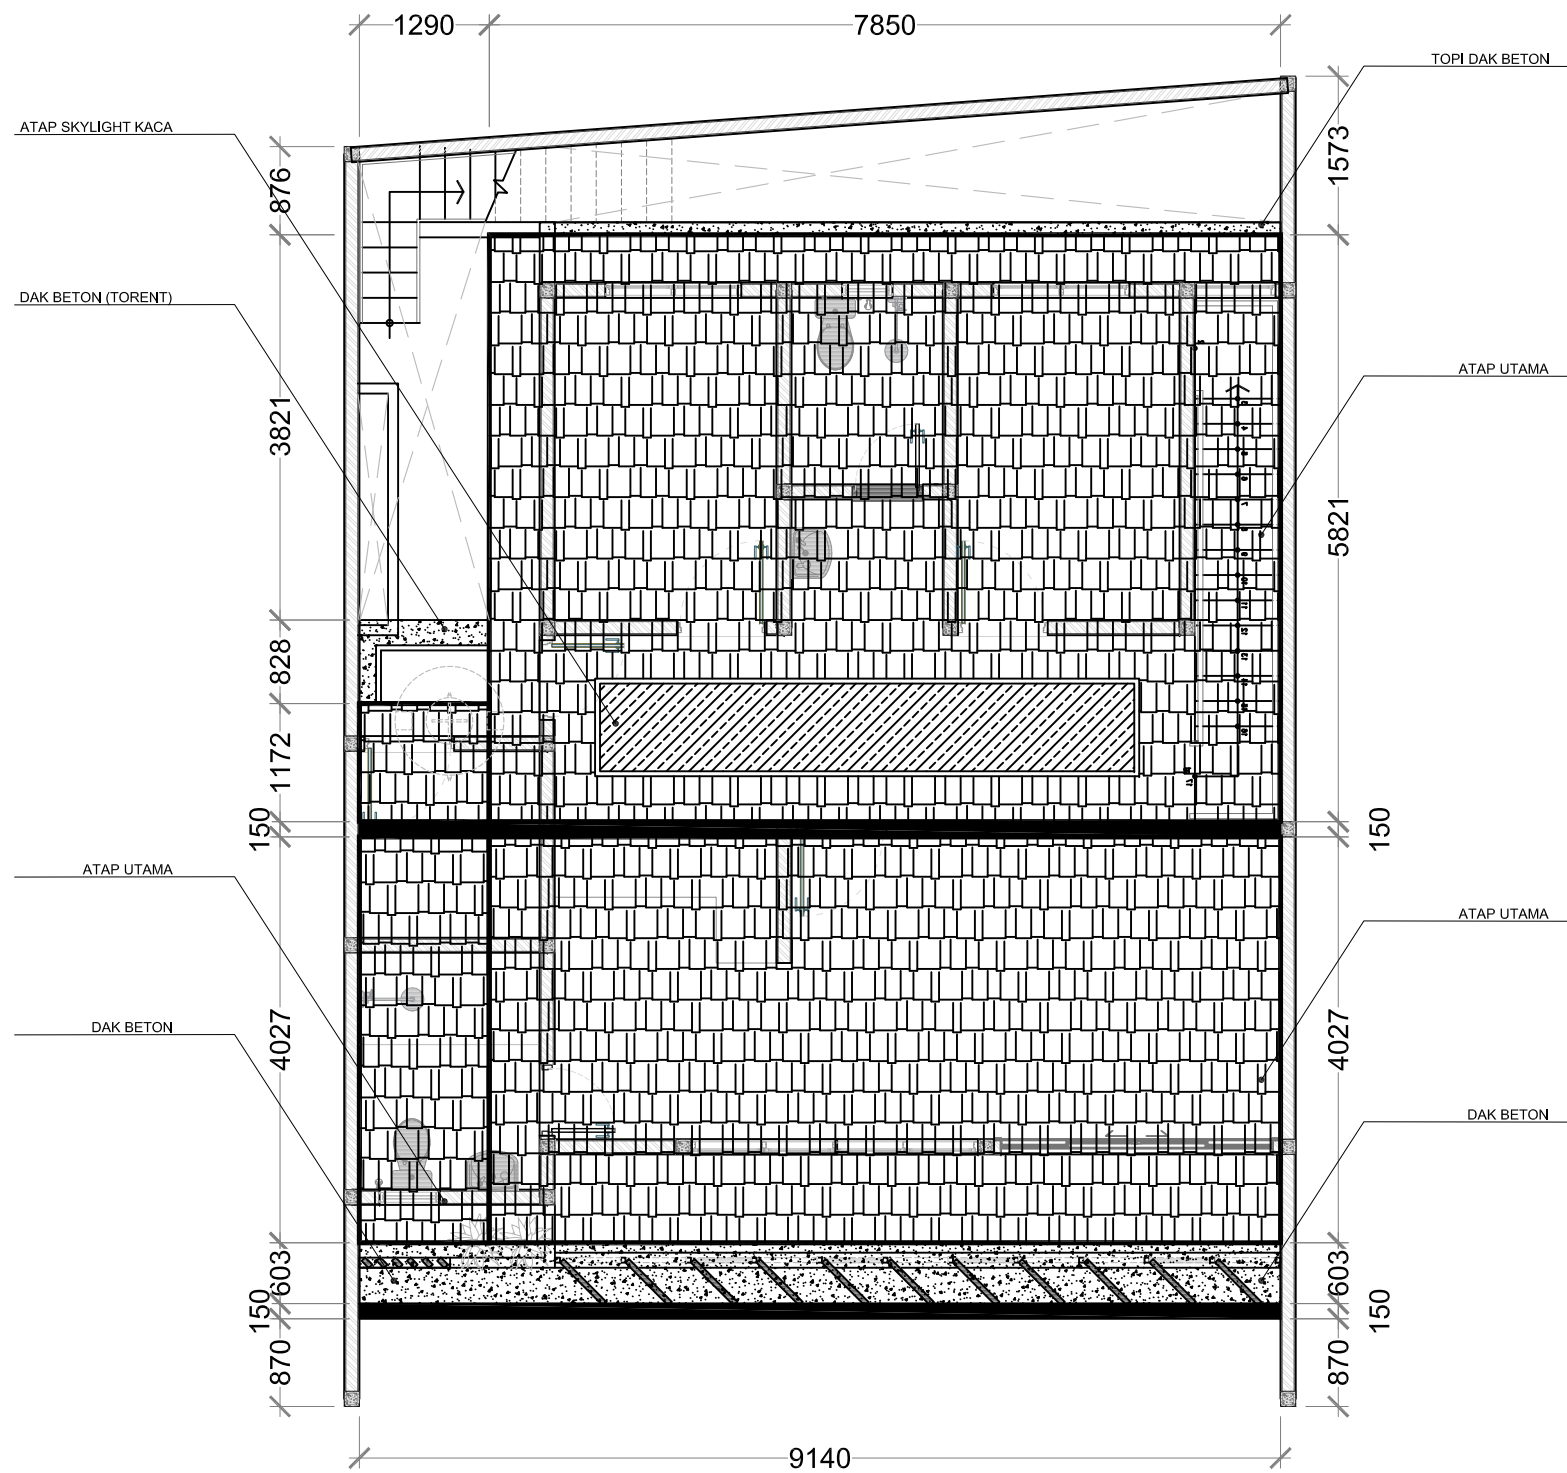


RENCANA ATAP
SKALA 1: 75

KONSULTAN				
KONTRAKTOR				
PROYEK				
TOWN HOUSE JALAN JOE JAGAKARSA JAKARTA SELATAN				
KETERANGAN				
REVISI				
			TGL	BLN
			THN	
ARSITEK				
DIGAMBAR				
DIPERIKSA				
DISETUJUI				
NO. PROYEK				
-				
NAMA GAMBAR				
RENCANA ATAP KAVLING 5				
SKALA				
1 : 75				
AR-029				
SUBKAT		NO. LEMBAR		

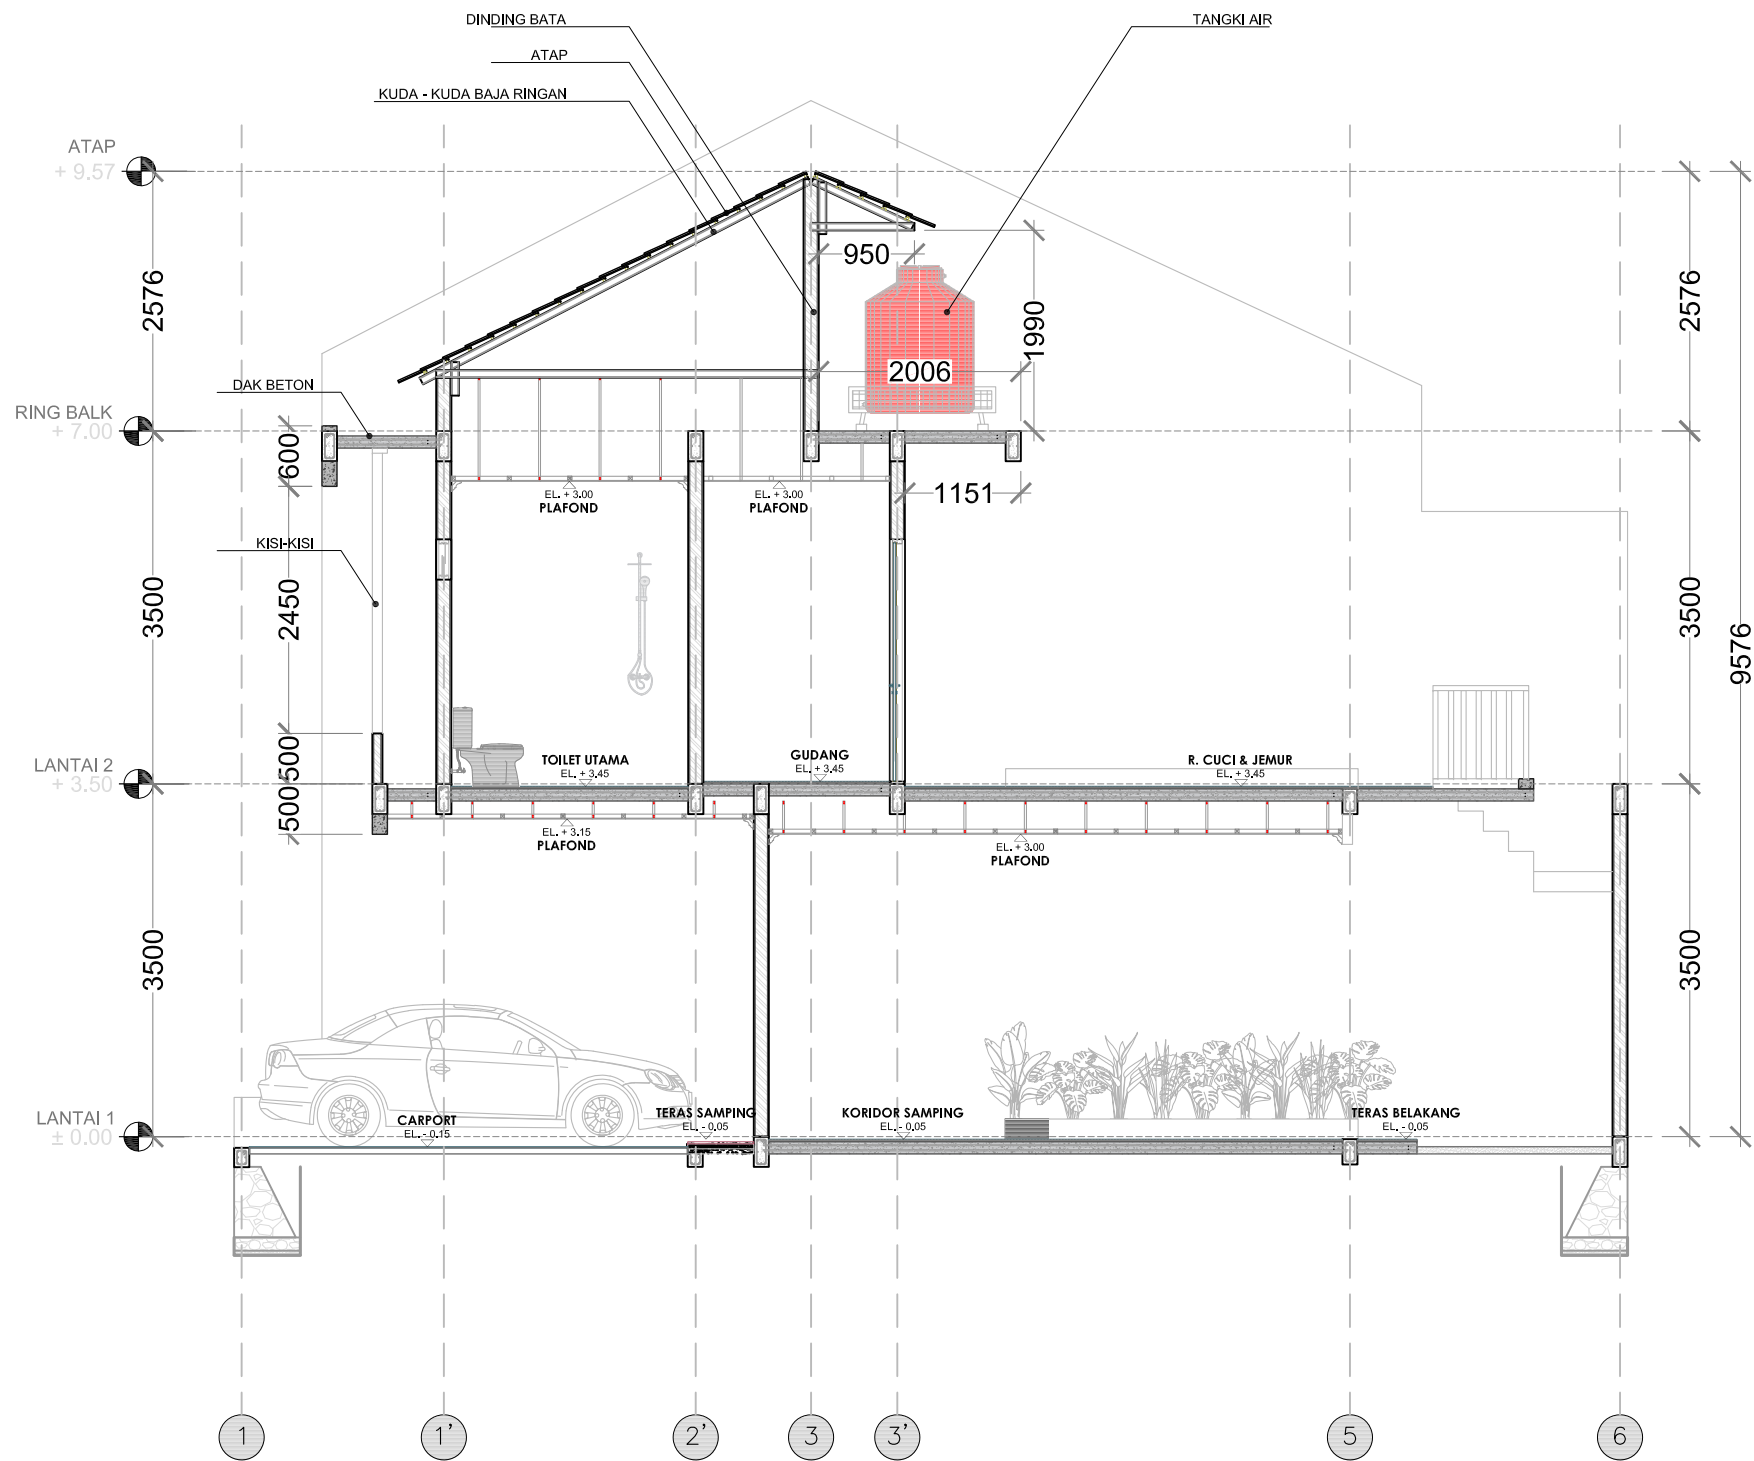


POTONGAN A - A
SKALA 1: 75

KONSULTAN			
KONTRAKTOR			
PROYEK			
TOWN HOUSE JALAN JOE JAGAKARSA JAKARTA SELATAN			
KETERANGAN			
REVISI			
		TGL	BLN
		THN	
ARSITEK			
DIGAMBAR			
DIPERIKSA			
DISETUJUI			
NO. PROYEK			
-			
NAMA GAMBAR			
POTONGAN A - A KAVLING 5			
SKALA			
1 : 75			
AR-030			
SUBKAT		NO. LEMBAR	

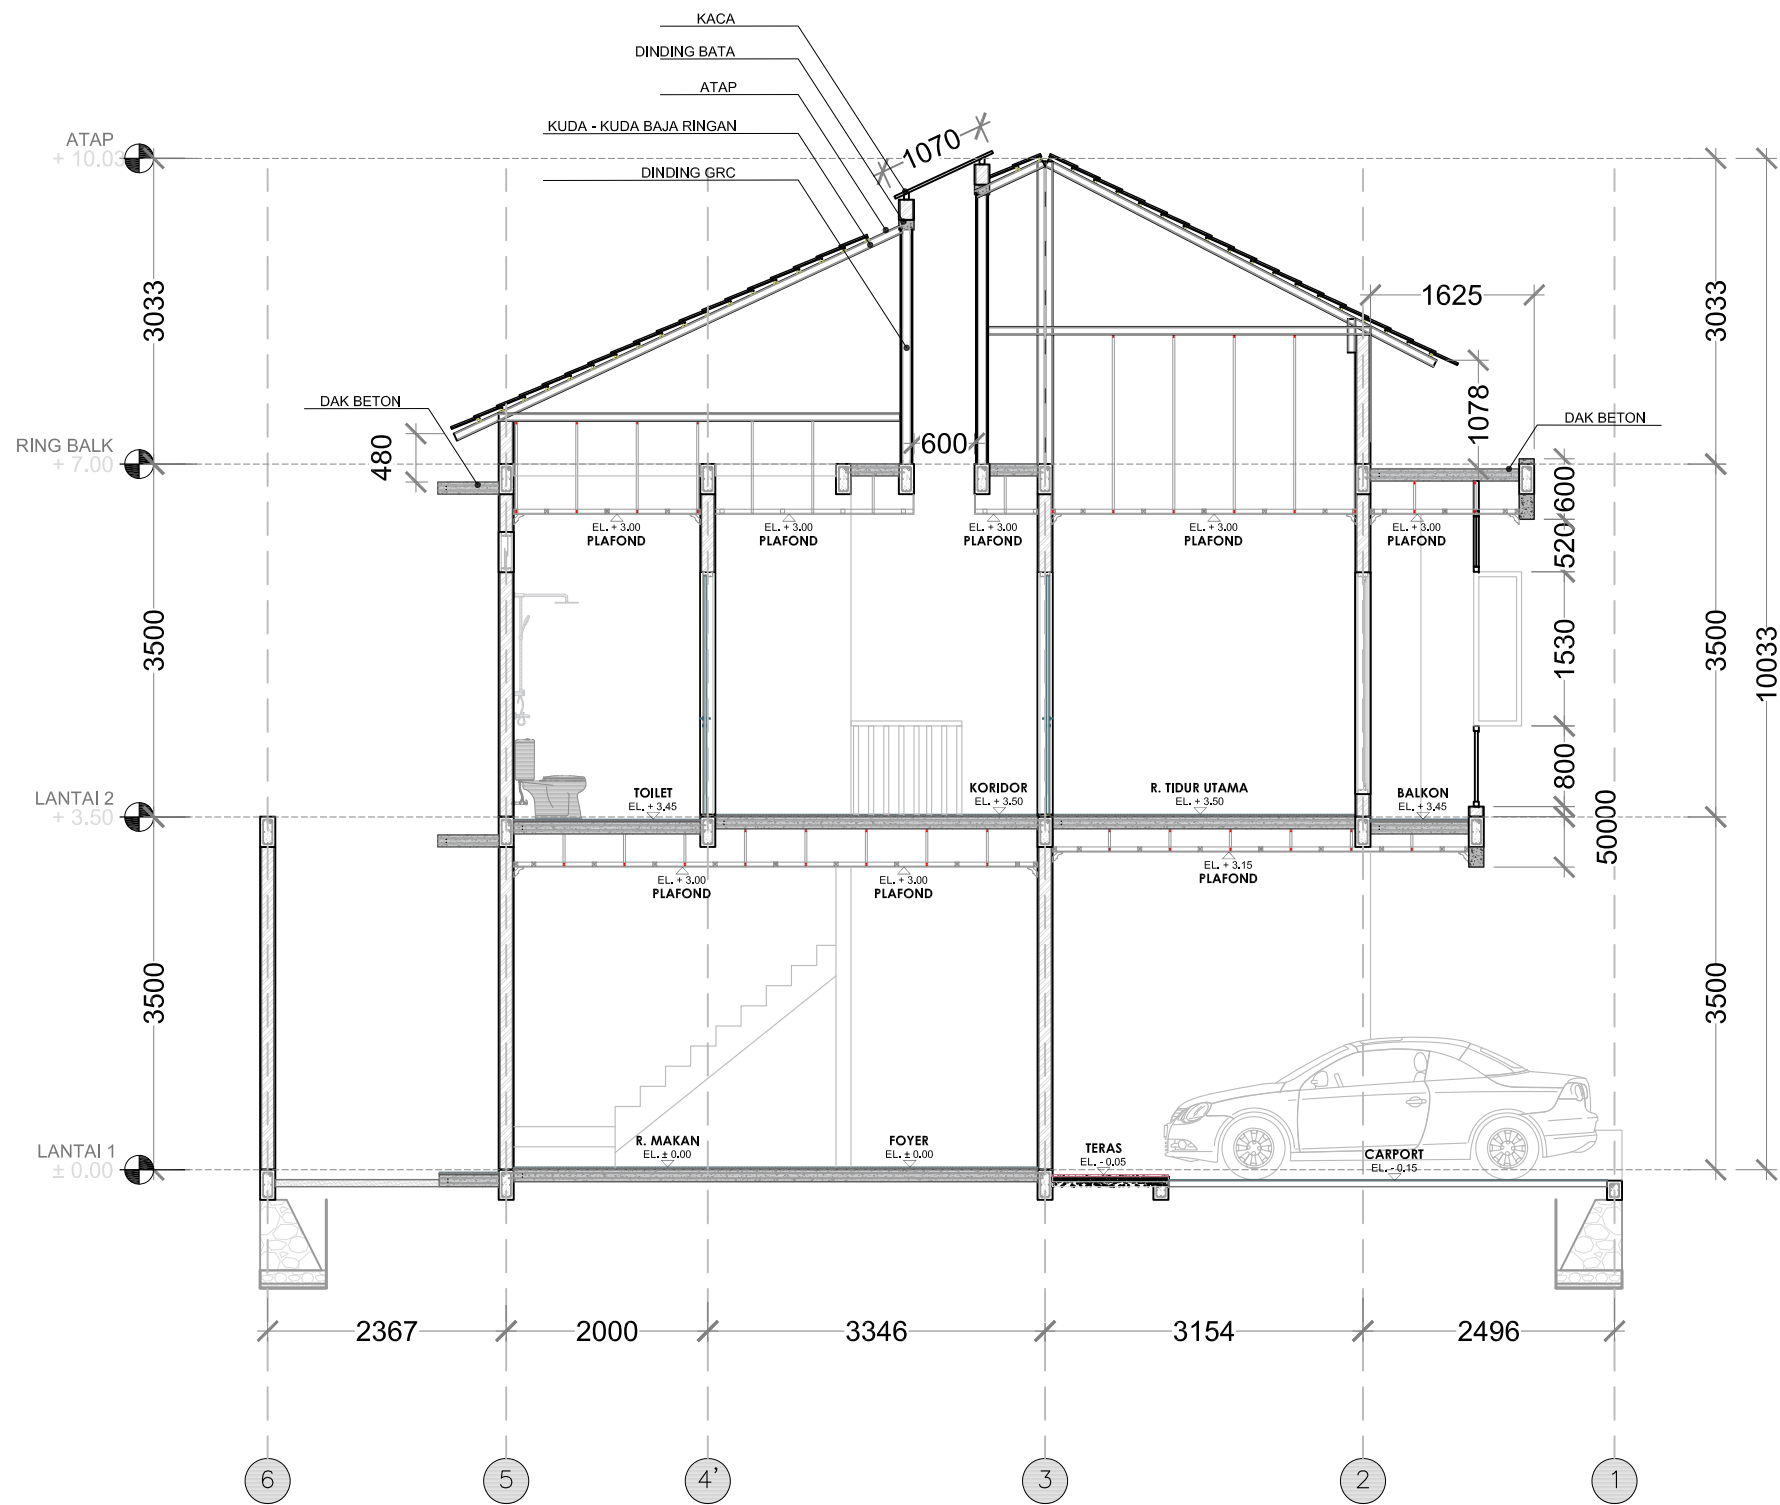


POTONGAN B - B
SKALA 1: 75

KONSULTAN			
KONTRAKTOR			
PROYEK			
TOWN HOUSE JALAN JOE JAGAKARSA JAKARTA SELATAN			
KETERANGAN			
REVISI			
		TGL	BLN
ARSITEK			
DIGAMBAR			
DIPERIKSA			
DISETUJUI			
NO. PROYEK			
-			
NAMA GAMBAR			
POTONGAN B - B KAVLING 5			
SKALA			
1 : 75			
AR-031			
SUBKAT		NO. LEMBAR	

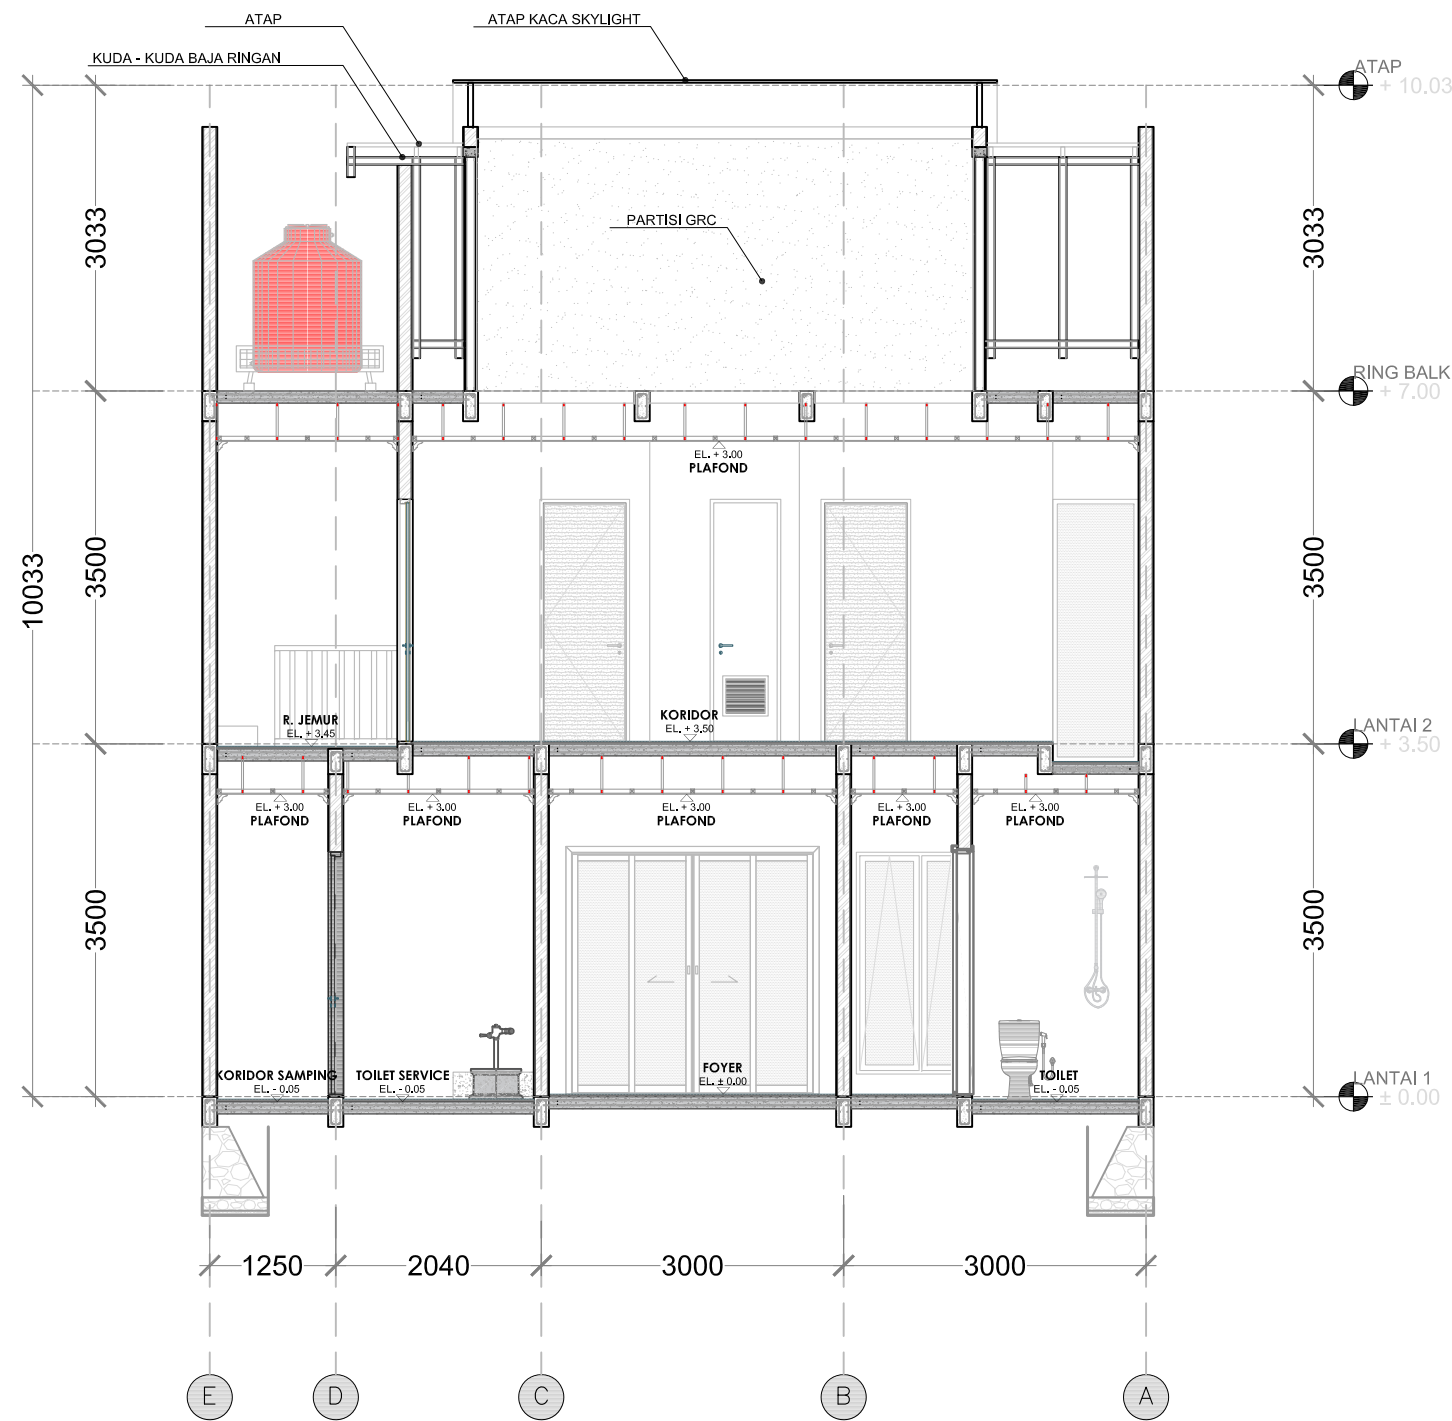


POTONGAN C - C
SKALA 1: 75

KONSULTAN																						
KONTRAKTOR																						
PROYEK																						
TOWN HOUSE JALAN JOE JAGAKARSA JAKARTA SELATAN																						
KETERANGAN																						
REVISI		<table><tr><td>TGL</td><td>BLN</td><td>THN</td></tr><tr><td></td><td></td><td></td></tr><tr><td></td><td></td><td></td></tr><tr><td></td><td></td><td></td></tr><tr><td></td><td></td><td></td></tr><tr><td></td><td></td><td></td></tr></table>			TGL	BLN	THN															
TGL	BLN	THN																				
ARSITEK																						
DIGAMBAR																						
DIPERIKSA																						
DISETUJUI																						
NO. PROYEK																						
-																						
NAMA GAMBAR																						
POTONGAN C - C KAVLING 5																						
SKALA																						
1 : 75																						
AR-032		2																				
SUBKAT		NO. LEMBAR																				


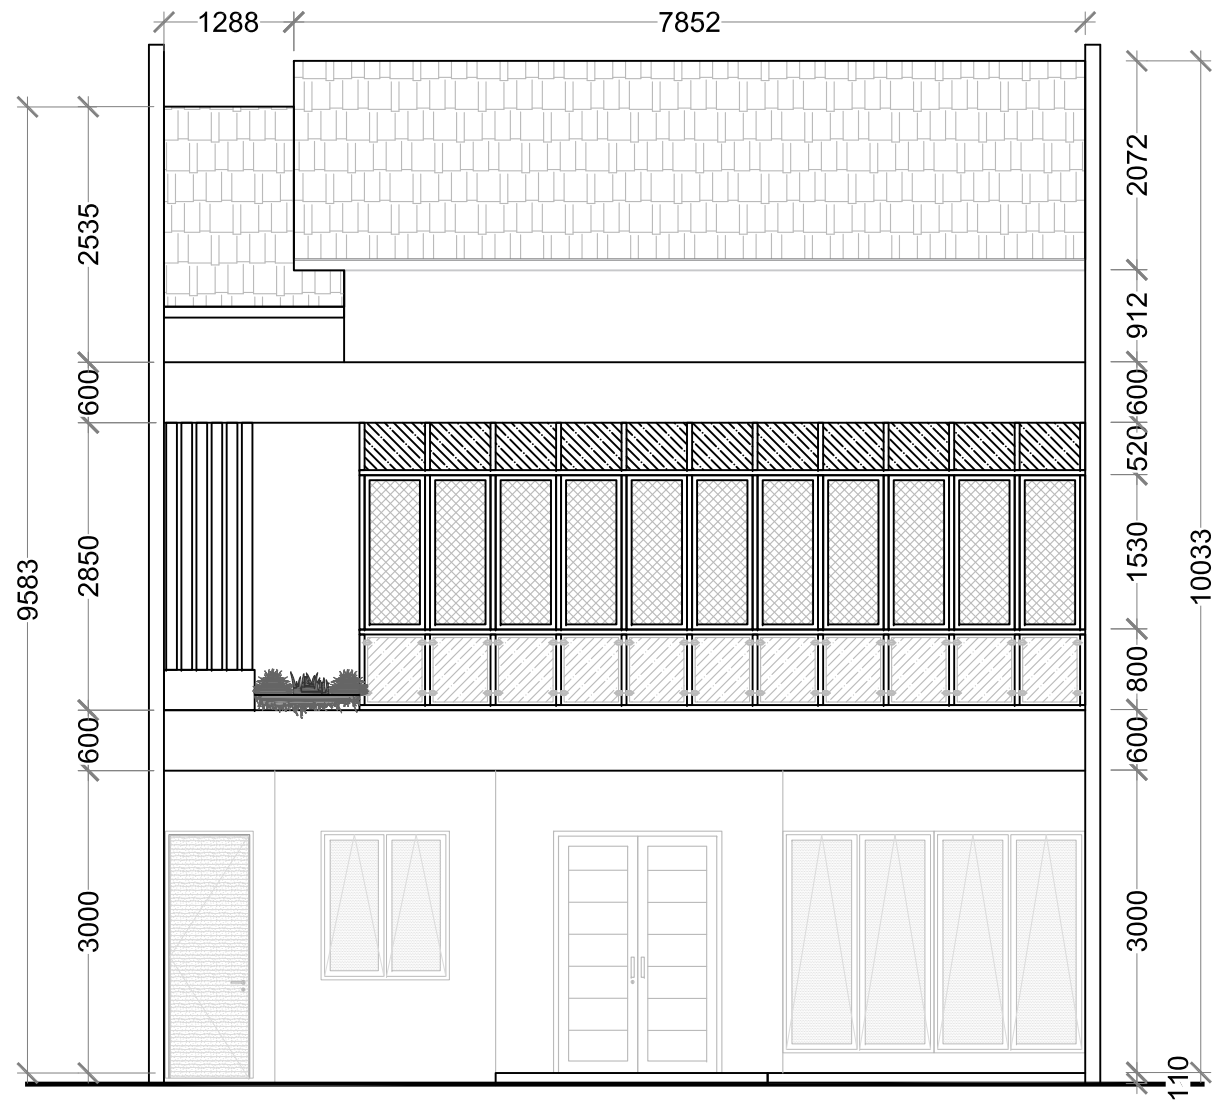


TAMPAK DEPAN
SKALA 1: 75

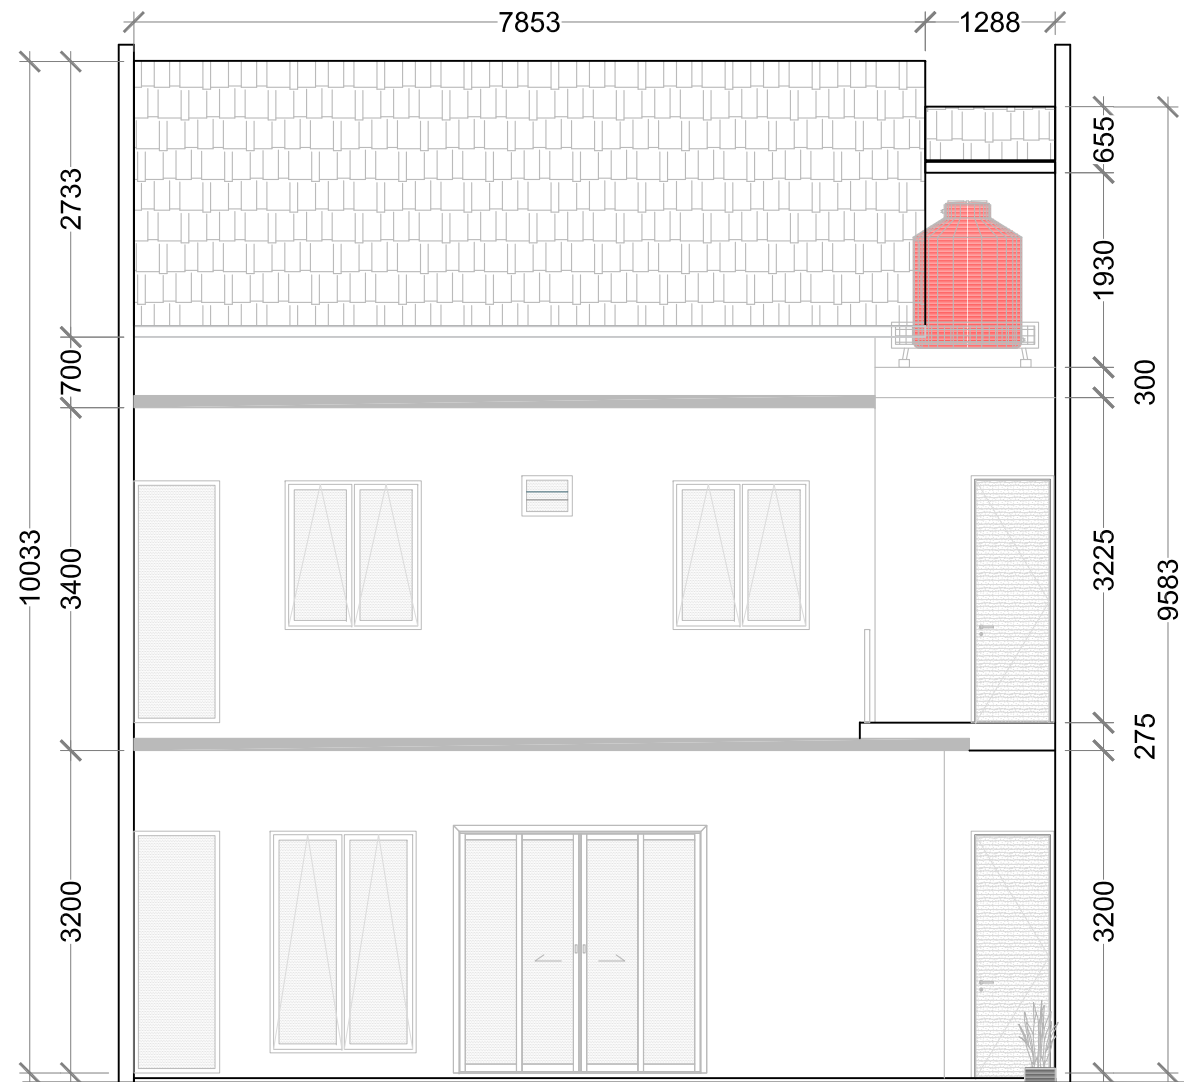

TAMPAK BELAKANG
SKALA 1: 75

KONSULTAN				
KONTRAKTOR				
PROYEK				
TOWN HOUSE JALAN JOE JAGAKARSA JAKARTA SELATAN				
KETERANGAN				
REVISI		TGL	BLN	THN
ARSITEK				
DIGAMBAR				
DIPERIKSA				
DISETUJUI				
NO. PROYEK				
-				
NAMA GAMBAR				
TAMPAK KAVLING 5				
SKALA 1 : 75				
AR-033				
SUBKAT	NO. LEMBAR			

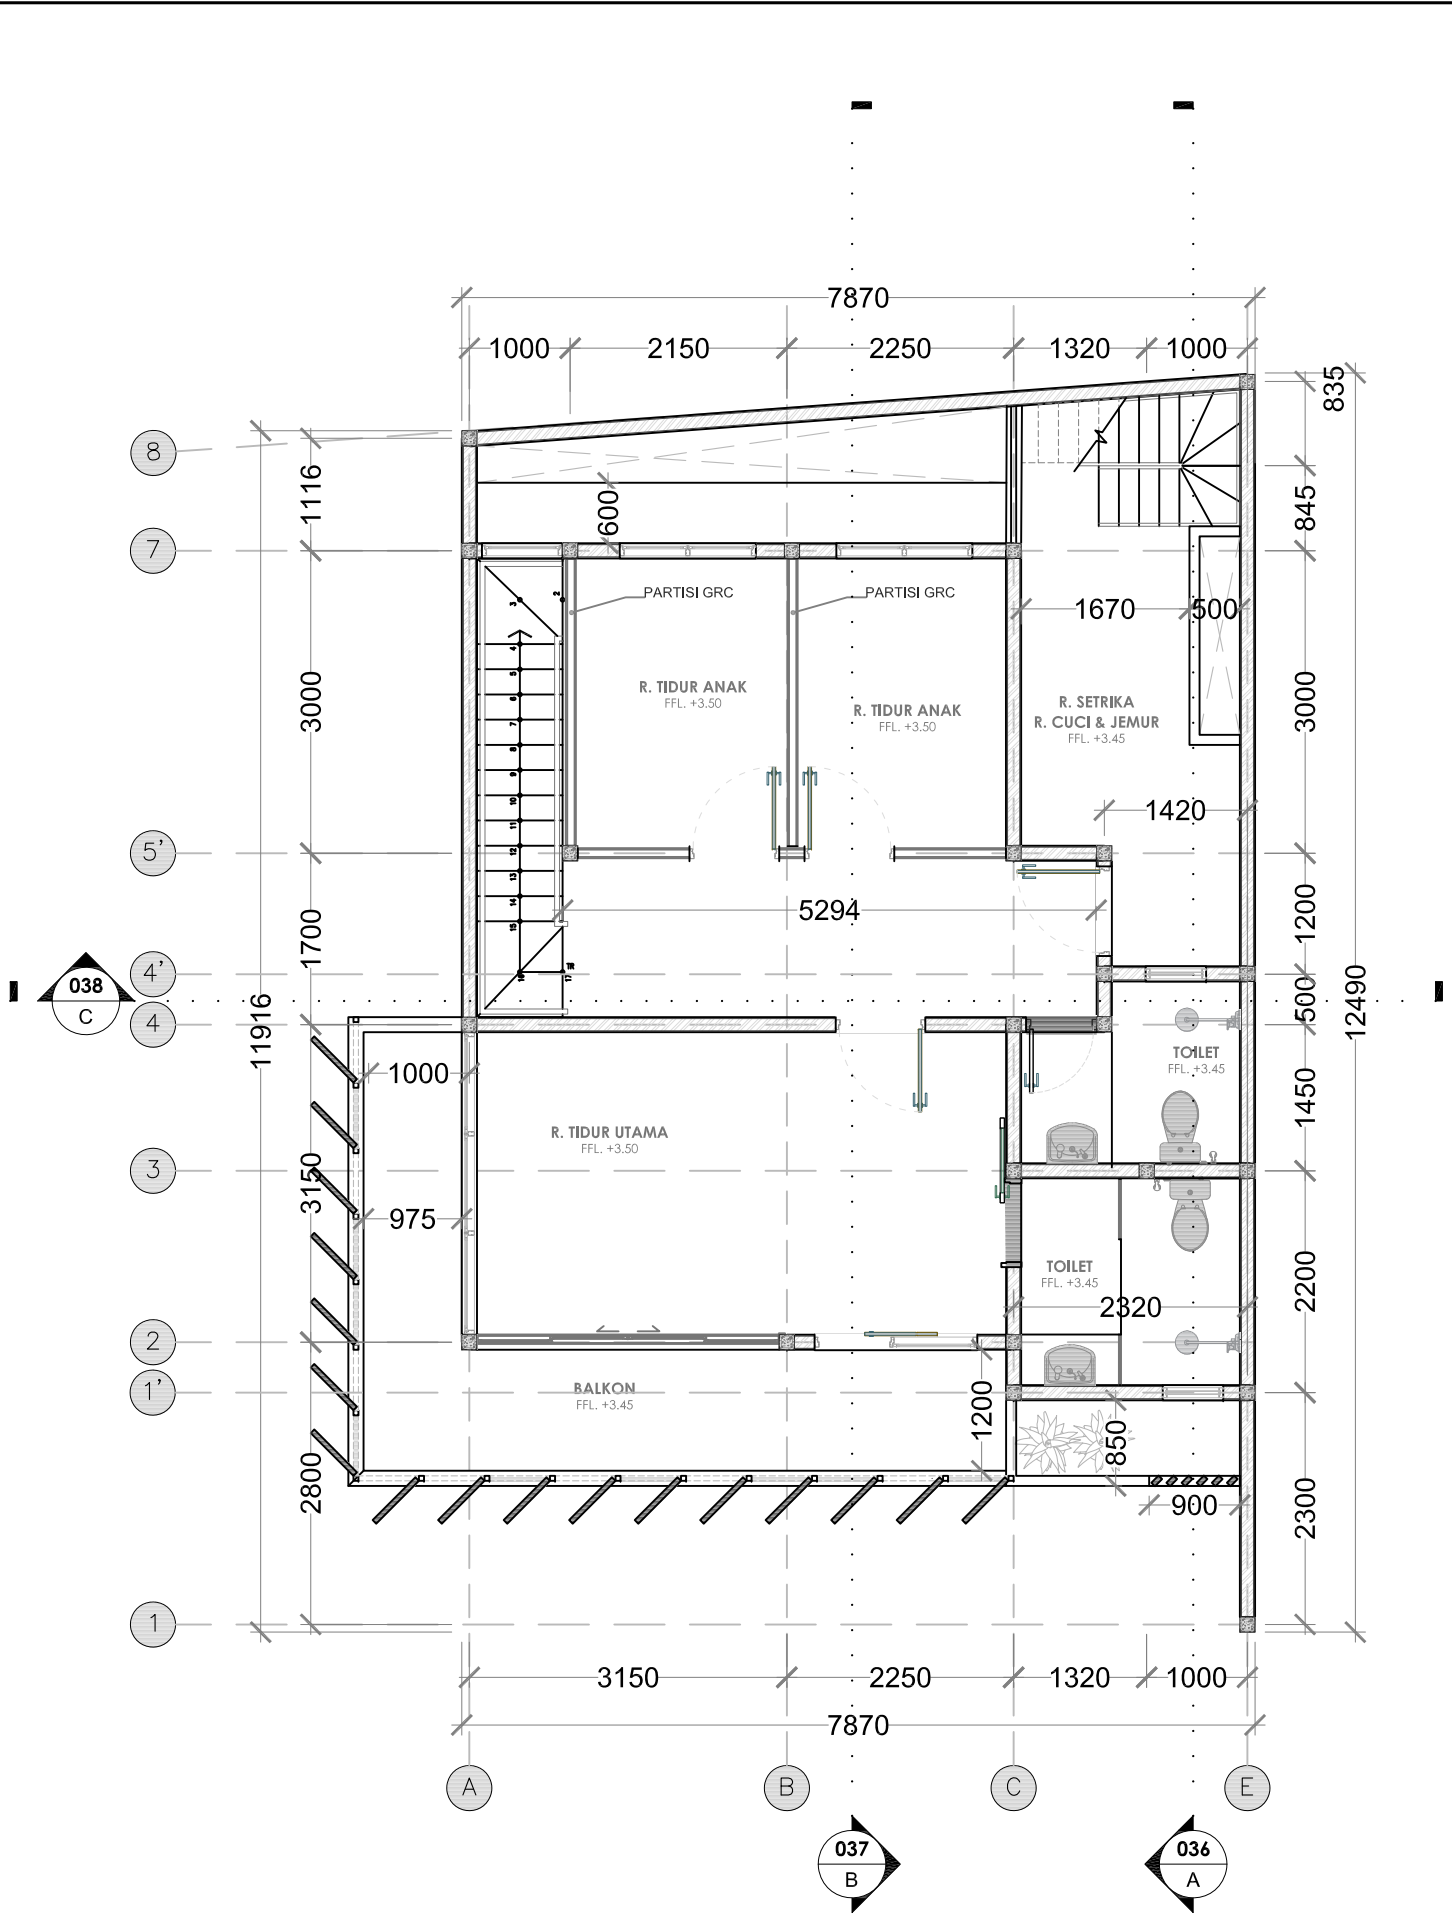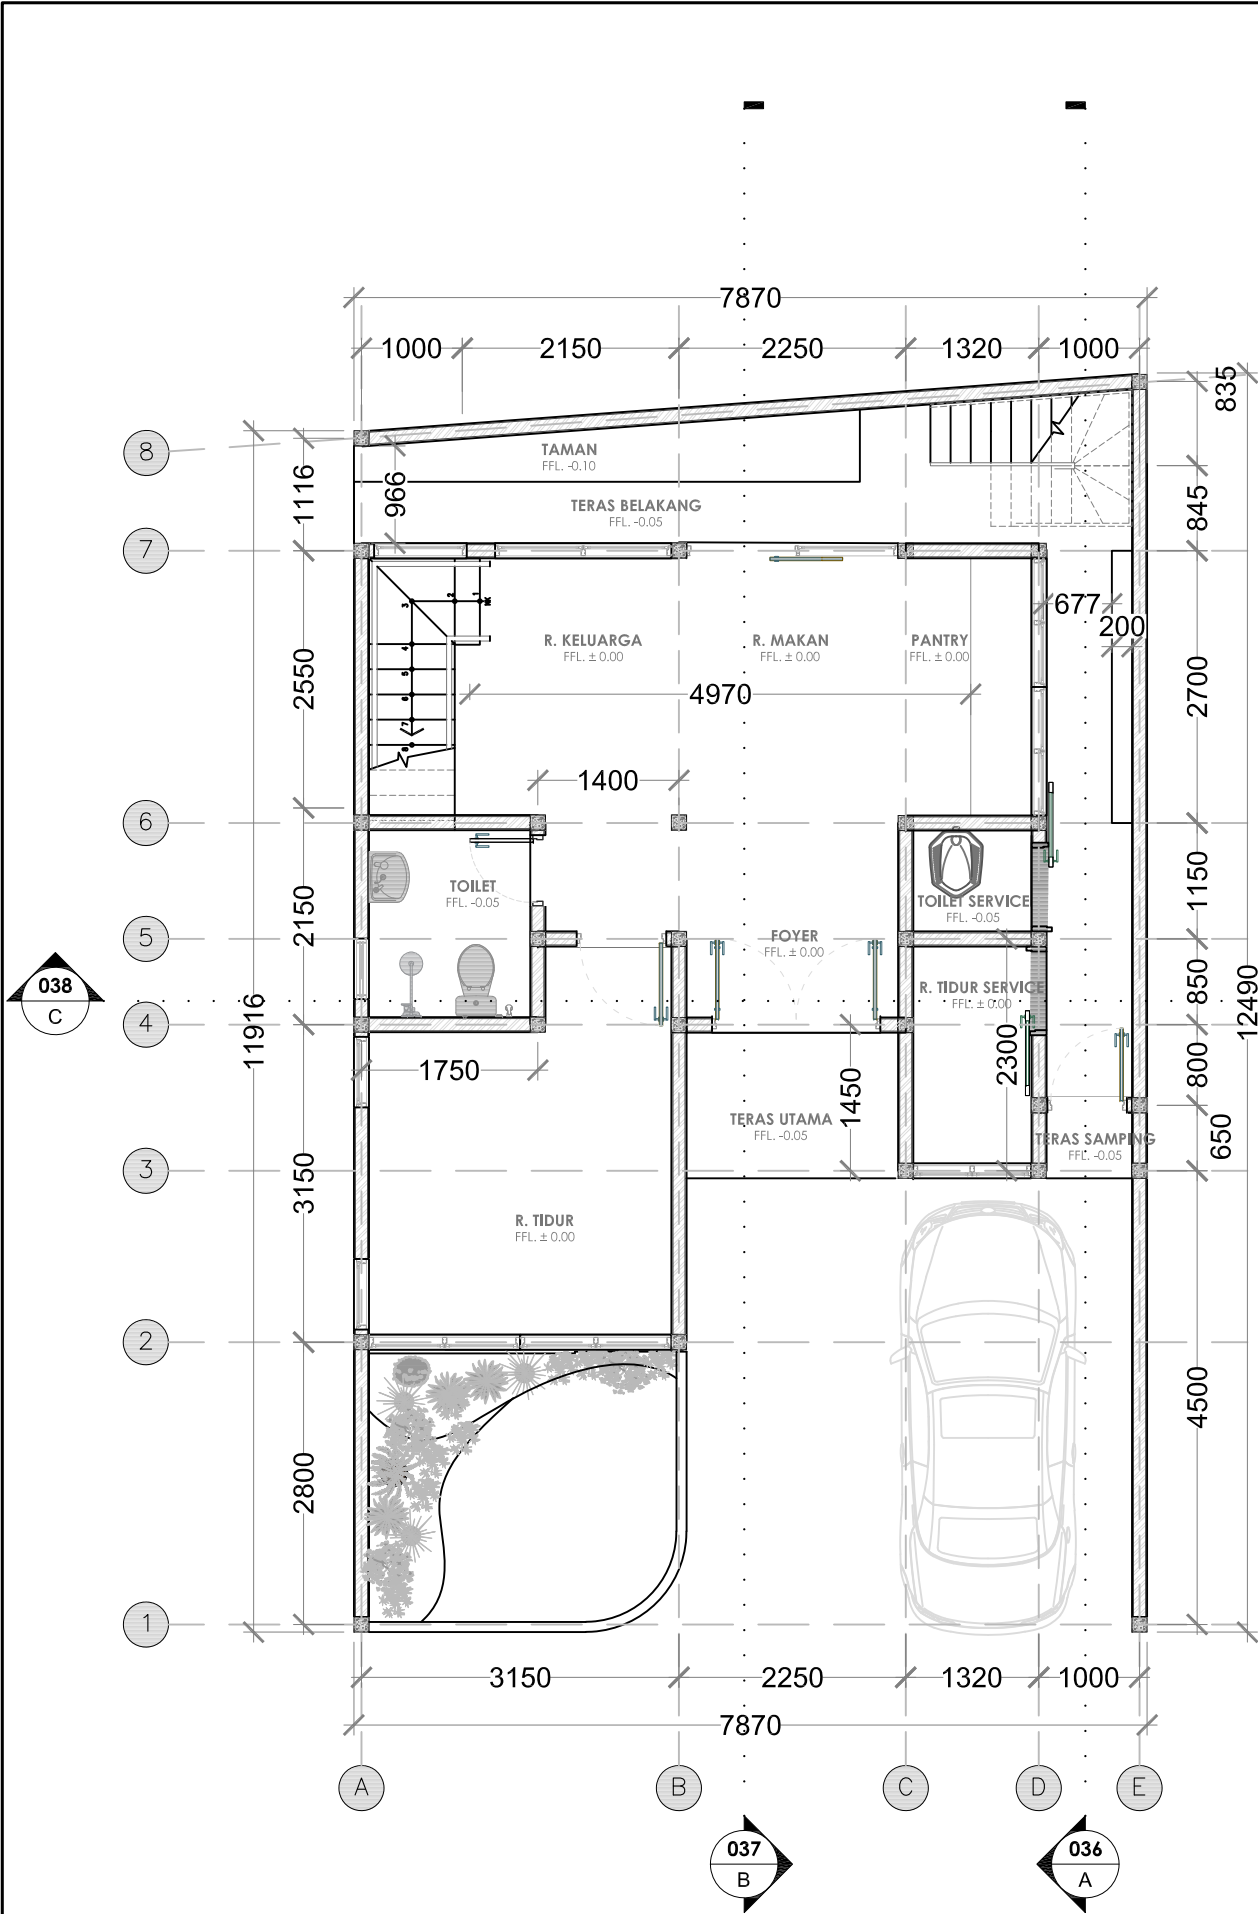

DENAH LANTAI DASAR
SKALA 1: 75

DENAH LANTAI ATAS
SKALA 1: 75

KONSULTAN				
KONTRAKTOR				
PROYEK				
TOWN HOUSE JALAN JOE JAGAKARSA JAKARTA SELATAN				
KETERANGAN				
REVISI		TGL	BLN	THN
ARSITEK				
DIGAMBAR				
DIPERIKSA				
DISETUJUI				
NO. PROYEK				
-				
NAMA GAMBAR				
DENAH KAVLING 6				
SKALA				
1 : 75				
AR-034				
SUBKAT		NO. LEMBAR		



SKALA 1:75

KONSULTAN

KONTRAKTOR

PROYEK

TOWN HOUSE
JALAN JOE
JAGAKARSA
JAKARTA SELATAN

KETERANGAN

REVISI	TGL	BLN	THN
ARSITEK			
DIGAMBAR			
DIPERIKSA			
DISETUJUI			

NO. PROYEK

NAMA GAMBAR

RENCANA ATAP KAVLING 6


SKALA

1 : 75

AR-035

SUBKAT

NO. LEMBAR

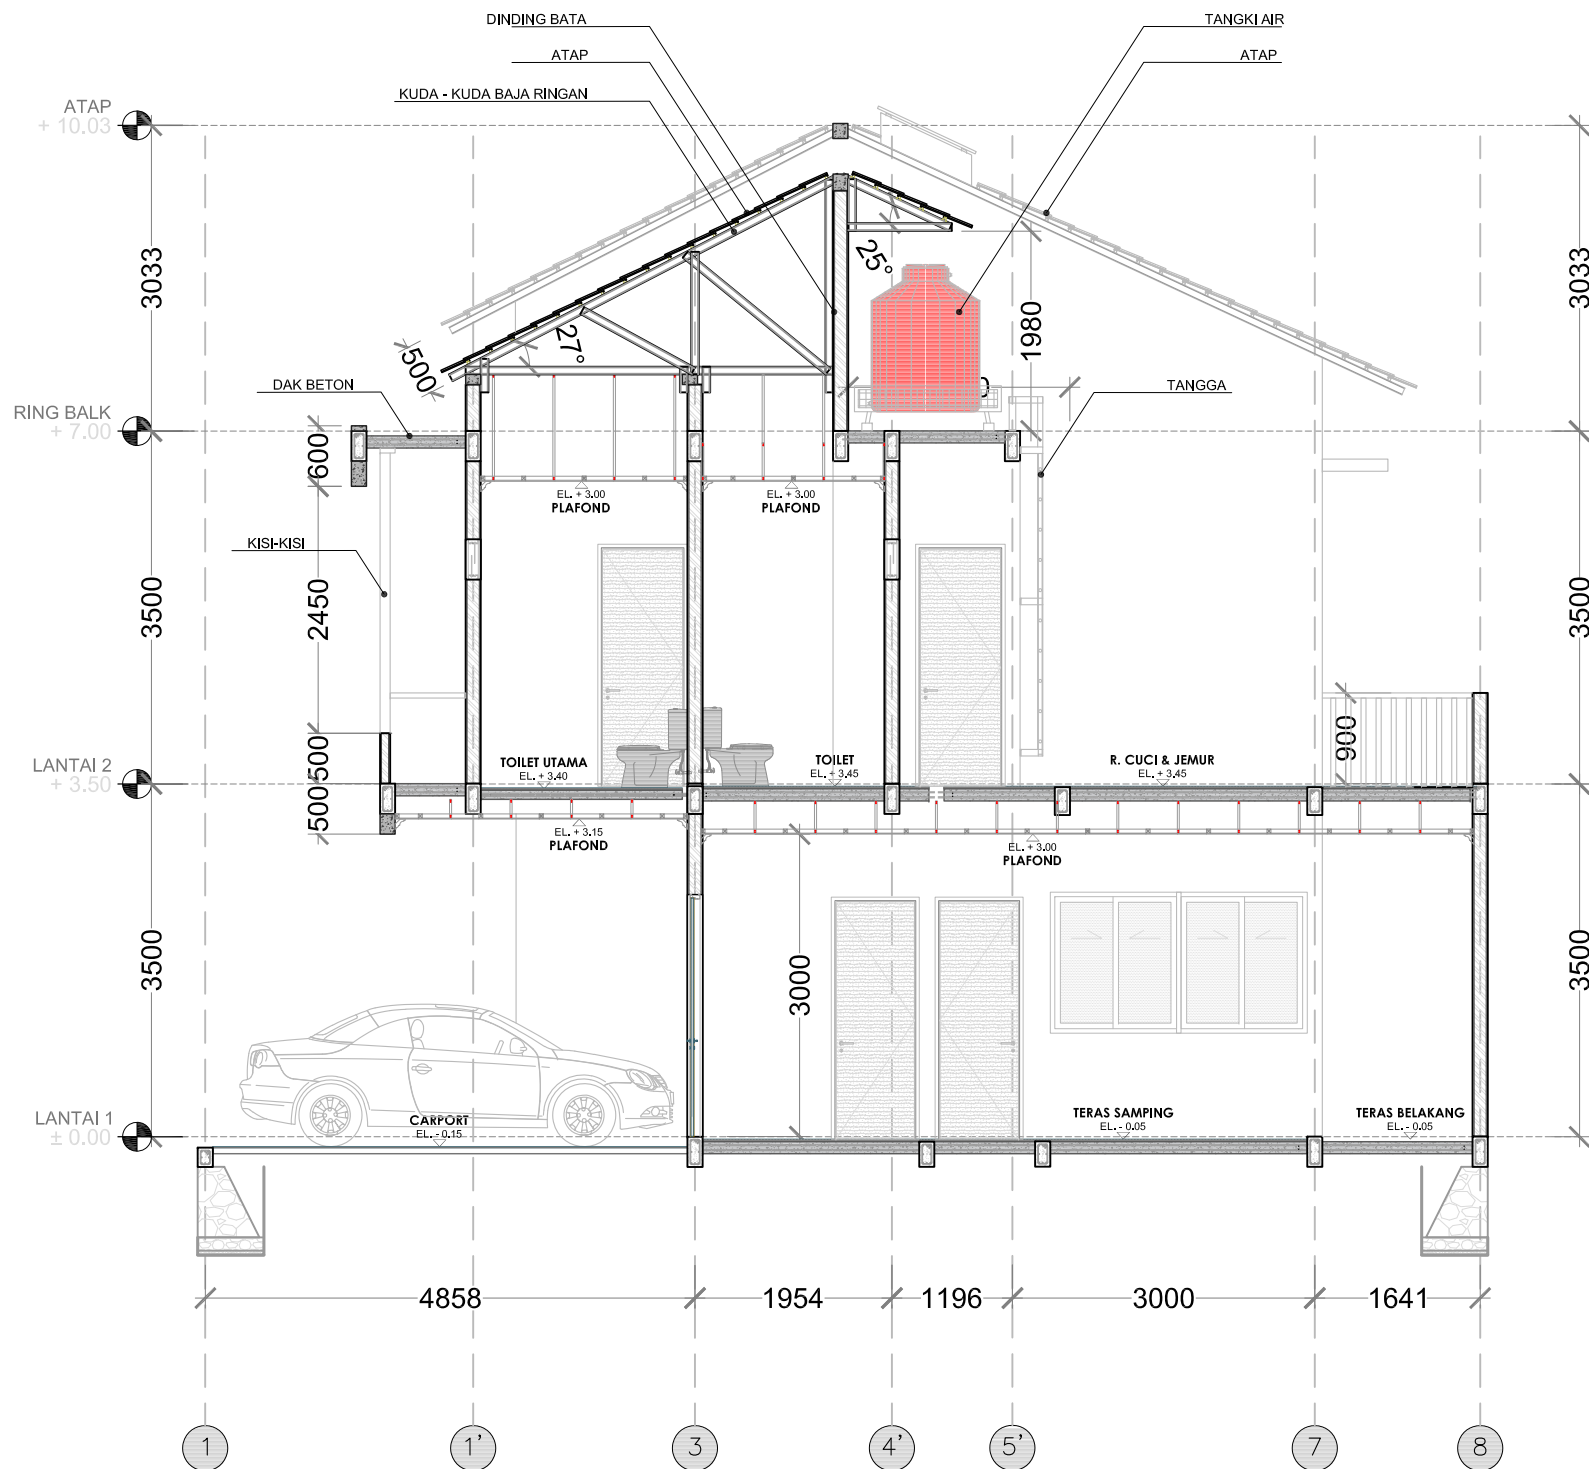


POTONGAN A - A
SKALA 1: 75

KONSULTAN			
KONTRAKTOR			
PROYEK			
TOWN HOUSE JALAN JOE JAGAKARSA JAKARTA SELATAN			
KETERANGAN			
REVISI			
		TGL	BLN
		THN	
ARSITEK			
DIGAMBAR			
DIPERIKSA			
DISETUJUI			
NO. PROYEK			
-			
NAMA GAMBAR			
POTONGAN A - A KAVLING 6			
SKALA			
1 : 75			
AR-036			
SUBKAT		NO. LEMBAR	

POTONGAN B - B

SKALA 1: 75

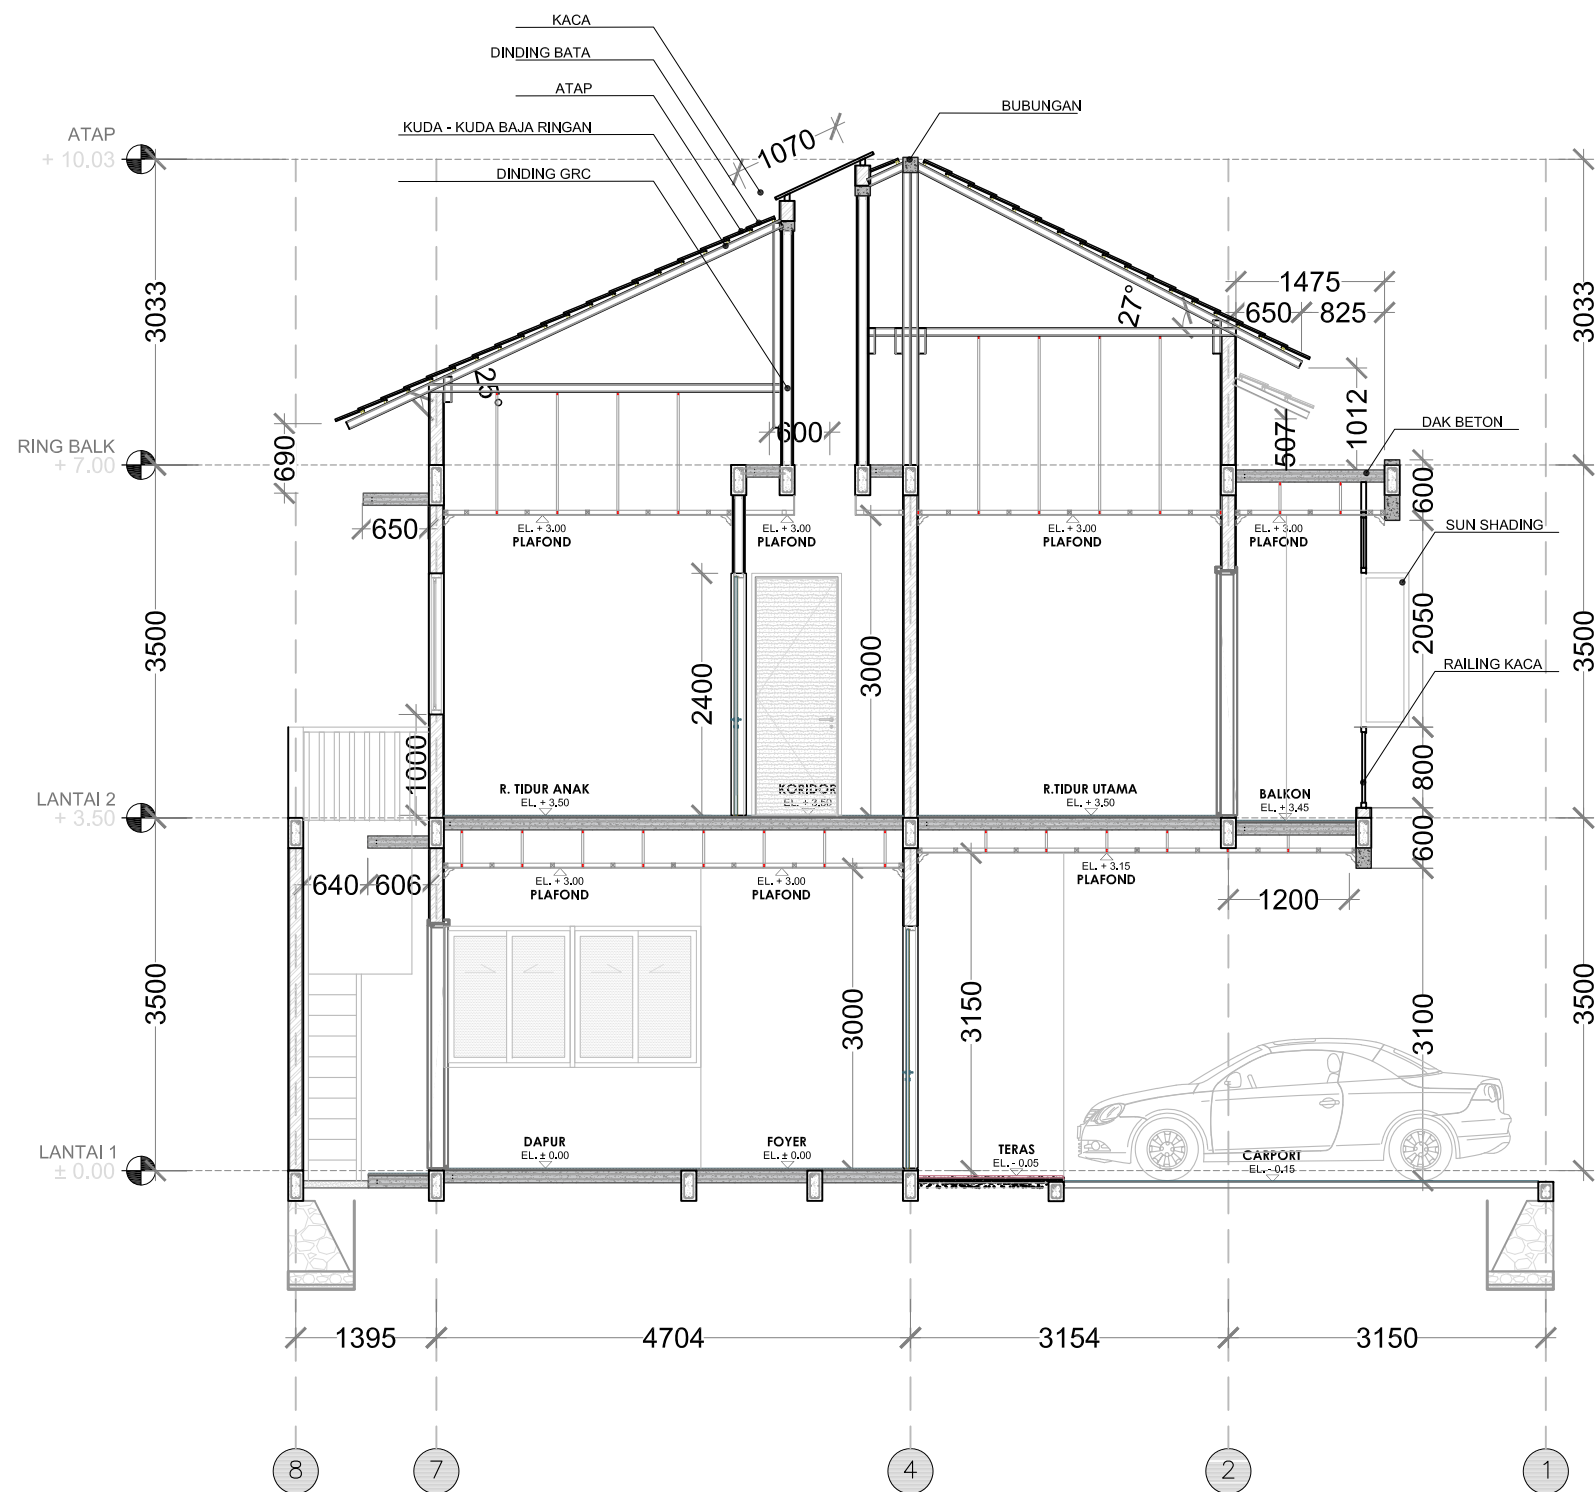

KONSULTAN

KONTRAKTOR

PROYEK

TOWN HOUSE
JALAN JOE
JAGAKARSA
JAKARTA SELATAN

KETERANGAN

REVISI

ARSITEK

DIGAMBAR

DIPERIKSA

DISETUJUI

NO. PROYEK

NAMA GAMBAR

POTONGAN B - B
KAVLING 6


SKALA

1 : 75

AR-037


SUBKAT

NO. LEMBAR

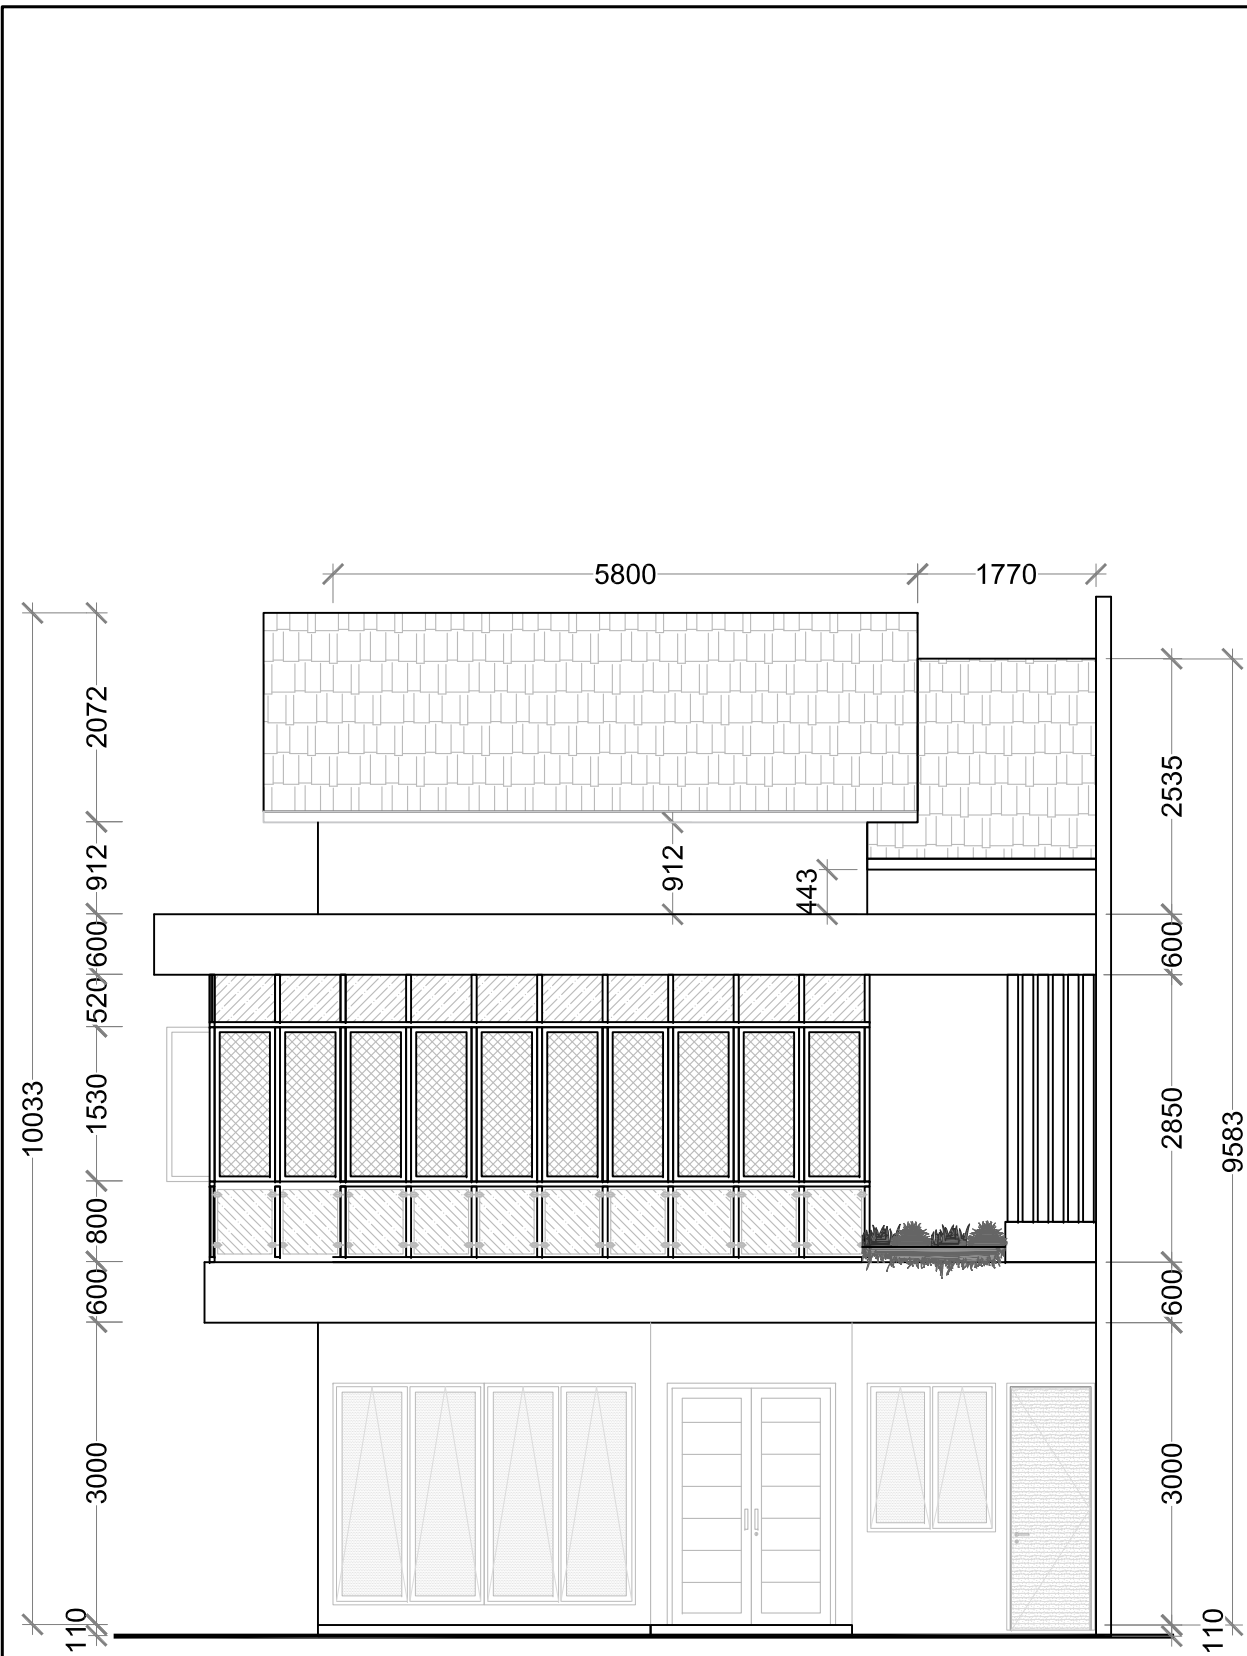

TAMPAK DEPAN


SKALA 1: 75

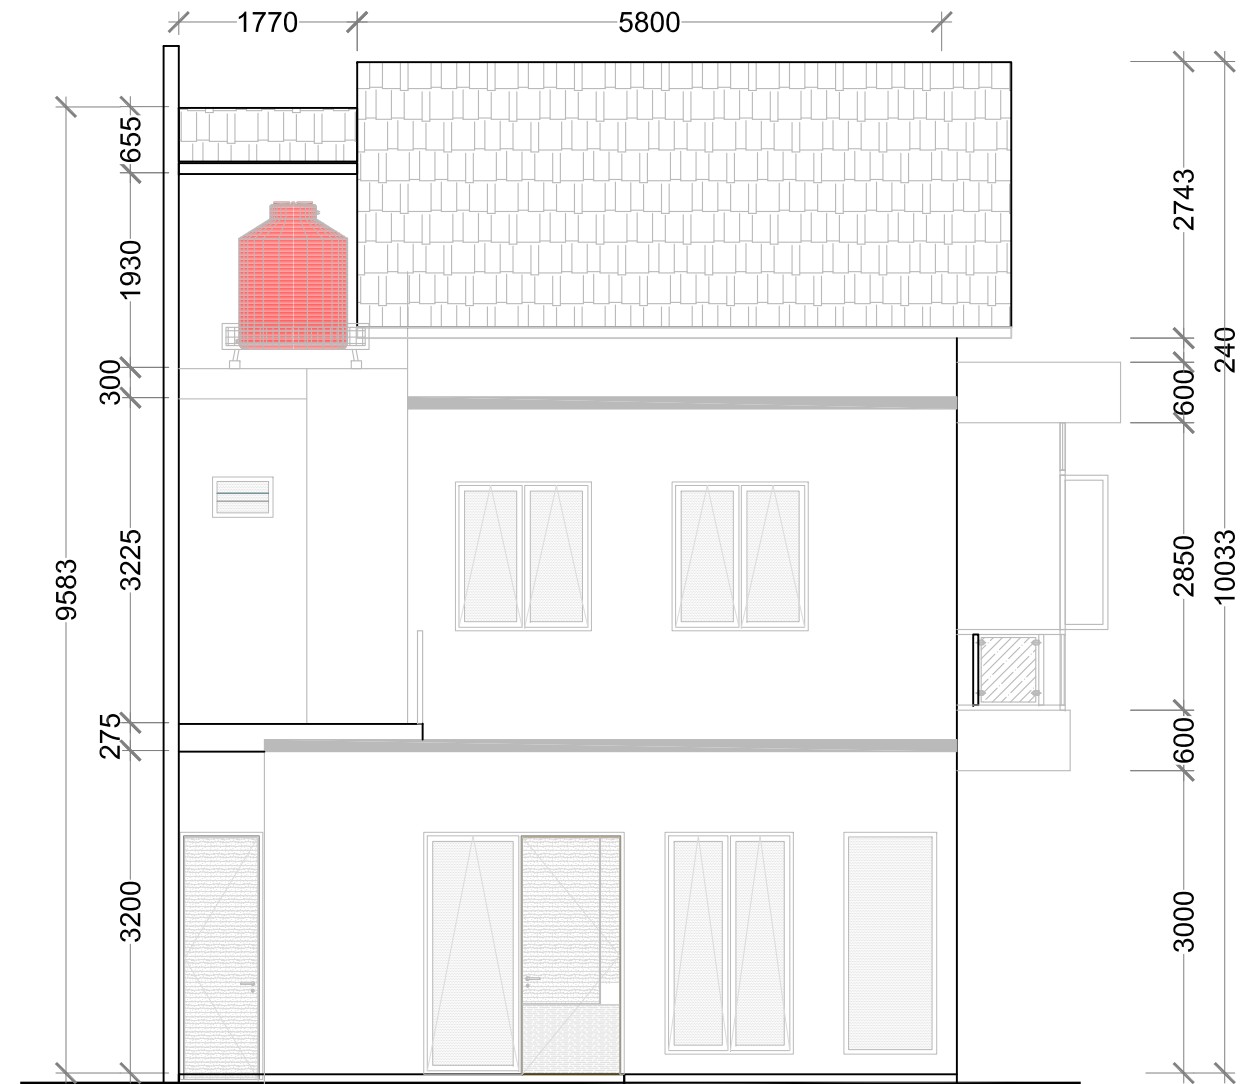

TAMPAK BELAKANG

SKALA 1: 75

KONSULTAN				
KONTRAKTOR				
PROYEK				
TOWN HOUSE JALAN JOE JAGAKARSA JAKARTA SELATAN				
KETERANGAN				
REVISI		TGL		
		BLN	THN	
ARSITEK				
DIGAMBAR				
DIPERIKSA				
DISETUJUI				
NO. PROYEK				
-				
NAMA GAMBAR				
TAMPAK KAVLING 6				
SKALA				
1 : 75				
AR-039				
SUBKAT		NO. LEMBAR		

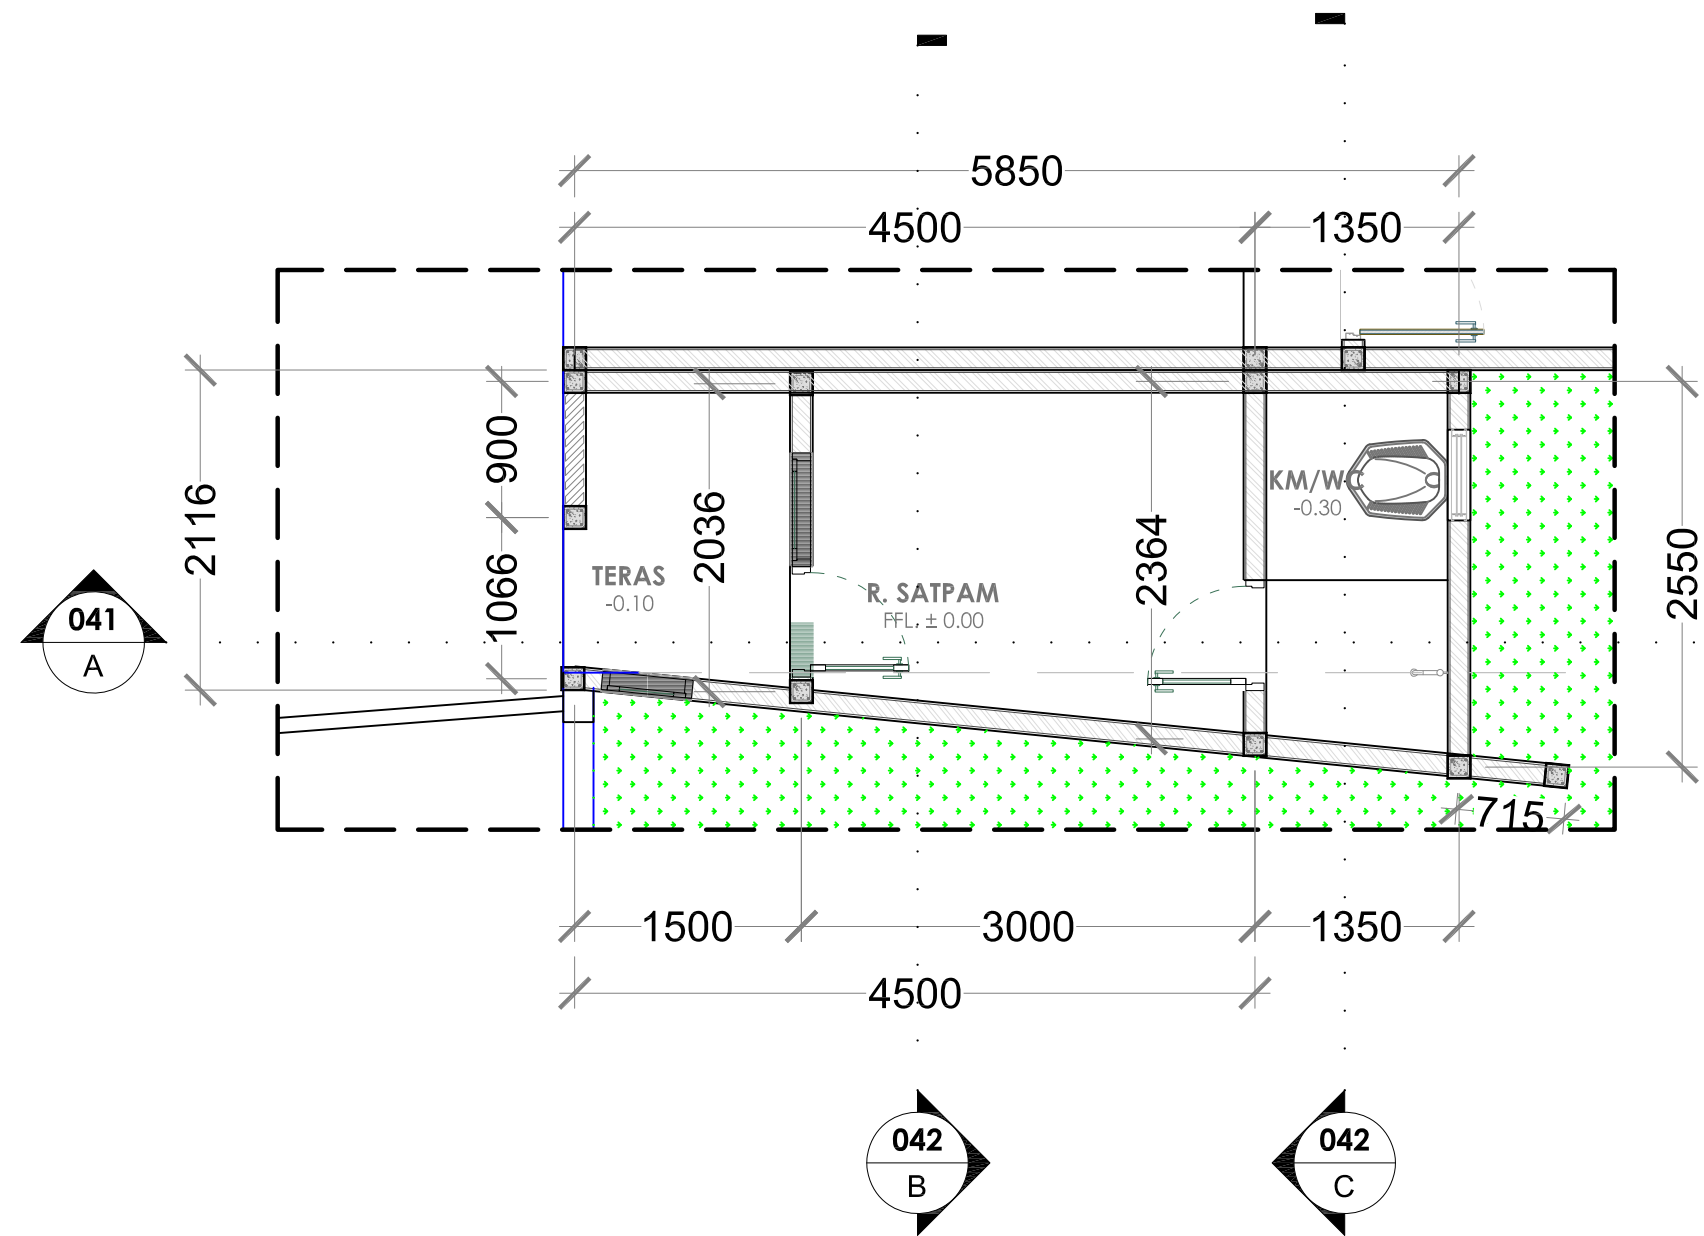

DENAH RG. SATPAM
SKALA 1: 50

KONSULTAN

KONTRAKTOR

PROYEK

TOWN HOUSE
JALAN JOE
JAGAKARSA
JAKARTA SELATAN

KETERANGAN

REVISI

ARSITEK

DIGAMBAR

DIPERIKSA

DISETUJUI

NO. PROYEK

NAMA GAMBAR

DENAH
RG. SATPAM

SKALA

1 : 50

AR-040

SUBKAT

NO. LEMBAR



NO. LEMBAR



KONSULTAN			
KONTRAKTOR			
PROYEK			
TOWN HOUSE JALAN JOE JAGAKARSA JAKARTA SELATAN			
KETERANGAN			
REVISI			
		TGL	BLN
		THN	
ARSITEK			
DIGAMBAR			
DIPERIKSA			
DISETUUJI			
NO. PROYEK			
-			
NAMA GAMBAR			
POTONGAN B & C RG. SATPAM			
SKALA			
1 : 50			
AR-042			
SUBKAT		NO. LEMBAR	



PERSPEKTIF

SKALA

KONSULTAN				
KONTRAKTOR				
PROYEK				
TOWN HOUSE JALAN JOE JAGAKARSA JAKARTA SELATAN				
KETERANGAN				
REVISI		TGL	BLN	THN
ARSITEK				
DIGAMBAR				
DIPERIKSA				
DISETUIJUI				
NO. PROYEK				
-				
NAMA GAMBAR				
PERSPEKTIF				
SKALA				
NTS				
AR-043				
SUBKAT		NO. LEMBAR		



PERSPEKTIF
SKALA:NTS

KONSULTAN				
KONTRAKTOR				
PROYEK				
TOWN HOUSE JALAN JOE JAGAKARSA JAKARTA SELATAN				
KETERANGAN				
REVISI		TGL	BLN	THN
ARSITEK				
DIGAMBAR				
DIPERIKSA				
DISETUJUI				
NO. PROYEK				
-				
NAMA GAMBAR				
PERSPEKTIF				
SKALA				
NTS				
AR		-	044	
SUBKAT		NO. LEMBAR		



PERSPEKTIF
SKALA:NTS


KONSULTAN				
KONTRAKTOR				
PROYEK				
TOWN HOUSE JALAN JOE JAGAKARSA JAKARTA SELATAN				
KETERANGAN				
REVISI		TGL	BLN	THN
ARSITEK				
DIGAMBAR				
DIPERIKSA				
DISETUJUI				
NO. PROYEK				
-				
NAMA GAMBAR				
PERSPEKTIF				
SKALA				
NTS				
AR-045				
SUBKAT		NO. LEMBAR		



PERSPEKTIF

SKALA:NTS

KONSULTAN				
KONTRAKTOR				
PROYEK				
TOWN HOUSE JALAN JOE JAGAKARSA JAKARTA SELATAN				
KETERANGAN				
REVISI		TGL	BLN	THN
ARSITEK				
DIGAMBAR				
DIPERIKSA				
DISETUIJUI				
NO. PROYEK				
-				
NAMA GAMBAR				
PERSPEKTIF				
SKALA				
NTS				
AR-046				
SUBKAT		NO. LEMBAR		

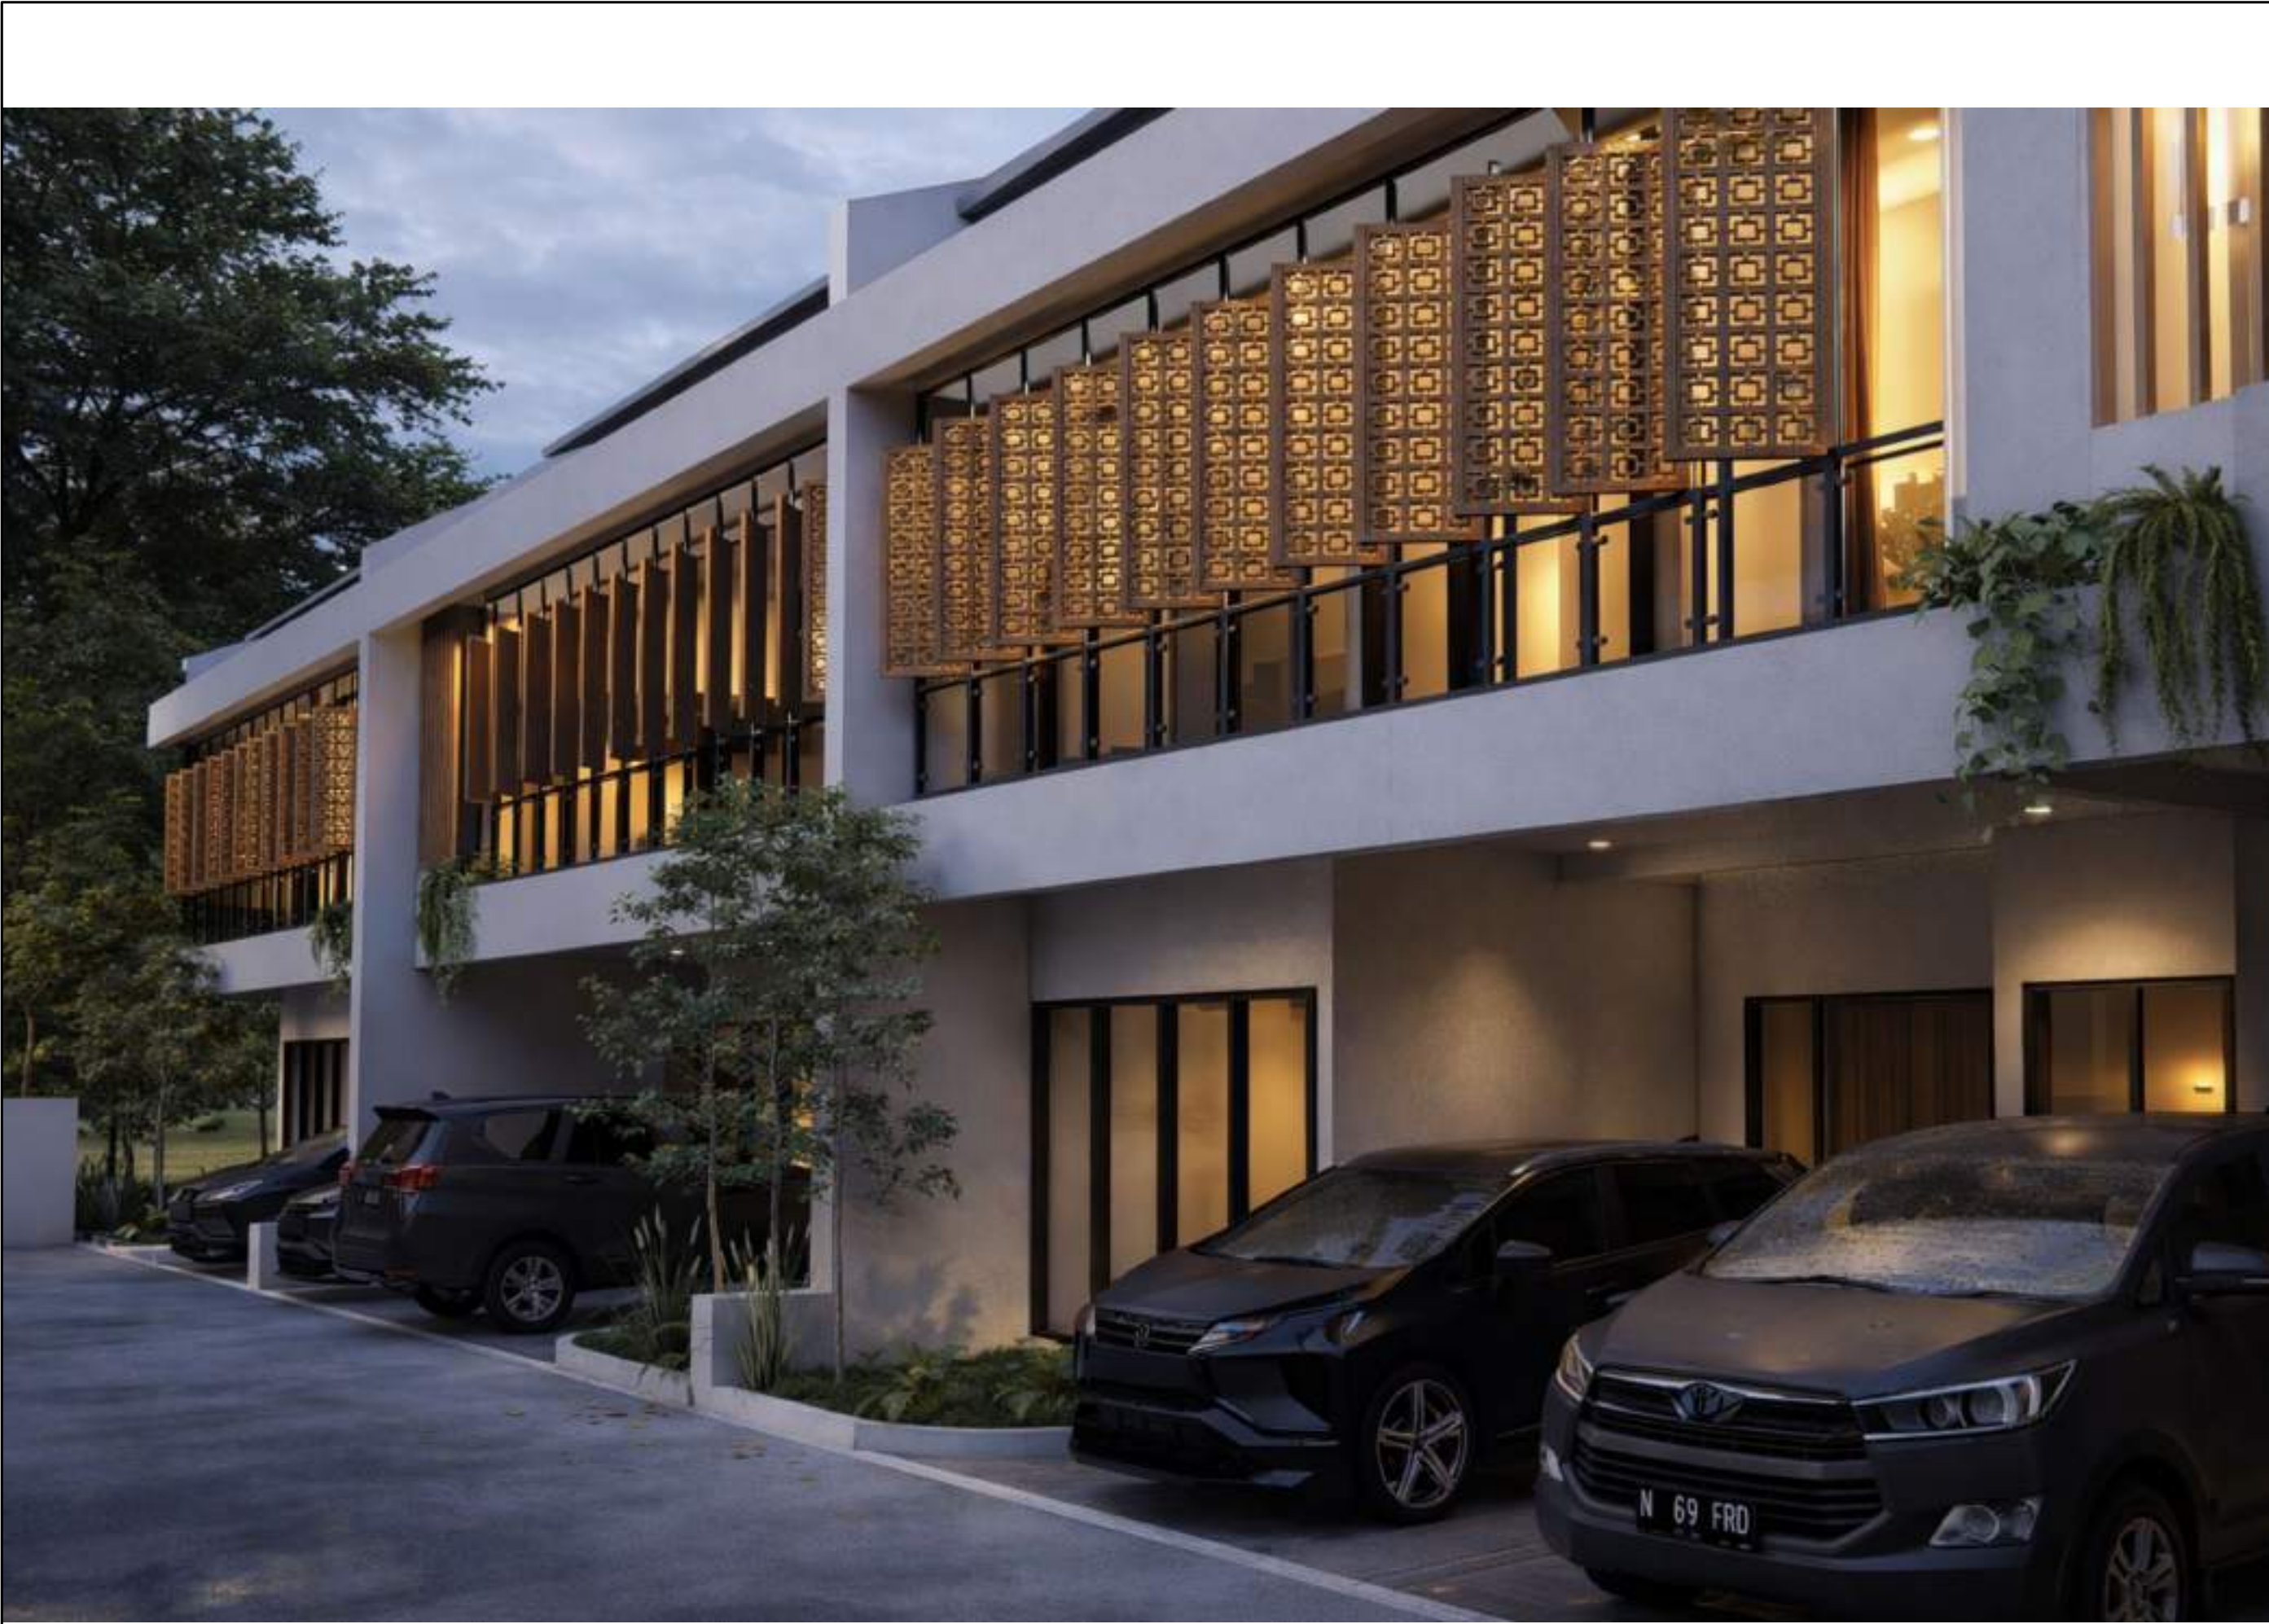

PERSPEKTIF

SKALA:NTS

KONSULTAN				
KONTRAKTOR				
PROYEK				
TOWN HOUSE JALAN JOE JAGAKARSA JAKARTA SELATAN				
KETERANGAN				
REVISI		TGL	BLN	THN
ARSITEK				
DIGAMBAR				
DIPERIKSA				
DISETUIJUI				
NO. PROYEK				
-				
NAMA GAMBAR				
PERSPEKTIF				
SKALA				
NTS				
AR-047				
SUBKAT		NO. LEMBAR		



PERSPEKTIF

SKALA: 1:50

KONSULTAN				
KONTRAKTOR				
PROYEK				
TOWN HOUSE JALAN JOE JAGAKARSA JAKARTA SELATAN				
KETERANGAN				
REVISI		TGL	BLN	THN
ARSITEK				
DIGAMBAR				
DIPERIKSA				
DISETUJUI				
NO. PROYEK		-		
NAMA GAMBAR				
PERSPEKTIF				
SKALA		NTS		
AR-048				
SUBKAT	NO. LEMBAR			



PERSPEKTIF

SKALA:NTS

KONSULTAN			
KONTRAKTOR			
PROYEK			
TOWN HOUSE JALAN JOE JAGAKARSA JAKARTA SELATAN			
KETERANGAN			
REVISI		TGL	BLN
ARSITEK			
DIGAMBAR			
DIPERIKSA			
DISETUUJI			
NO. PROYEK			
-			
NAMA GAMBAR			
PERSPEKTIF			
SKALA			
NTS			
AR-049			
SUBKAT		NO. LEMBAR	



PERSPEKTIF

SKALA:NTS

KONSULTAN			
KONTRAKTOR			
PROYEK			
TOWN HOUSE JALAN JOE JAGAKARSA JAKARTA SELATAN			
KETERANGAN			
REVISI		TGL	BLN
ARSITEK			
DIGAMBAR			
DIPERIKSA			
DISETUJUI			
NO. PROYEK			
-			
NAMA GAMBAR			
PERSPEKTIF			
SKALA			
NTS			
AR-050			
SUBKAT		NO. LEMBAR	